

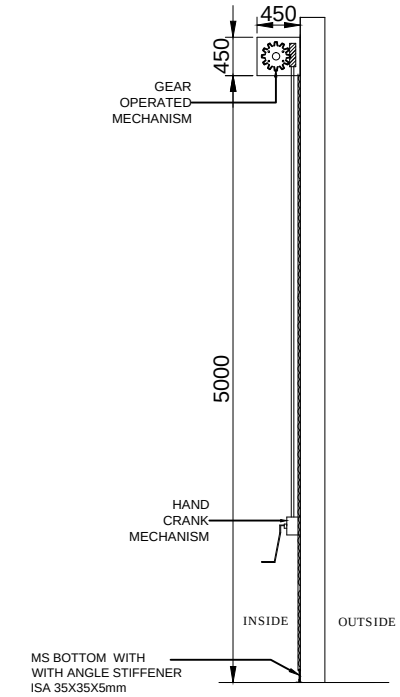



SIDE VIEW

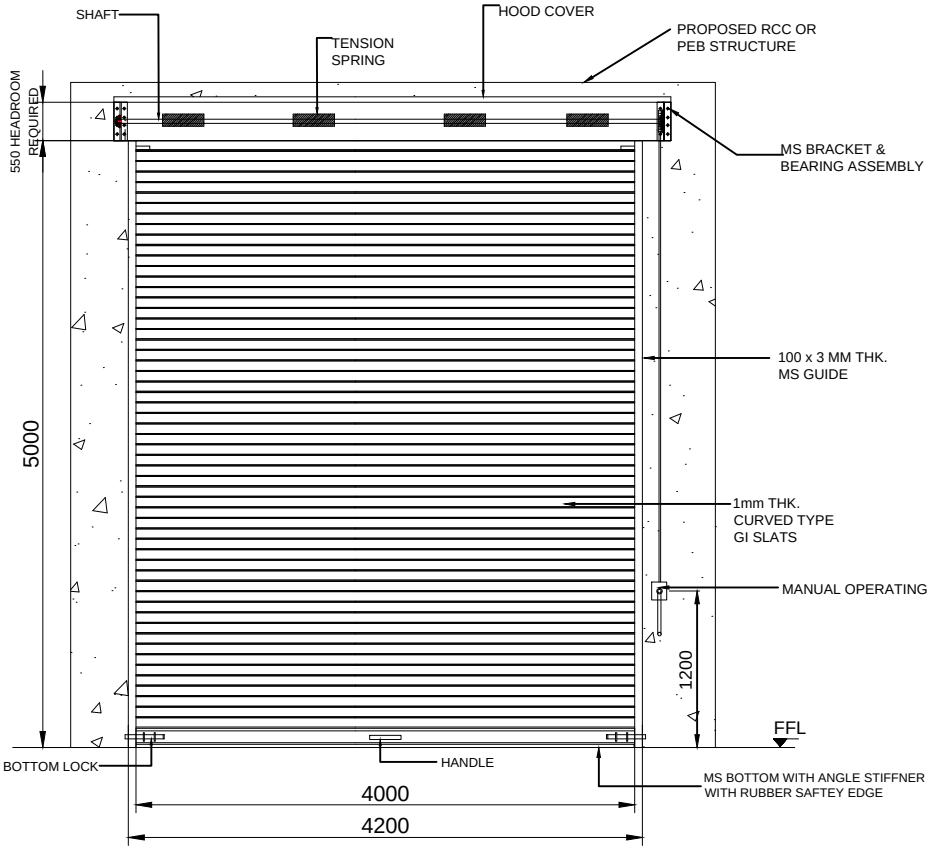


INSIDE ELEVATION

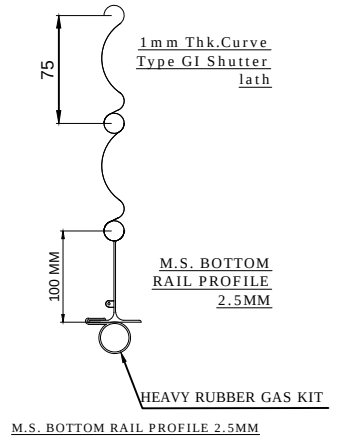

M.S. BOTTOM RAIL PROFILE 2.5MM

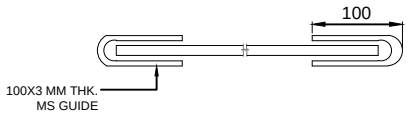

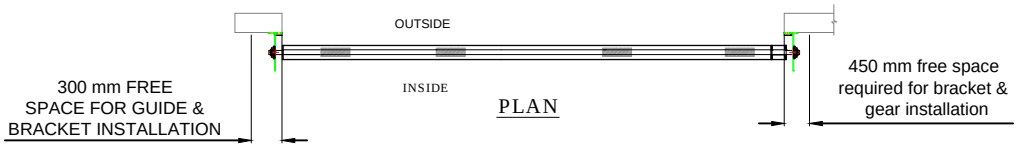

PLAN

TOLERANCE - ±10mm

S.N.	LOCATION	SIZE	QUANTITY
1	B6A	4000(W)X5000(H)	01

NOTE-
1. ALL CIVIL WORK WILL BE CLIENT'S SCOPE.
2.STRUCTURE REQUIRED FOR SHUTTER IS IN CLIENT'S SCOPE.
3.FINAL FINISH OF SHUTTER WILL BE IN POWDER COATING OF APPROVED COLOR i.e. RAL 7001.

This drawing & design is the property of NIHVA TECHNOLOGIES. Not to be sold or copied to any other concern.

TITLE	GEAR OPERATED ROLLING SHUTTER 4mX5m With Right side gearbox		
	NAME	SIGN	DATE
DRAWN	SURAJ		21.08.2018
CHECK	PRADEEP		21.08.2018
APPRD.	R.D		21.08.2018

NIHVA TECHNOLOGIES PVT. LTD.
Website:- www.nihva.com
NIHVA TECHNOLOGIES PVT. LTD. PUNE
Tel : 020 66304033
Email:- info@nihva.com

CLIENT - INDOSPACE
PROJECT - BUILDING B6A
SITE LOCATION - CHAKAN 1

If any queries contact : design@nihva.com
DWG. NO. : NIHVA/18-19/0099
REV- 0
ALL DIMENSION ARE IN mm
SCALE: NTS
WT:
SHEET: 01 OF 01