

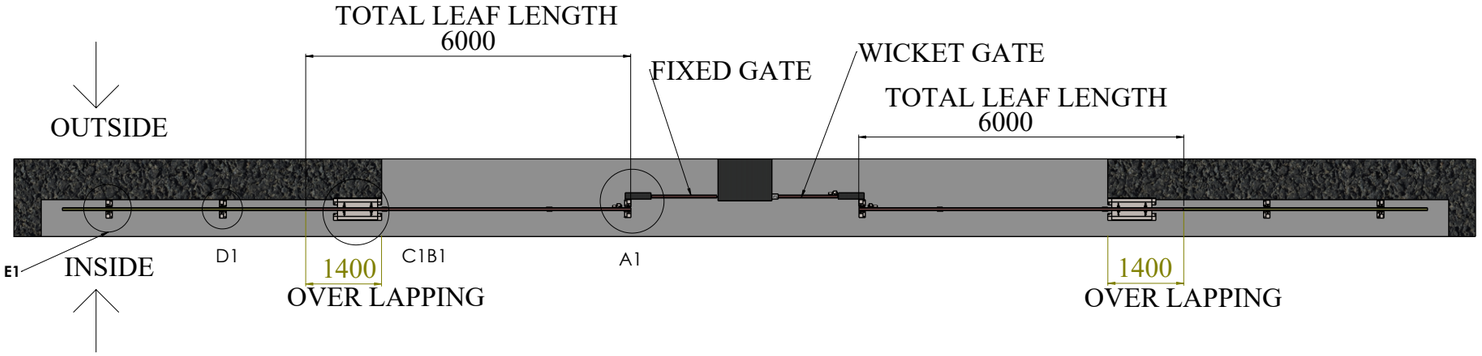
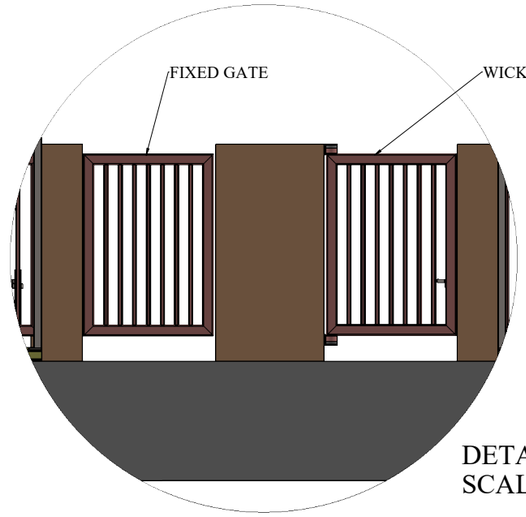




DETAIL E1
SCALE 1 : 20

FIXED GATE AND SWING
GATE VIEW

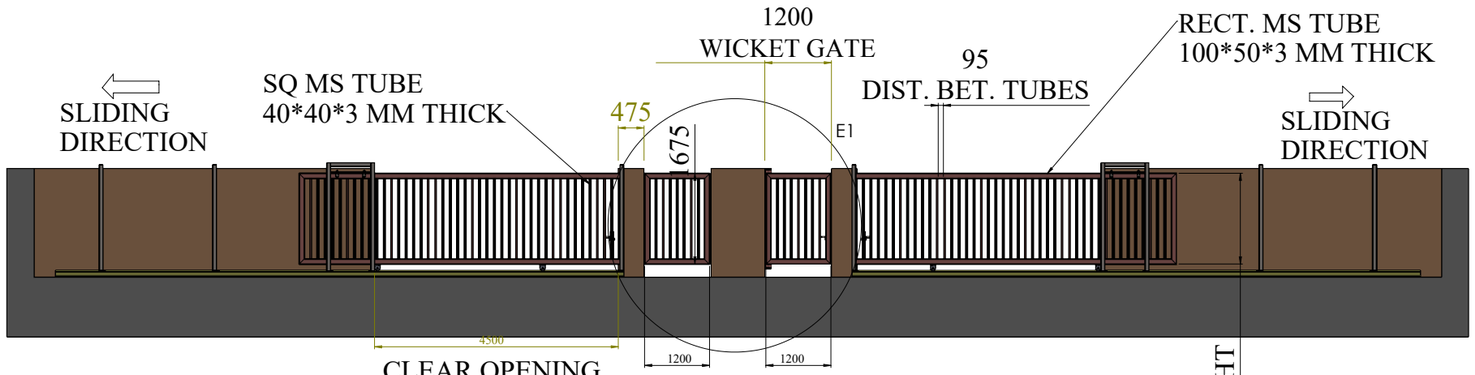


DETAIL D1
SCALE 1 : 4

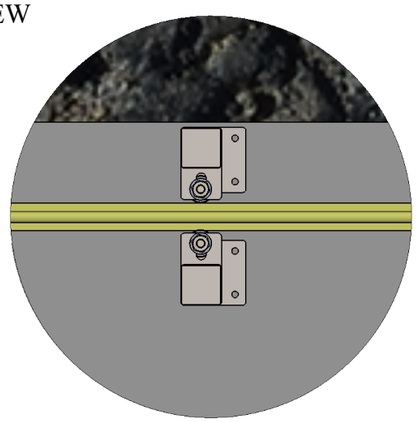


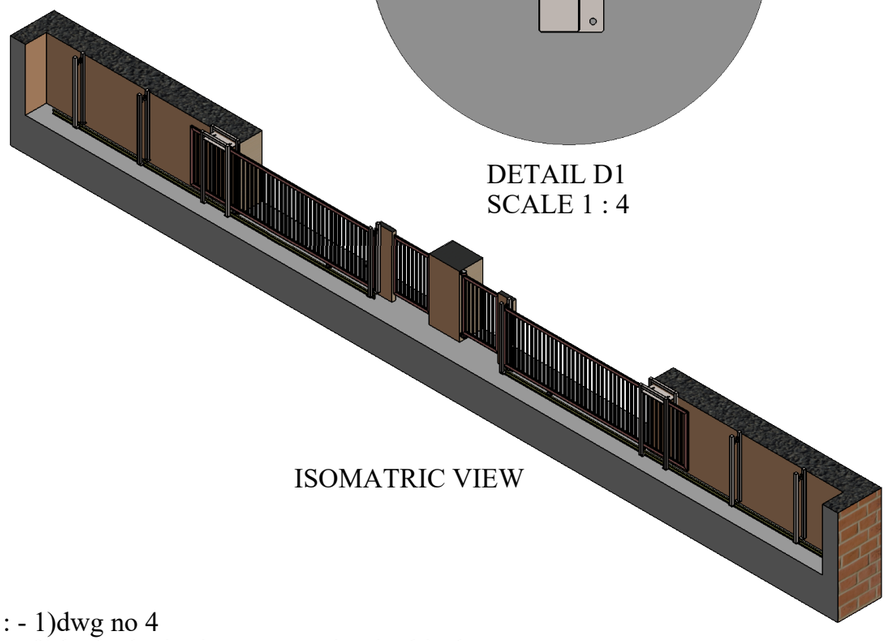ISOMATRIC VIEW

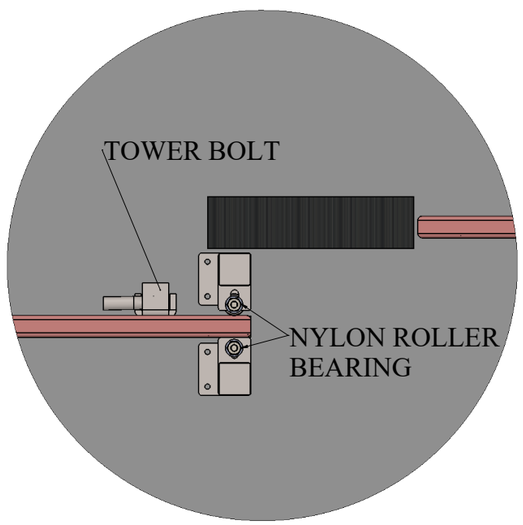


POST 1 AND NYLON ROLLER
BEARING ASSEM.

DETAIL A1
SCALE 1 : 5

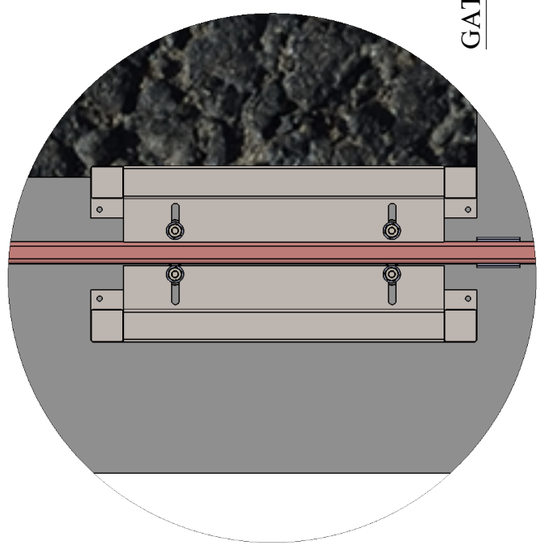

POST 2 AND NYLON ROLLER
BEARING ASSEM.

DETAIL C1B1
SCALE 1 : 5

Note : - 1)dwg no 4
2) barbed wire is not menstion in this dwg.
3)Total column -10(A1,B1,C1,D1,E1 SAME AS RIGHT SIDE ADD 5 POST )
4) 03 column posts when the gates is in the closed position.(A1,B1,C1)
5) 04 column posts when the gates is in the fully open position.(B1,C1,D1,E1)


| | | | | | |
|---|---|---|---|---|---|
| TITLE - GATE AUTOMATION | | | | NIHVA TECHNOLOGIES PVT.LTD.PUNE Website - www.nihva.com | |
| DWG NO - NTPL-290-PM-004 | | | | PRODUCT - SLIDING_GATE | |
| | NAME | SIGNATURE | DATE | PROJECT NO - NTPL-290-PM | REVISION - 00 |
| DRAWN | V.W. | | 29-07-2025 | SITE LOCATION - AMRAVATI | WEIGHT - |
| CHKD | B.S. | | 29-07-2025 | MATRIAL - | QTY - 1 |
| APP'D | V.T. | | 29-07-2025 | | |
| If any queries contact - design@nihva.com | | | | PROJECTION METHOD: | SCALE : |
| ALL DIMENSION ARE IN mm | | | A3 | | SHEET 1 OF 1 |





| ITEM NO. | PART NUMBER | DESCRIPTION | QTY. |
|---|---|---|---|
| 1 | CIVIL BASE | 27000 (L) X3100 (H) | 1 |
| 2 | EN8 & ISMB BEAM | 20 MM (DIA) 10610 MM (L) | 2 |
| 3 | FIXED GATE LEAF | 1200 (W) X1675 (H) | 1 |
| 4 | WICKET GATE LEAF | 1200 (W) X 1675 (H) | 1 |
| 5 | BOTTOM PLATE FOR HINGES | 80X75X6 THK | 2 |
| 6 | DOUBLE POST ASM | 320(L) X350 (W) X1827(H) | 2 |
| 7 | SLIDING GATE LEAF | 6000 (W) X 1675 (H) | 2 |
| 8 | SINGLE POST ASM | 320(L) X75 (W) X1827(H) | 6 |
| 9 | NYLON ROLLER AND BEARING ASM | 75 (H) X 50 (DIA ) | 20 |
| 10 | HEX NUT | M14 | 20 |
| 11 | M14 ANCHOR ASSY | M14 X150 | 82 |
| 12 | NYLON STOPPER | 215X110 X110 | 2 |
| 13 | TOWER BOLT | 300 (L) 15 MM(DIA) & 18 MM DIA & 3 MM THK (HOLLOW PIPE ) | 3 |
| 14 | HINGS | 3 INCH HINGS | 2 |




DETAIL A
SCALE 1 : 15

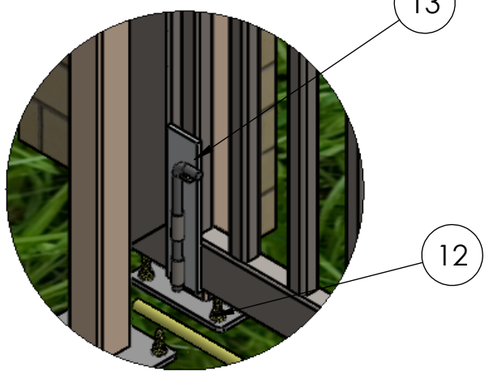



DETAIL C
SCALE 1 : 10

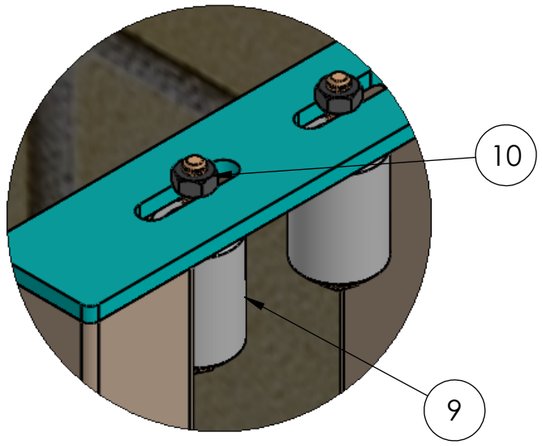



DETAIL B
SCALE 1 : 3

| | | | | |
|---|---|---|---|---|
| TITLE - GATE AUTOMATION | | | | NIHVA TECHNOLOGIES PVT.LTD.PUNE |
| DWG NO - NTPL-290-PM-004 | | | | Website - www.nihva.com |
| | NAME | SIGNATURE | DATE | PROJECT NO - NTPL-290-PM |
| DRAWN | V.B. | | 16-08-2025 | PRODUCT - SLIDING GATE |
| CHK'D | B.S. | | 16-08-2025 | SITE LOCATION - AMRAVATI |
| APPV'D | V.T. | | 16-08-2025 | TYPE 4 |
| if any queries contact - design@nihva.com | | | | REVISION -00 / QTY - 1 |
| ALL DIMENSION ARE IN mm | | A3 | | SCALE - / SHEET 1 OF 1 |

| ITEM NO. | PART NUMBER | DESCRIPTION | QTY. |
|---|---|---|---|
| 1 | SLIDING GATE LEAF | 6000 (L) X 1675 (H) | 2 |
| 2 | WHEEL AND PLATE ASM | 4 INCH WHEEL | 4 |

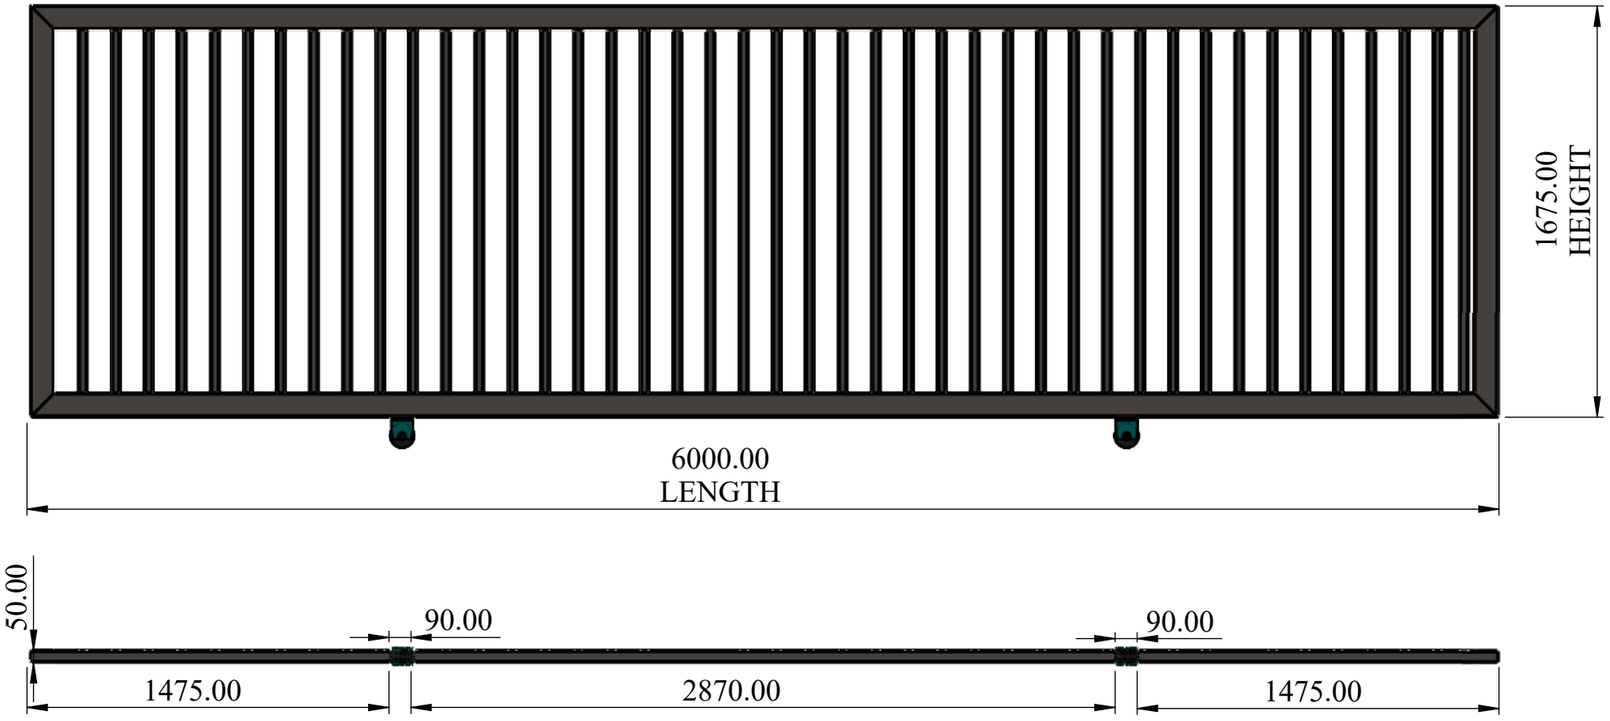


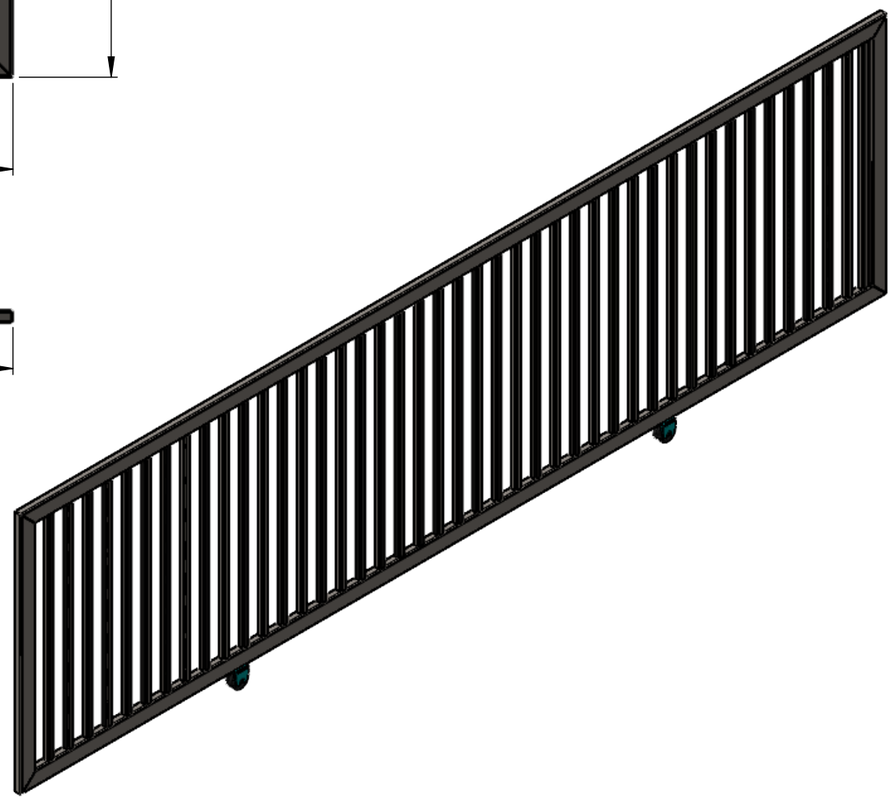



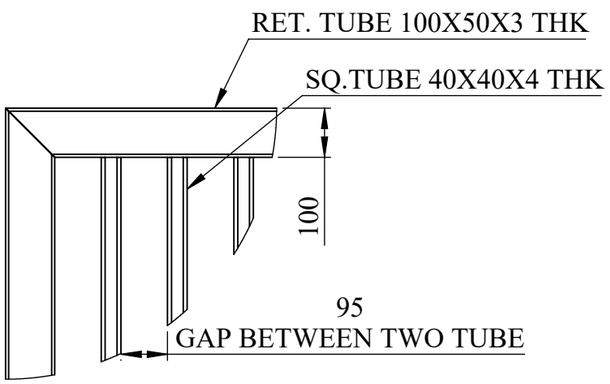
**SLIDING LEAF- 2 NOS**

| | | | | |
|---|---|---|---|---|
| TITLE - GATE AUTOMATION | | | | NIHVA TECHNOLOGIES PVT.LTD.PUNE<br>Website - www.nihva.com |
| DWG NO - NTPL-290-PM-004-01 | | | | |
| | NAME | SIGNATURE | DATE | PROJECT NO - NTPL-290-PM |
| DRAWN | V.B. | | 16-08-2025 | PRODUCT - SLIDING GATE |
| CHK'D | B.S. | | 16-08-2025 | SITE LOCATION - AMRAVATI |
| APPV'D | V.T. | | 16-08-2025 | TYPE 4 |
| if any queries contact - design@nihva.com | | | | REVISION -00 / QTY - 1 |
| ALL DIMENSION ARE IN mm | | A3 | | SCALE - / SHEET 1 OF 18 |

| ITEM NO. | PART NAME | DESCRIPTION | QTY. |
|---|---|---|---|
| | OUTER FRAME | 100X 50 X3 THK | 8 |
| | INNER SQ TUBE | 40 X 40 X 3 THK | 84 |

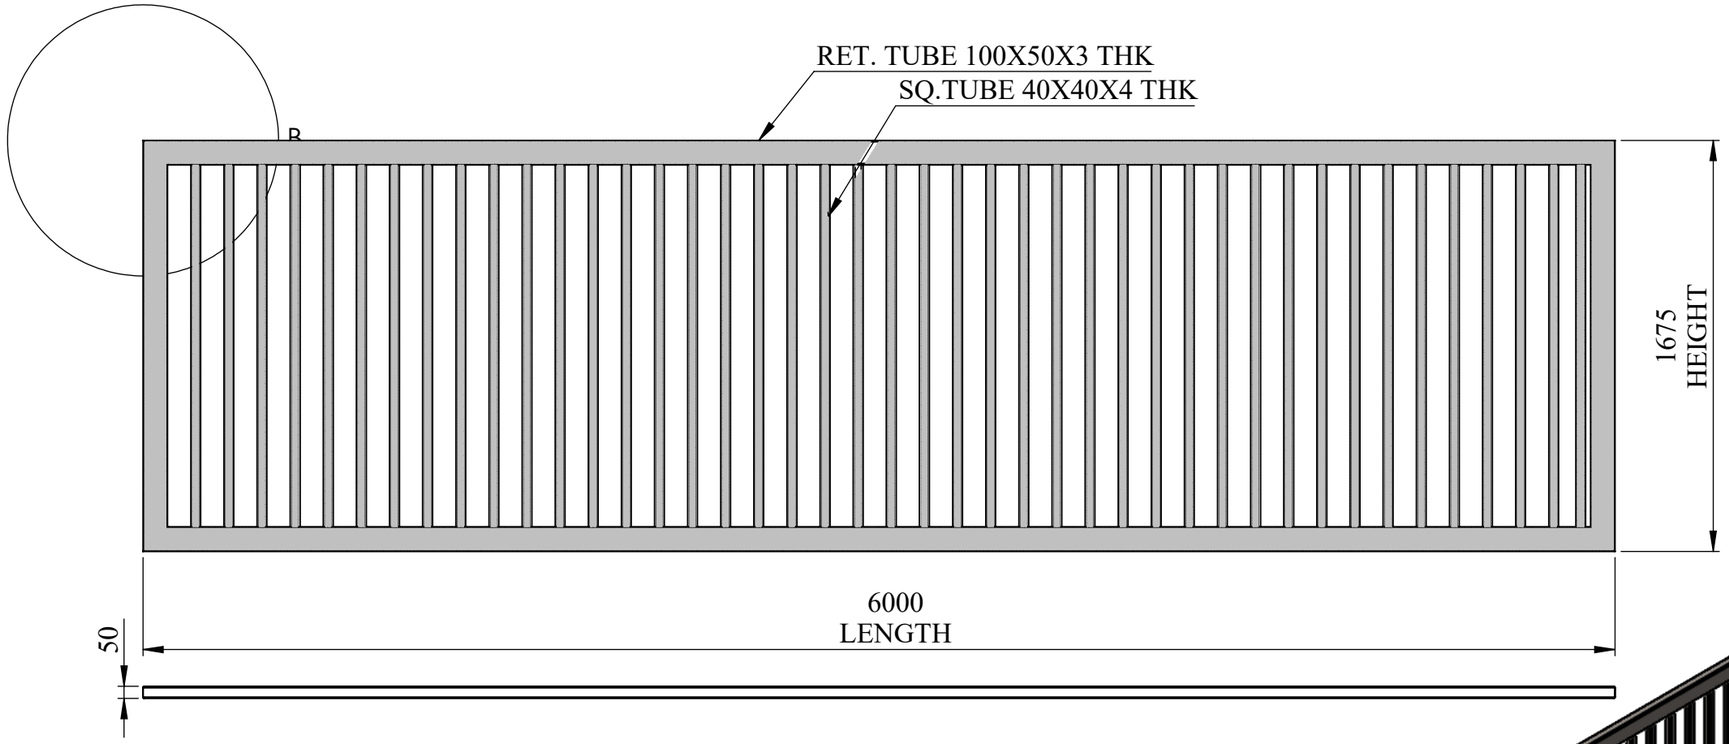

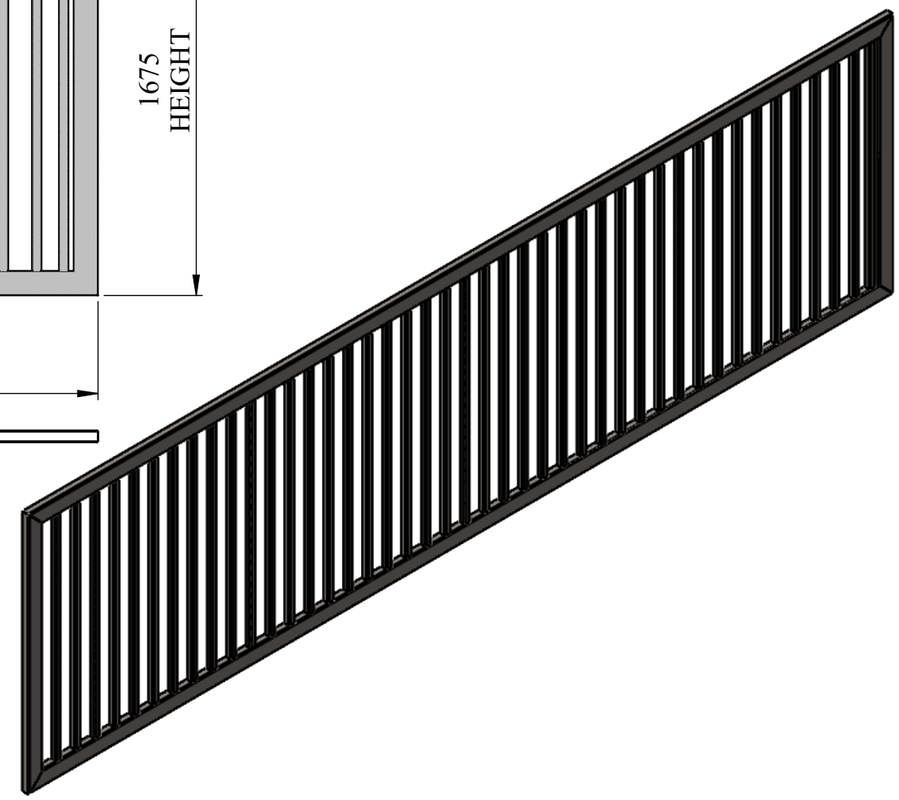




DETAIL B
SCALE 2 : 25

**SUPPORT TUBE**
**QTY-84 NOS FOR TWO LEAF**

| | | | | |
|---|---|---|---|---|
| TITLE - GATE AUTOMATION | | | | NIHVA TECHNOLOGIES PVT.LTD.PUNE |
| DWG NO - NTPL-290-PM-001-01-01 | | | | Website - www.nihva.com |
| | NAME | SIGNATURE | DATE | PROJECT NO - NTPL-290-PM |
| DRAWN | V.B. | | 16-08-2025 | PRODUCT - SLIDING GATE |
| CHK'D | B.S. | | 16-08-2025 | SITE LOCATION - AMRAVATI |
| APPV'D | V.T. | | 16-08-2025 | TYPE 4 |
| if any queries contact - supportautomation@nihva.com | | | | REVISION -00 / QTY - 1 |
| ALL DIMENSION ARE IN mm | | A3 | | SCALE - / SHEET 2 OF 18 |

| ITEM NO. | PART NUMBER | DESCRIPTION | QTY. |
|---|---|---|---|
| 1 | BOTTOM PLATE | 215X150X10 | 12 |
| 2 | SINGLE POST PLATE | 320X75X10 | 6 |
| 3 | VERTICAL TUBE | 75X75X3 | 12 |

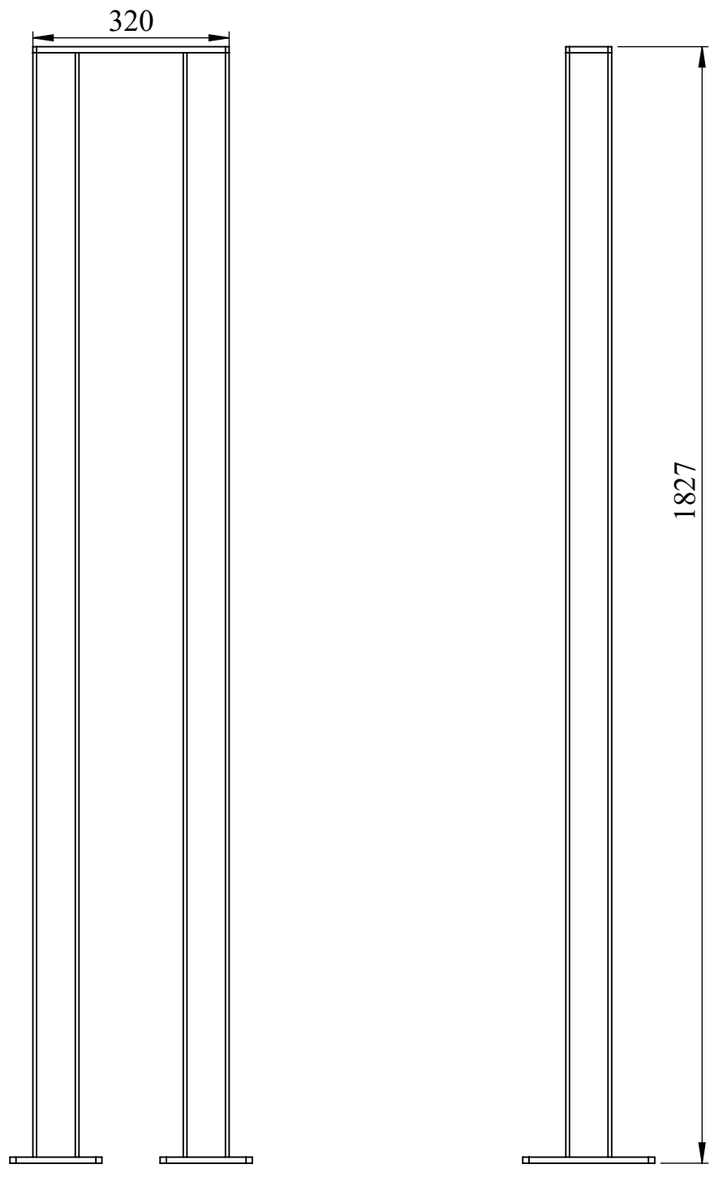


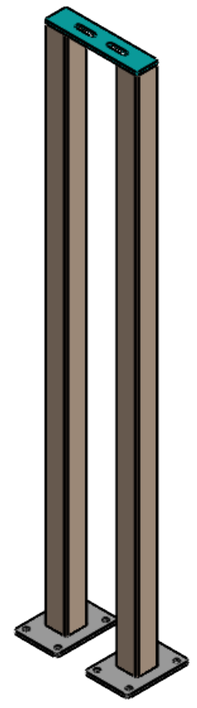



**SINGLE POST ASM**
**QTY- 6 NOS**

| | | | | |
|---|---|---|---|---|
| TITLE -GATE AUTOMATION | | | | NIHVA TECHNOLOGIES PVT.LTD.PUNE<br>Website - www.nihva.com |
| DWG NO - NTPL-290-PM-004-02 | | | | |
| | NAME | SIGNATURE | DATE | PROJECT NO - NTPL-290-PM |
| DRAWN | V.B. | | 16-08-2025 | PRODUCT -SLIDING GATE |
| CHK'D | B.S. | | 16-08-2025 | SITE LOCATION - AMRAVATI |
| APPV'D | V.T. | | 16-08-2025 | TYPE 4 |
| if any queries contact - design@nihva.com | | | | REVISION -00 / QTY - 1 |
| ALL DIMENSION ARE IN mm | | A3 | | SCALE - / SHEET 3 OF 18 |

| ITEM NO. | PART NUMBER | DESCRIPTION | QTY. |
|---|---|---|---|
| 1 | SINGLE POST PLATE | 320X75X10 | 6 |

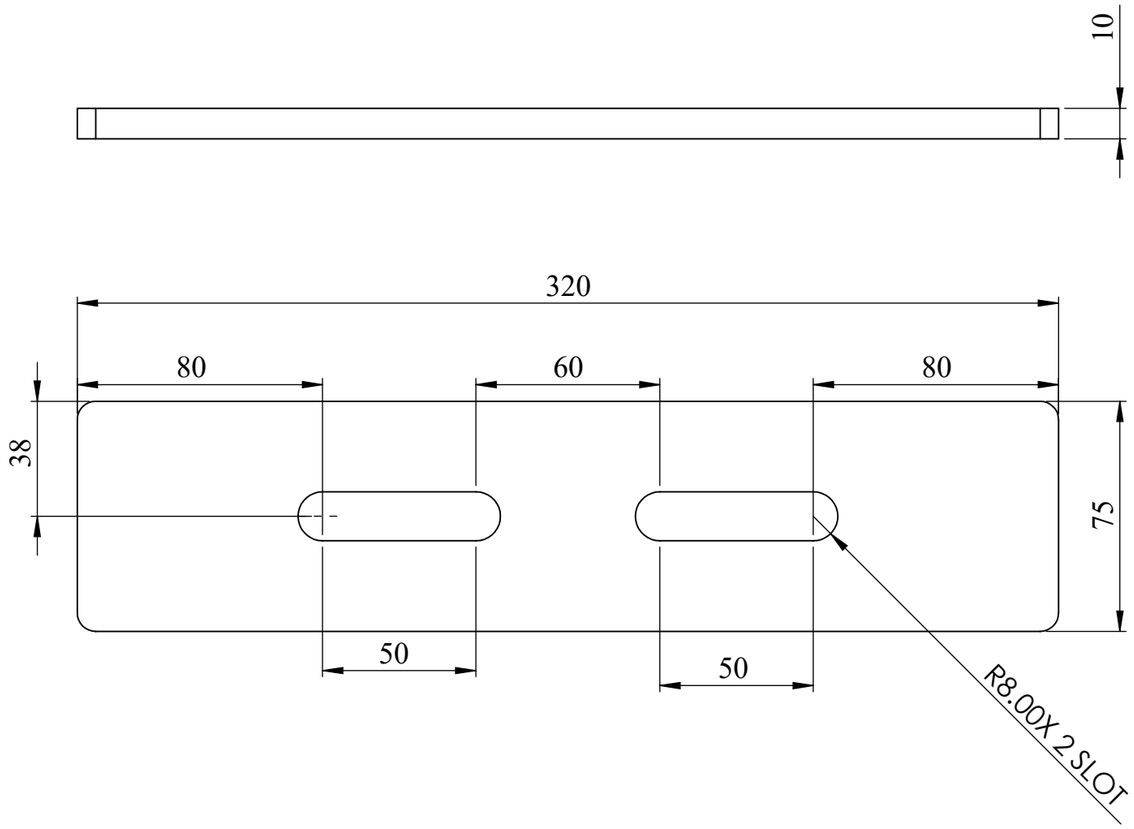


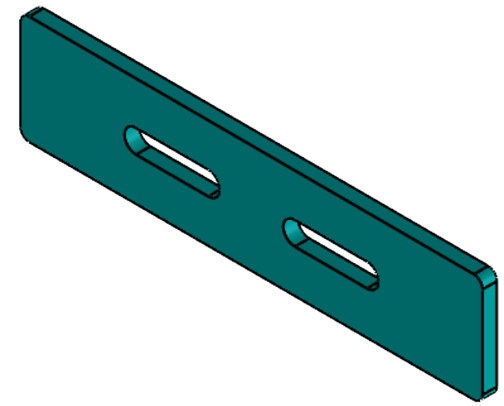



**SINGLE POST PLATE**
**320X75X10 MM THK**
**QTY-6 NOS**

| | | | | |
|---|---|---|---|---|
| TITLE -GATE AUTOMATION | | | | NIHVA TECHNOLOGIES PVT.LTD.PUNE<br>Website - www.nihva.com |
| DWG NO - NTPL-290-PM-004-02-01 | | | | |
| | NAME | SIGNATURE | DATE | PROJECT NO - NTPL-290-PM |
| DRAWN | V.B. | | 16-08-2025 | PRODUCT - SLIDING GATE |
| CHK'D | B.S. | | 16-08-2025 | SITE LOCATION - AMRAVATI |
| APPV'D | V.T. | | 16-08-2025 | TYPE 4 |
| if any queries contact - design@nihva.com | | | | REVISION -00 / QTY - 1 |
| ALL DIMENSION ARE IN mm | | A3 | | SCALE - / SHEET 4 OF 18 |

| ITEM NO. | PART NUMBER | DESCRIPTION | QTY. |
|---|---|---|---|
| 1 | VERTICAL SUPPORT TUBE | 75X75X3 | 20 |

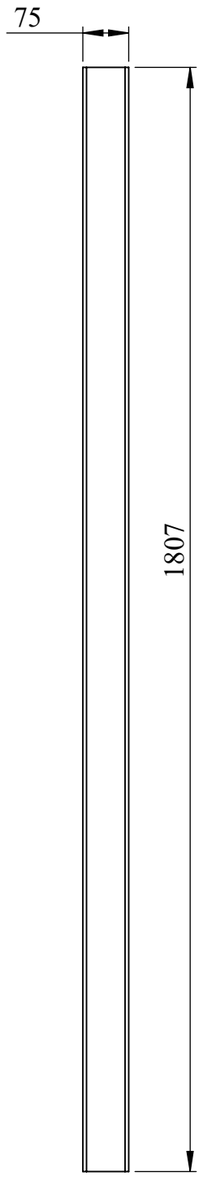


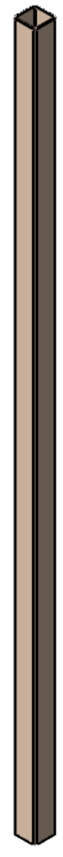



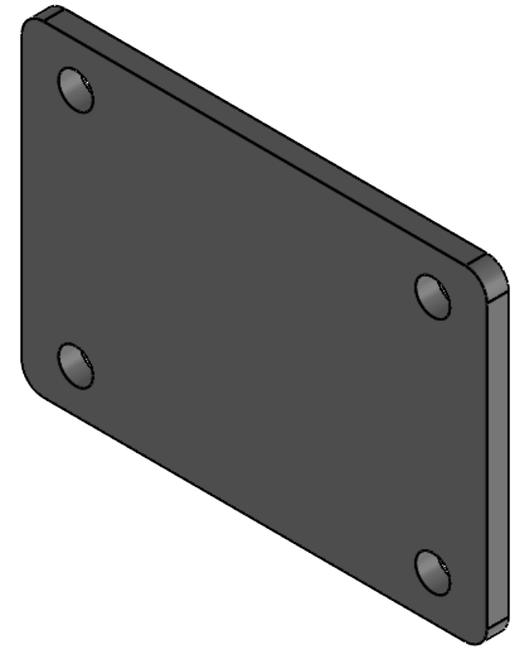
**VERTICAL SUPPORT TUBE**
**75X75X3 MM THK**
**QTY-20 NOS**
**THIS VERTICAL SUPPORT TUBE SAME AS USE DOUBLE POST**

| | | | | |
|---|---|---|---|---|
| TITLE -GATE AUTOMATION | | | | NIHVA TECHNOLOGIES PVT.LTD.PUNE |
| DWG NO - NTPL-290-PM-004-02-02 | | | | Website - www.nihva.com |
| | NAME | SIGNATURE | DATE | PROJECT NO - NTPL-290-PM |
| DRAWN | V.B. | | 14-08-2025 | PRODUCT - SLIDING GATE |
| CHK'D | B.S. | | 14-08-2025 | SITE LOCATION - AMRAVATI |
| APPV'D | V.T. | | 14-08-2025 | TYPE 4 |
| if any queries contact - design@nihva.com | | | | REVISION -00 / QTY - 1 |
| ALL DIMENSION ARE IN mm | | A3 | | SCALE - / SHEET 5 OF 18 |

| ITEM NO. | PART NUMBER | DESCRIPTION | QTY. |
|---|---|---|---|
| 1 | BOTTOM PLATE | 215X150X10 | 20 |

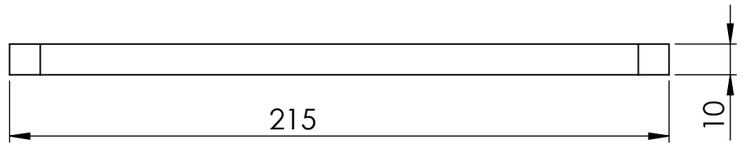

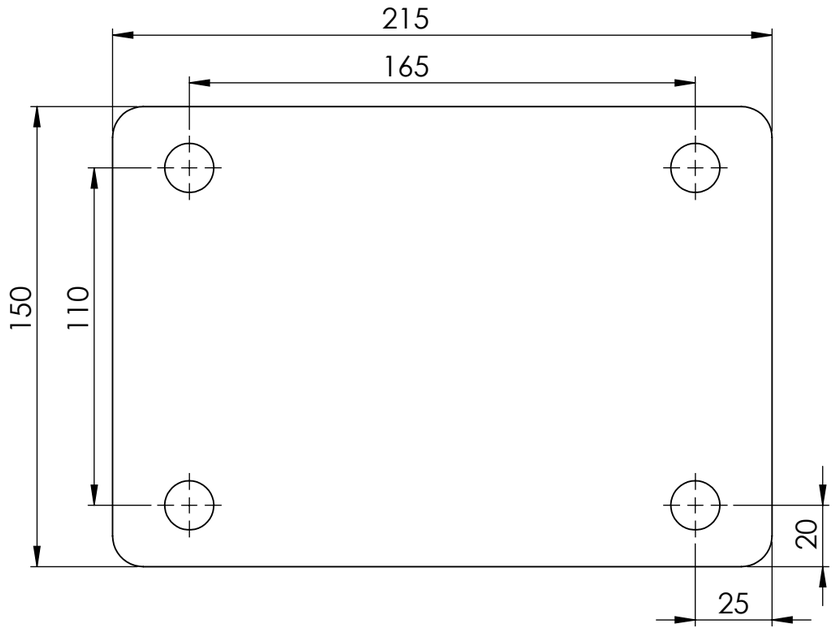



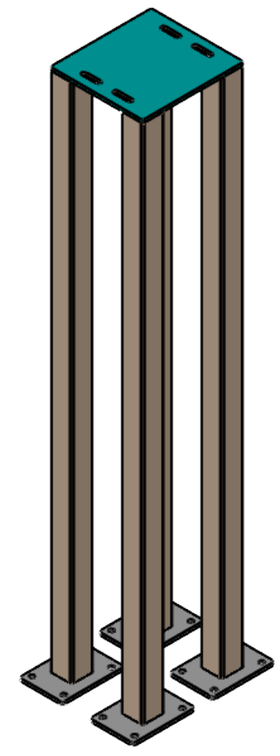



**BOTTOM PLATE FOR POST**
**215X150X10 MM THK**
**QTY-20 NOS**
**THIS BOTTOM PLATE SAME AS USE DOUBLE POST**

| | | | | |
|---|---|---|---|---|
| TITLE -GATE AUTOMATION | | | | NIHVA TECHNOLOGIES PVT.LTD.PUNE |
| DWG NO - NTPL-290-PM-004-02-03 | | | | Website - www.nihva.com |
| | NAME | SIGNATURE | DATE | PROJECT NO - NTPL-290-PM |
| DRAWN | V.B. | | 16-08-2025 | PRODUCT -SLIDING GATE |
| CHK'D | B.S. | | 16-08-2025 | SITE LOCATION - AMRAVATI |
| APPV'D | V.T. | | 16-08-2025 | TYPE 4 |
| if any queries contact - design@nihva.com | | | | REVISION -00 / QTY - 1 |
| ALL DIMENSION ARE IN mm | | A3 | | SCALE - / SHEET 6 OF 18 |

| ITEM NO. | PART NUMBER | DESCRIPTION | QTY. |
|---|---|---|---|
| 1 | BOTTOM PLATE | 215X150X10 | 8 |
| 2 | DOUBLE POST PLATE | 350X320X10 | 2 |
| 3 | VERTICAL TUBE | 75X75X3 | 8 |

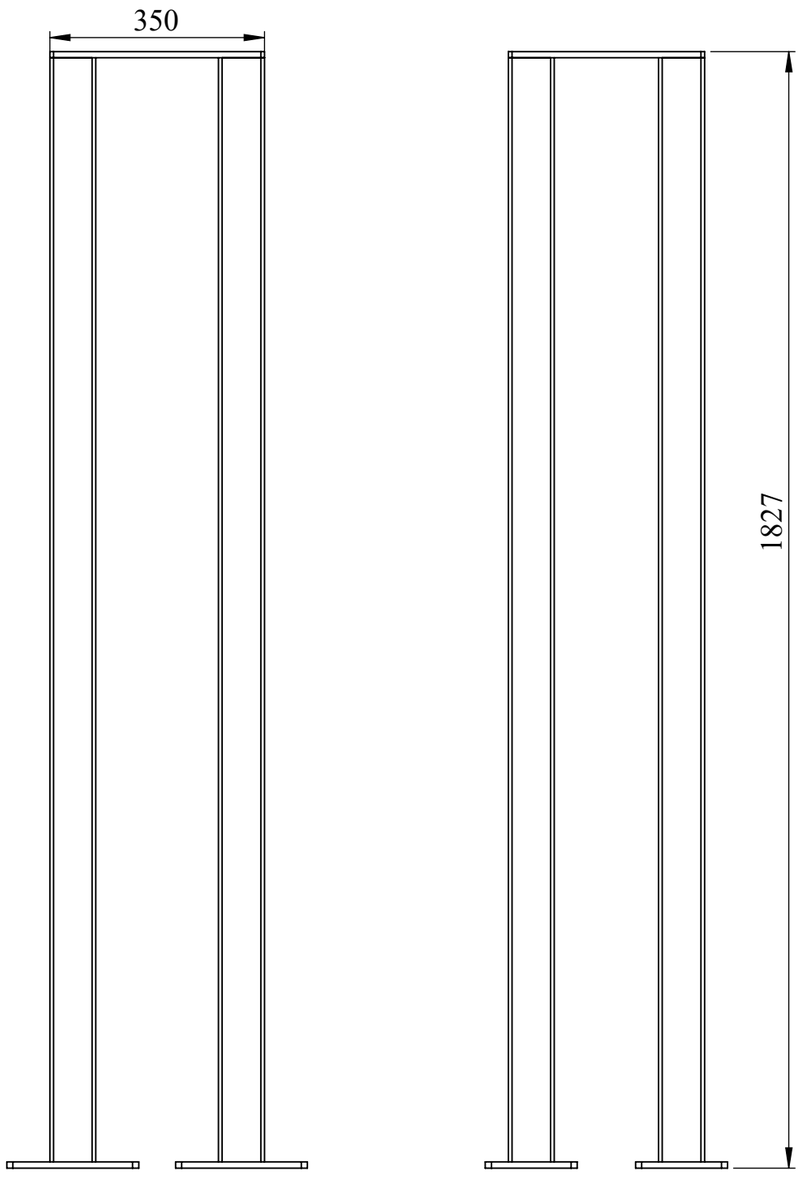





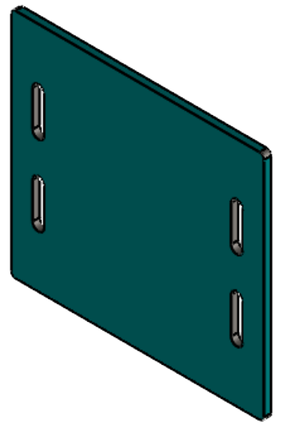
**DOUBLE POST ASM**
**QTY- 2 NOS**

| | | | | |
|---|---|---|---|---|
| TITLE -GATE AUTOMATION | | | | NIHVA TECHNOLOGIES PVT.LTD.PUNE |
| DWG NO - NTPL-290-PM-004-03 | | | | Website - www.nihva.com |
| | NAME | SIGNATURE | DATE | PROJECT NO - NTPL-290-PM |
| DRAWN | V.B. | | 16-08-2025 | PRODUCT - SLIDING GATE |
| CHK'D | B.S. | | 16-08-2025 | SITE LOCATION - AMRAVATI |
| APPV'D | V.T. | | 16-08-2025 | TYPE 4 |
| if any queries contact - design@nihva.com | | | | REVISION -00 / QTY - 1 |
| ALL DIMENSION ARE IN mm | | A3 | | SCALE - / SHEET 7 OF 18 |

| ITEM NO. | PART NUMBER | DESCRIPTION | QTY. |
|---|---|---|---|
| 1 | DOUBLE POST PLATE | 350X320X10 | 2 |



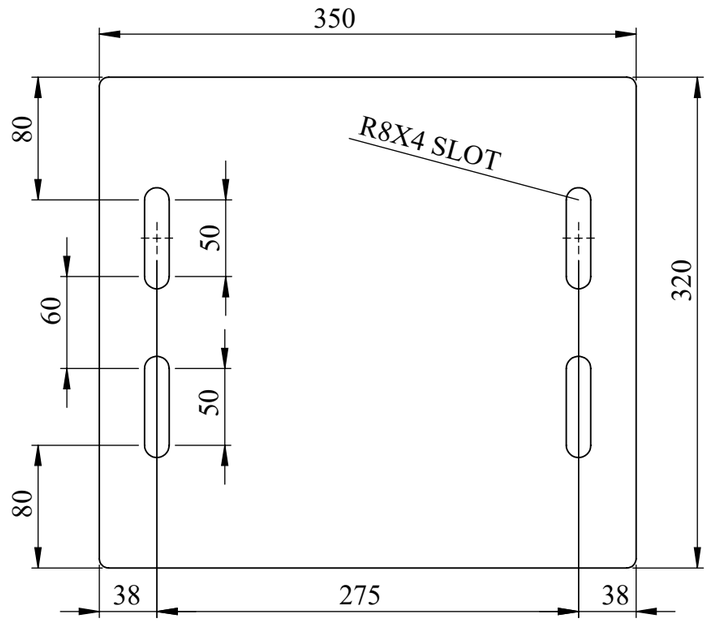



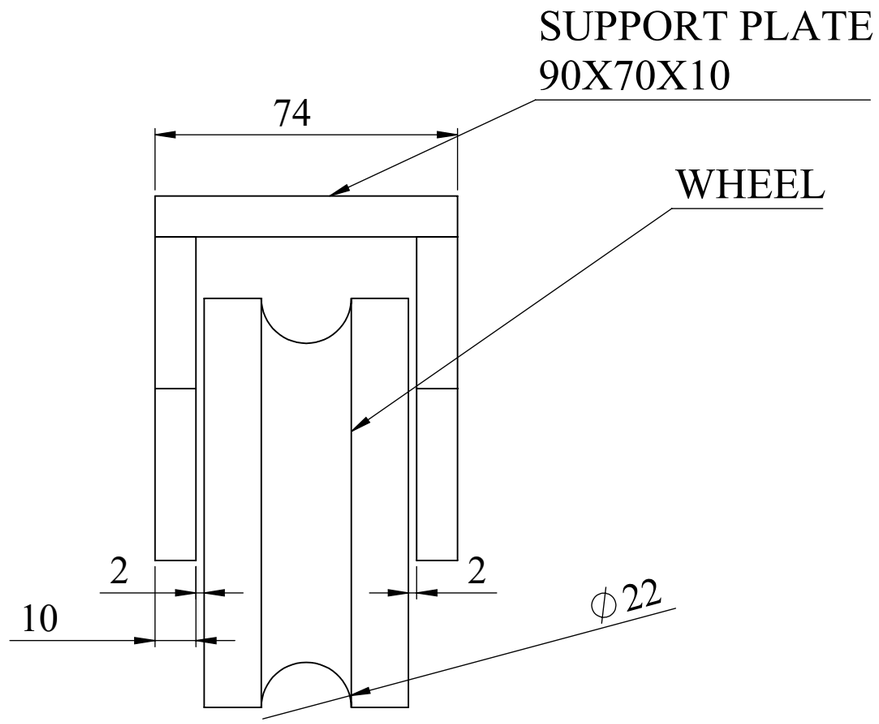



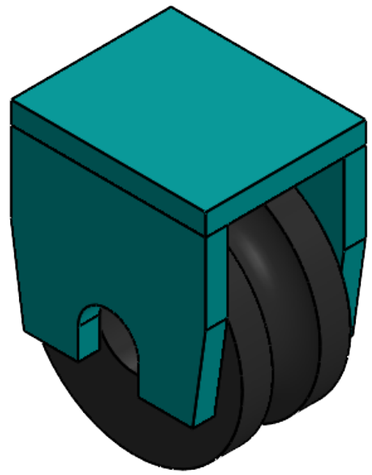
**DOUBLE POST PLATE**
**350X320X10 MM THK**
**QTY-2 NOS**

| | | | | |
|---|---|---|---|---|
| TITLE -GATE AUTOMATION | | | | NIHVA TECHNOLOGIES PVT.LTD.PUNE |
| DWG NO - NTPL-290-PM-004-03-01 | | | | Website - www.nihva.com |
| | NAME | SIGNATURE | DATE | PROJECT NO - NTPL-290-PM |
| DRAWN | V.B. | | 16-08-2025 | PRODUCT -SLIDING GATE |
| CHK'D | B.S. | | 16-08-2025 | SITE LOCATION - AMRAVATI |
| APPV'D | V.T. | | 16-08-2025 | TYPE 4 |
| if any queries contact - design@nihva.com | | | | REVISION -00 / QTY - 1 |
| ALL DIMENSION ARE IN mm | | A3 | | SCALE - / SHEET 8 OF 18 |

| ITEM NO. | PART NUMBER | DESCRIPTION | QTY. |
|---|---|---|---|
| 1 | GUIDE PLATE | ID-14 (H)-79 (W)-10 | 8 |
| 2 | SUPPORT PLATE | 90x74x10 | 4 |
| 3 | WHEEL | 100x50 | 4 |

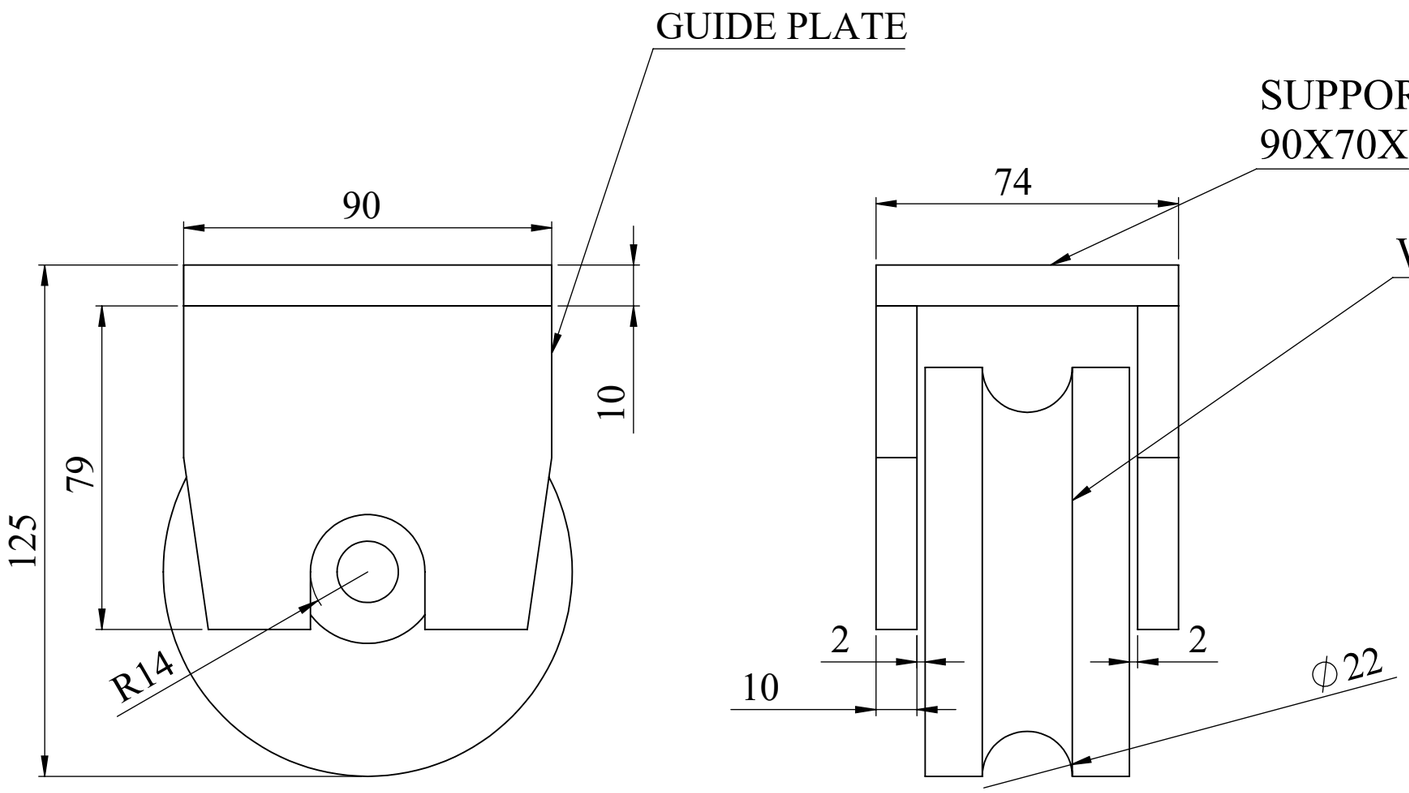





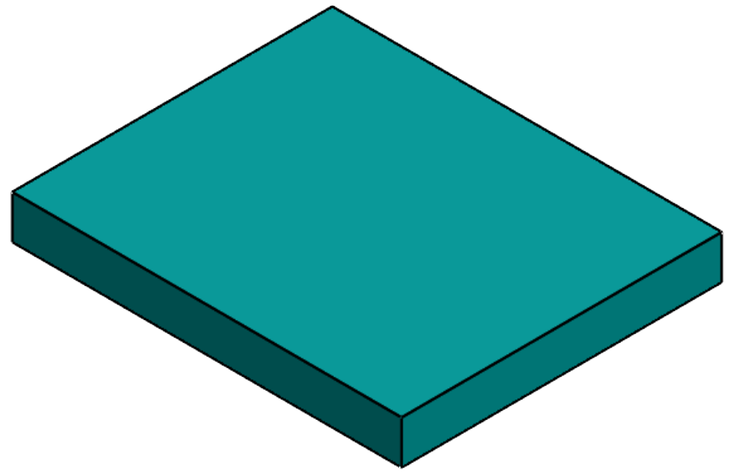



**QTY- 4 NOS**

| | | | | | |
|---|---|---|---|---|---|
| TITLE - GATE AUTOMATION | | | | NIHVA TECHNOLOGIES PVT.LTD.PUNE | |
| DWG NO - NTPL-290-PM-004-01-02 | | | | Website - www.nihva.com | |
| | NAME | SIGNATURE | DATE | PROJECT NO -NTPL-290-PM | |
| DRAWN | V.B. | | 16-08-25 | PRODUCT -SLIDING GATE | |
| CHK'D | B.S. | | 16-08-25 | SITE LOCATION - AMRAVATI | |
| APPV'D | V.T. | | 16-08-25 | TYPE 4 | |
| if any queries contact - design@nihva.com | | | | REVISION -00 | QTY - 1 |
| ALL DIMENSION ARE IN mm | | A3 | | SCALE - | SHEET 9 OF 18 |

| ITEM NO. | PART NUMBER | DESCRIPTION | QTY. |
|---|---|---|---|
| 1 | SUPPORT PLATE | 90x74x10 | 4 |

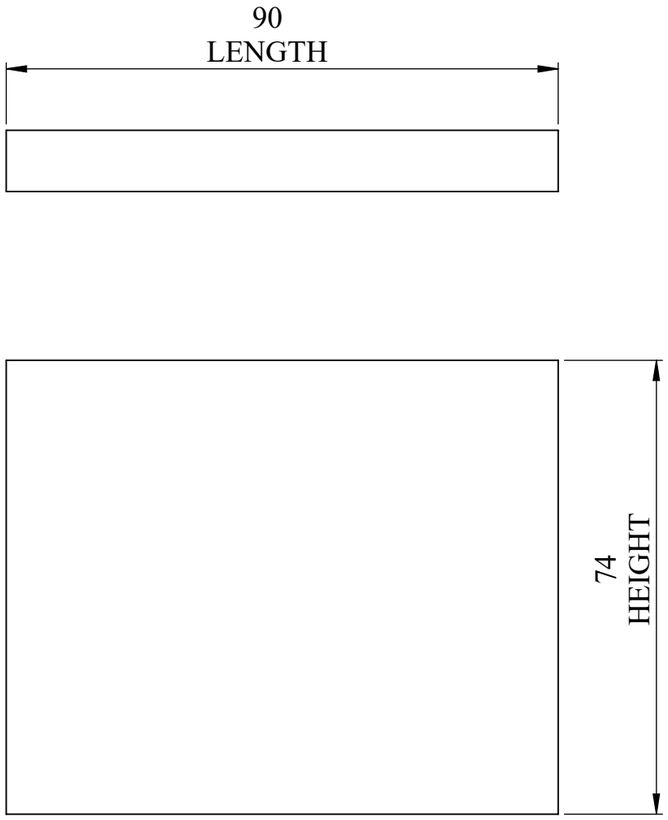






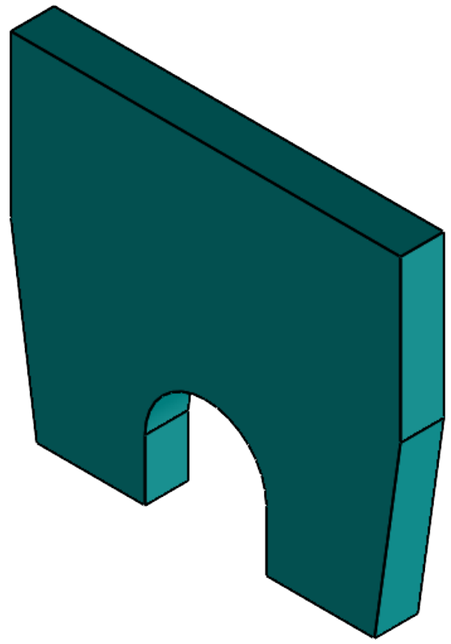
**SUPPORT PLATE**
**QTY- 4 NOS**

| | | | | |
|---|---|---|---|---|
| TITLE - GATE AUTOMATION | | | | NIHVA TECHNOLOGIES PVT.LTD.PUNE |
| DWG NO - NTPL-290-PM-004-01-02-01 | | | | Website - www.nihva.com |
| | NAME | SIGNATURE | DATE | PROJECT NO - NTPL-290-PM |
| DRAWN | V.B. | | 16-08-2025 | PRODUCT - SLIDING GATE |
| CHK'D | B.S. | | 16-08-2025 | SITE LOCATION -AMRAVATI |
| APPV'D | V.T. | | 16-08-2025 | TYPE 4 |
| if any queries contact - design@nihva.com | | | | REVISION -00 / QTY - 1 |
| ALL DIMENSION ARE IN mm | | A3 | | SCALE - / SHEET 10 OF 18 |

| ITEM NO. | PART NUMBER | DESCRIPTION | QTY. |
|---|---|---|---|
| 1 | GUIDE PLATE | ID-14 (H)-79 (W)-10 | 8 |

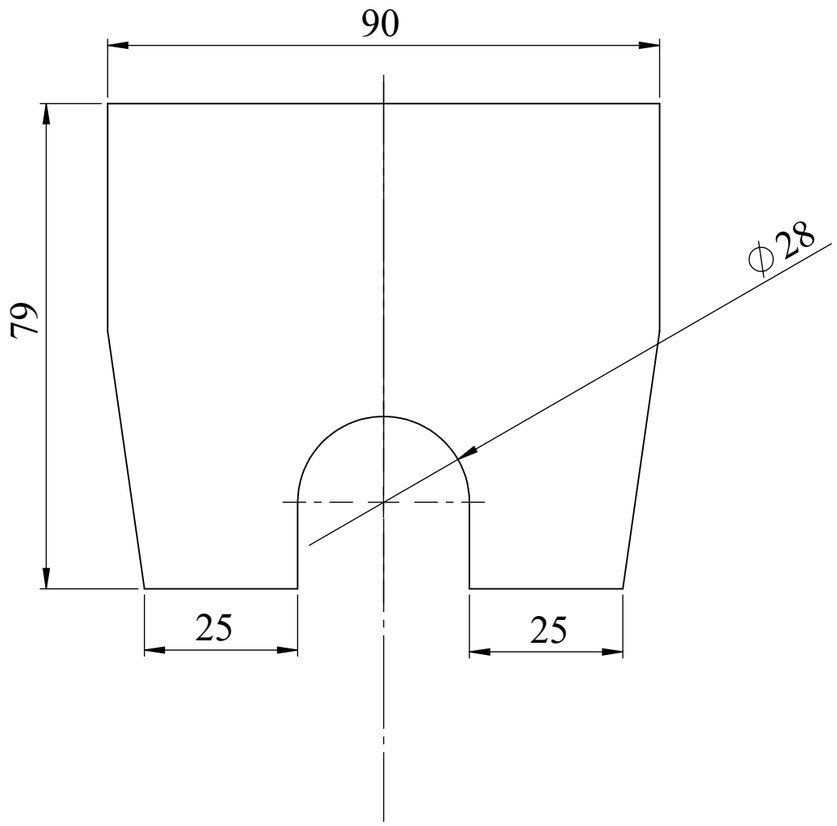

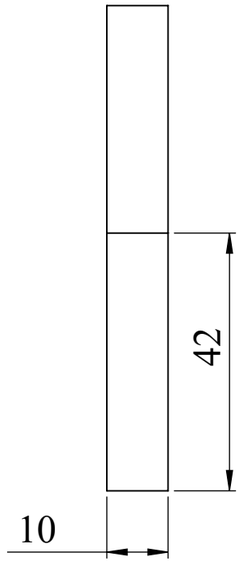



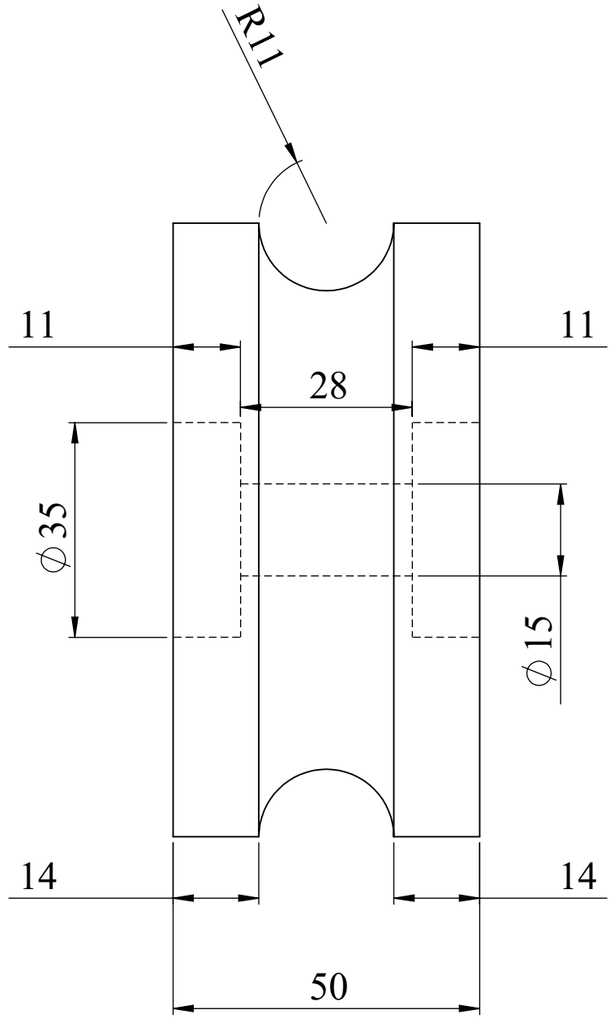



# GUIDE PLATE
# QTY- 8 NOS

| | | | | | |
|---|---|---|---|---|---|
| TITLE - GATE AUTOMATION | | | | NIHVA Technologies Pvt. Ltd. | NIHVA TECHNOLOGIES PVT.LTD.PUNE<br>Website - www.nihva.com |
| DWG NO - NTPL-290-PM-004-01-02-02 | | | | | |
| | NAME | SIGNATURE | DATE | PROJECT NO - NTPL-290-PM | |
| DRAWN | V.B. | | 16-08-2025 | PRODUCT -SLIDING GATE | |
| CHK'D | B.S. | | 16-08-2025 | SITE LOCATION -AMRAVATI | |
| APPV'D | V.T. | | 16-08-2025 | TYPE 4 | |
| if any queries contact - design@nihva.com | | | | REVISION -00 | QTY - 1 |
| ALL DIMENSION ARE IN mm | | A3 | | SCALE - | SHEET 11 OF 18 |

| ITEM NO. | PART NUMBER | DESCRIPTION | QTY. |
|---|---|---|---|
| 1 | WHEEL | 100x50 | 4 |

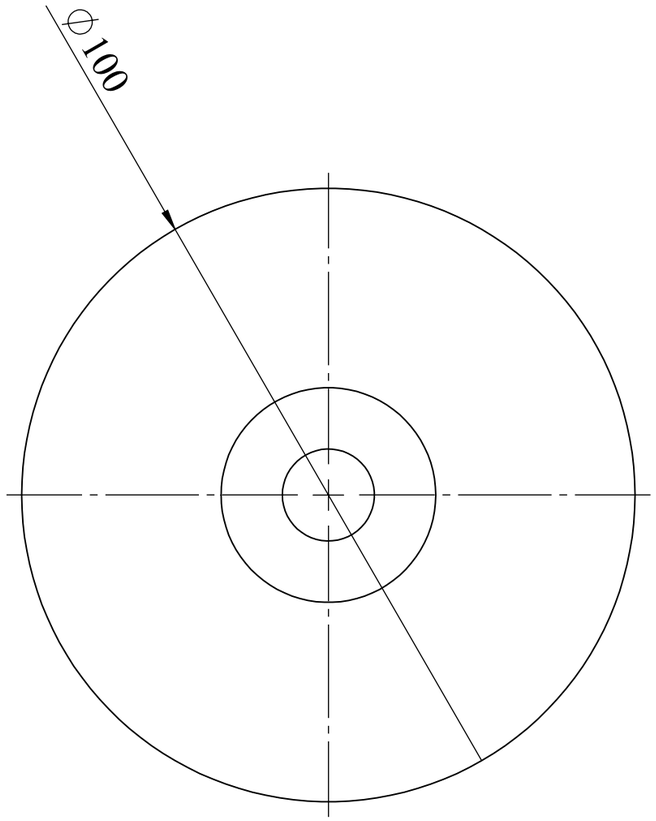








**WHEEL**
**QTY- 4 NOS**

| | | | | |
|---|---|---|---|---|
| TITLE - GATE AUTOMATION | | | | NIHVA TECHNOLOGIES PVT.LTD.PUNE |
| DWG NO - NTPL-290-PM-004-01-02-03 | | | | Website - www.nihva.com |
| | NAME | SIGNATURE | DATE | PROJECT NO - NTPL -290-PM |
| DRAWN | V.B. | | 16-08-2025 | PRODUCT -SLIDING GATE |
| CHK'D | B.S. | | 16-08-2025 | SITE LOCATION -AMRAVATI |
| APPV'D | V.T. | | 16-08-2025 | TYPE 4 |
| if any queries contact - design@nihva.com | | | | REVISION -00 / QTY - 1 |
| ALL DIMENSION ARE IN mm | | A3 | | SCALE - / SHEET 12 OF 18 |
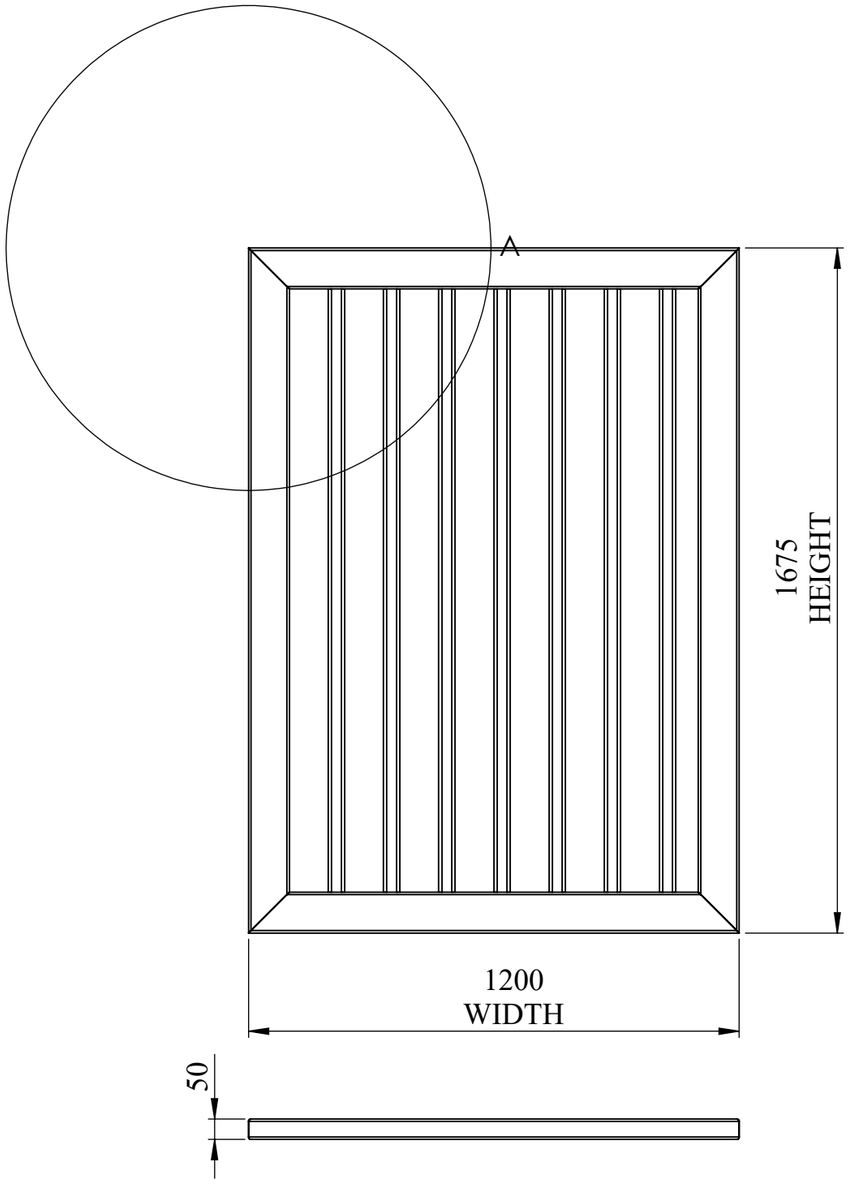
| ITEM NO. | PART NUMBER | DESCRIPTION | QTY. |
|---|---|---|---|
| 1 | WICKET GATE | 1200 (W)x1675 (H) | 1 |








DETAIL A
SCALE 2 : 15



**SUPPORT TUBE**
**QTY-7 NOS**

| | | | | |
|---|---|---|---|---|
| TITLE - GATE AUTOMATION | | | | NIHVA TECHNOLOGIES PVT.LTD.PUNE<br>Website - www.nihva.com |
| DWG NO - NTPL-290-PM-004-04 | | | | |
| | NAME | SIGNATURE | DATE | PROJECT NO - NTPL-290-PM |
| DRAWN | V.B. | | 16-08-2025 | PRODUCT - SLIDING GATE |
| CHK'D | B.S. | | 16-08-2025 | SITE LOCATION - AMRAVATI |
| APPV'D | V.T. | | 16-08-2025 | TYPE 4 |
| if any queries contact - design@nihva.com | | | | REVISION -00 / QTY - 1 |
| ALL DIMENSION ARE IN mm | | A3 | | SCALE - / SHEET 1 OF 2 |


| ITEM NO. | PART NUMBER | DESCRIPTION | QTY. |
|---|---|---|---|
| 1 | FIXED GATE | 1200 (W)x1675 (H) | 1 |

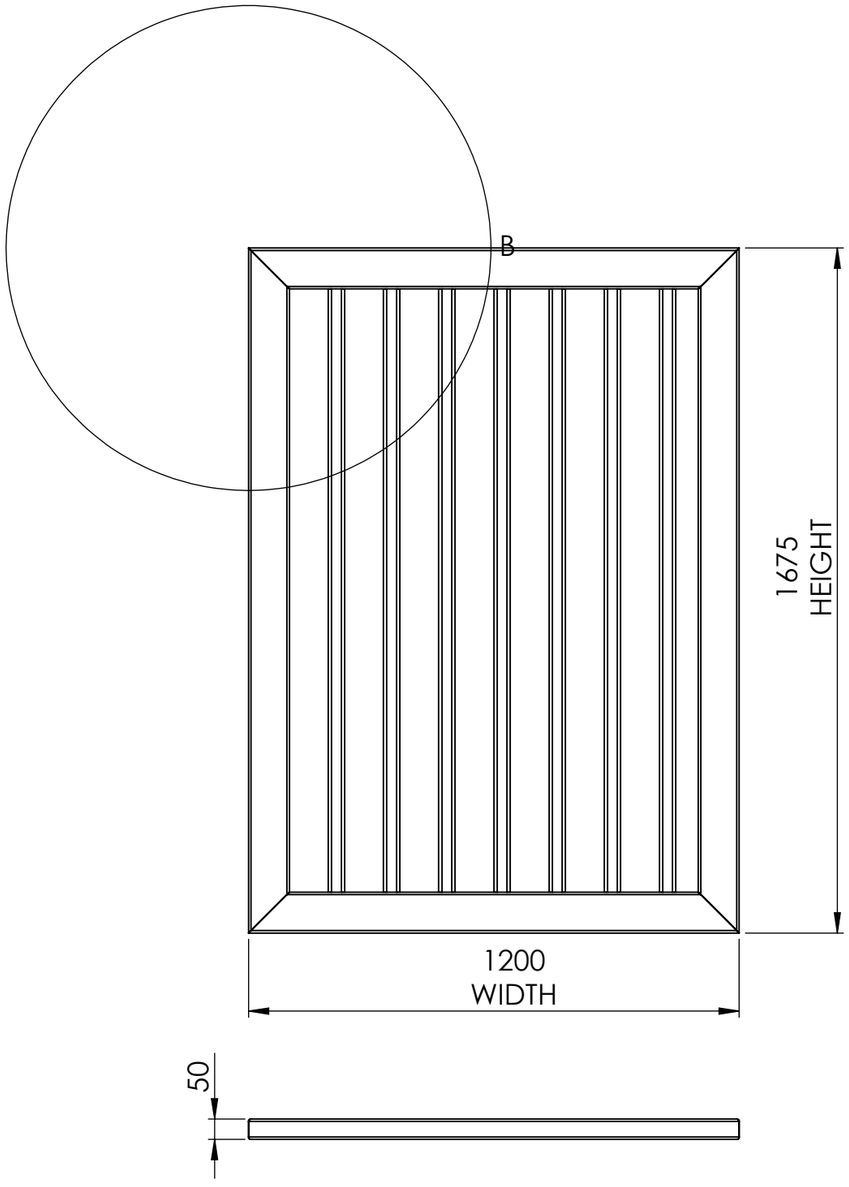






DETAIL B
SCALE 2 : 15

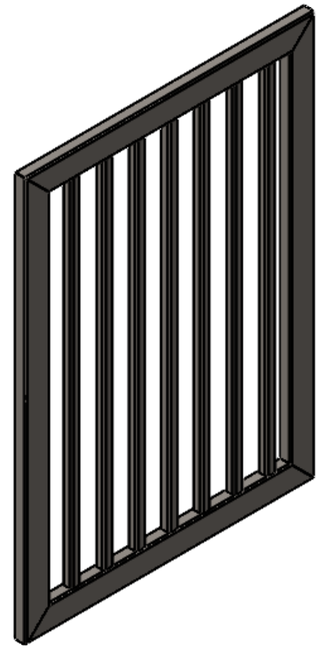



**SUPPORT TUBE**
**QTY-7 NOS**

| | | | | |
|---|---|---|---|---|
| TITLE - GATE AUTOMATION | | | | NIHVA TECHNOLOGIES PVT.LTD.PUNE |
| DWG NO - NTPL-290-PM-004-05 | | | | Website - www.nihva.com |
| | NAME | SIGNATURE | DATE | PROJECT NO - NTPL-290-PM |
| DRAWN | V.B. | | 16-08-2025 | PRODUCT - SLIDING GATE |
| CHK'D | B.S. | | 16-08-2025 | SITE LOCATION - AMRAVATI |
| APPV'D | V.T. | | 16-08-2025 | TYPE 4 |
| if any queries contact - design@nihva.com | | | | REVISION -00 / QTY - 1 |
| ALL DIMENSION ARE IN mm | | A3 | | SCALE - / SHEET 2 OF 2 |

| ITEM NO. | PART NUMBER | DESCRIPTION | QTY. |
|---|---|---|---|
| 1 | EN8 BAR | OD- 20 MM | 2 |
| | ISMB BEAM | SIZE- 100 X 50 10610MM (L) | 2 |

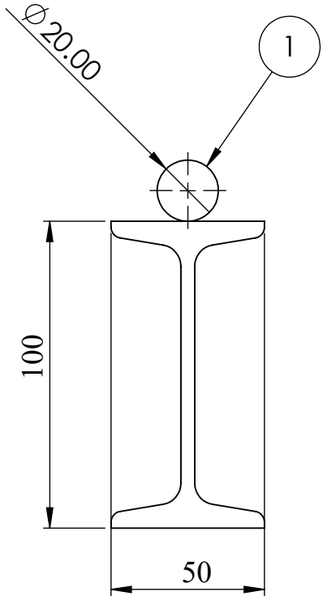

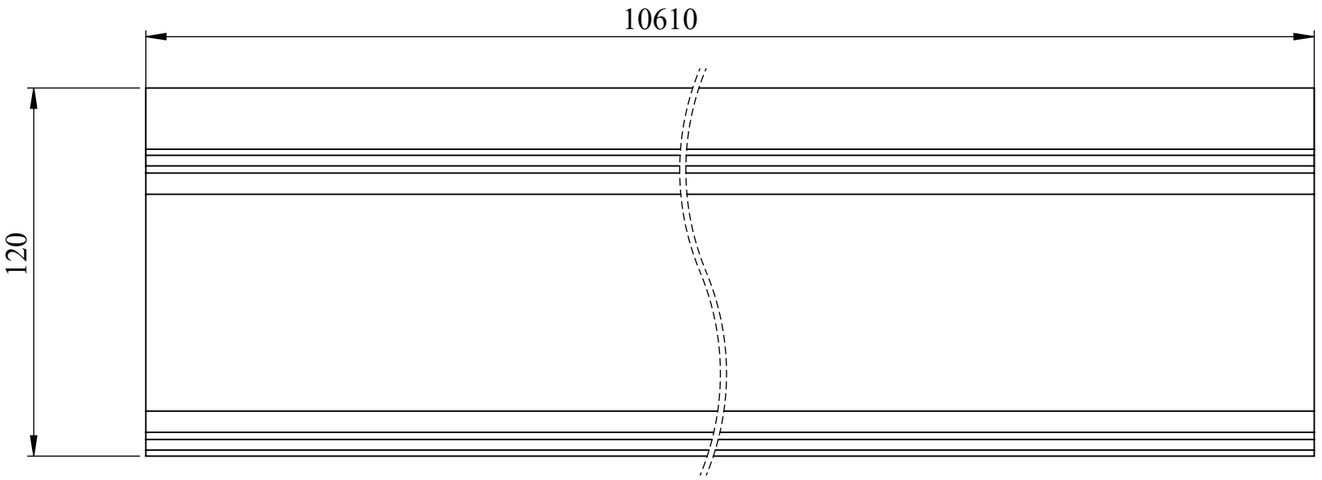


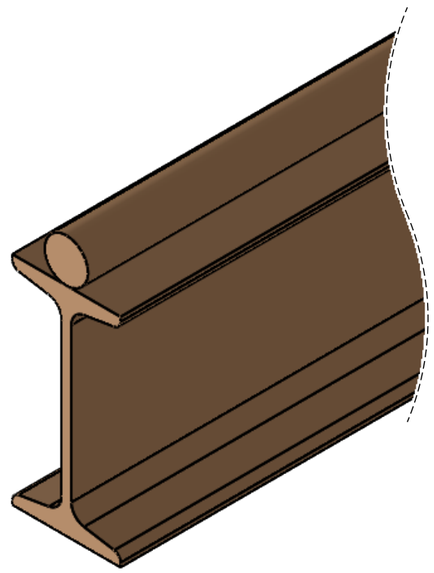
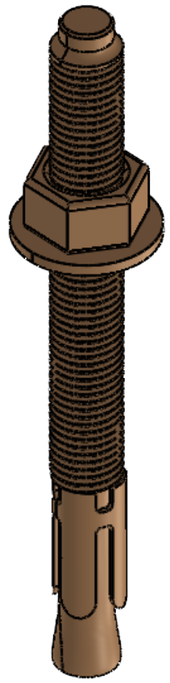



**GATE TRACK**
**QTY- 2NOS**

| | | | | | |
|---|---|---|---|---|---|
| TITLE - GATE AUTOMATION | | | | NIHVA Technologies Pvt. Ltd. | NIHVA TECHNOLOGIES PVT.LTD.PUNE<br>Website - www.nihva.com |
| DWG NO - NTPL-290-PM-004-06 | | | | | |
| | NAME | SIGNATURE | DATE | PROJECT NO - NTPL-290-PM | |
| DRAWN | V.B. | | 16-08-2025 | PRODUCT -SLIDING GATE | |
| CHK'D | B.S. | | 16-08-2025 | SITE LOCATION - AMRAVATI | |
| APPV'D | V.T. | | 16-08-2025 | TYPE-4 | |
| if any queries contact - design@nihva.com | | | | REVISION -00 | QTY - 1 |
| ALL DIMENSION ARE IN mm | | | A3 | SCALE - | SHEET 13 OF 21 |

| ITEM NO. | PART NUMBER | DESCRIPTION | QTY. |
|---|---|---|---|
| 1 | M14 ANCHOR | M14X150 | 70 |

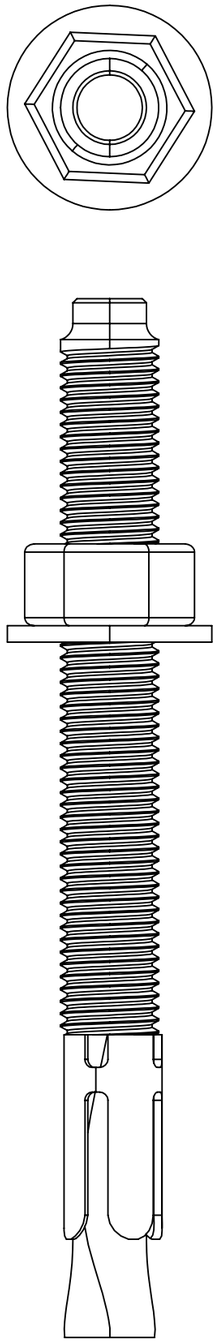





**NOTE -**
**M14 X 150 MM ANCHOR BOLT**
**QTY- 70 NOS**


| | | | | |
|---|---|---|---|---|
| TITLE -GATE AUTOMATION | | | | NIHVA TECHNOLOGIES PVT.LTD.PUNE |
| DWG NO - NTPL-290-PM-004-07 | | | | Website - www.nihva.com |
| | NAME | SIGNATURE | DATE | PROJECT NO - NTPL-290-PM |
| DRAWN | V.B. | | 16-08-2025 | PRODUCT -SLIDING GATE |
| CHK'D | B.S. | | 16-08-2025 | SITE LOCATION - AMRAVATI |
| APPV'D | V.T. | | 16-08-2025 | TYPE 4 |
| if any queries contact - design@nihva.com | | | | REVISION -00 / QTY - 1 |
| ALL DIMENSION ARE IN mm | | A3 | | SCALE - / SHEET 14 OF 21 |

| ITEM NO. | PART NUMBER | DESCRIPTION | QTY. |
|---|---|---|---|
| 1 | NYLON STOPPER | | 2 |
| 2 | NYLON STOPPER PLATE | 135X135X10 | 2 |

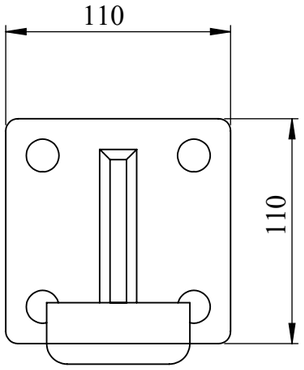


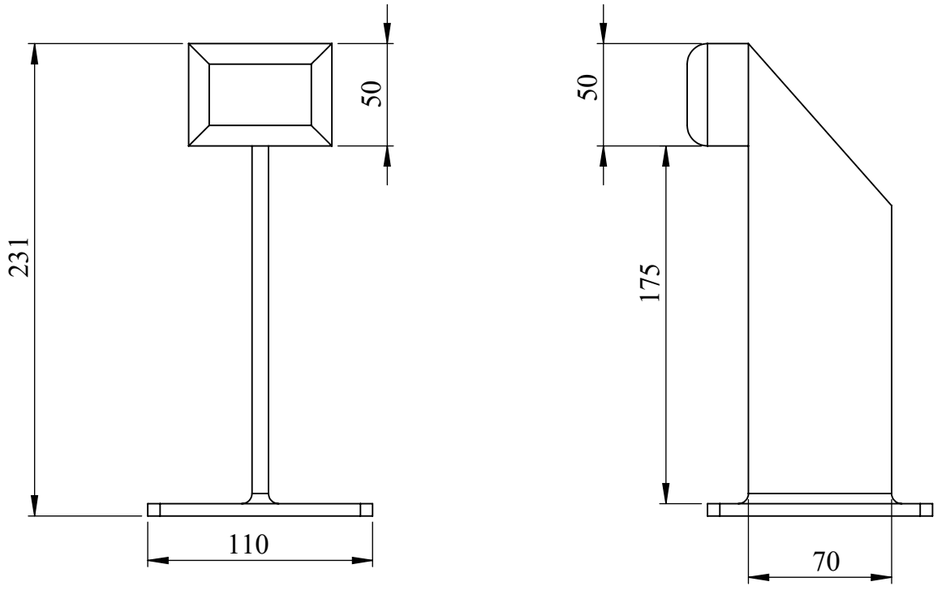

**NOTE -**
**NYLON STOPPER**
**QTY- 2 NOS**

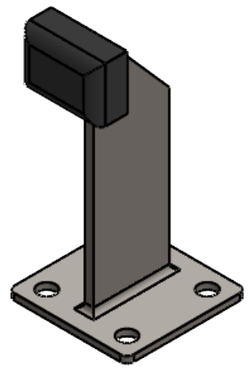


| | | | | |
|---|---|---|---|---|
| TITLE -GATE AUTOMATION | | | | NIHVA TECHNOLOGIES PVT.LTD.PUNE |
| DWG NO - NTPL-290-PM-004-08 | | | | Website - www.nihva.com |
| | NAME | SIGNATURE | DATE | PROJECT NO - NTPL-290-PM |
| DRAWN | V.B. | | 16-08-2025 | PRODUCT -SLIDING GATE |
| CHK'D | B.S. | | 16-08-2025 | SITE LOCATION - AMRAVATI |
| APPV'D | V.T. | | 16-08-2025 | TYPE 4 |
| if any queries contact - design@nihva.com | | | | REVISION -00 / QTY - 1 |
| ALL DIMENSION ARE IN mm | | A3 | | SCALE - / SHEET 15 OF 21 |

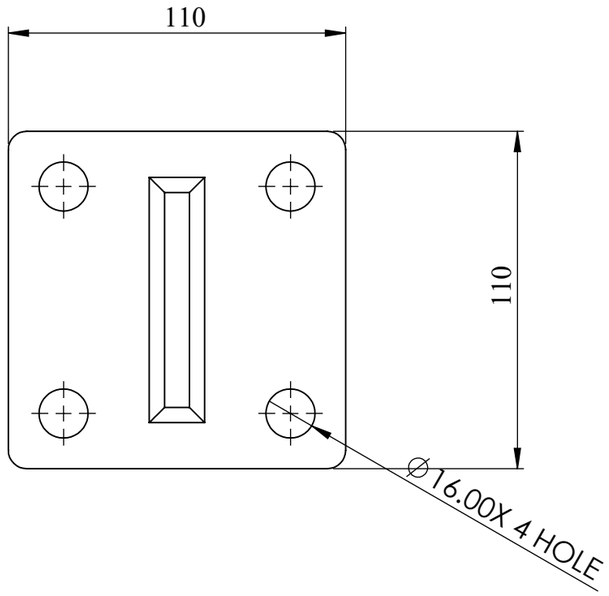


| ITEM NO. | PART NUMBER | DESCRIPTION | QTY. |
|---|---|---|---|
| 2 | NYLON STOPPER PLATE | 135X135X10 | 2 |

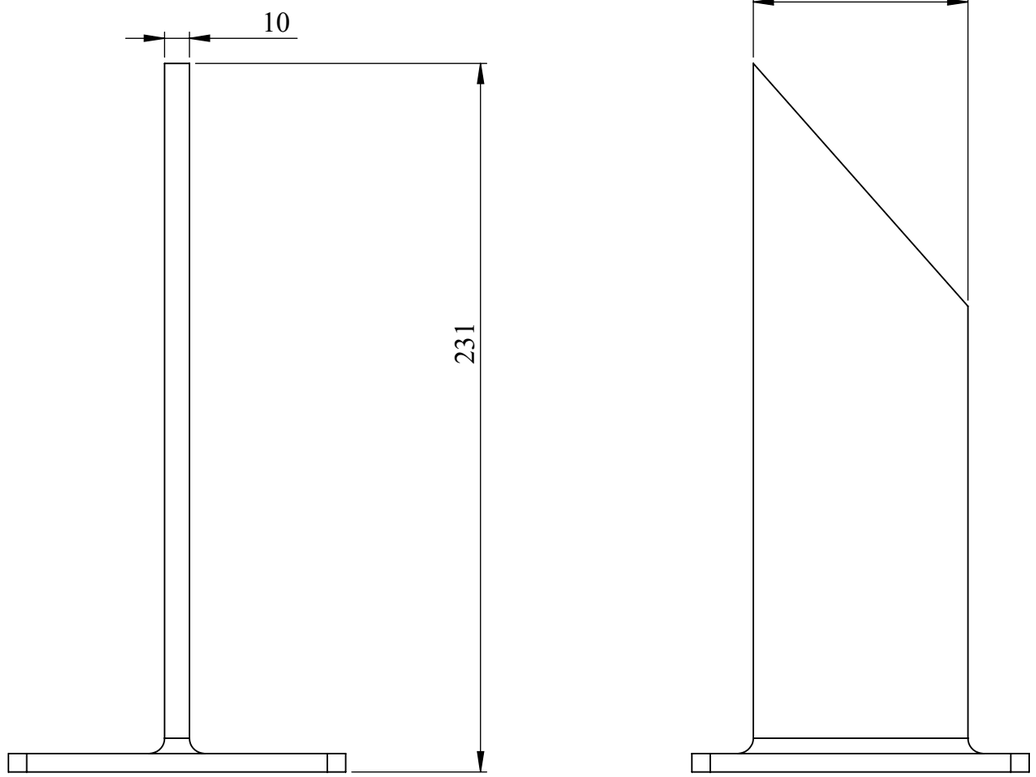




**NOTE -**
**NYLON STOPPER**
**QTY- 2 NOS**

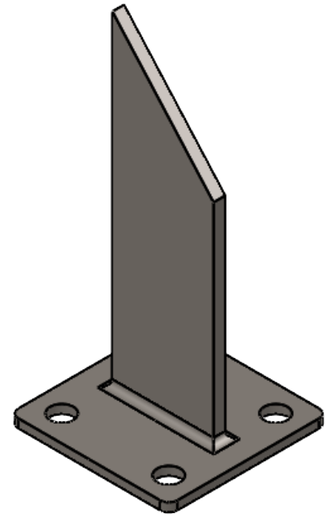


| | | | | |
|---|---|---|---|---|
| TITLE -GATE AUTOMATION | | | | NIHVA TECHNOLOGIES PVT.LTD.PUNE Website - www.nihva.com |
| DWG NO - NTPL-290-PM-004-08-01 | | | | |
| | NAME | SIGNATURE | DATE | PROJECT NO - NTPL-290-PM |
| DRAWN | V.B. | | 16-08-2025 | PRODUCT -SLIDING GATE |
| CHK'D | B.S. | | 16-08-2025 | SITE LOCATION - AMRAVATI |
| APPV'D | V.T. | | 16-08-2025 | TYPE 4 |
| if any queries contact - design@nihva.com | | | | REVISION -00 / QTY - 1 |
| ALL DIMENSION ARE IN mm | | A3 | | SCALE - / SHEET 16 OF 21 |

| ITEM NO. | PART NUMBER | DESCRIPTION | QTY. |
|---|---|---|---|
| 1 | NYLON STOPPER | | 2 |

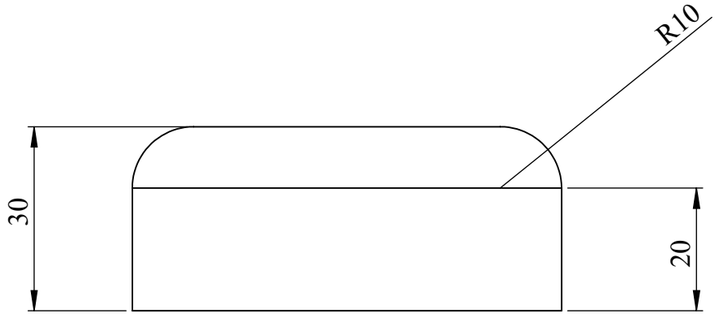

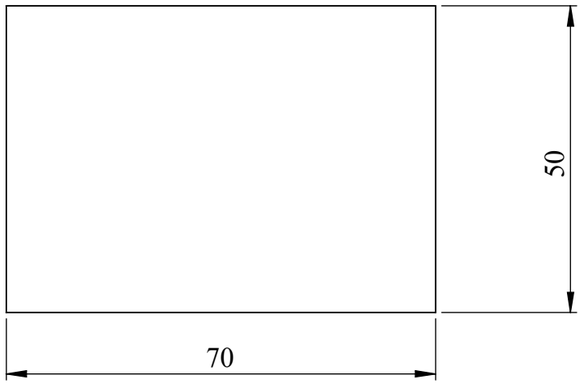


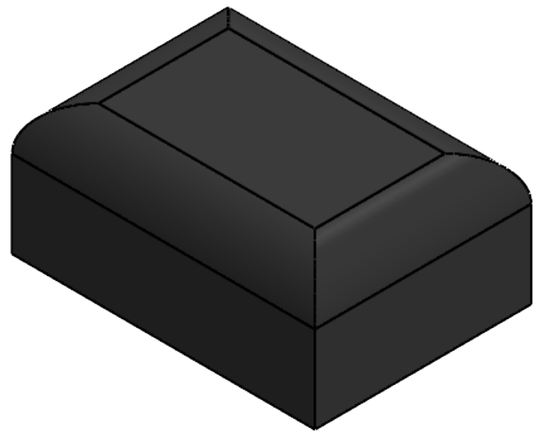
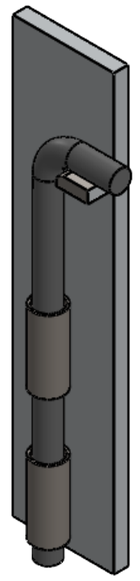



**NOTE -**
**NYLON STOPPER**
**QTY- 2 NOS**

| | | | | |
|---|---|---|---|---|
| TITLE -GATE AUTOMATION | | | | NIHVA TECHNOLOGIES PVT.LTD.PUNE |
| DWG NO - NTPL-290-PM-004-08-02 | | | | Website - www.nihva.com |
| | NAME | SIGNATURE | DATE | PROJECT NO - NTPL-290-PM |
| DRAWN | V.B. | | 16-08-2025 | PRODUCT -SLIDING GATE |
| CHK'D | B.S. | | 16-08-2025 | SITE LOCATION - AMRAVATI |
| APPV'D | V.T. | | 16-08-2025 | TYPE 4 |
| if any queries contact - design@nihva.com | | | | REVISION -00 / QTY - 1 |
| ALL DIMENSION ARE IN mm | | A3 | | SCALE - / SHEET 17 OF 21 |

| ITEM NO. | PART NUMBER | DESCRIPTION | QTY. |
|---|---|---|---|
| 1 | TOWER BOLT HOLLOW PIPE | DIA- 18MM (3 MM THK) | 3 |
| 2 | Tower Bolt | DIA- 15MM 300(L) | 3 |

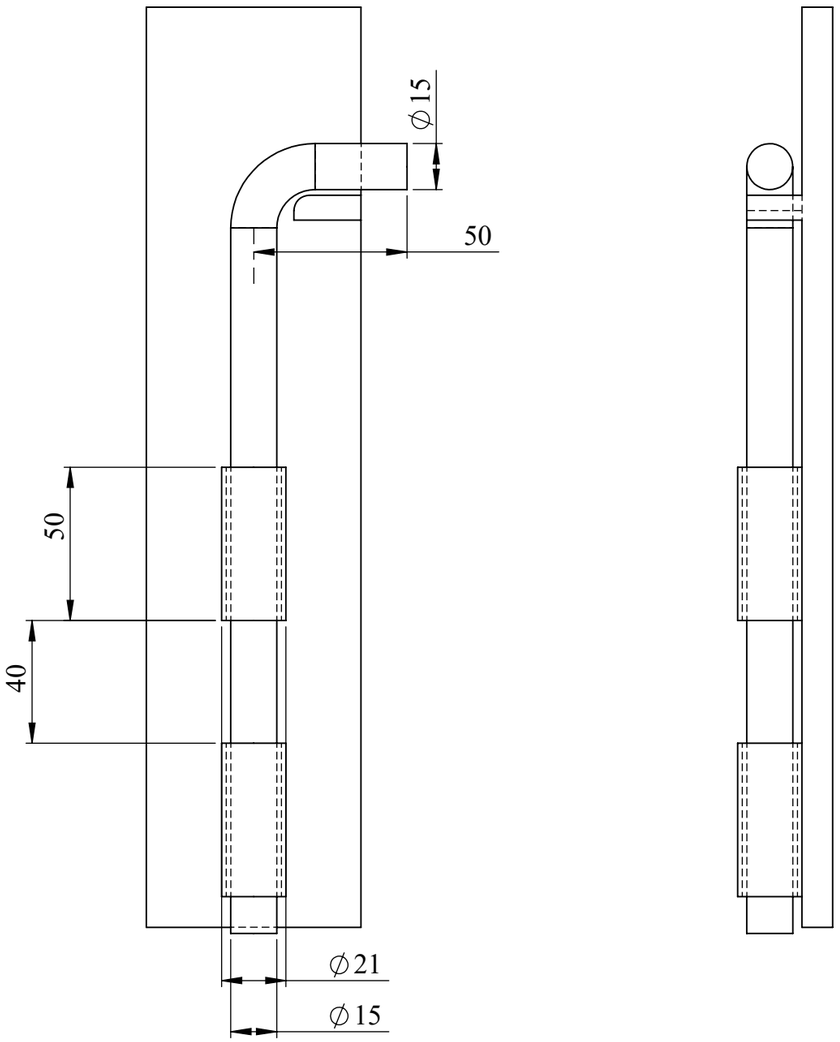






**NOTE -**
**TOWER BOLT**
**QTY- 3 NOS**

| | | | | |
|---|---|---|---|---|
| TITLE -GATE AUTOMATION | | | | NIHVA TECHNOLOGIES PVT.LTD.PUNE |
| DWG NO - NTPL-290-PM-004-09 | | | | Website - www.nihva.com |
| | NAME | SIGNATURE | DATE | PROJECT NO - NTPL-290-PM |
| DRAWN | V.B. | | 16-08-2025 | PRODUCT -SLIDING GATE |
| CHK'D | B.S. | | 16-08-2025 | SITE LOCATION - AMRAVATI |
| APPV'D | V.T. | | 16-08-2025 | TYPE 4 |
| if any queries contact - design@nihva.com | | | | REVISION -00 / QTY - 1 |
| ALL DIMENSION ARE IN mm | | A3 | | SCALE - / SHEET 18 OF 21 |

| ITEM NO. | PART NUMBER | DESCRIPTION | QTY. |
|---|---|---|---|
| 1 | WICKET GATE | 1200X1675 | 1 |
| 2 | BOTTOM SIDE HINGS PLATE | 80X75X6 | 2 |
| 3 | MALE - FEMALE Hings | 3 INCH | 2 |
| 4 | hing bearing | | 2 |
| 5 | UPPER SUPPORT HINGS PLATE | 100X197X10 | 2 |
| 7 | female hings | 3 INCH | 2 |

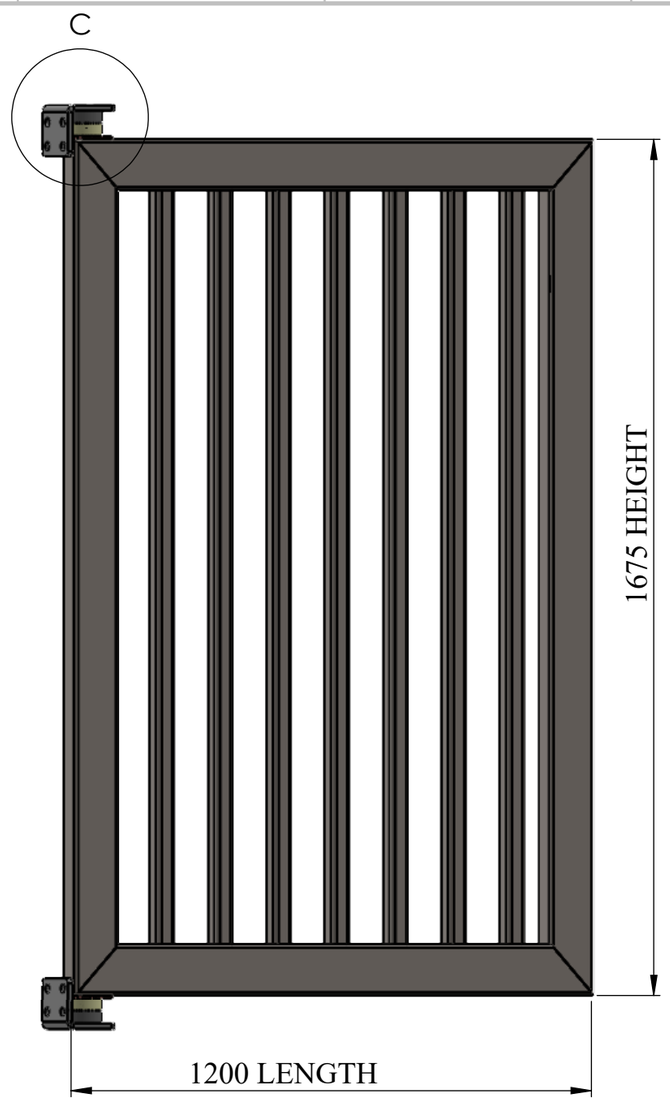

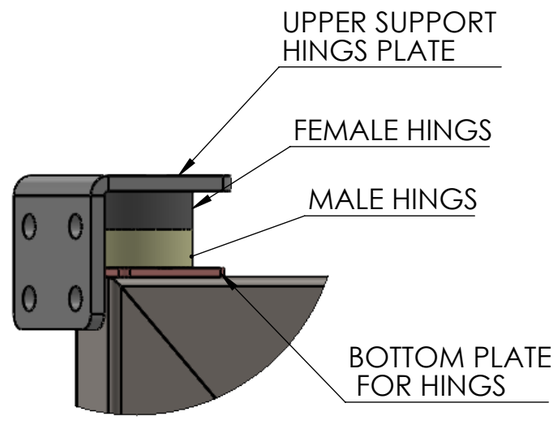
DETAIL C
SCALE 1 : 4







**QTY- 1NOS**

| | | | | |
|---|---|---|---|---|
| TITLE - RETRACTABLE ROOF | | | | NIHVA TECHNOLOGIES PVT.LTD.PUNE |
| DWG NO - NTPL290-PM-004-11 | | | QTY - 1 | Website - www.nihva.com |
| | NAME | SIGNATURE | DATE | PROJECT NO - NTPL290-PM |
| DRAWN | V.B. | | 16-08-2025 | PRODUCT - SLIDING GATE |
| CHK'D | B.S. | | 16-08-2025 | SITE LOCATION - AMRAVATI |
| APPV'D | V.T. | | 16-08-2025 | TYPE 4 |
| if any queries contact - design@nihva.com | | | | REVISION -00 |
| ALL DIMENSION ARE IN mm | | | A3 | SCALE - |
| | | | | SHEET 19 OF 21 |

| ITEM NO. | PART NUMBER | DESCRIPTION | QTY. |
|---|---|---|---|
| 1 | Bottom Hinges Plate | 80x75x6 mm THK | 2 |

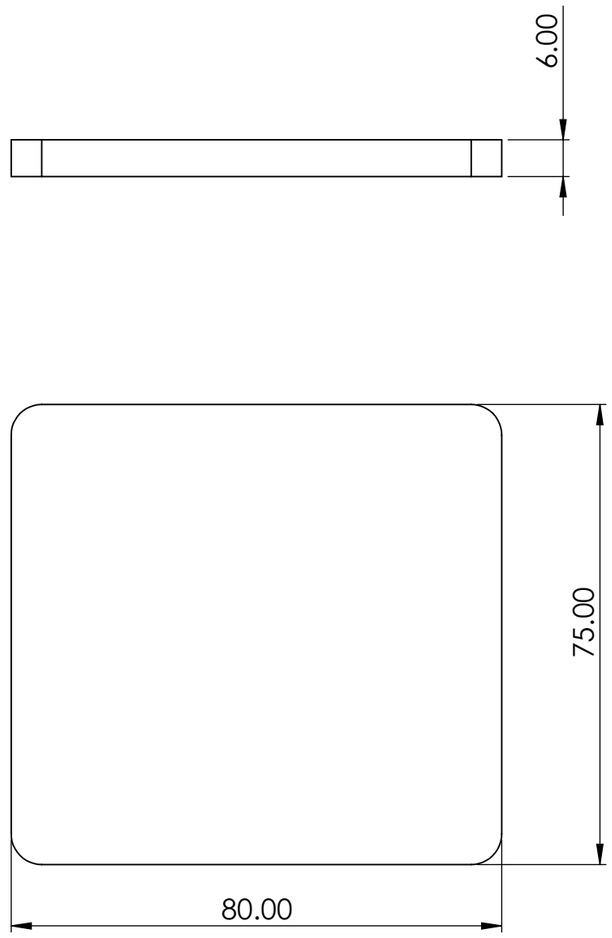


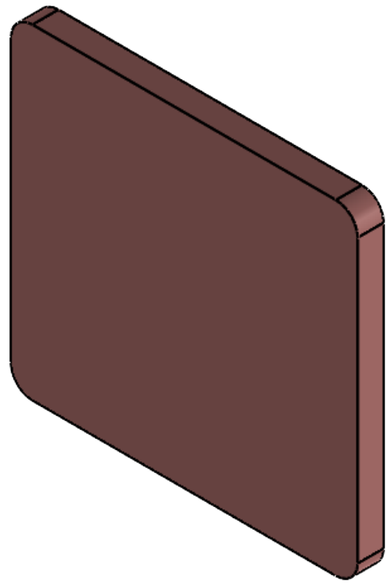



**BOTTOM PLATE FOR HINGES**
**SIZE:- 80X75X6MM THK**
**MATERIAL:- MS**
**QTY:- 2 NOS**

| | | | | |
|---|---|---|---|---|
| TITLE -GATE AUTOMATION | | | | NIHVA TECHNOLOGIES PVT.LTD.PUNE |
| DWG NO - NTPL-290-PM-004-11-01 | | | | Website - www.nihva.com |
| | NAME | SIGNATURE | DATE | PROJECT NO - NTPL-290-PM |
| DRAWN | V.B. | | 16-08-2025 | PRODUCT -SLIDING GATE |
| CHK'D | B.S. | | 16-08-2025 | SITE LOCATION - AMRAVATI |
| APPV'D | V.T. | | 16-08-2025 | TYPE 4 |
| if any queries contact - design@nihva.com | | | | REVISION -00 / QTY - 1 |
| ALL DIMENSION ARE IN mm | | A3 | | SCALE - / SHEET 20 OF 21 |

| ITEM NO. | PART NUMBER | DESCRIPTION | QTY. |
|---|---|---|---|
| 1 | UPPER SUPPORT PLATE | 100X197X10 THK | 2 |

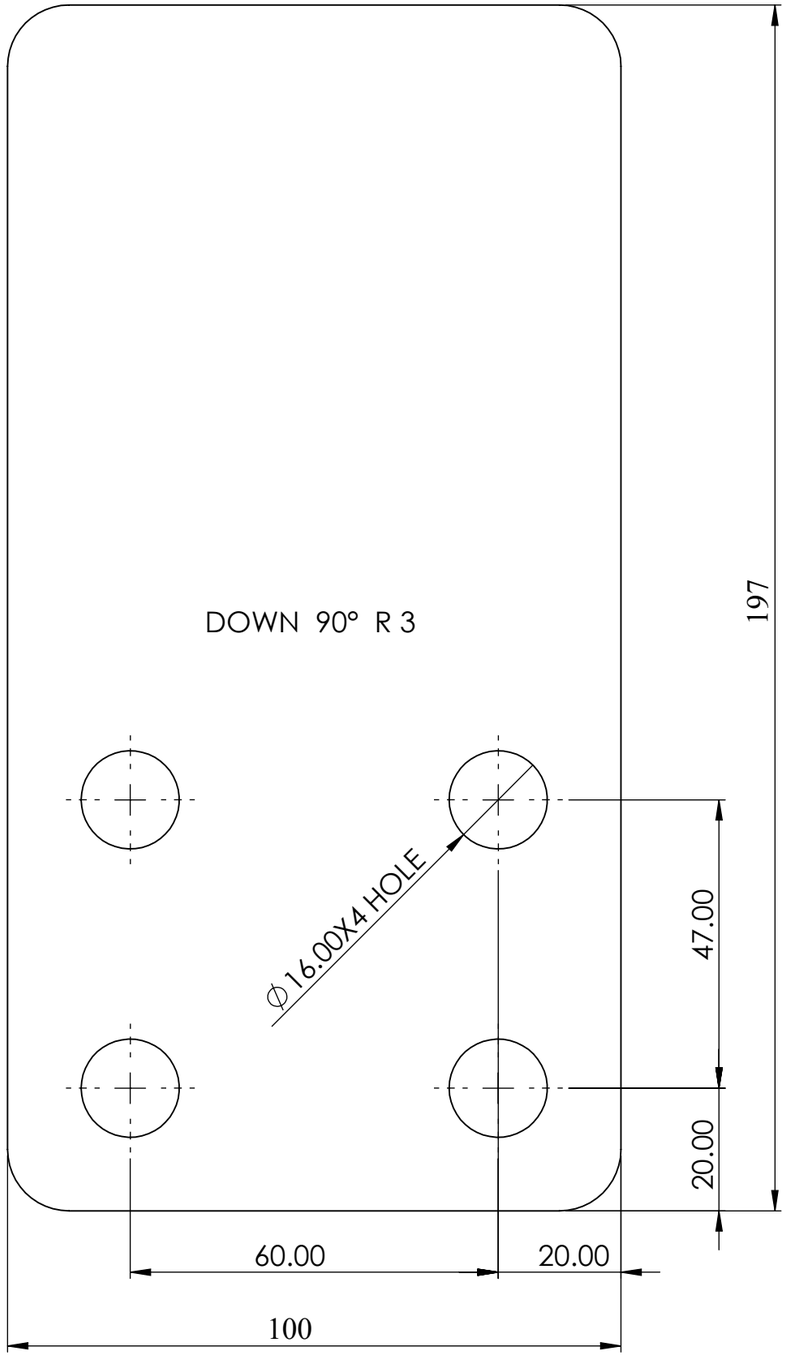

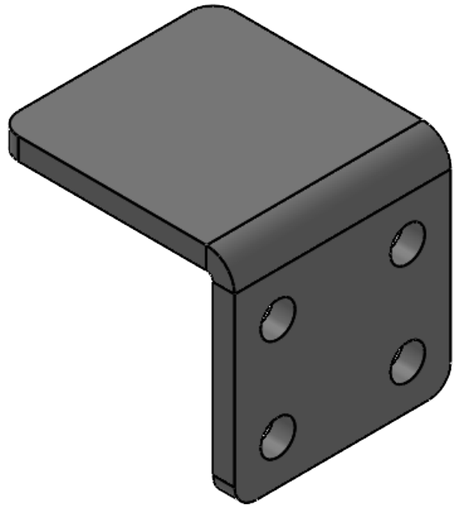**UPPER SUPPORT PLATE FOR HINGES**
**SIZE:- 100X197X10THK**
**MATERIAL:- MS**
**QTY:- 2 NOS**

| | | | | |
|---|---|---|---|---|
| TITLE -GATE AUTOMATION | | | | NIHVA TECHNOLOGIES PVT.LTD.PUNE |
| DWG NO - NTPL-290-PM-004-11-02 | | | | Website - www.nihva.com |
| | NAME | SIGNATURE | DATE | PROJECT NO - NTPL-290-PM |
| DRAWN | V.B. | | 16-08-2025 | PRODUCT -SLIDING GATE |
| CHK'D | B.S. | | 16-08-2025 | SITE LOCATION - AMRAVATI |
| APPV'D | V.T. | | 16-08-2025 | TYPE 4 |
| if any queries contact - design@nihva.com | | | | REVISION -00 / QTY - 1 |
| ALL DIMENSION ARE IN mm | | A3 | | SCALE - / SHEET 21 OF 21 |