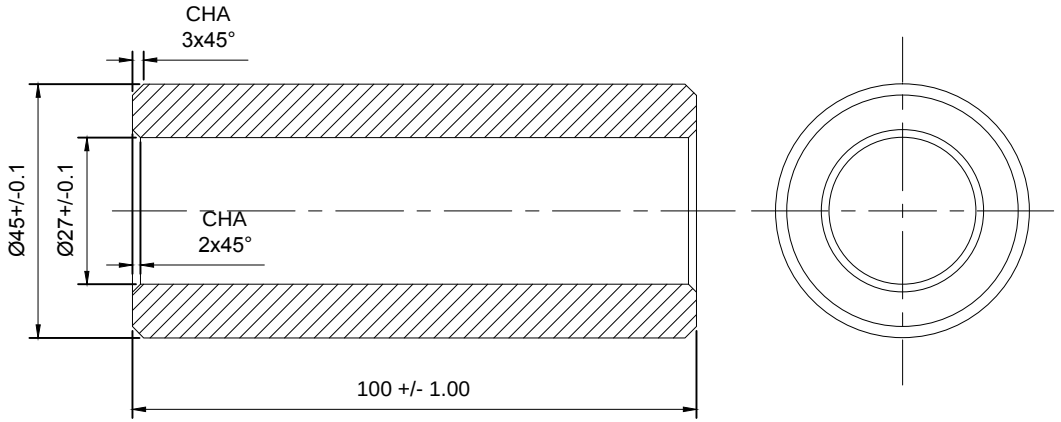


NOTE:~ MTL : MS

BUSH Ø45 X 103L = 22 NOS

NOTE : ~ PLEASE MAINTAIN 7 MM GAP BETWEEN TWO LIP BUSHES.

This drawing & design is the property of NIHVA TECHNOLOGIES. Not to be sold or copied to any other concern.

TITLE: LIP MOUNTING BUSH			NIHVA TECHNOLOGIES PVT. LTD. PUNE Tel : 020 66304033 Email:- info@nihva.com Website:- www.nihva.com
	NAME	SIGN	DATE
DRAWN	P.V.A		20.06.2019
CHECK	V.M.T		20.06.2019
APPRD.			
CLIENT -			
PROJECT - NDL451			
SITE LOCATION -			
If any queries contact : design@nihva.com			DWG. NO. : NIHVA/19-20/VDR/070
ALL DIMENSION ARE IN mm			SCALE: NTS / WT: / REV- 0