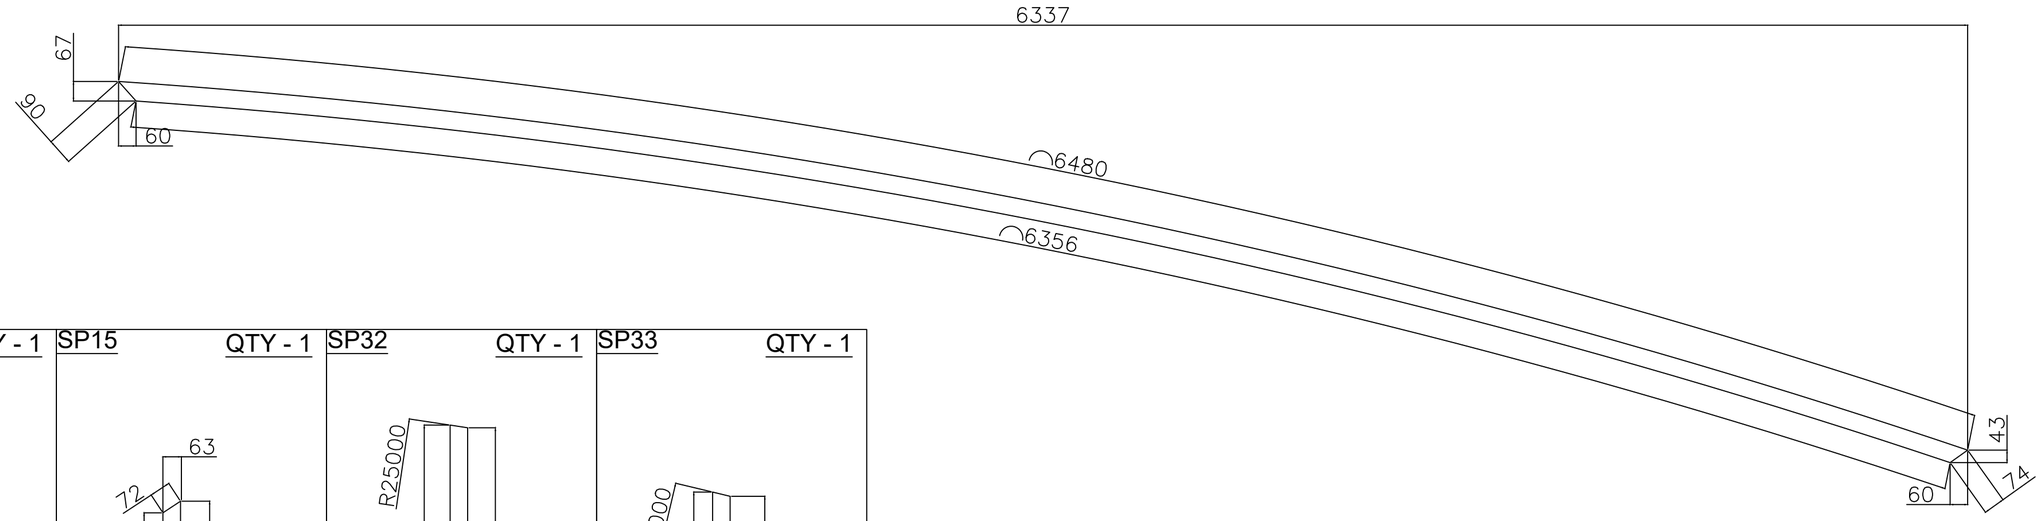
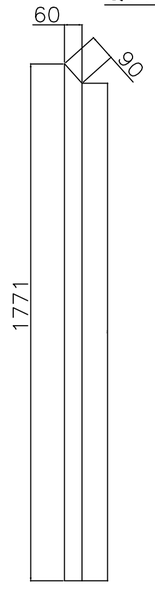
C6
QTY - 1

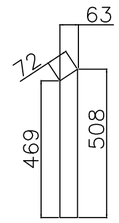
LARGE END FACE





SP14 QTY - 1





SP15 QTY - 1





SP32 QTY - 1

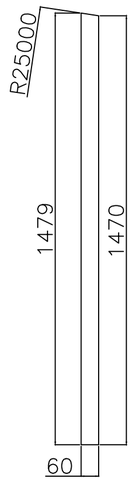


SP33 QTY - 1

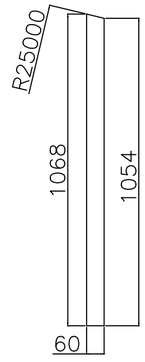


SP16 QTY - 1

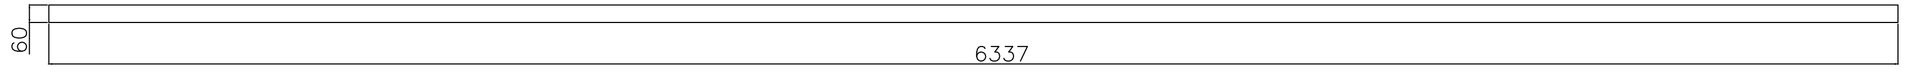


| REV NO. | DESCRIPTION | Date | Revised By |
|---|---|---|---|
| | | | |

TITLE:- LARGE END FACE

| | NAME | DATE | SIGN |
|---|---|---|---|
| DRAWN | MAHESH S. | 22/10/22 | |
| CHECK | MAHESH S. | 22/10/22 | |
| APPRD. | VIJAY T. | 22/10/22 | |

If any queries contact : design@nihva.com

ALL DIMENSION ARE IN mm

NIHVA TECHNOLOGIES PVT. LTD.

NIHVA TECHNOLOGIES PVT. LTD. PUNE
Tel : 020 66304033
Email:- info@nihva.com
Website:- www.nihva.com

CLIENT - NIHVA TECHNOLOGIES PVT.LTD

LOCATION -

PRODUCT: FIX & RETRACTABLE ROOF

DWG NO:-NIHVA/22-23/MFG/0048 | REV- 0

SCALE: NTS | SCALE:-- 1:1 | SHEET: 01 OF 01