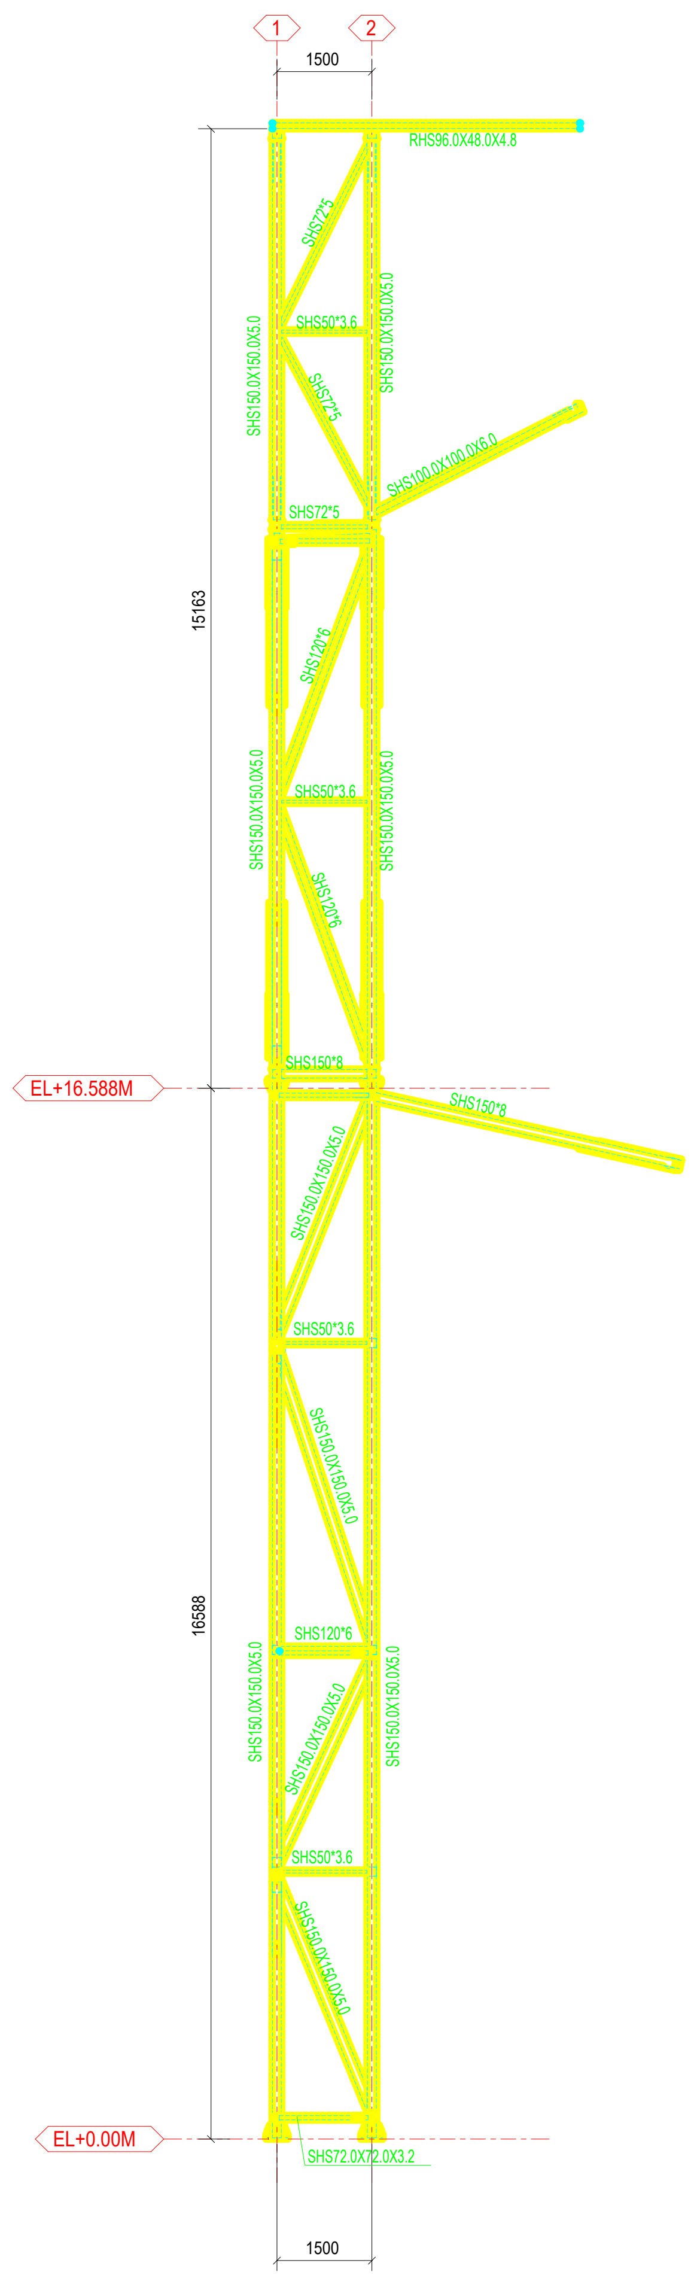

SECTION D - D
1:80

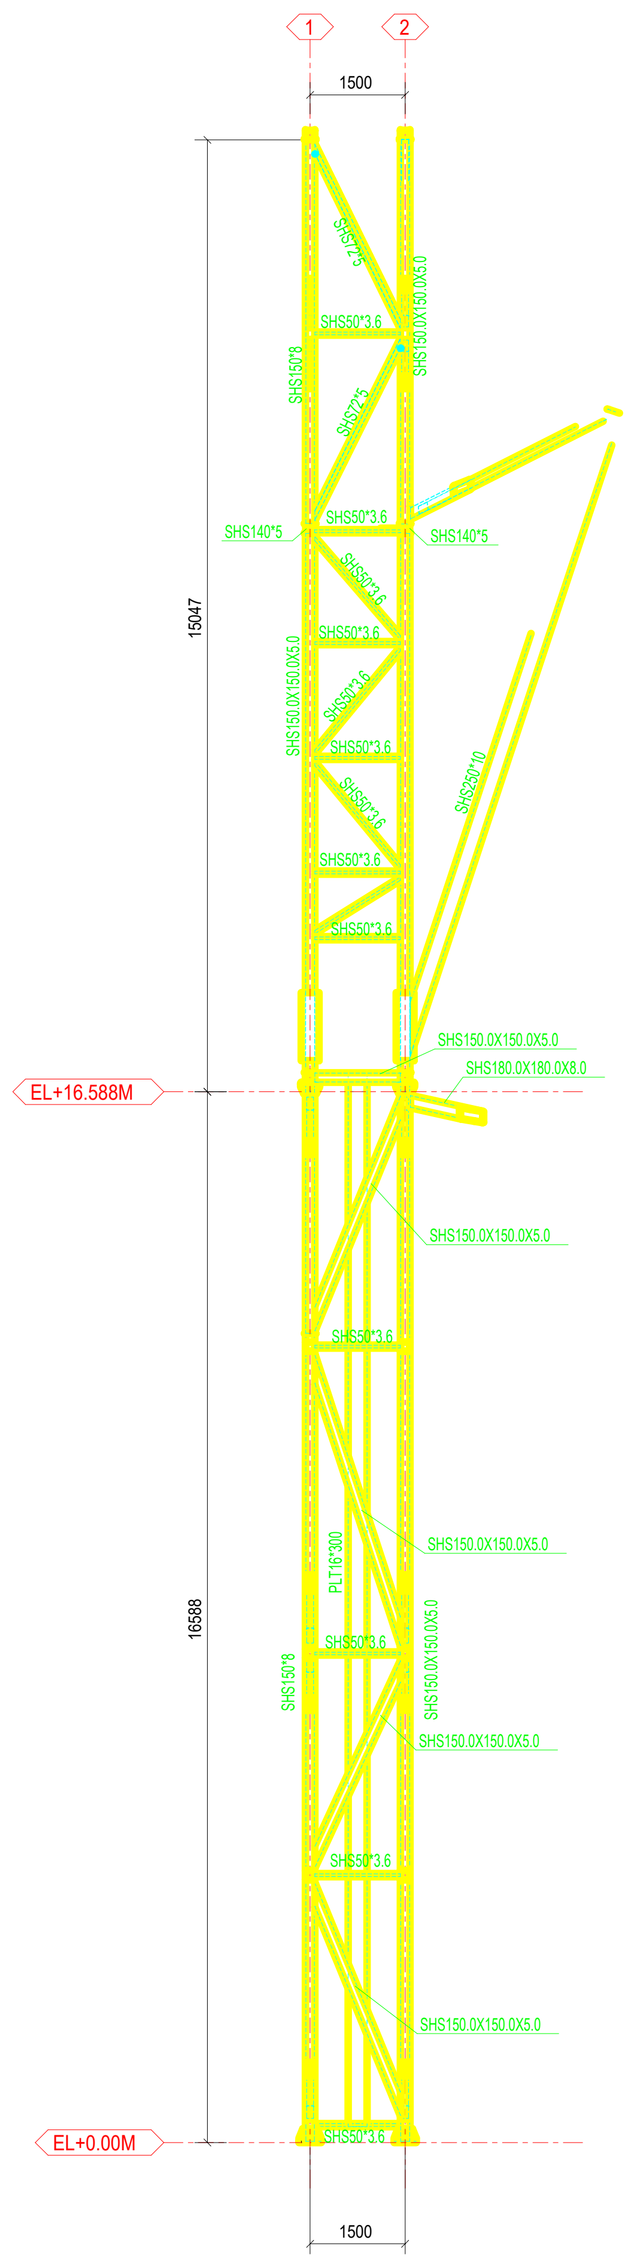

SECTION E - E
1:80

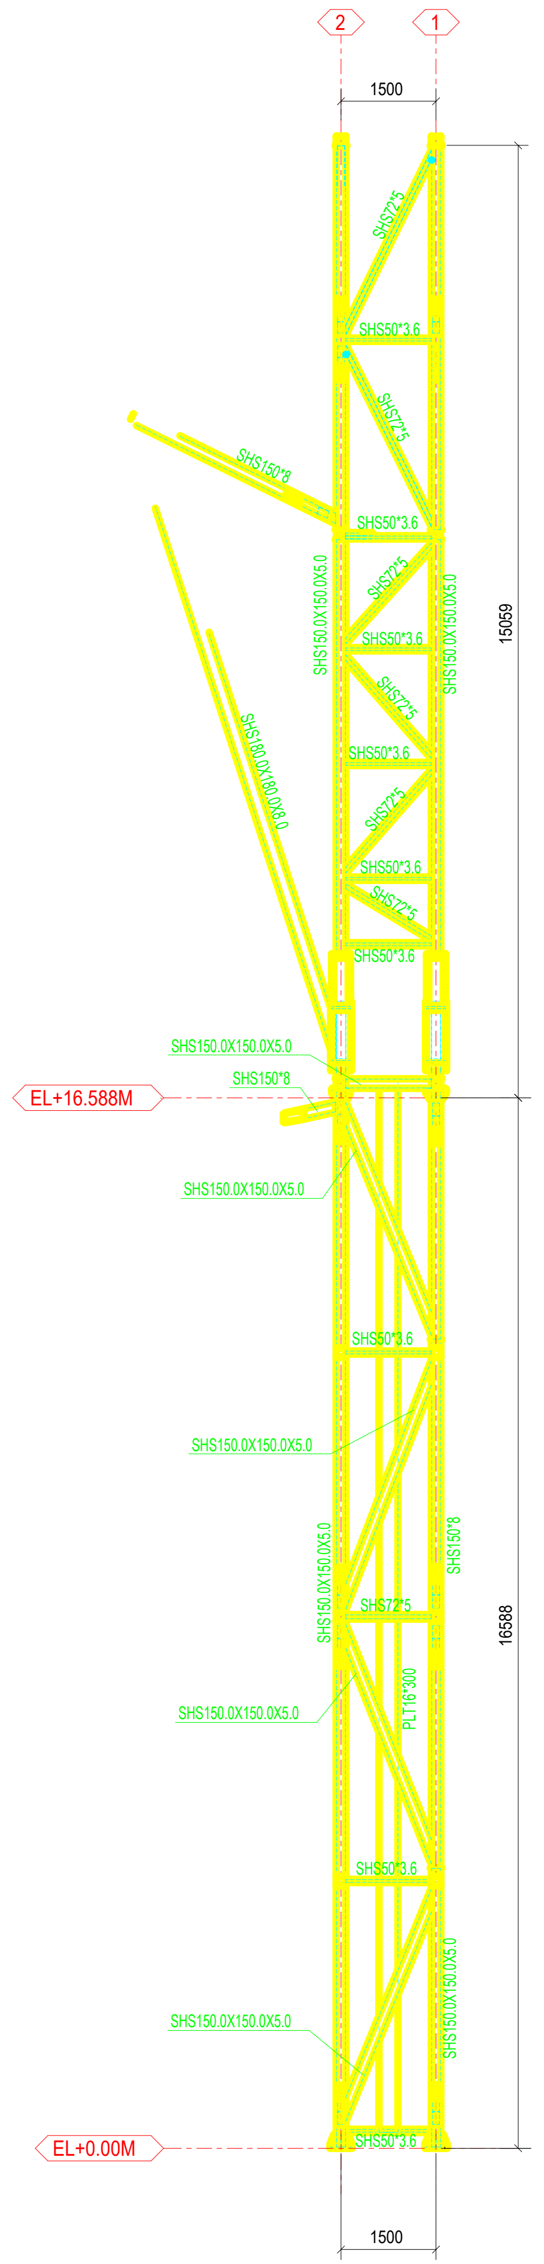

SECTION F - F
1:80

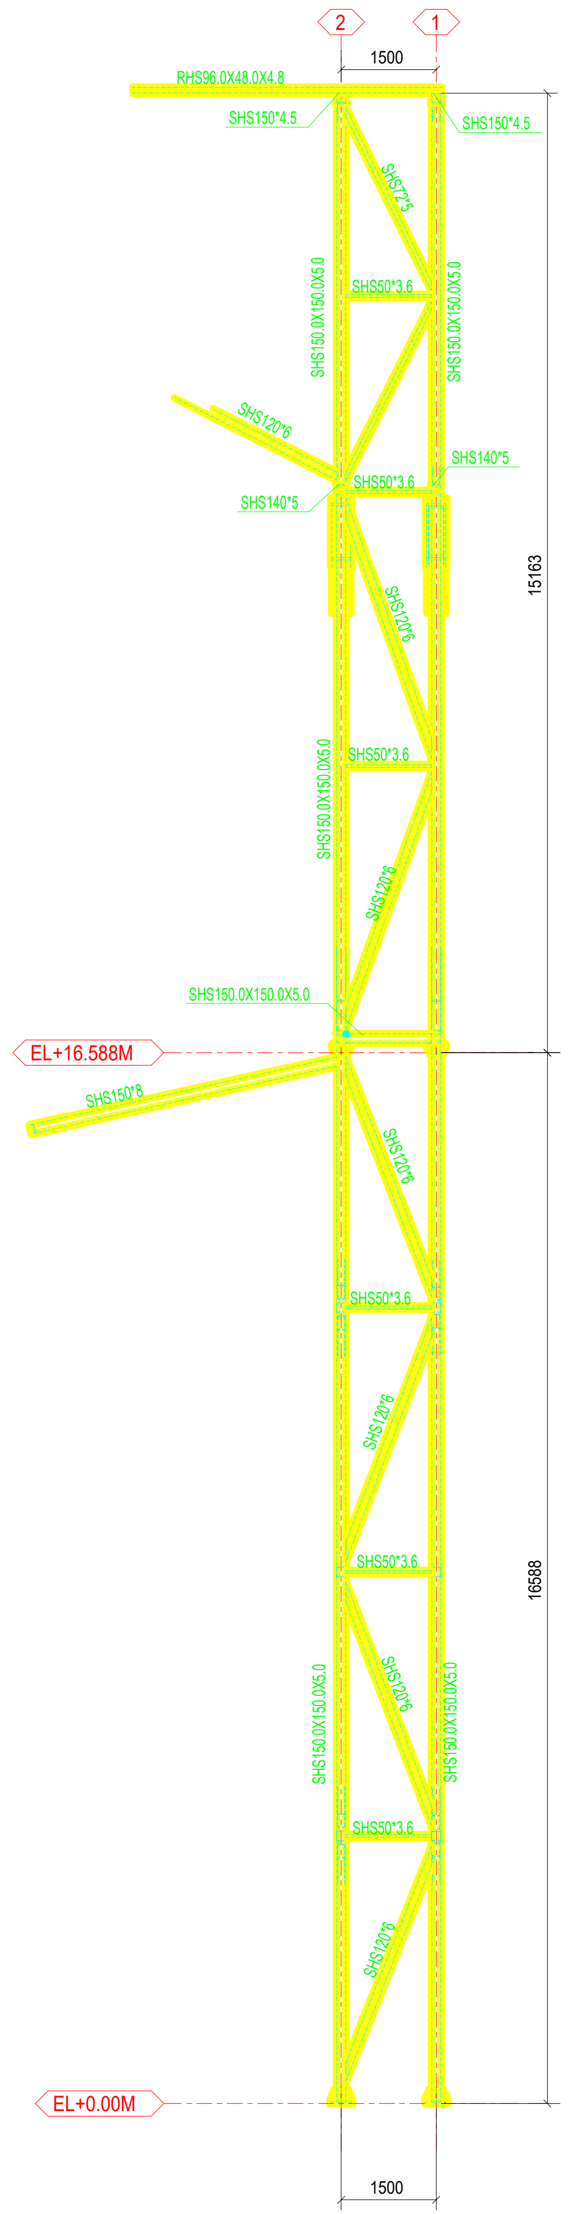

SECTION G - G
1:80

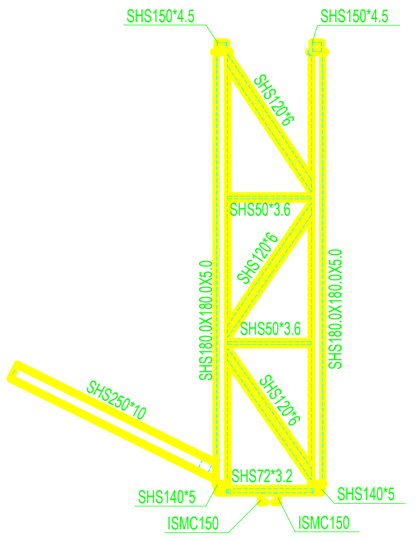

SECTION P - P
1:80

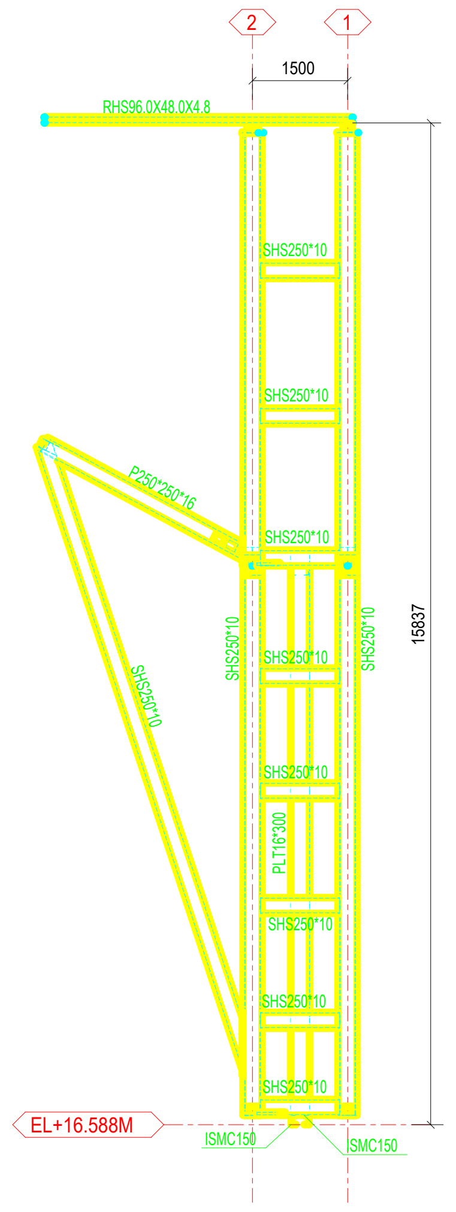

SECTION V - V
1:80

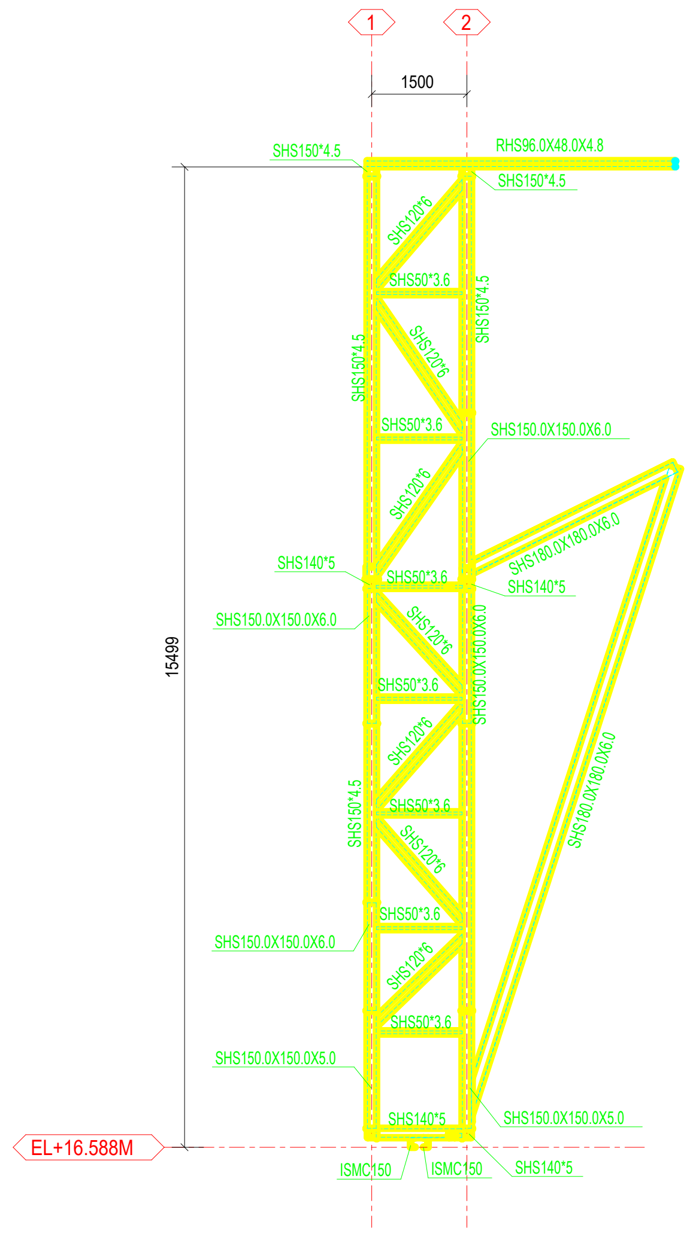

SECTION S - S
1:80

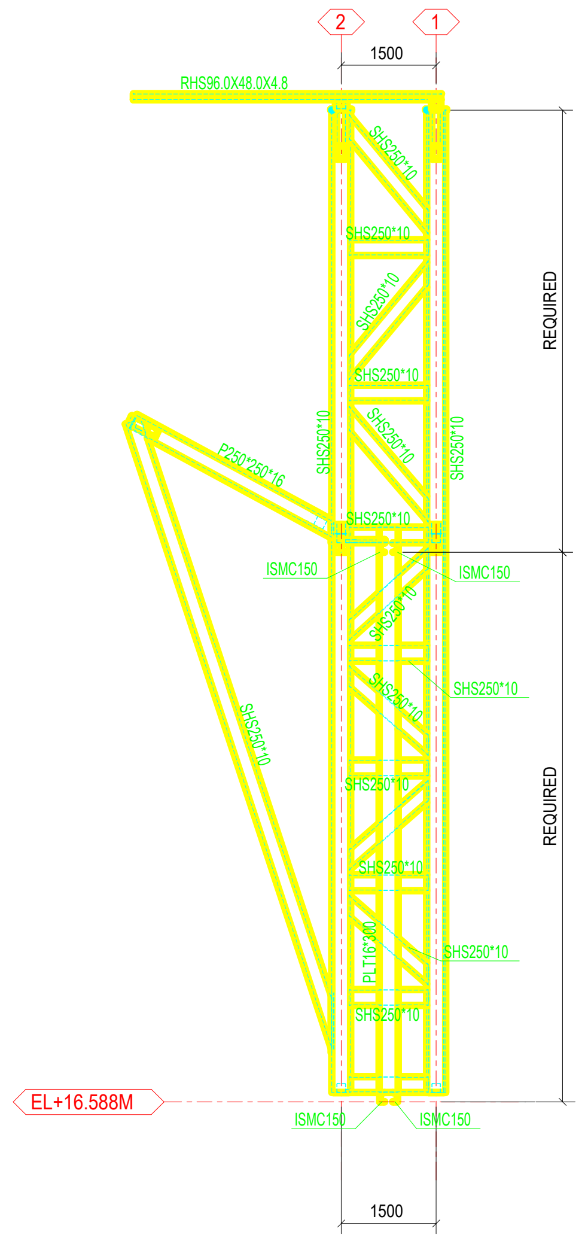

SECTION H - H
1:80

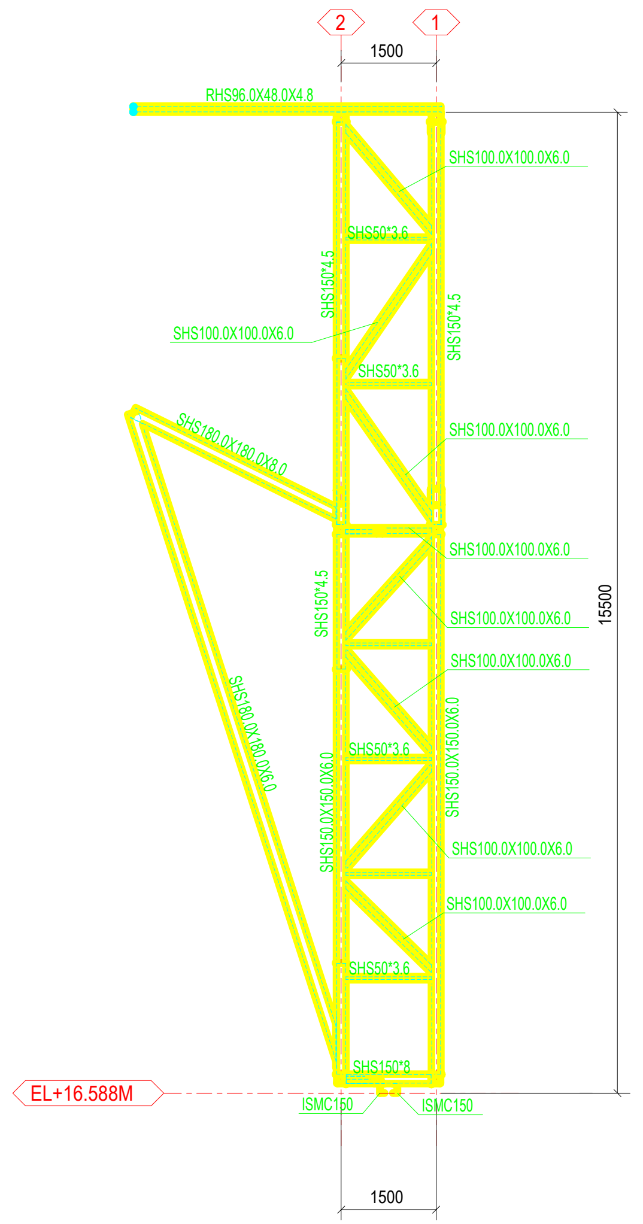

SECTION J - J
1:80

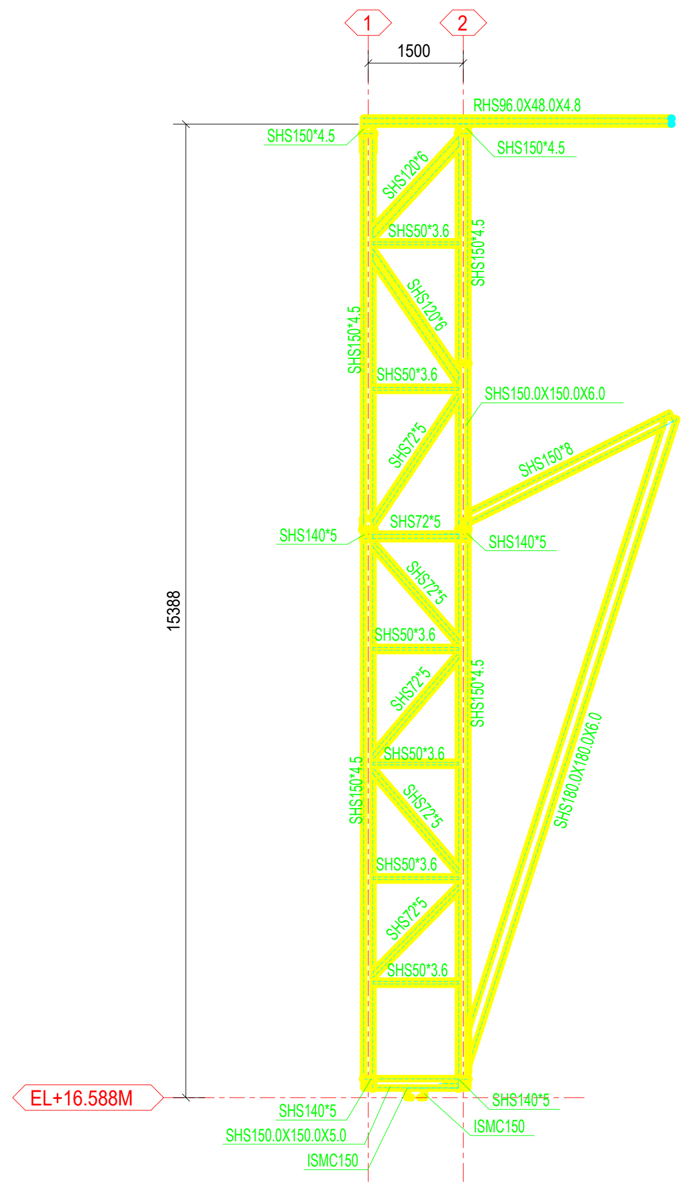

SECTION T - T
1:80

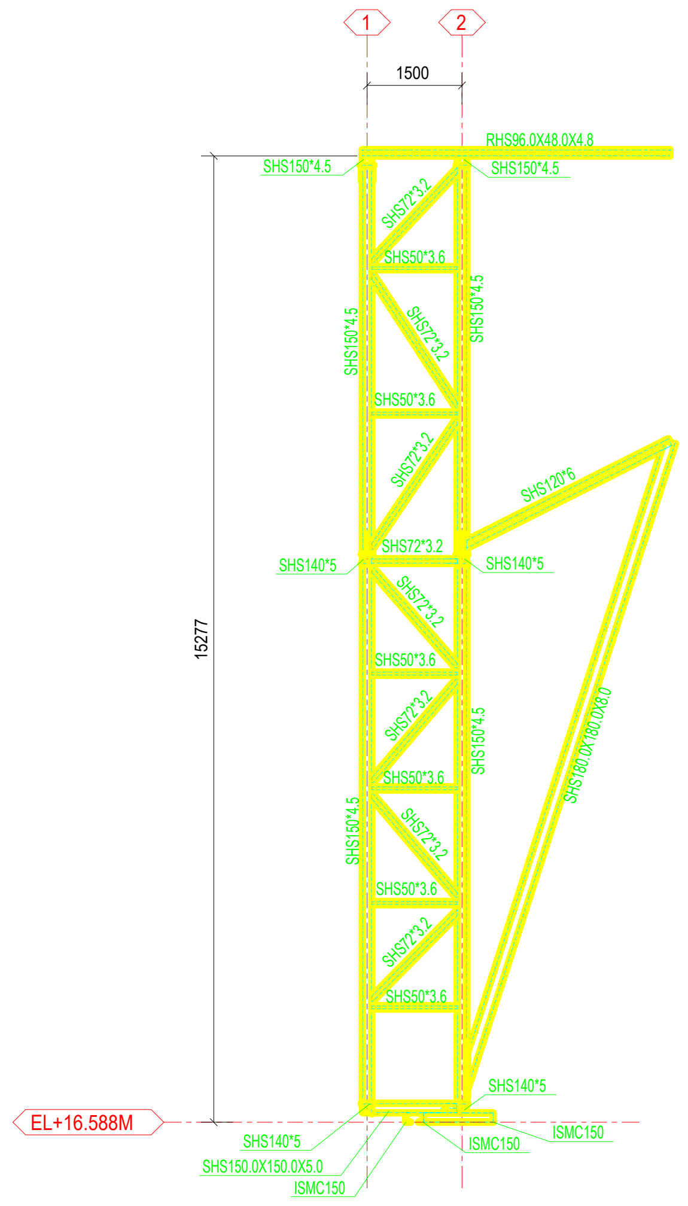

SECTION U - U
1:80

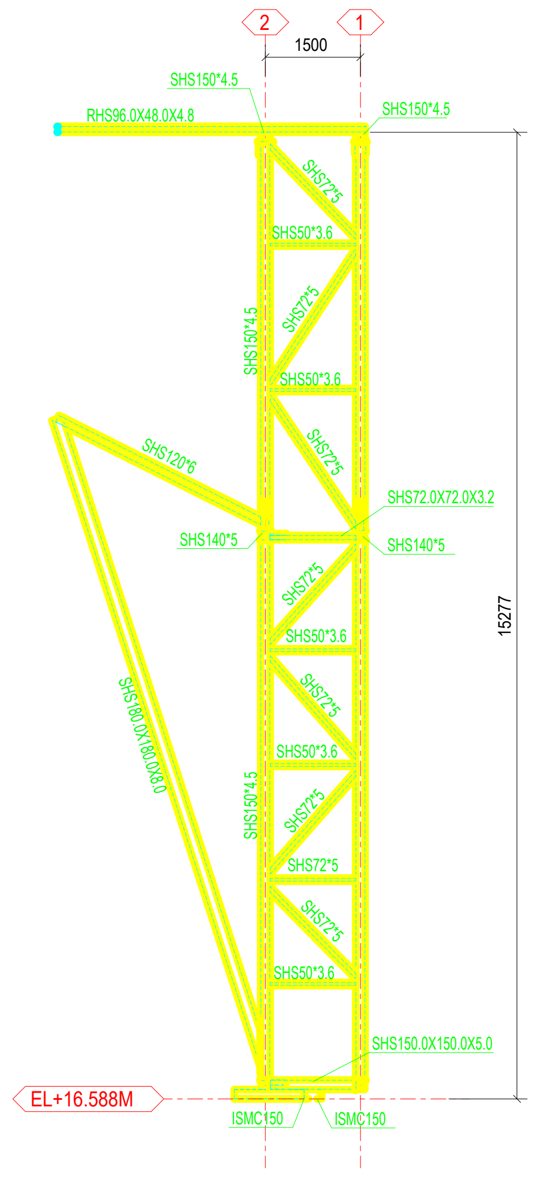

SECTION K - K
1:80

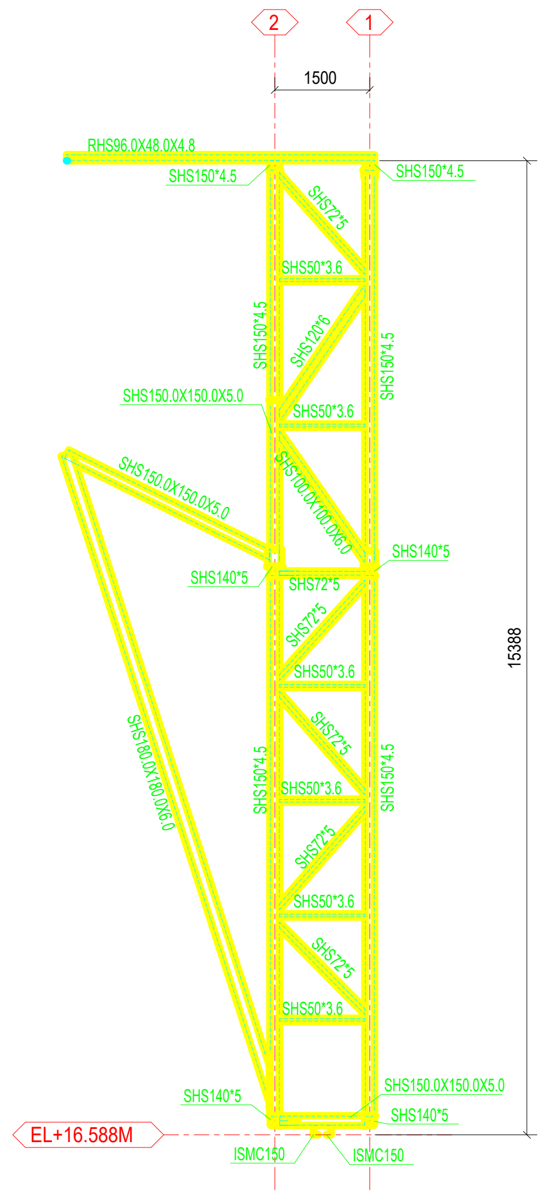

SECTION L - L
1:80

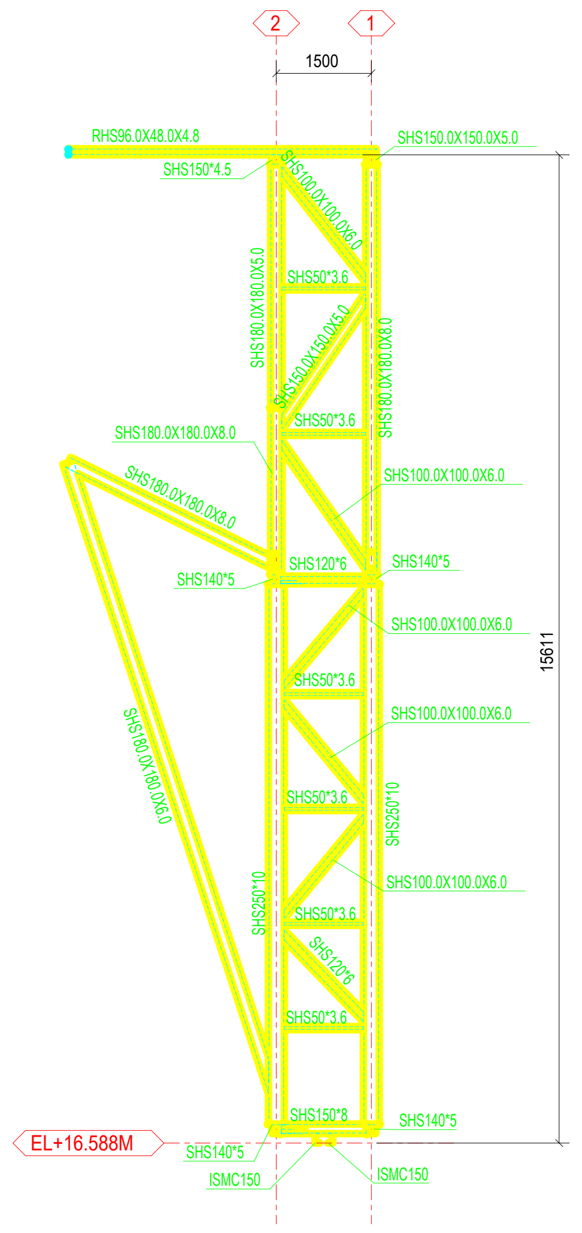

SECTION M - M
1:80

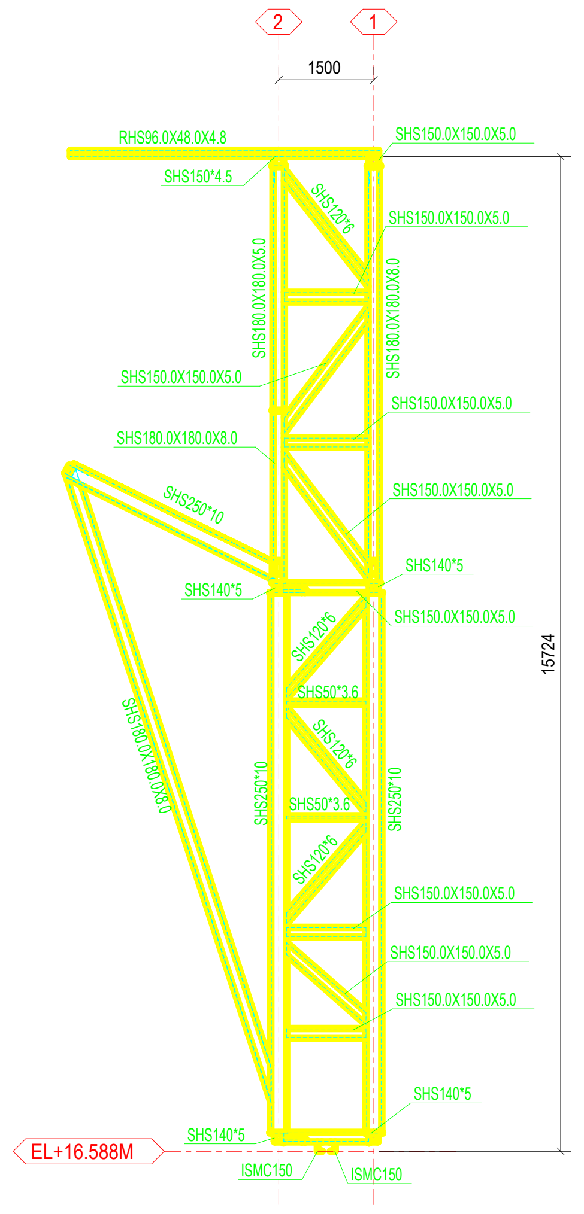

SECTION N - N
1:80

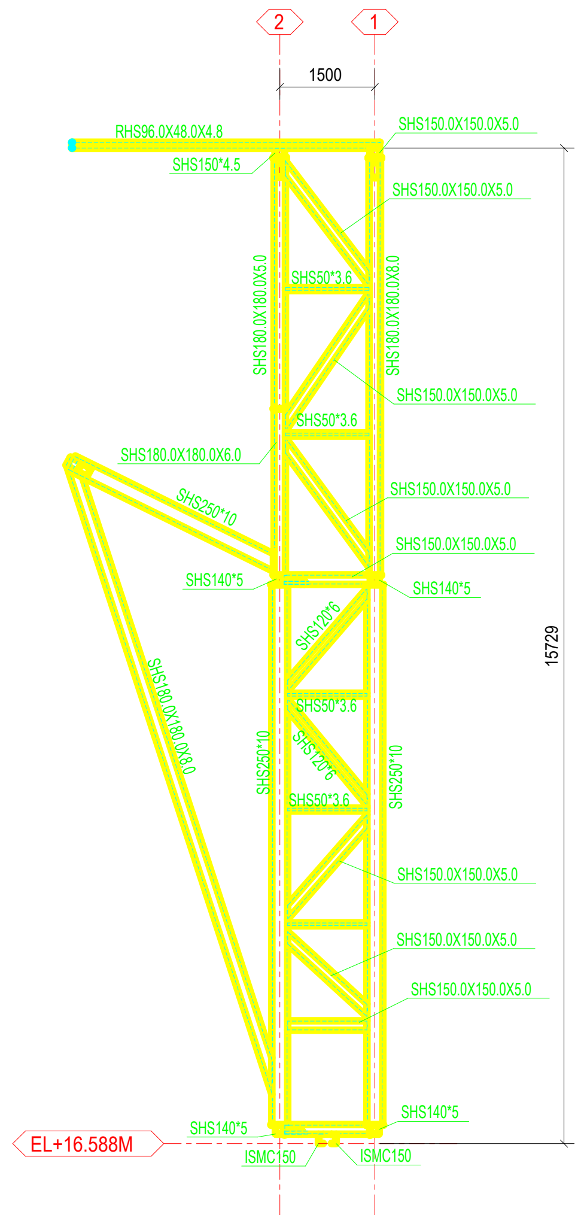

SECTION Q - Q
1:80

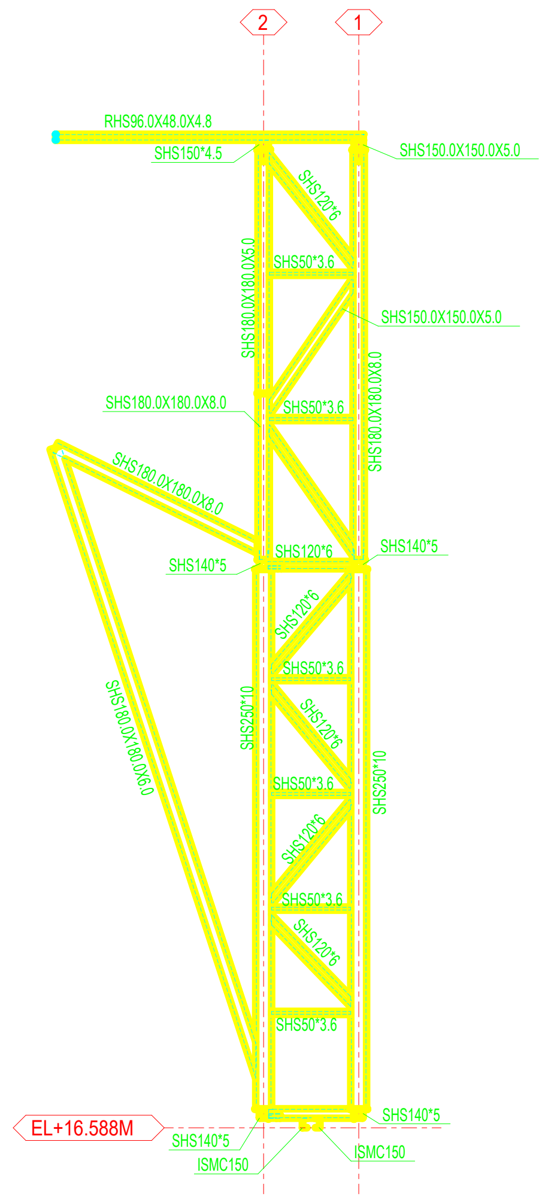

SECTION R - R
1:80

REV.NO.	DESCRIPTION.	REV.DATE	DRAWN.	CHKD.	APPD.
0	GA DRAWING FOR APPROVAL	05.11.22	MEGHA	HAB	HAB

DWG.TITLE :- GA DRAWING FOR DOOR FRAME(84M)

PROJECT
MEGADOOR INSTALLATION AT HYDRABAD AIRPORT

CLIENT
GMR

SALT DESIGN SERVICES

NIHVA TECHNOLOGIES
PVT. LTD. PUNE
Tel : 020 66304033
Email:- info@nihva.com
Website:- www.nihva.com

DRAWN :RRK
CHECKED : HAB
SCALE: 1:100
APPROVED : HAB
JOB CODE. : 1729
DATE: 05.11.2022

DWG.NO: SALT_1729_GA_01_R0
(SH-2OF3)
REV. - R0
SIZE. - A0