
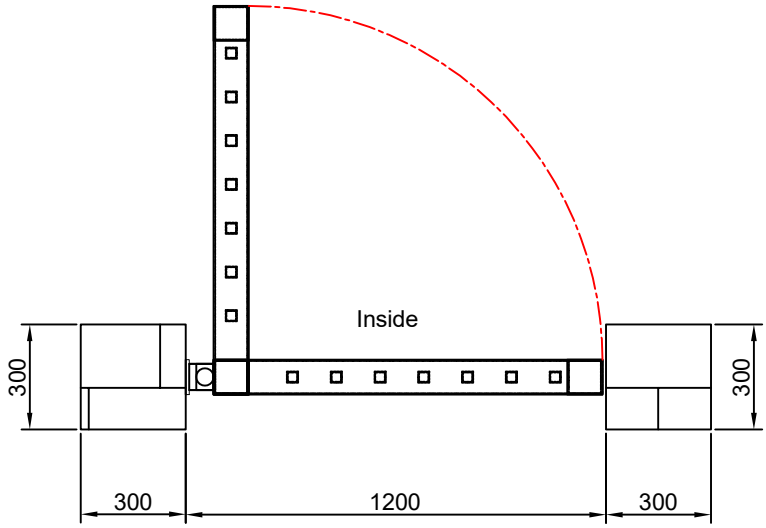


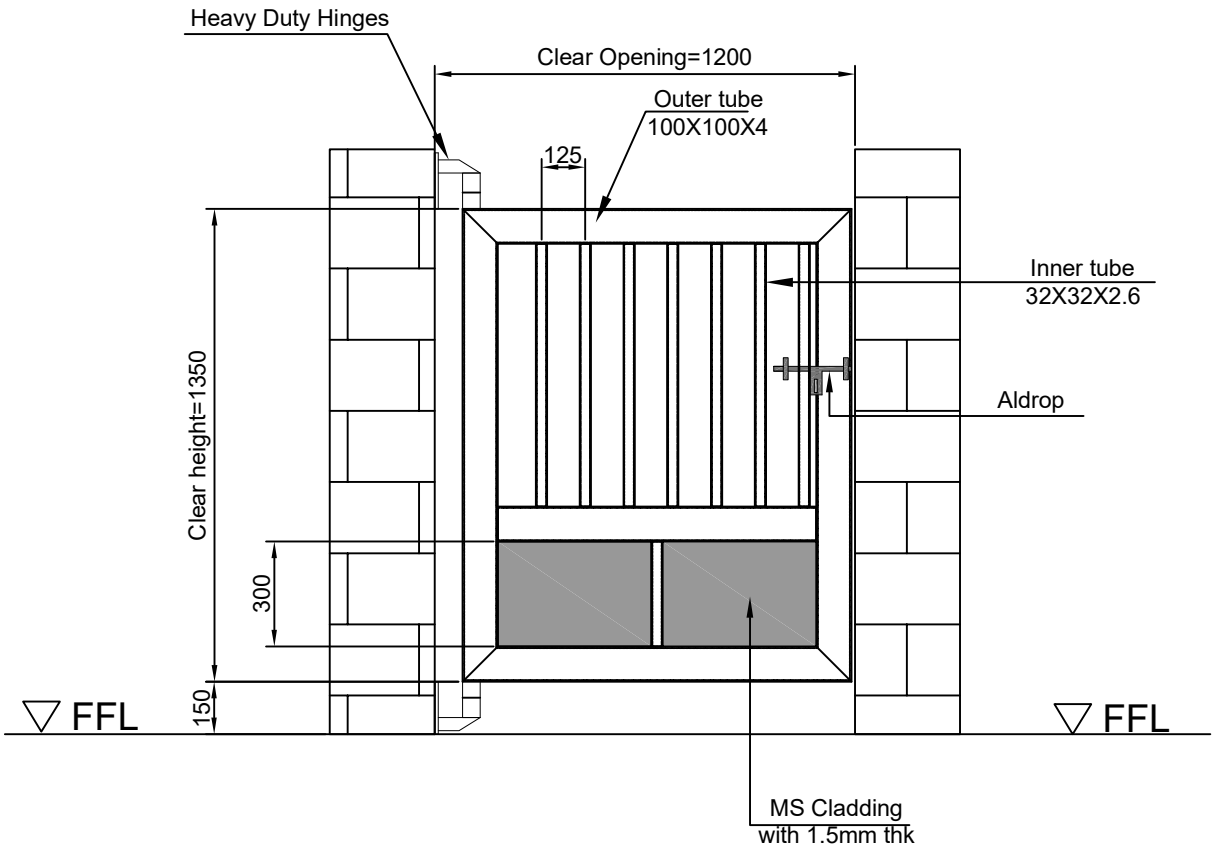

TECHNICAL SPECS FOR SWING GATE		
SL NO.	SPECIFICATION	
1	OPENING LENGTH	1200MM
2	OPENING HEIGHT	1350MM
3	OUTER TUBE	100X100X4
4	INNER TUBE	32X32X2.6
6	OPERATION	MANUAL

Note:-

1.All dimension are in mm.

2.All civil work is in client scope.

Rev No.	Revision	Date	Revised By
1.	Clear Height of the gate changed 1800mm to 1350mm	08/01/2022	Sujata
2.	Gate Orientation has been changed	08/01/2022	Sujata

This drawing & design is the property of NIHVA TECHNOLOGIES. Not to be sold or copied to any other concern.

TITLE:- WICKET GATE

NIHVA TECHNOLOGIES PVT. LTD.

NIHVA TECHNOLOGIES PVT. LTD, PUNE
Tel : 020 66304033
Email:- info@nihva.com
Website:- www.nihva.com

	NAME	DATE	SIGN
DRAWN	SUJATA.B	03/01/2022	
CHECK	G.PATIL	03/01/2022	
APPRD.	A.KURHADE	03/01/2022	

If any queries contact : design@nihva.com

ALL DIMENSION ARE IN mm

CLIENT -Fanidhar Mega Food Park Private Limited

LOCATION - GUJARAT

PRODUCT -WICKET GATE | QTY:-01NO

DWG NO:-NIHVA/21-22/CLT/0297 | REV- 0

SCALE: NTS | SCALE:-- 1:1 | SHEET: 01 OF 01