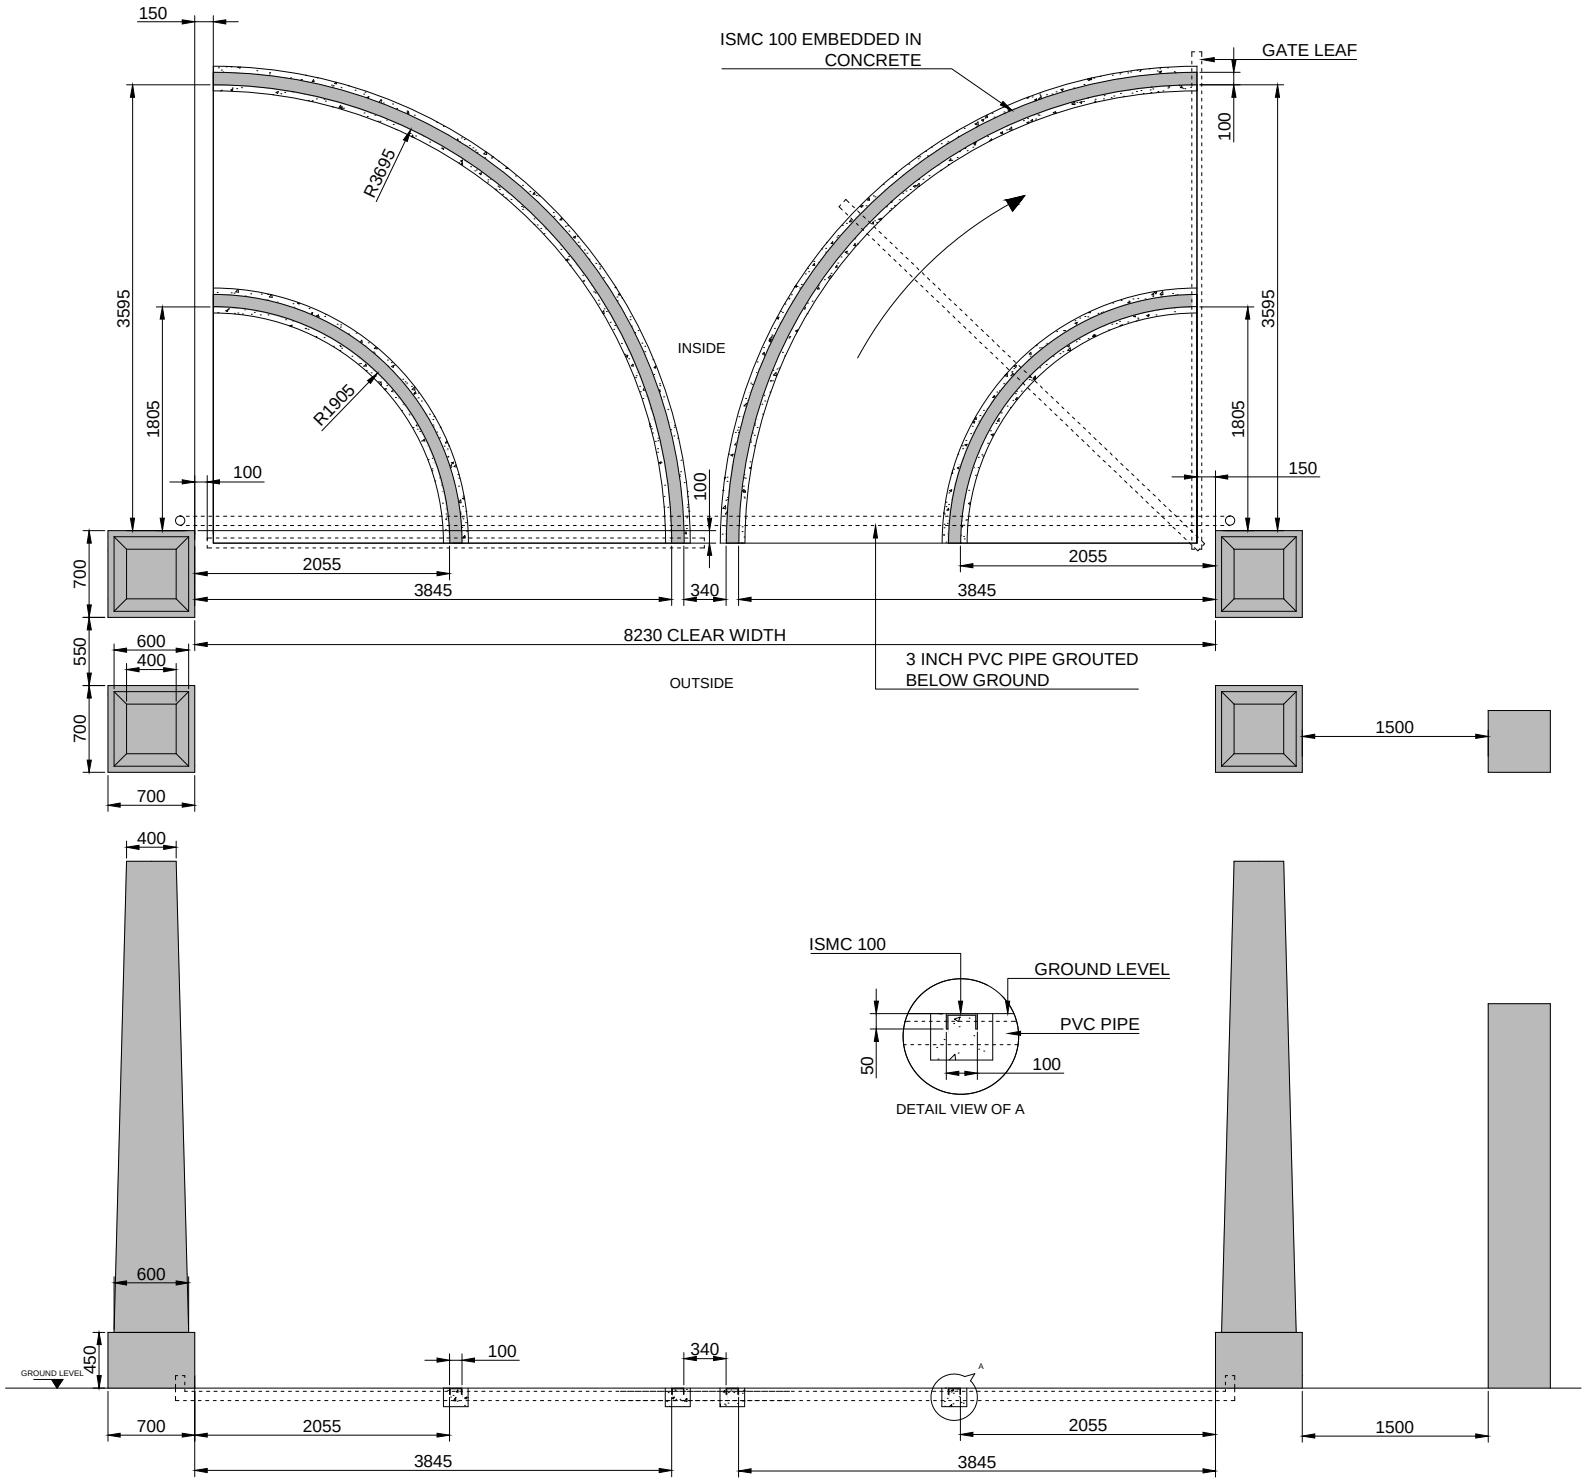

DIMENSION :

CLEAR WIDTH	CLEAR HEIGHT	QUANTITY

MATERIAL :

THICKNESS :

REVISION DONE:-

1.ADDITIONAL RAILS ARE PROVIDED FOR BETTER SUPPORT TO GATE

NIHVA TECHNOLOGIES PVT. LTD.

NIHVA TECHNOLOGY PVT. LTD. PUNE
Email:- info@nihva.com
Website:- www.nihva.com

TITLE:

FOUNDATION OF RAIL FOR AUTOMATIC SWING DOOR

CLIENT'S APPROVAL :

CLIENT - LUPIN LIMITED

PROJECT -

SITE LOCATION - SIKKIM

DWG. NO. : NIHVA/16-17/0099/R02

SCALE: 1:1	WT:	SHEET:1 OF 1

DRAWN BY: OMKAR	DATE: 12-12-2016
CHECK : SAGAR P.	DATE: 12-12-2016
APPROVED BY : R.K.	DATE: 12-12-2016

If any queries contact : projects@nihva.com

NOTE: ALL DIMENSION ARE IN mm

THIS DRAWING & DESIGNING IS THE PROPERTY OF NIHVA TECHNOLOGIES. NOT BE SOLD OR COPY TO ANY OTHER CONCERN.