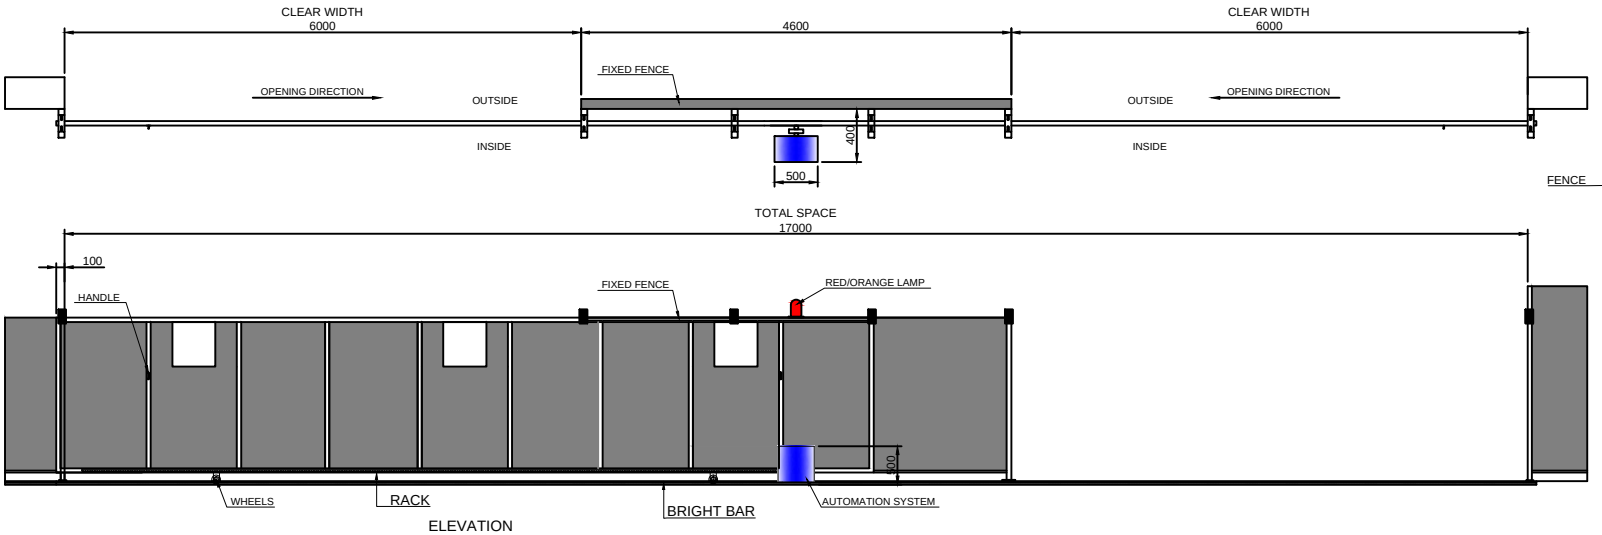
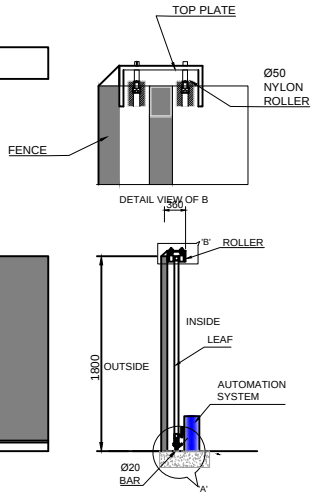
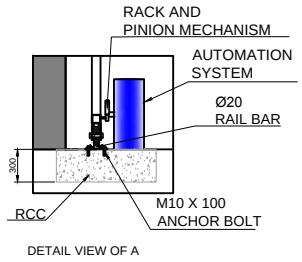



NOTE-
1. ALL REQUIRED CIVIL WORK WILL BE IN CLIENTS SCOPE.
2. TWO COATS OF PRIMER AND TWO COATS OF SYNTHETIC ENAMEL PAINT OF APPROVE SHADE.
3. SAFETY ACCESSORIES : FLASHING LIGHT, SAFETY PHOTOCELL.
4. GATE LEAF WILL BE IN TWO PARTS FOR TRANSPORTATION & WILL BE WELD TOGETHER ON SITE.
5. TWO PUSH BUTTON PENDENT PROVIDE FOR OPERATION.

TOLERANCE- ±10mm

| REV NO | DATE | DRAWN | REMARK |
|---|---|---|---|
| R03 | 01.09.20 | P.A | 1. GATE HEIGHT CHANGE |
| R02 | 28.08.20 | P.A | 1. GATE HEIGHT CHANGE |
| R01 | 20.08.20 | P.A | 1. MOTOR DIMENSIONS ADD |

This drawing & design is the property of NIHVA TECHNOLOGIES. Not to be sold or copied to any other concern.

TITLE: AUTOMATIC SLIDING GATE

NIHVA TECHNOLOGIES PVT. LTD.

NIHVA TECHNOLOGIES PVT. LTD, PUNE
Tel : 020 66304033
Email:- info@nihva.com
Website:- www.nihva.com

| | NAME | SIGN | DATE |
|---|---|---|---|
| DRAWN | P.A | | 06.04.2020 |
| CHECK | G.J | | 06.04.2020 |
| APPRD. | | | |

CLIENT - CLOOS INDIA WELDING TECHNOLOGY PVT LTD
PROJECT -
SITE LOCATION - BHOSARI, PUNE
If any queries contact : design@nihva.com
DWG. NO. : NIHVA/20-21/0001/R03 REV- R03
ALL DIMENSION ARE IN mm
SCALE: NTS WT: SHEET: