
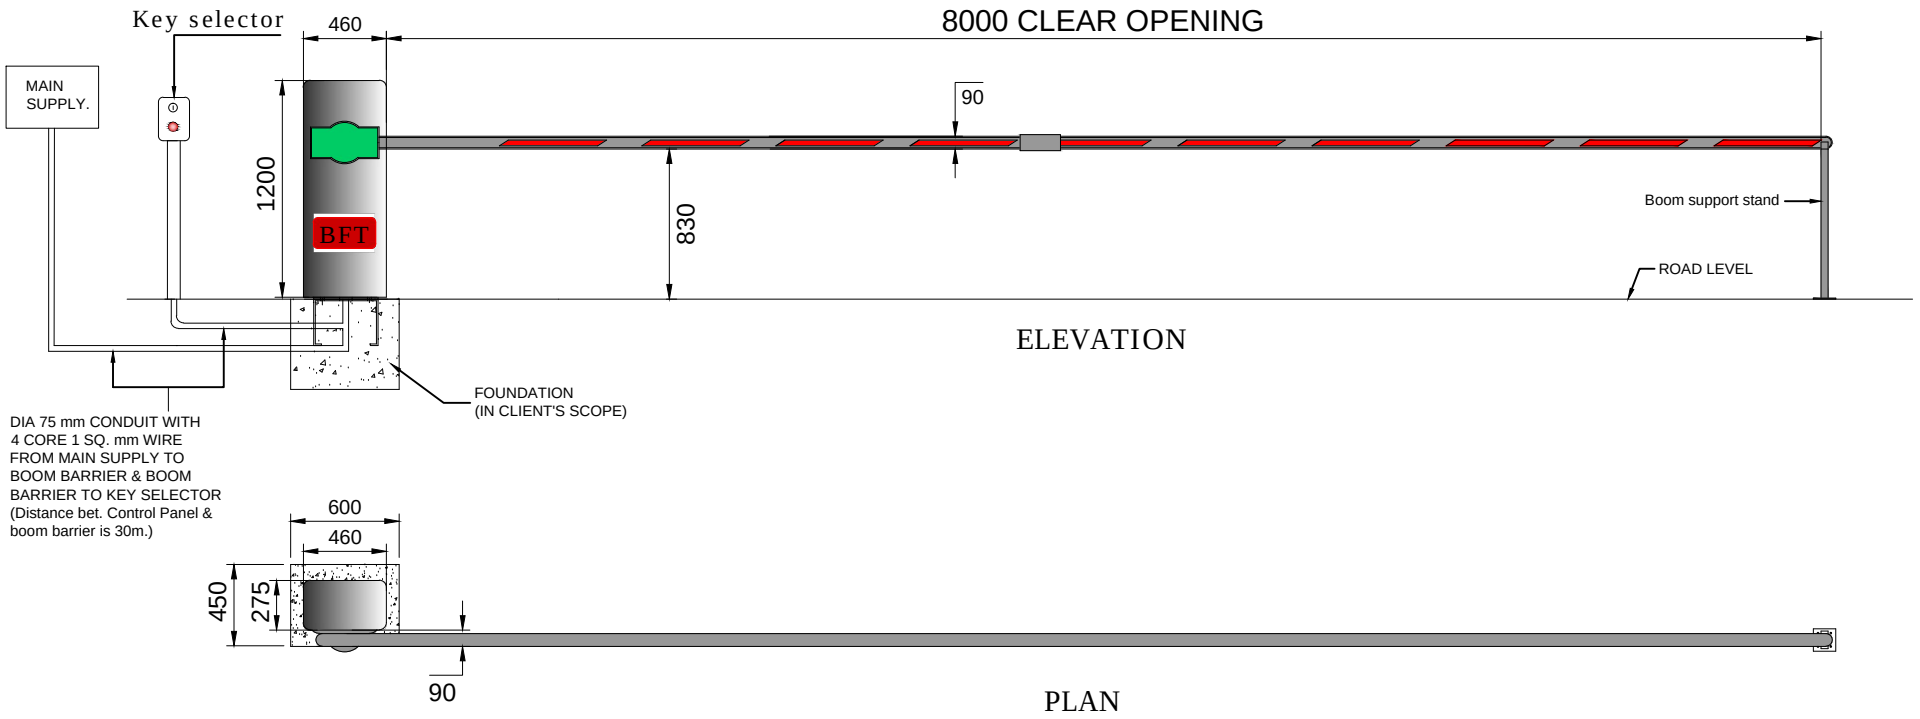


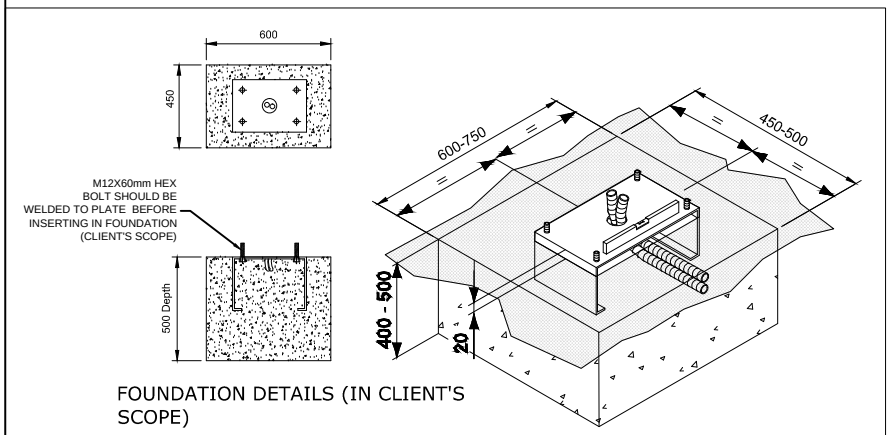

FOUNDATION DETAILS (IN CLIENT'S SCOPE)

SR NO	CLEAR WIDTH	QTY.
1	8000mm	01 NOS

REV 1 Date- 02/02/2018
Cable length is specified by client i.e. distance between control panel & boom barrier is 30m.
REV 2 Date- 10/02/2018
1.Key selector switch is shown. 2.Boom stand is shown 3.cable from boom barrier to key selector is in NIHVA scope.

Note- Boom will be in two parts.

TOLERANCE - ±10mm

This drawing & design is the property of NIHVA TECHNOLOGIES. Not to be sold or copied to any other concern.

TITLE: BOOM BARRIER 8m

NIHVA TECHNOLOGIES PVT. LTD. PUNE
Tel : 020 66304033
Email :- info@nihva.com
Website :- www.nihva.com

	NAME	SIGN	DATE
DRAWN	SURAJ		29-01-2018
CHECK	OMKAR		29-01-2018
APPRD.	SHEKHAR		29-01-2018
MFG.			

If any queries contact : projects@nihva.com

ALL DIMENSION ARE IN mm

CLIENT - INBISCO INDIA PVT LTD.

PROJECT -

SITE LOCATION -AHMEDABAD,GUJARAT.

DWG. NO. : NIHVA/17-18/0341 | REV-2

SCALE: NTS | WT: | SHEET: 01 OF 01