

1

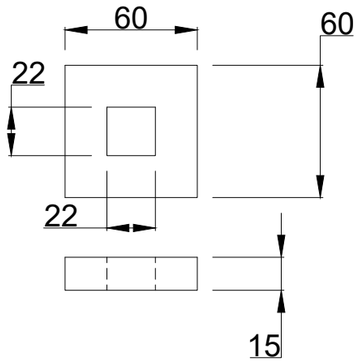

MNTG PLATE - 60 X 60 X 15 MM
MTRL - M.S.

QTY=65 NOS


2

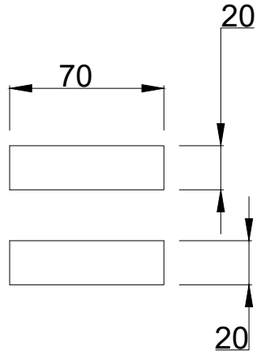

HORIZONTAL SQ. BAR
- 20 X 20 X 70 MM
MTRL - M.S.

QTY=65 NOS

3

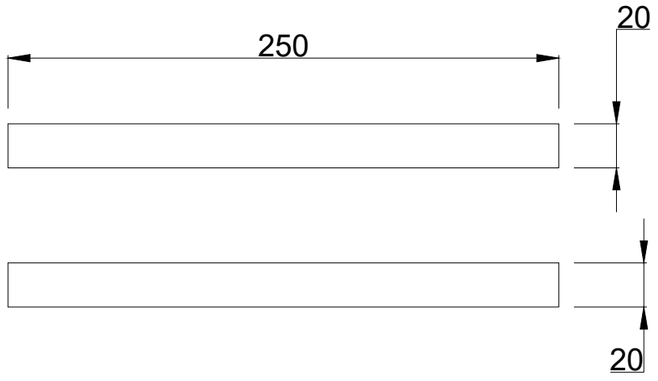


VERTICAL SQ. BAR
- 20 X 20 X 250 MM
MTRL - M.S.

QTY=65 NOS

SUBASSEMBLY AT SHOP
PER HEIGHT MNTG PLATE

QTY=65 NOS

A

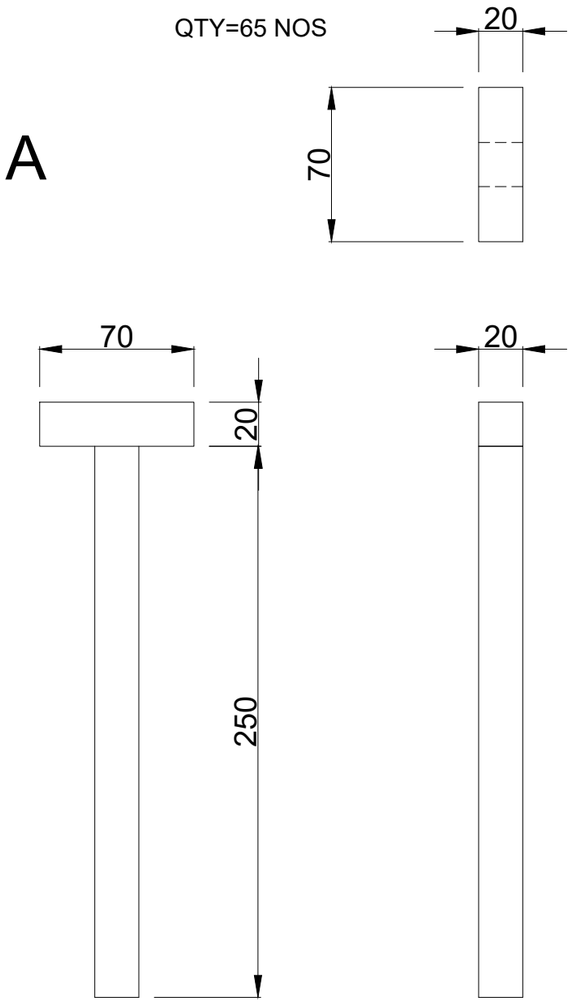


QTY=65 NOS

FINAL FITTING AT SITE
PER HEIGHT MNTG PLATE

QTY=65 NOS

B

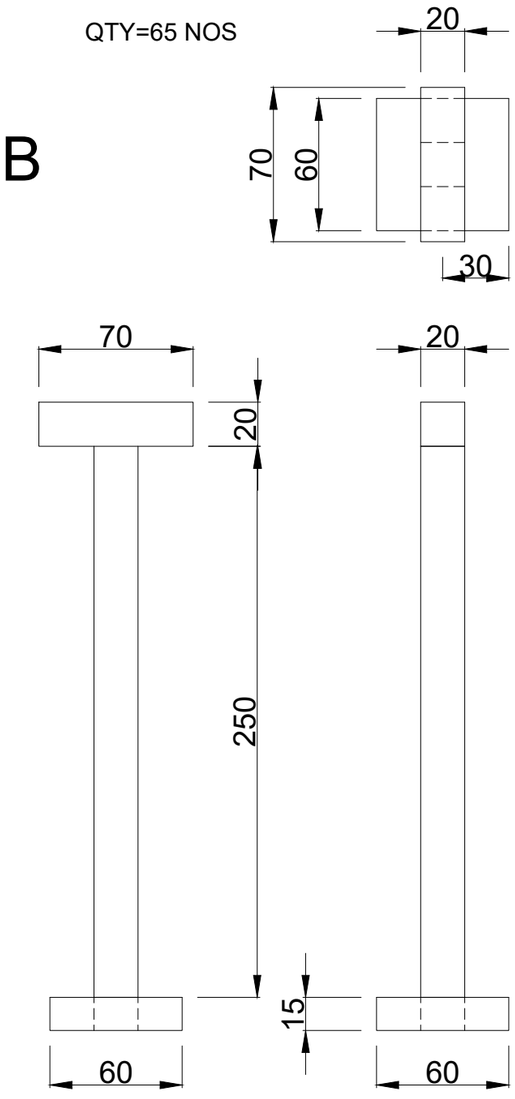

This drawing & design is the property of NIHVA TECHNOLOGIES. Not to be sold or copied to any other concern.

	Date	Revised By

TITLE:- 4 LEAF
CRM DOOR 10

NIHVA TECHNOLOGIES PVT. LTD.

NIHVA TECHNOLOGIES
PVT. LTD. PUNE
Tel : 020 66304033
Email:- info@nihva.com
Website:- www.nihva.com

	NAME	DATE	SIGN
DRAWN	M.SUTAR	15/06/2022	
CHECK	M.SUTAR	15/06/2022	
APPRD.			

CLIENT - NIHVA TECHNOLOGIES PVT.LTD

LOCATION -

PRODUCT - SLIDING DOOR

If any queries contact : design@nihva.com

DWG NO:-NIHVA/22-23/MNFG/0036 REV- 0

ALL DIMENSION ARE IN mm

SCALE: NTS SCALE:-- 1:1 SHEET: 01 OF 01