

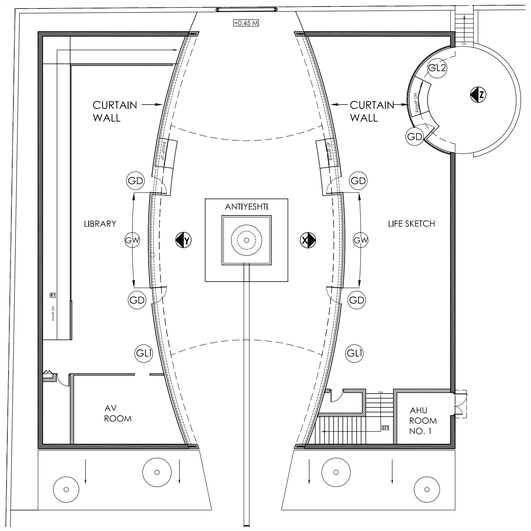


KEY PLAN
SCALE - 1:200

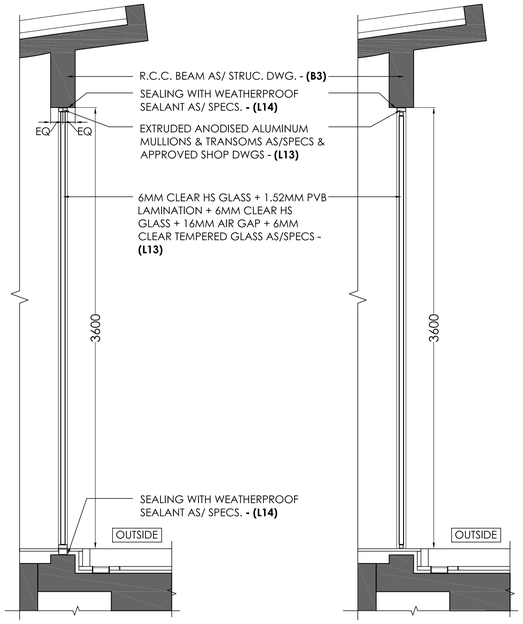


SECTION AA'
(FIXED GLASS PANEL)
SCALE - 1:25


SECTION BB'
(OPENABLE GLASS PANEL)
SCALE - 1:25

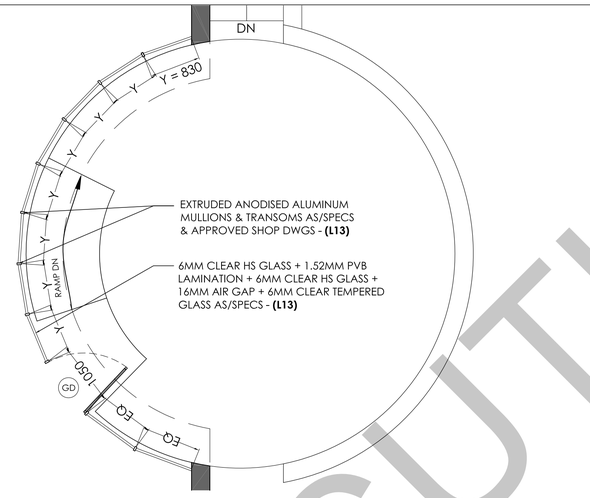

PLAN Z
SCALE - 1:50

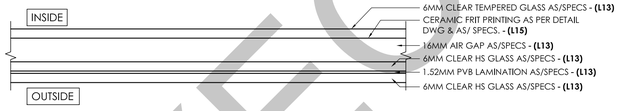


DETAIL AT 'S'
SCALE 1:2

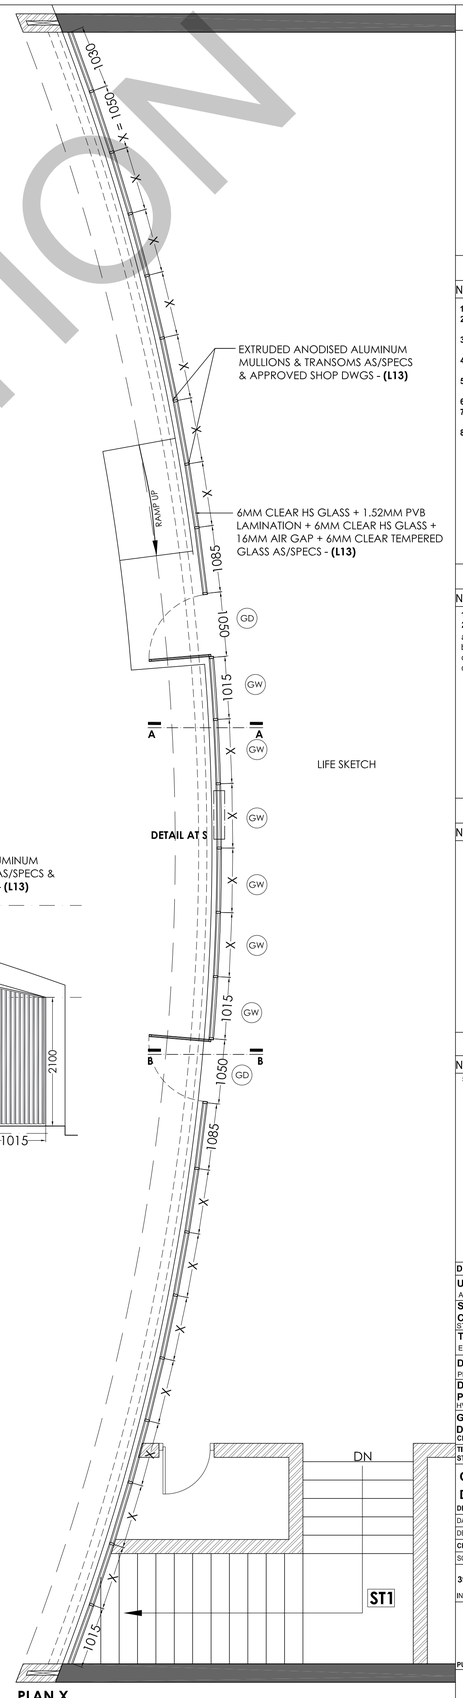

PLAN X
SCALE - 1:50

NOTE:
GLASS CURTAIN WALL DETAILS FOR THE LIBRARY & AV ROOM SHALL BE IDENTICAL MIRROR IMAGES OF THE DETAILS PROVIDED IN PLAN X AND ELEVATION X

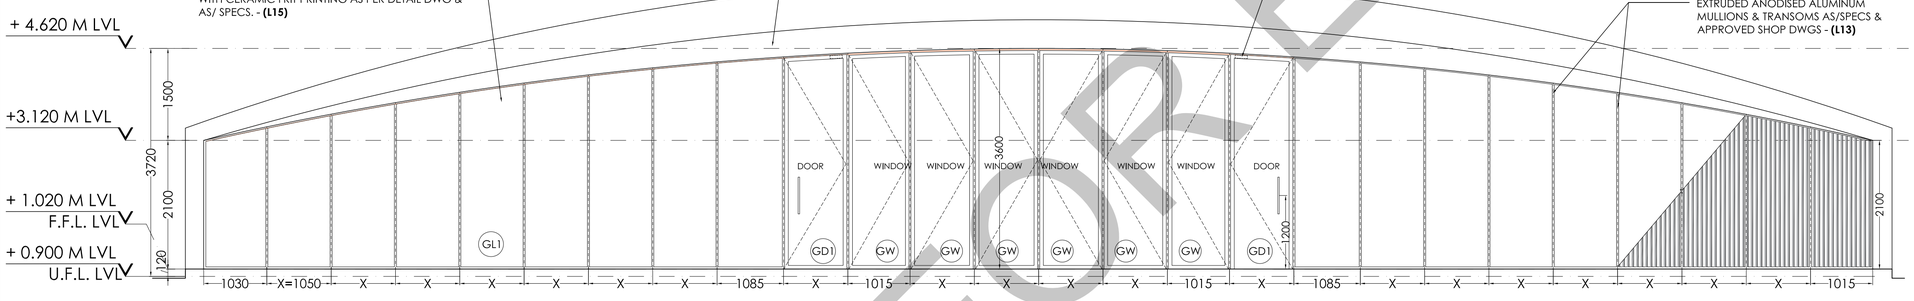


OPENED OUT ELEVATION X & Y
SCALE - 1:50

HARDWARE REQUIREMENTS

GLASS DOOR (GD) - (L14):
- D-PULL HANDLES, BACK TO BACK - 1 SET
- CONCEALED DOOR CLOSER
- MORTISE DEAD LOCK WITH BOTH SIDE KEY OPERATION
- HEAVY DUTY HINGES


GLASS WINDOW (GW) - (L14):
- ALLEN KEY LOCK
- HEAVY DUTY HINGES

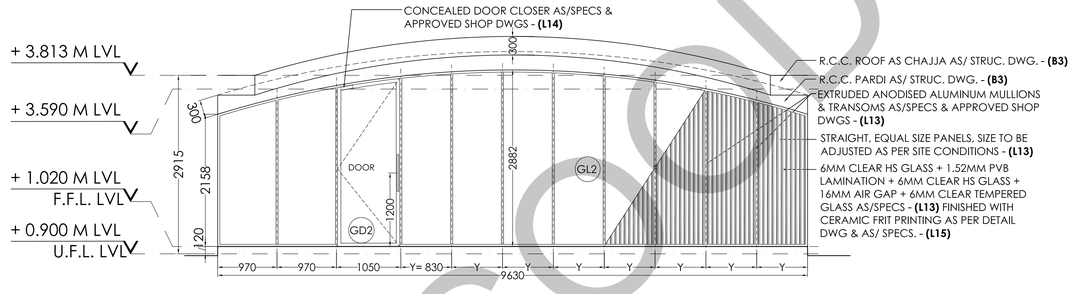

OPENED OUT ELEVATION Z
SCALE - 1:50

HARDWARE REQUIREMENTS

GLASS DOOR (GD) - (L14)
- D-PULL HANDLES, BACK TO BACK - 1 SET
- CONCEALED DOOR CLOSER
- MORTISE DEAD LOCK WITH BOTH SIDE KEY OPERATION
- HEAVY DUTY HINGES

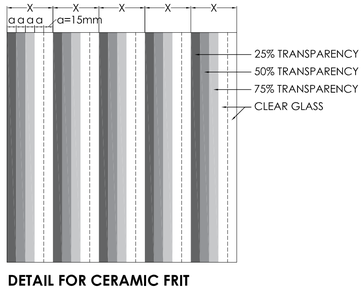

DETAIL FOR CERAMIC FRIT
SCALE - 1:5

CERAMIC FRIT COLOUR = WHITE
NOTE:
SAMPLES & MOCK-UP SHALL BE SUBMITTED FOR APPROVAL BEFORE EXECUTION

NOTES:
1. SHOP DRAWINGS INCLUDING ALL SUPPORTING FRAMEWORK, SAMPLES FOR HARDWARE, GLASS, ETC. TO BE SUBMITTED TO THE ARCHITECT FOR APPROVAL BEFORE EXECUTION
2. ALL SIZES AND QUANTITIES TO BE VERIFIED ON SITE BEFORE EXECUTION
3. **WIND LOAD CALCULATIONS FOR ALL EXTERNAL GLAZING TO BE SUBMITTED ALONG WITH THE SHOP DRAWINGS**

GOOD FOR EXECUTION

KEY PLAN / LEGEND

GENERAL NOTES

No	DESCRIPTION
1.	ALL EXTERNAL WALLS ARE 230 THK
2.	ALL INTERNAL WALLS ARE 115 THK UNLESS OTHERWISE SPECIFIED
3.	ALL LEVELS GIVEN ARE UNFINISHED FLOOR LEVELS (U.F.L.) UNLESS OTHERWISE SPECIFIED
4.	ALL DIMENSIONS ARE IN MM UNLESS OTHERWISE SPECIFIED
5.	ALL LEVELS ARE IN METER UNLESS OTHERWISE SPECIFIED
6.	DO NOT SCALE THIS DRAWING
7.	ANY DISCREPANCY IN THIS DRAWING BE BROUGHT TO THE IMMEDIATE NOTICE OF THE ARCHITECTS
8.	THIS DRAWING IS A COPYRIGHT AND MUST NOT BE USED, DISCLOSED OR REPRODUCED IN ANY FORM WITHOUT EXPRESS PERMISSION OF UCJ ARCHITECTURE & ENVIRONMENT

REFERENCES

No	DESCRIPTION
1.	GENERAL NOTES & LEGEND
2.	REFER RELEVANT DRGS./ DETAILS FOR:
a.	FLOOR PLANS
b.	SECTIONS
c.	ELEVATIONS
d.	STRUCTURE DWGS

REVISIONS

No	DESCRIPTION	DATE

COPIES SENT TO

No	DESCRIPTION	DATE
5	MD, GSIDC (FOR EXECUTION)	04/09/2020

DRAWING ISSUED BY

UCJ ARCHITECTURE & ENVIRONMENT ARCHITECT	●
SHANGHVI & ASSOCIATES CONSULTANTS PVT. LTD. STRUCTURAL CONSULTANT	○
TRANSENERGY ELECTRICAL CONSULTANT	○
DNYANESH G. BHAVE PLUMBING & FIRE FIGHTING CONSULTANT	○
DIKSHIT CONSULTANTS & ENGINEERS PVT. LTD. HVAC CONSULTANT	○
GENERAL ADMINISTRATIVE DEPARTMENT, GOA CLIENT	○

TITLE : CONSTRUCTION OF LATE SHRI. MANOHAR PARRIKAR SMRITI STHAL,MIRAMAR,GOA

GLASS CURTAIN WALL DETAILS
DESCRIPTION

NORTH

DATE 04 SEPT 2020	WORKING DRAWING
DEALT BY MM	
CHKD BY RI	
SCALE AS SHOWN	REMARKS
394/GSS/2020	GSS WD-515
INDEX	DRG.NO.

R0
REVISION NO.

PURPOSE & DATE OF ISSUE

architecture & environment
408 Regent Chambers
208 Nariman Point, Mumbai 400021, India
Phone: +91 22 43483333
Fax.: +91 22 43483334
E-mail: ucjain@ucjain.com
www.ucjain.com