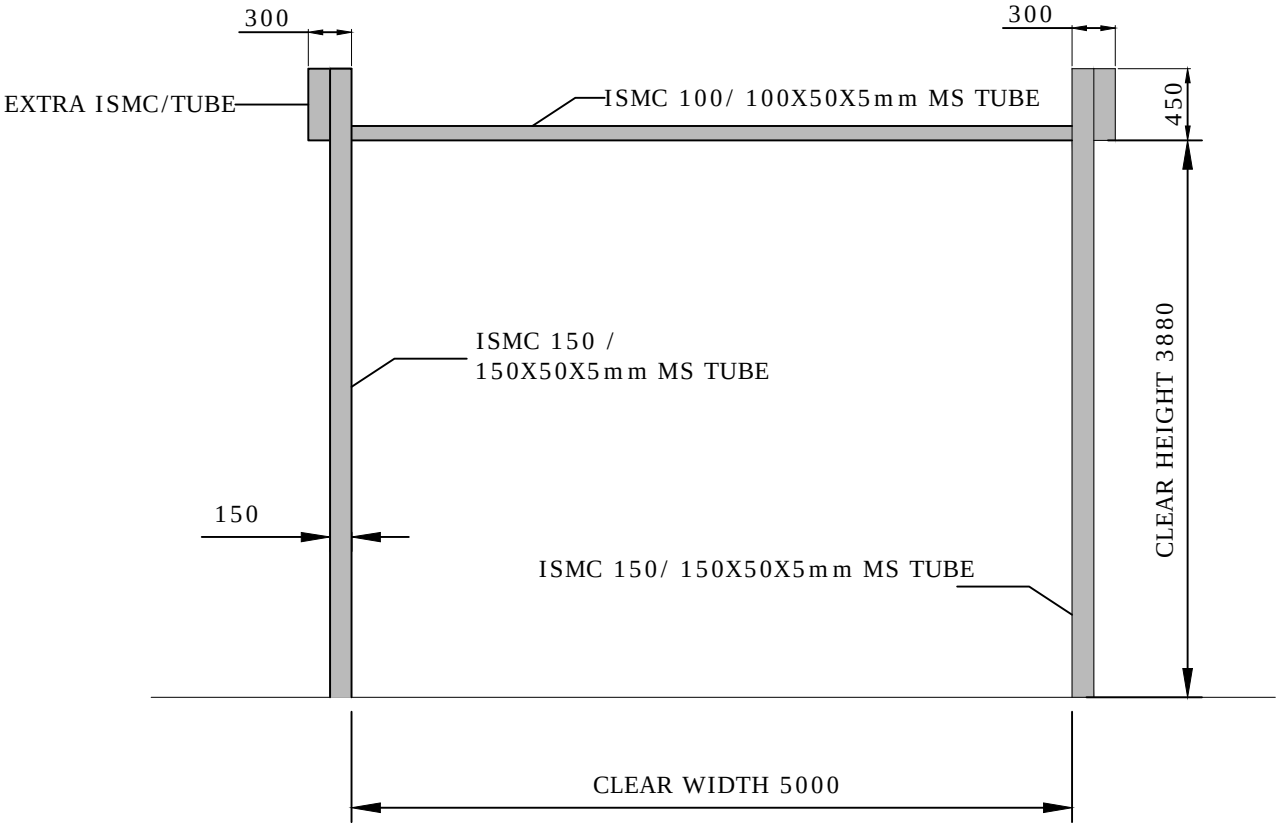

CLEAR WIDTH	CLEAR HEIGHT	QUANTITY
5000	3880	1

NOTE-
1. IF RCC LINTEL FOR MS BRACKET & WALL FOR MS GUIDE IS AVAILABLE AT SITE THEN NO NEED OF MS STRUCTURE.
2. REQUIRED STRUCTURE FOR ROLLING SHUTTER WILL BE CLIENT'S SCOPE.

This drawing & designing is the property of NIHVA TECHNOLOGIES. Not to be sold or copied to any other concern.

TITLE: STRUCTURE FOR ROLLING SHUTTER

NIHVA TECHNOLOGIES PVT. LTD. PUNE
Tel : 020 66304033
Email:- info@nihva.com
Website:- www.nihva.com

	SIGN	DATE
DRAWN	SURAJ	24/08/17
CHECK	SHEKHAR	24/08/17
REV.	00	
APPROVAL		

If any queries contact : projects@nihva.com

ALL DIMENSION ARE IN mm

CLIENT - SHILCHAR TECHNOLOGIES LTD.
PROJECT -
SITE - VADODARA
DWG. NO. : NIHVA/17-18/0180
SCALE: NTS | WT: | SHEET: 01 OF 01