


DRAWING

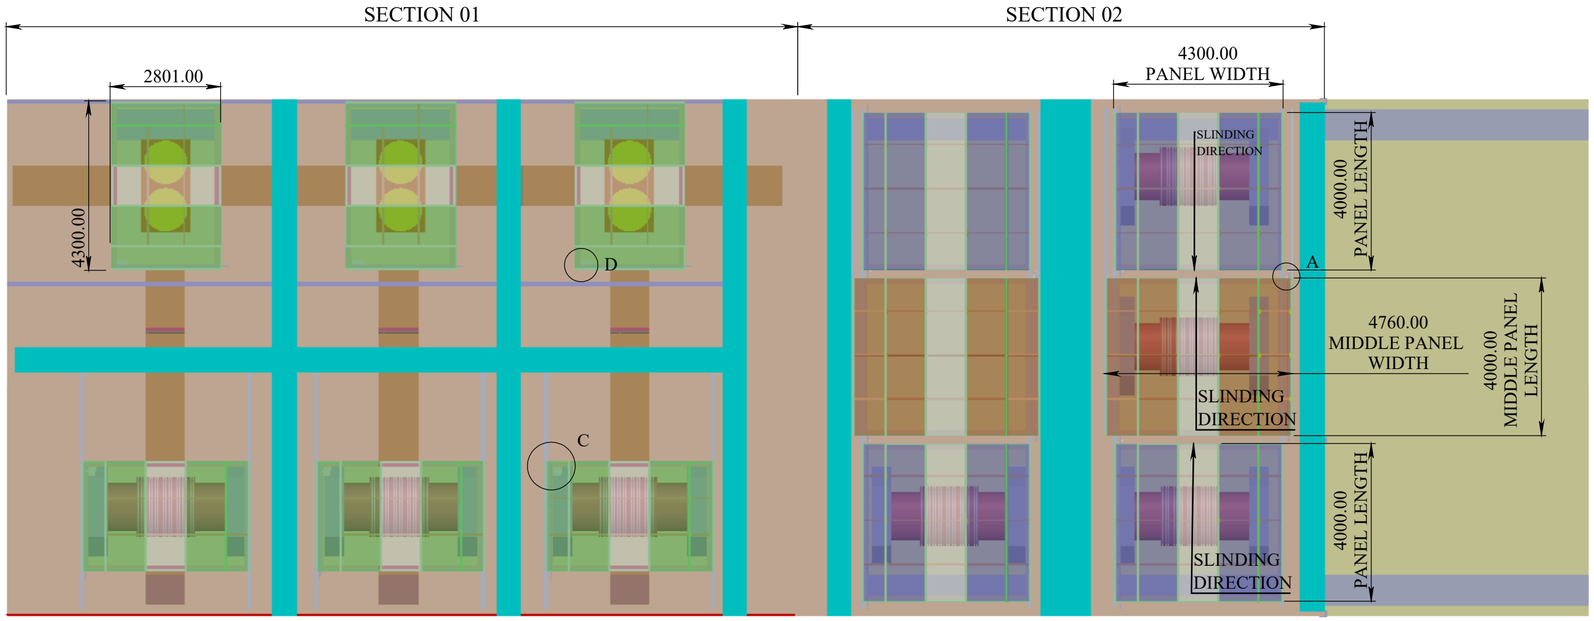


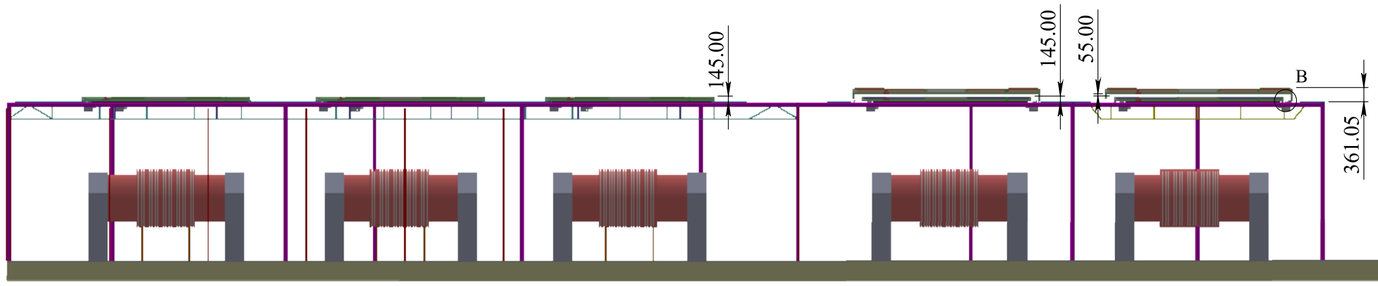

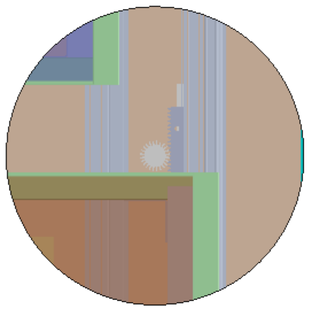


DETAIL A
SCALE 1 : 10

MIDDLE PANEL
MOTOR POSITION

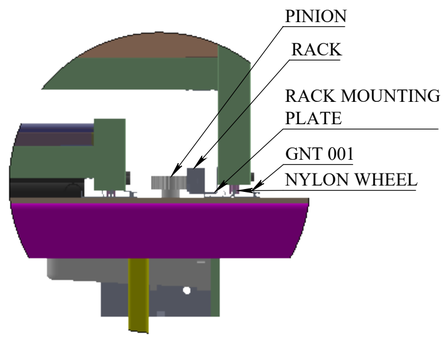


DETAIL B
SCALE 1 : 8

MOTOR MOUNTING
MIDDLE PANEL

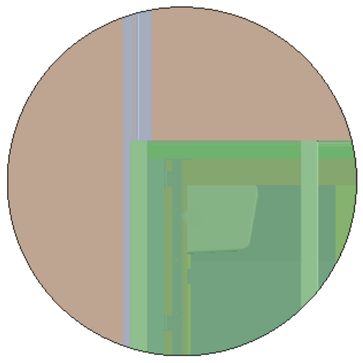

DETAIL C
SCALE 1 : 15

SECTION 01
HORIZONTAL PANEL
MOTOR MOUNTING

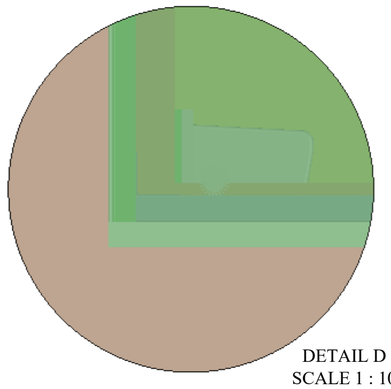

DETAIL D
SCALE 1 : 10

SECTION 02
VERTICAL PANEL
MOTOR MOUNTING

REV DESCRIPTION	DATE	REV NO
03. AIR TIGHTENING & DUST PROOF RUBBER IS ADDED	00-00-2025	REV 03
04. PANEL MODIFICATION	10-07-2025	REV 04
05. SAME UNIT ANTHOER THREE PANEL MODIFICATION	15-07-2025	REV 05
06. MIDDLE PANEL MOTOR POSITION CHANGE	24-07-2025	REV 06

NOTE :

SPECIAL INSTRUCTION'S :

TITLE - ROOF AUTOMATION

DWG NO - NTPL-244-PM-001-00-00-00

NIHVA Technologies Pvt. Ltd.

NIHVA TECHNOLOGIES PVT.LTD.PUNE
Website - www.nihva.com

	NAME	SIGNATURE	DATE
DRAWN	V.W.		23-07-2025
CHK'D	S.P.		24-07-2025
APPV'D	V.T.		24-07-2025

PRODUCT - RETRACTABLE ROOF

PROJECT NO - NTPL-244-PM | REVISION - 06

SITE LOCATION - AHMEDABAD | WEIGHT -

MATRIAL - | QTY - 1


If any queries contact - design.nihva@gmail.com


ALL DIMENSION ARE IN mm | A2

PROJECTION METHOD:


SCALE :

DRAWING

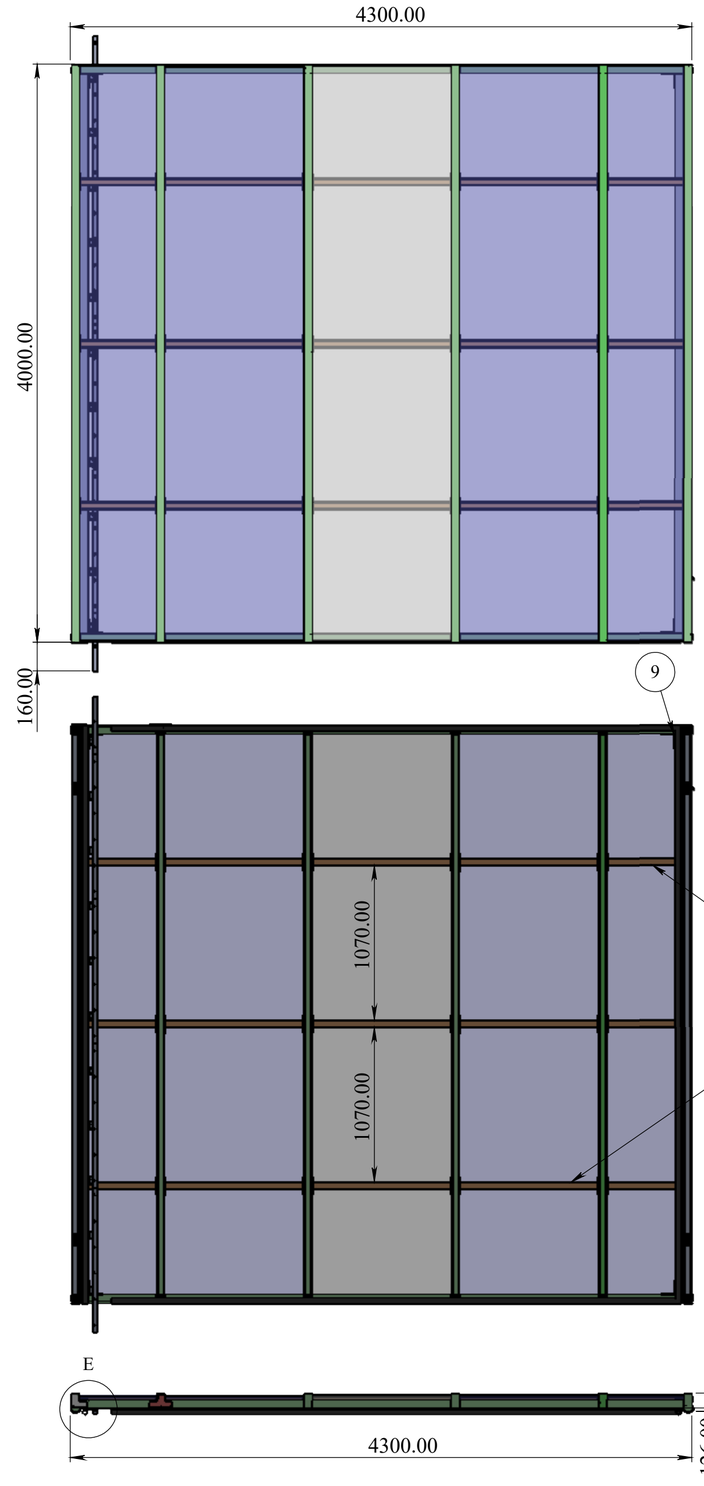


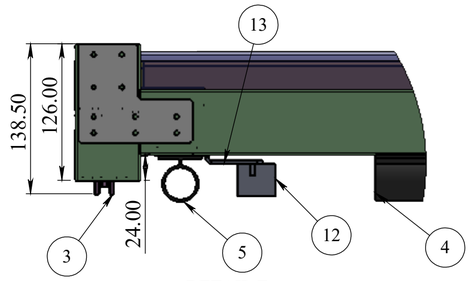

DETAIL E
SCALE 1 : 4

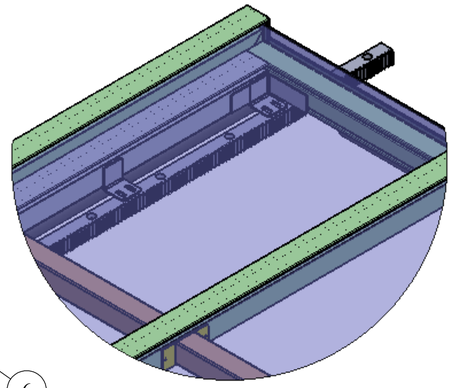

DETAIL F
SCALE 1 : 8

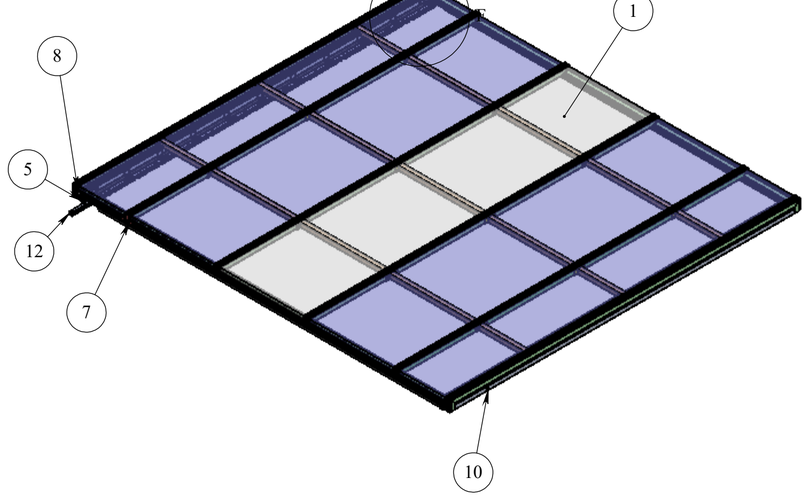

ITEM NO.	PART NUMBER	DESCRIPTION	QTY.
1	.Rev_02_paneel modify-03.		1
2	.Rev_02_panel modifiy-03 intermediate support assembly.		9
3	.Rev_02_SS WHEEL.	SS WHEEL ∅65X18	4
4	NP-PROF01	MS50X50X4T	2
5	NP-PROF01	MS50X50X4T	2
6	.Rev_02_panel modifiy-02 intermediate support assembly.		6
7	T PLATE	156X91X3 MM THK	1
8	L PLATE	91X106X3 MM THK	1
9	.Rev_02_AL INSIDE CORNER WELD PLATE.	196X40X3 MM THK	4
10	C-MSBL12-35.SLDASM	SHOULDER BOLT	1
11	.rev0202RACK.		4
12	RACK CUT 200MM L.		1
13	RACK SUPPORT PLATE.		11

REV DESCRIPTION	DATE	REV NO
	23-07-2025	REV 06
1.		

NOTE :

MODIFIED PANEL NO 01 ASM
QTY - 04 No'S.

SPECIAL INSTRUCTION'S :

TITLE - ROOF AUTOMATION

DWG NO - NTPL-244-PM-001-00-00-00

NIHVA TECHNOLOGIES PVT.LTD.PUNE
Website - www.nihva.com

	NAME	SIGNATURE	DATE
DRAWN	V.W.		23-07-2025
CHK'D	S.P.		25-07-2025
APPV'D	V.T.		25-07-2025


PRODUCT - RETRACTABLE ROOF
PROJECT NO - NTPL-244-PM
REVISION - 06
SITE LOCATION - AHMEDABAD
WEIGHT -
MATRIAL -
QTY - 1
SCALE :
SHEET 2 OF 14


If any queries contact - design.nihva@gmail.com
ALL DIMENSION ARE IN mm
A2
PROJECTION METHOD:


DRAWING

ITEM NO.	PART NUMBER	DESCRIPTION	QTY.
1	.Rev_02_paneel modify-03.		1


REV DESCRIPTION	DATE	REV NO
	23-07-2025	REV 06
1.		

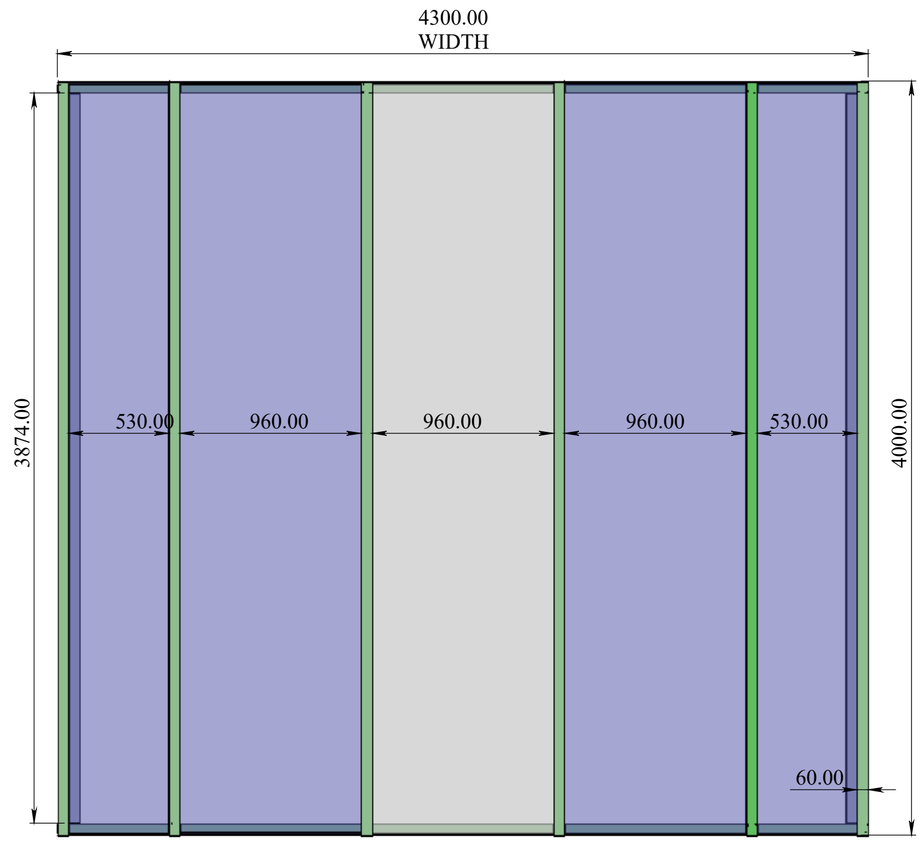


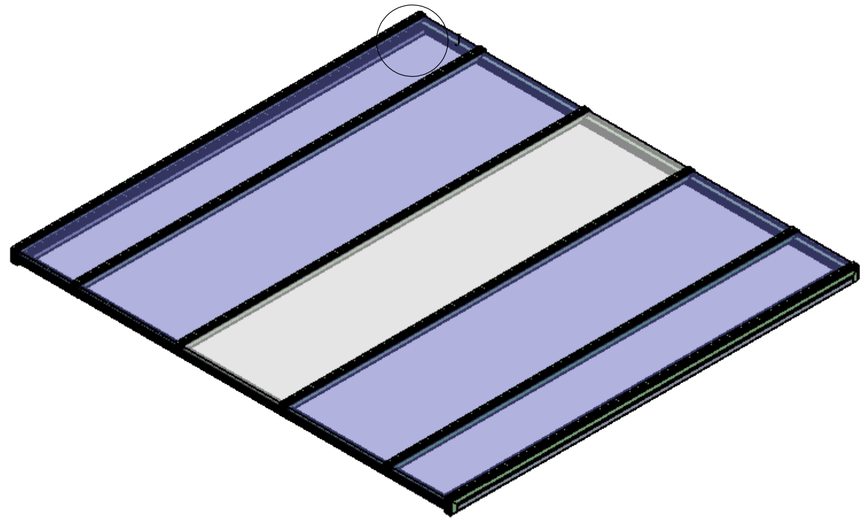

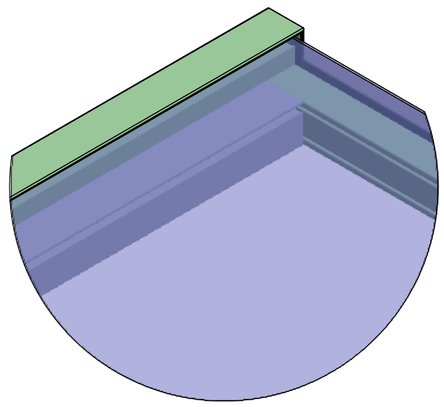

DETAIL J
SCALE 1 : 5

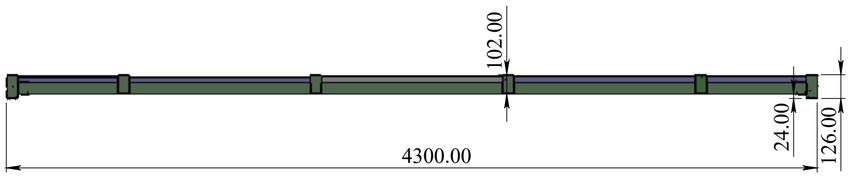

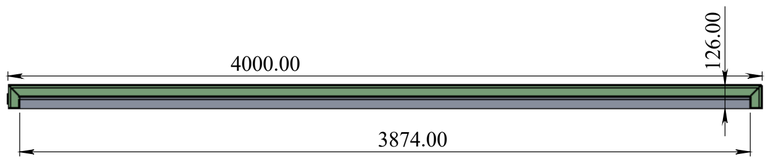

NOTE :

MODIFIED PANEL NO 1
ALL PROFILE IN AL GNT-006
QTY - 4 No'S.

SPECIAL INSTRUCTION'S :

ALL PROFILE IN GNT-006

TITLE - ROOF AUTOMATION

DWG NO - NTPL-244-PM-001-00-00-00

NIHVA TECHNOLOGIES PVT.LTD.PUNE
Website - www.nihva.com

	NAME	SIGNATURE	DATE	
DRAWN	V.W.		23-07-2025	PRODUCT - RETRACTABLE ROOF
CHK'D	S.P.		25-07-2025	PROJECT NO - NTPL-244-PM / REVISION - 06
APPV'D	V.T.		25-07-2025	SITE LOCATION - AHMEDABAD / WEIGHT -
				MATRIAL - / QTY - 1


If any queries contact - design.nihva@gmail.com


ALL DIMENSION ARE IN mm | A2 | PROJECTION METHOD: | SCALE :

DRAWING

REV DESCRIPTION	DATE	REV NO
	24-07-2025	REV 06
1.		

ITEM NO.	PART NUMBER	DESCRIPTION	QTY.
1	INTERMEDIATE SUPPORT TUBE - 960 MM L	SQ - 50X50X1.5 THK	9

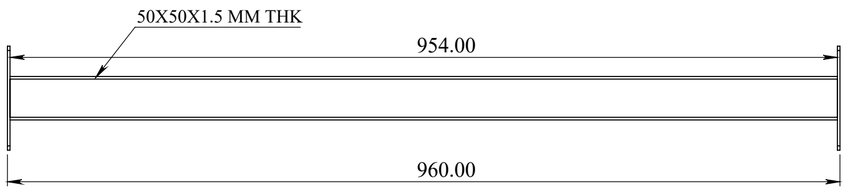

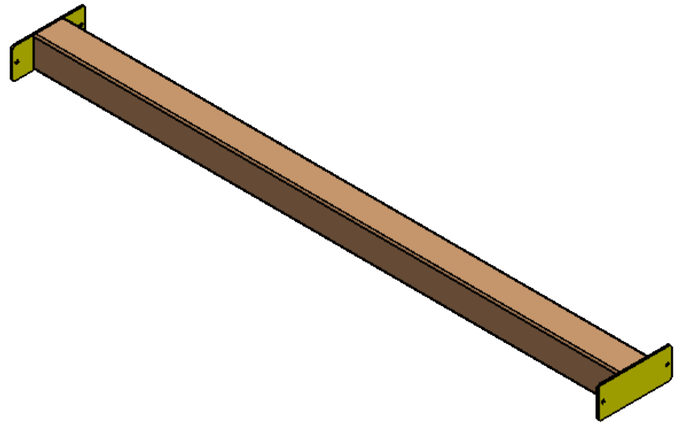

NOTE :

INTERMEDIATE SUPPORT TUBE - 50X50X1.5 MM THK - 960 MM L
ONE PANEL REQ QTY - 09 No'S
TOTAL REQ QTY - 54 No'S
MTL - AL

SPECIAL INSTRUCTION'S :

TITLE - ROOF AUTOMATION

DWG NO - NTPL-244-PM-001-00-00-00


NIHVA TECHNOLOGIES PVT.LTD.PUNE
Website - www.nihva.com


	NAME	SIGNATURE	DATE
DRAWN	V.W.		24-07-2025
CHK'D	S.P.		25-07-2025
APPV'D	V.T.		25-07-2025

PRODUCT - RETRACTABLE ROOF
PROJECT NO - NTPL-244-PM | REVISION - 06
SITE LOCATION - AHMEDABAD | WEIGHT -
MATRIAL - | QTY - 1
If any queries contact - design.nihva@gmail.com | PROJECTION METHOD: | SCALE :
ALL DIMENSION ARE IN mm | A2 | SHEET 4 OF 14

DRAWING

ITEM NO.	PART NUMBER	DESCRIPTION	QTY.
1	INTERMEDIATE SUPPORT TUBE - 530 MM L	REC - 50X50X1.5 THK	6

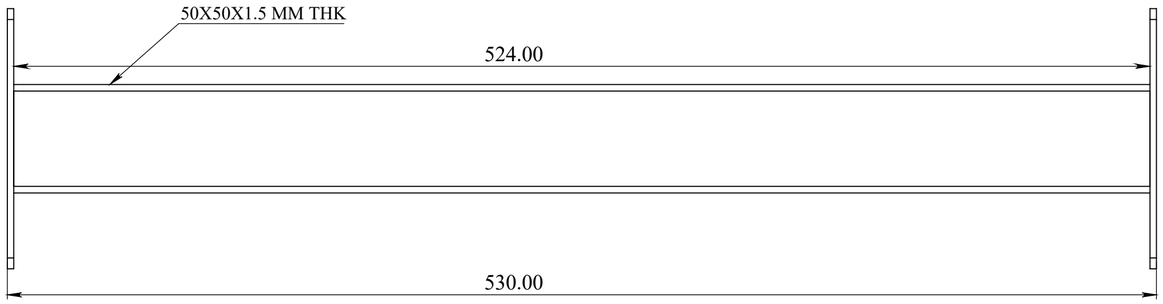

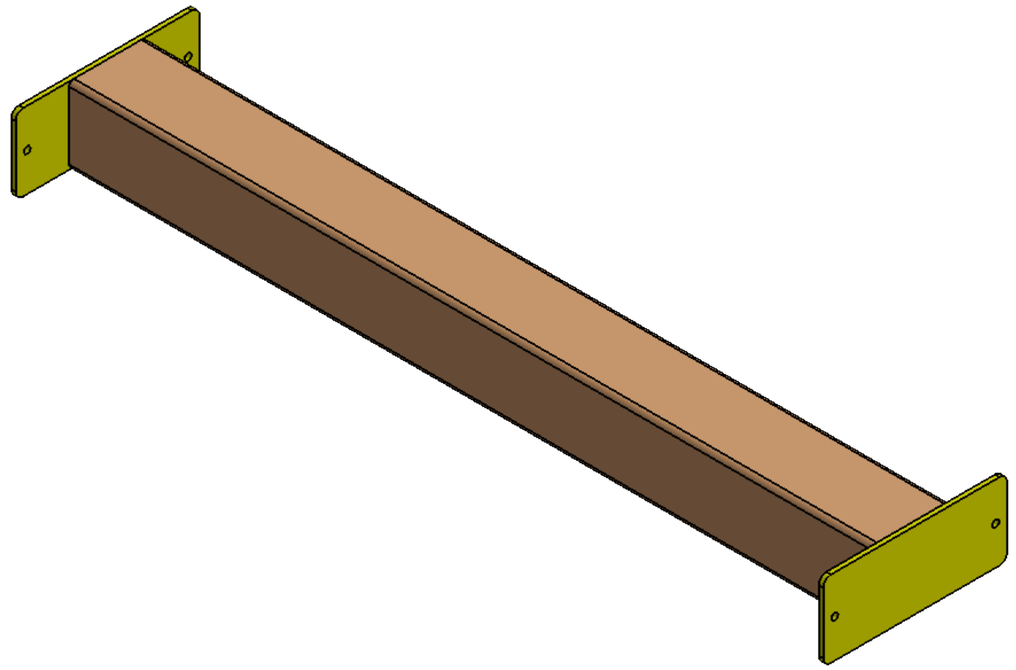

REV DESCRIPTION	DATE	REV NO
	24-07-2025	REV 06
1.		

NOTE :

INTERMEDIATE SUPPORT TUBE - 50X50X1.5 MM THK
ON'E PANEL REQ QTY - 06 No'S
TOTAL REQ QTY - 24 No'S
MTL - AL.

SPECIAL INSTRUCTION'S :

TITLE - ROOF AUTOMATION

DWG NO - NTPL-244-PM-001-00-00-00

NIHVA Technologies Pvt. Ltd.

NIHVA TECHNOLOGIES PVT.LTD.PUNE
Website - www.nihva.com


	NAME	SIGNATURE	DATE
DRAWN	V.W.		24-07-2025
CHK'D	S.P.		25-07-2025
APPV'D	V.T.		25-07-2025


PRODUCT - RETRACTABLE ROOF
PROJECT NO - NTPL-244-PM | REVISION - 06
SITE LOCATION - AHMEDABAD | WEIGHT -
MATRIAL - | QTY - 1
If any queries contact - design.nihva@gmail.com
ALL DIMENSION ARE IN mm | A2
PROJECTION METHOD:
SCALE :
SHEET 5 OF 14


DRAWING

REV DESCRIPTION	DATE	REV NO
	24-07-2025	REV 06
1.		

ITEM NO.	PART NUMBER	DESCRIPTION	QTY.
1	NYLON WHEEL	NYLON WHEEL ∅65X18	1

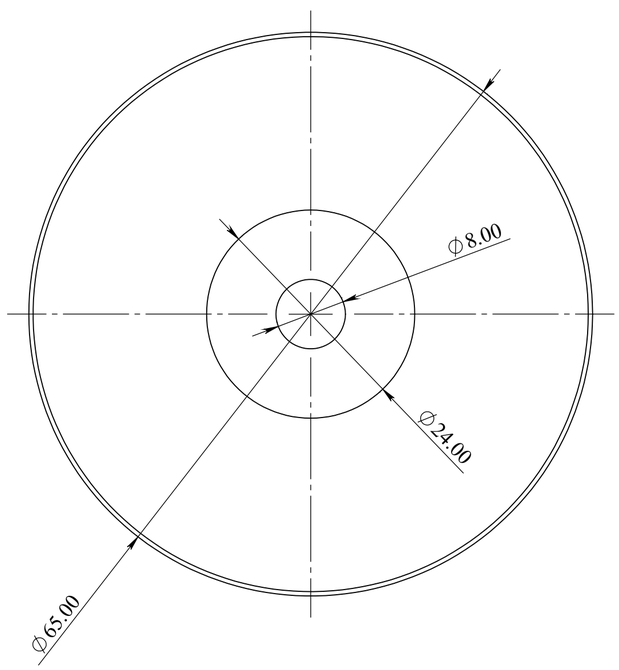

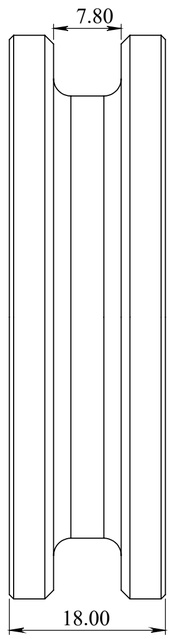

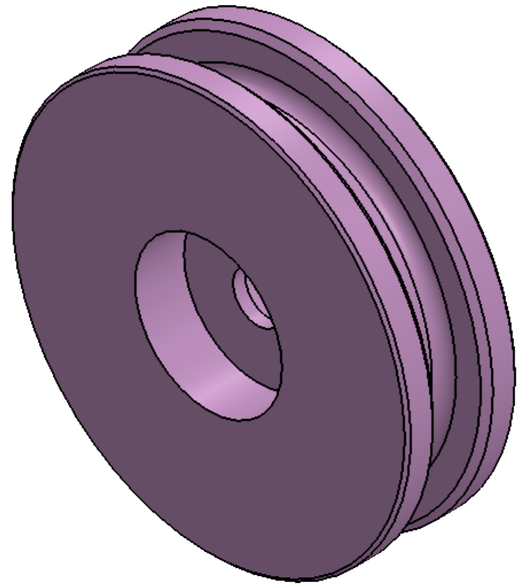

NOTE :

NYLON WHEEL - DIA 65X W 18 MM
ONE PANEL REQ QTY - 04 No'S.
TOTAL REQ QTY - 24 No'S

SPECIAL INSTRUCTION'S :

TITLE - ROOF AUTOMATION

DWG NO - NTPL-244-PM-001-00-00-00

NIHVA Technologies Pvt. Ltd.

NIHVA TECHNOLOGIES PVT.LTD.PUNE
Website - www.nihva.com

	NAME	SIGNATURE	DATE		
DRAWN	V.W.		24-07-2025	PROJECT NO - NTPL-244-PM	REVISION - 06
CHK'D	S.P.		25-07-2025	SITE LOCATION - AHMEDABAD	WEIGHT -
APPV'D	V.T.		25-07-2025	MATRIAL -	QTY - 1

If any queries contact - design.nihva@gmail.com

ALL DIMENSION ARE IN mm | A2


PROJECTION METHOD:


SCALE :

DRAWING

REV DESCRIPTION	DATE	REV NO
	24-07-2025	REV 06
1.		

ITEM NO.	PART NUMBER	DESCRIPTION	QTY.
1	L PLATE	91X106X3 MM THK	04

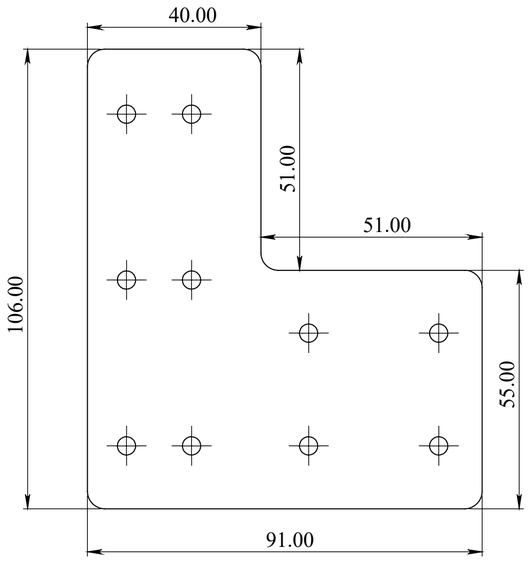

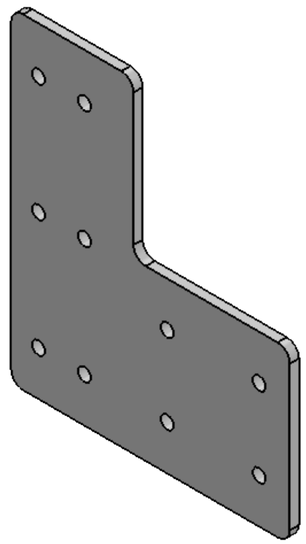

NOTE :

NAME - L PLATE
SIZE - 106X91X3 MM THK
THK - 3 MM
ONE PANEL REQ QTY - 4 No'S
TOTAL REQ QTY - 24 No'S
MTL - SS.

SPECIAL INSTRUCTION'S :

TITLE - ROOF AUTOMATION

DWG NO - NTPL-244-PM-001-00-00-00

NIHVA Technologies Pvt. Ltd.

NIHVA TECHNOLOGIES PVT.LTD.PUNE
Website - www.nihva.com


	NAME	SIGNATURE	DATE
DRAWN	V.W.		24-07-2025
CHK'D	S.P.		25-07-2025
APPV'D	V.T.		25-07-2025


PRODUCT - RETRACTABLE ROOF
PROJECT NO - NTPL-244-PM
REVISION - 06
SITE LOCATION - AHMEDABAD
WEIGHT -
MATRIAL -
QTY - 1
SCALE :
PROJECTION METHOD:
If any queries contact - design.nihva@gmail.com
ALL DIMENSION ARE IN mm
A2
SHEET 7 OF 14

DRAWING

REV DESCRIPTION	DATE	REV NO
	00-00-2025	REV 06
1.		

ITEM NO.	PART NUMBER	DESCRIPTION	QTY.
1	L ANGLE PLATE	17X52X3 MM THK	08

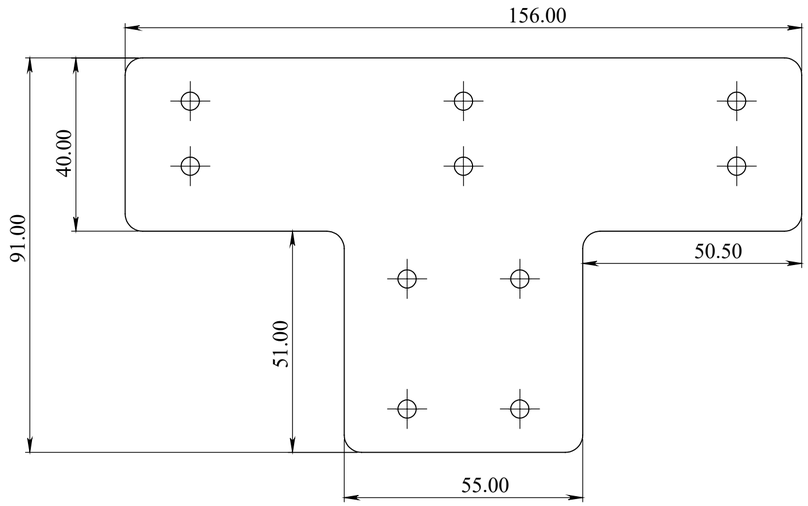

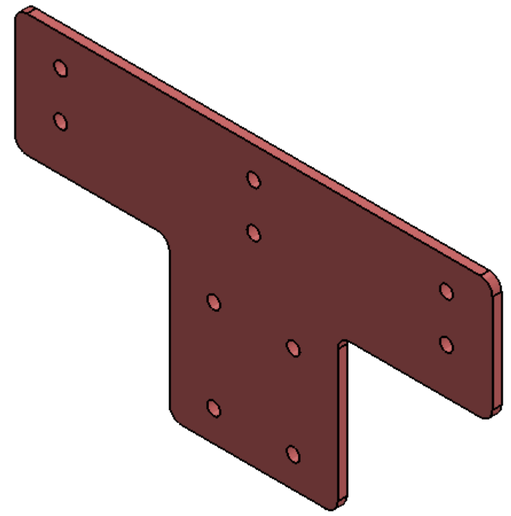

NOTE :

NAME - T PLATE
SIZE - 156X91X3 MM THK
THK - 3 MM
MTL - SS
ONE PANEL REQ QTY - 08 No'S
TOTAL REQ QTY - 48 No'S.

SPECIAL INSTRUCTION'S :

TITLE - ROOF AUTOMATION

DWG NO - NTPL-244-PM-001-00-00-00

NIHVA Technologies Pvt. Ltd.

NIHVA TECHNOLOGIES PVT.LTD.PUNE
Website - www.nihva.com


	NAME	SIGNATURE	DATE
DRAWN	V.W.		23-07-2025
CHK'D	S.P.		24-07-2025
APPV'D	V.T.		24-07-2025


PRODUCT - RETRACTABLE ROOF
PROJECT NO - NTPL-244-PM | REVISION - 06
SITE LOCATION - AHMEDABAD | WEIGHT -
MATRIAL - | QTY - 1
If any queries contact - design.nihva@gmail.com
ALL DIMENSION ARE IN mm | A2
PROJECTION METHOD:
SCALE :


DRAWING

ITEM NO.	PART NUMBER	DESCRIPTION	QTY.
1	.Rev_02_AL INSIDE CORNER WELD PLATE.	196X40X3 MM THK	04

REV DESCRIPTION	DATE	REV NO
	00-00-2025	REV 06
1.		

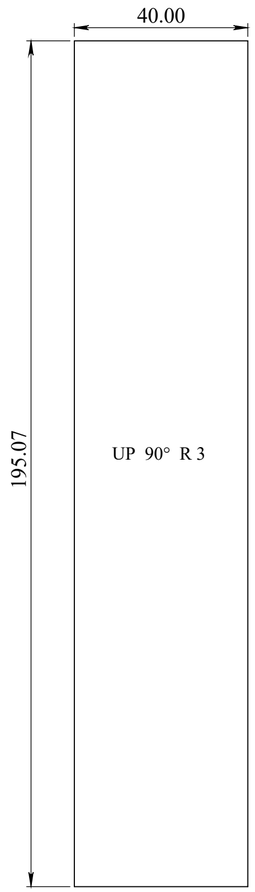

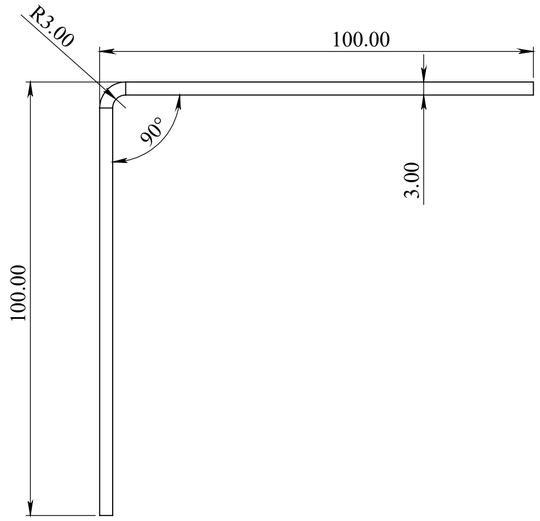

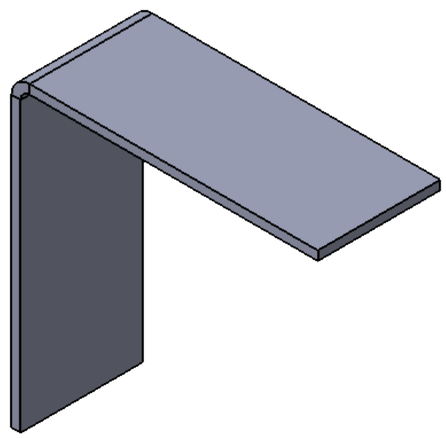

NOTE :

NAME - L ANGLE CORNER WELDING PLATE
SIZE - 195.07X40X3 MM THK
THK - 3 MM
MTL - AL
ONE PANEL REQ QTY - 04 No'S
TOTAL REQ QTY - 24 No'S.

SPECIAL INSTRUCTION'S :

TITLE - ROOF AUTOMATION

DWG NO - NTPL-244-PM-001-00-00-00

NIHVA Technologies Pvt. Ltd.

NIHVA TECHNOLOGIES PVT.LTD.PUNE
Website - www.nihva.com


	NAME	SIGNATURE	DATE
DRAWN	V.W.		23-07-2025
CHK'D	S.P.		24-07-2025
APPV'D	V.T.		24-07-2025


PRODUCT - RETRACTABLE ROOF
PROJECT NO - NTPL-244-PM | REVISION - 06
SITE LOCATION - AHMEDABAD | WEIGHT -
MATRIAL - | QTY - 1
If any queries contact - design.nihva@gmail.com
PROJECTION METHOD:
ALL DIMENSION ARE IN mm | A2 | SCALE :


DRAWING


REV DESCRIPTION	DATE	REV NO
	24-07-2025	REV 06
1.		

ITEM NO.	PART NUMBER	DESCRIPTION	QTY.
1	RACK SUPPORT PLATE.		1

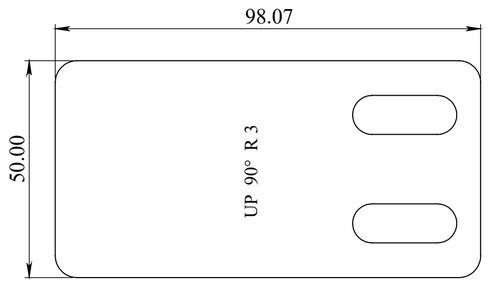

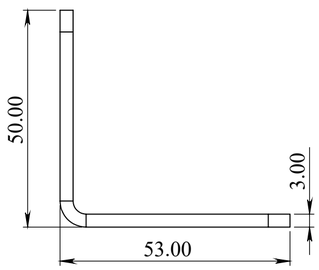

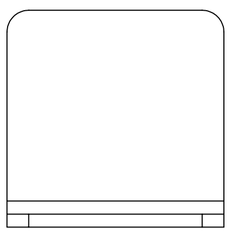

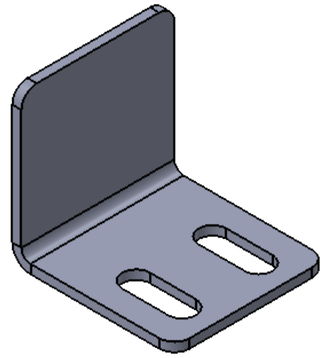

NOTE :

NAME - RACK SUPPORT PLATE
SIZE - 98.07X50X3 MM THK
THK - 3 MM
MTL - AL
ONE PANEL PANEL REQ QTY - 12 No'S
TOTAL REQ QTY - 48 No'S.

SPECIAL INSTRUCTION'S :

TITLE - ROOF AUTOMATION

DWG NO - NTPL-244-PM-001-00-00-00

NIHVA Technologies Pvt. Ltd.

NIHVA TECHNOLOGIES PVT.LTD.PUNE
Website - www.nihva.com

	NAME	SIGNATURE	DATE
DRAWN	V.W.		24-07-2025
CHK'D	S.P.		25-07-2025
APPV'D	V.T.		25-07-2025


PRODUCT - RETRACTABLE ROOF
PROJECT NO - NTPL-244-PM | REVISION - 06
SITE LOCATION - AHMEDABAD | WEIGHT -
MATRIAL - | QTY - 1


If any queries contact - design.nihva@gmail.com
ALL DIMENSION ARE IN mm | A2
PROJECTION METHOD:
SCALE :
SHEET 10 OF 14

DRAWING

REV DESCRIPTION	DATE	REV NO
	24-07-2025	REV 06
1.		

ITEM NO.	PART NUMBER	DESCRIPTION	QTY.
1	.Rev_02_RACK..		1

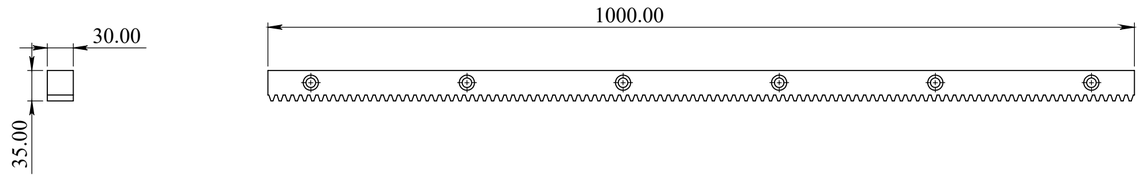

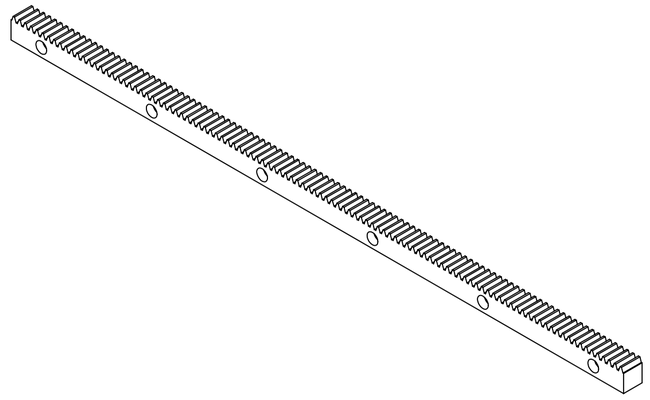

NOTE :

NAME - RACK
QTY - 30 No'S.

SPECIAL INSTRUCTION'S :


TITLE - ROOF AUTOMATION


DWG NO - NTPL-244-PM-001-00-00-00

NIHVA TECHNOLOGIES PVT.LTD.PUNE
Website - www.nihva.com


	NAME	SIGNATURE	DATE		
DRAWN	V.W.		24-07-2025	PRODUCT - RETRACTABLE ROOF	
CHK'D	S.P.		25-07-2025	PROJECT NO - NTPL-244-PM	REVISION - 06
APPV'D	V.T.		25-07-2025	SITE LOCATION - AHMEDABAD	WEIGHT -
				MATRIAL -	QTY - 1
If any queries contact - design.nihva@gmail.com				PROJECTION METHOD:	SCALE :
ALL DIMENSION ARE IN mm			A2		SHEET 11 OF 14

DRAWING

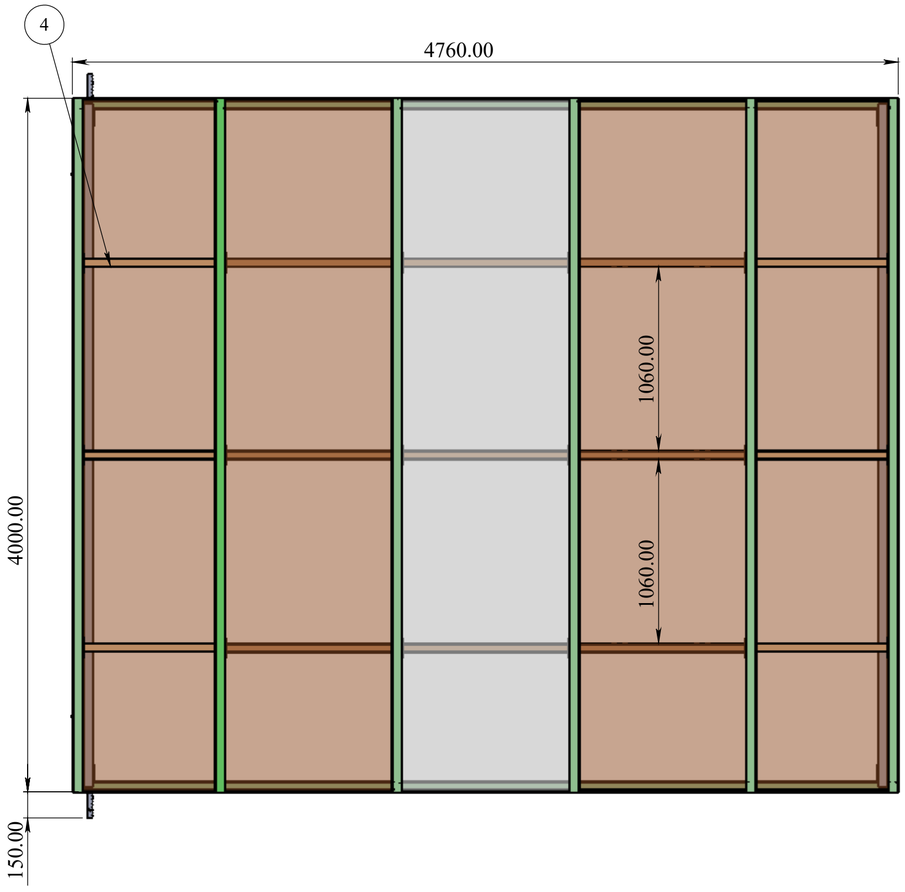


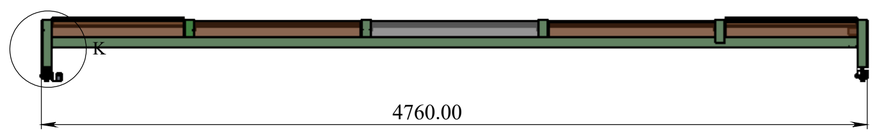

ITEM NO.	PART NUMBER	DESCRIPTION	QTY.
1	.Rev_02_paneel modify-03..		1
2	.Rev_02_panel modifiy-03 intermediate support assembly..		9
3	.Rev_02_SS WHEEL..	SS WHEEL ∅65X18	4
4	.Rev_02_panel modifiy-02 intermediate support assembly..		6
5	L ANGLE PLATE	17X52X3 MM THK	1
6	L PLATE	91X106X3 MM THK	1
7	.Rev_02_AL INSIDE CORNER WELD PLATE..	196X40X3 MM THK	4
8	C-MSBL12-35.SLDASM	SHOULDER BOLT	4
9	.Rev_02_RACK..		4
10	RACK CUT 200MM L.		1
11	2ND OPEN POSITININGRACK SUPPORT PLATE.		11

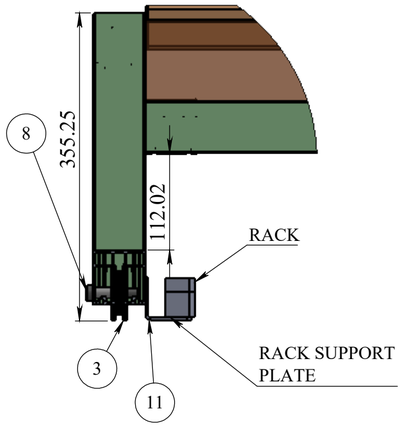

DETAIL K
SCALE 1 : 5

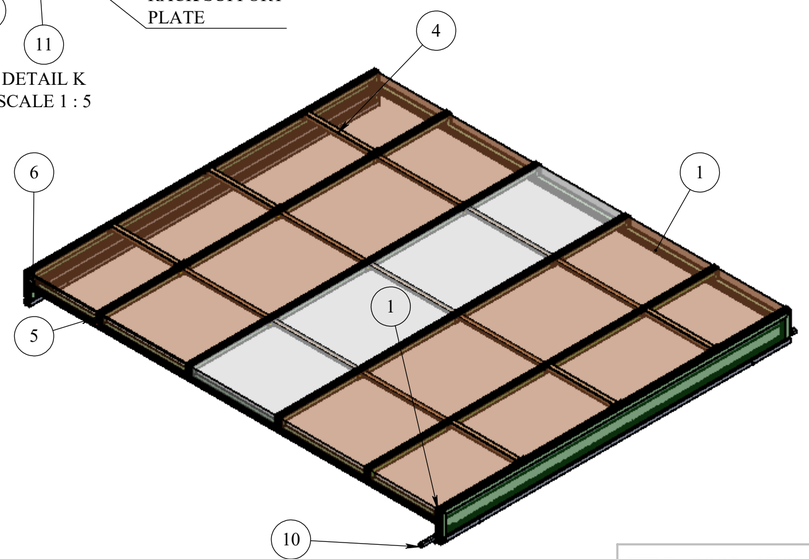

REV DESCRIPTION	DATE	REV NO
	24-07-2025	REV 06
1.		

NOTE :

MODIFIED MIDDLE PANEL
QTY - 02 No'S

SPECIAL INSTRUCTION'S :

TITLE - ROOF AUTOMATION

DWG NO - NTPL-244-PM-001-00-00-00

NIHVA TECHNOLOGIES PVT.LTD.PUNE
Website - www.nihva.com


	NAME	SIGNATURE	DATE
DRAWN	V.W.		24-07-2025
CHK'D	S.P.		25-07-2025
APPV'D	V.T.		25-07-2025


PRODUCT - RETRACTABLE ROOF
PROJECT NO - NTPL-244-PM | REVISION - 06
SITE LOCATION - AHMEDABAD | WEIGHT -
MATRIAL - | QTY - 1
If any queries contact - design.nihva@gmail.com
ALL DIMENSION ARE IN mm | A2
PROJECTION METHOD:
SCALE :
SHEET 12 OF 14


DRAWING


REV DESCRIPTION	DATE	REV NO
	24-07-2025	REV 06
1.		


ITEM NO.	PART NUMBER	DESCRIPTION	QTY.
1	.Rev_02_paneel modify-03.. MIDDLE PANEL		2

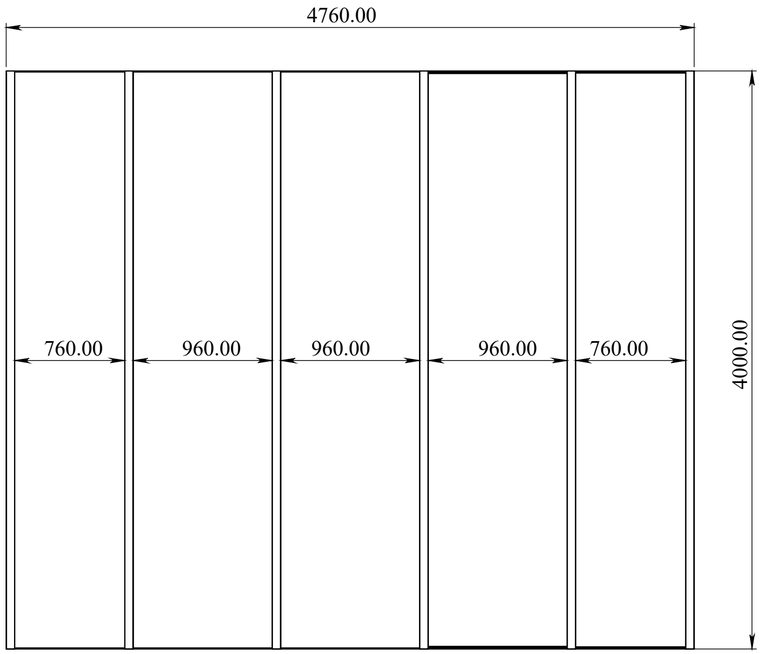

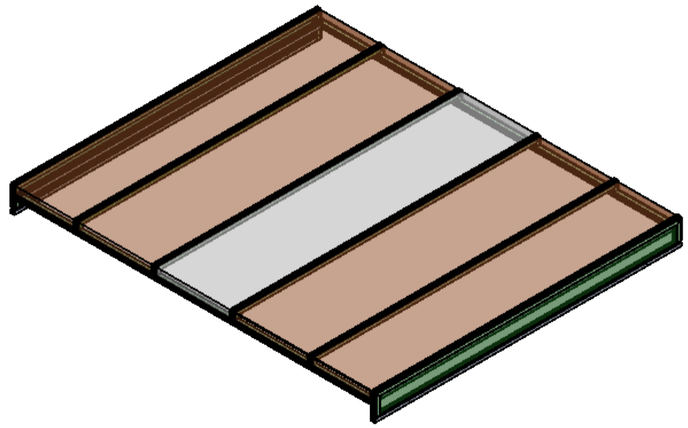

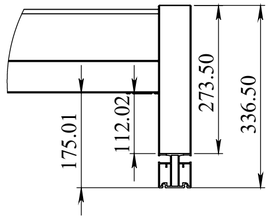

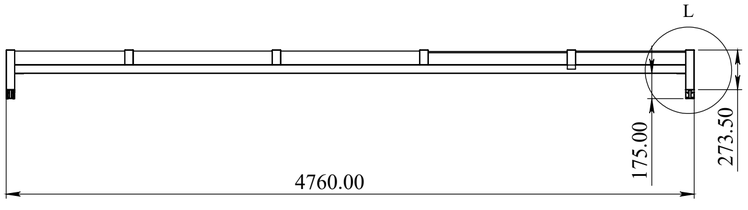

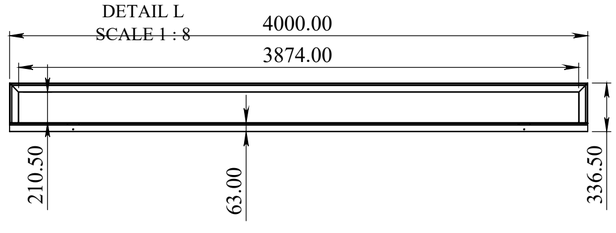

NOTE :

MIDDLE NODIFIED PANEL
QTY - 02 No'S.

SPECIAL INSTRUCTION'S :

TITLE - ROOF AUTOMATION

DWG NO - NTPL-244-PM-001-00-00-00

NIHVA TECHNOLOGIES PVT.LTD.PUNE
Website - www.nihva.com


	NAME	SIGNATURE	DATE
DRAWN	V.W.		24-07-2025
CHK'D	S.P.		25-07-2025
APPV'D	V.T.		25-07-2025


PRODUCT - RETRACTABLE ROOF
PROJECT NO - NTPL-244-PM | REVISION - 06
SITE LOCATION - AHMEDABAD | WEIGHT -
MATRIAL - | QTY - 1
If any queries contact - design.nihva@gmail.com
ALL DIMENSION ARE IN mm | A2
PROJECTION METHOD:
SCALE :
SHEET 13 OF 14

DRAWING

REV DESCRIPTION	DATE	REV NO
	24-07-2025	REV 06
1.		

ITEM NO.	PART NUMBER	DESCRIPTION	QTY.
1	INTERMEDIATE SUPPORT TUBE - 760 MM L	REC - 50X50X1.5T	1

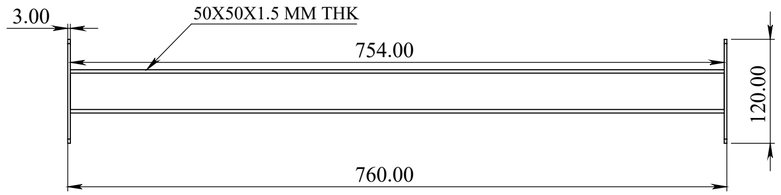

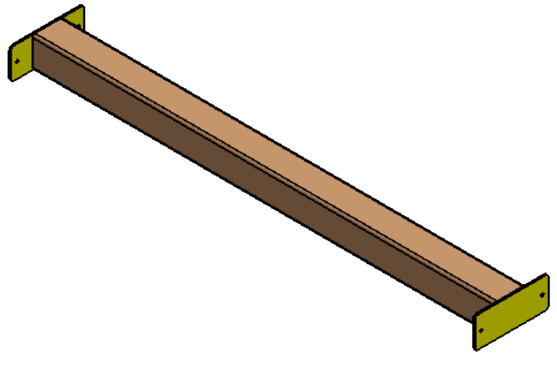

NOTE :

NAME - INTERMEDIATE SUPPORT TUBE
SIZE - 50X50X1.5 MM THK - 760 MM L
MTL - AL
ONE PANEL REQ QTY - 06 No'S
TOTAL REQ QTY - 12 No'S.

SPECIAL INSTRUCTION'S :

TITLE - ROOF AUTOMATION

DWG NO - NTPL-244-PM-001-00-00-00

NIHVA Technologies Pvt. Ltd.

NIHVA TECHNOLOGIES PVT.LTD.PUNE
Website - www.nihva.com

	NAME	SIGNATURE	DATE
DRAWN	V.W.		24-07-2025
CHK'D	S.P.		25-07-2025
APPV'D	V.T.		25-07-2025

PRODUCT - RETRACTABLE ROOF
PROJECT NO - NTPL-244-PM
REVISION - 06
SITE LOCATION - AHMEDABAD
WEIGHT -
MATRIAL -
QTY - 1
If any queries contact - design.nihva@gmail.com
PROJECTION METHOD:
SCALE :
ALL DIMENSION ARE IN mm
A2