




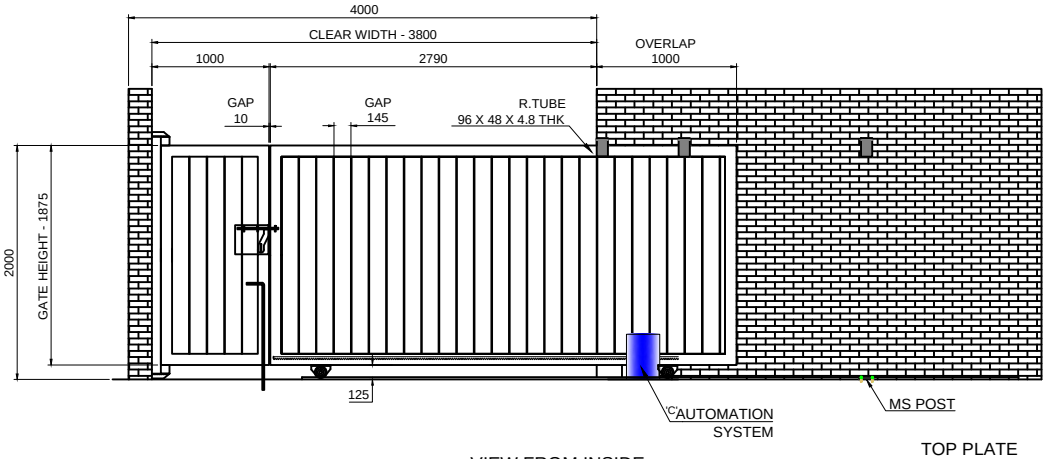

VIEW FROM INSIDE

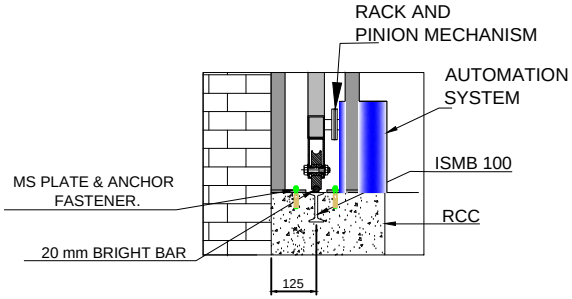

DETAIL VIEW OF A

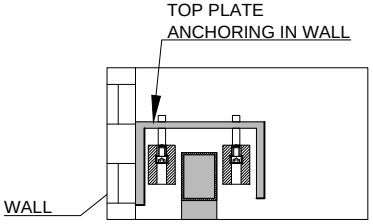

DETAIL VIEW OF B

REV NO	REV DATE	DRAWN	REMARK
R03	09.11.2019	P.V.A	1. POST DESIGN CHANGE 2. ISMB CENTER DISTANCE CHANGE.
R02	04.11.2019	P.V.A	1. CLEAR WIDTH CHANGE.
R01	18.09.2019	P.V.A	1. GATE POSITION CHANGE

SR.NO	RAL CODE	RAL COLOR
04	RAL 7035	LIGHT GREY
03	RAL 5002	ULTRAMARINE BLUE
02	RAL 9002	GREY WHITE
01	RAL 1004	GOLDEN YELLOW

DIMENSION :

CLEAR WIDTH	CLEAR HEIGHT	QUANTITY
2800 mm	1875mm	1 NO
1000 mm	1875mm	1 NO

MATERIAL: MS

THICKNESS :

NOTE-
1. ALL REQUIRED CIVIL WORK WILL BE IN CLIENTS SCOPE.

TOLERANCE:- ± 05mm

NIHVA
NIHVA TECHNOLOGIES PVT. LTD.
Website:- www.nihva.com
NIHVA TECHNOLOGIES PVT. LTD. PUNE
Email:- info@nihva.com
TEL :020 66304033

TITLE:
AUTOMATIC SINGLE LEAF SLIDING GATE & MANUAL WICKET GATE

CLIENT'S APPROVAL :

CLIENT - DHAMALE

PROJECT -

SITE LOCATION - NIGADI

DWG. NO. : NIHVA/19-20/0088/R03 | REV. : R03

SCALE: NTS | WT: | SHEET:1 OF 1

DRAWN	P.A		17.09.2019
CHECK	G.J		17.09.2019
APPROVED			

IF ANY QUERIES CONTACT:- design@nihva.com

NOTE: ALL DIMENSIONS ARE IN mm

THIS DRAWING & DESIGN IS THE PROPERTY OF NIHVA TECHNOLOGIES. NOT TO BE SOLD OR COPIED TO ANY OTHER CONCERN.