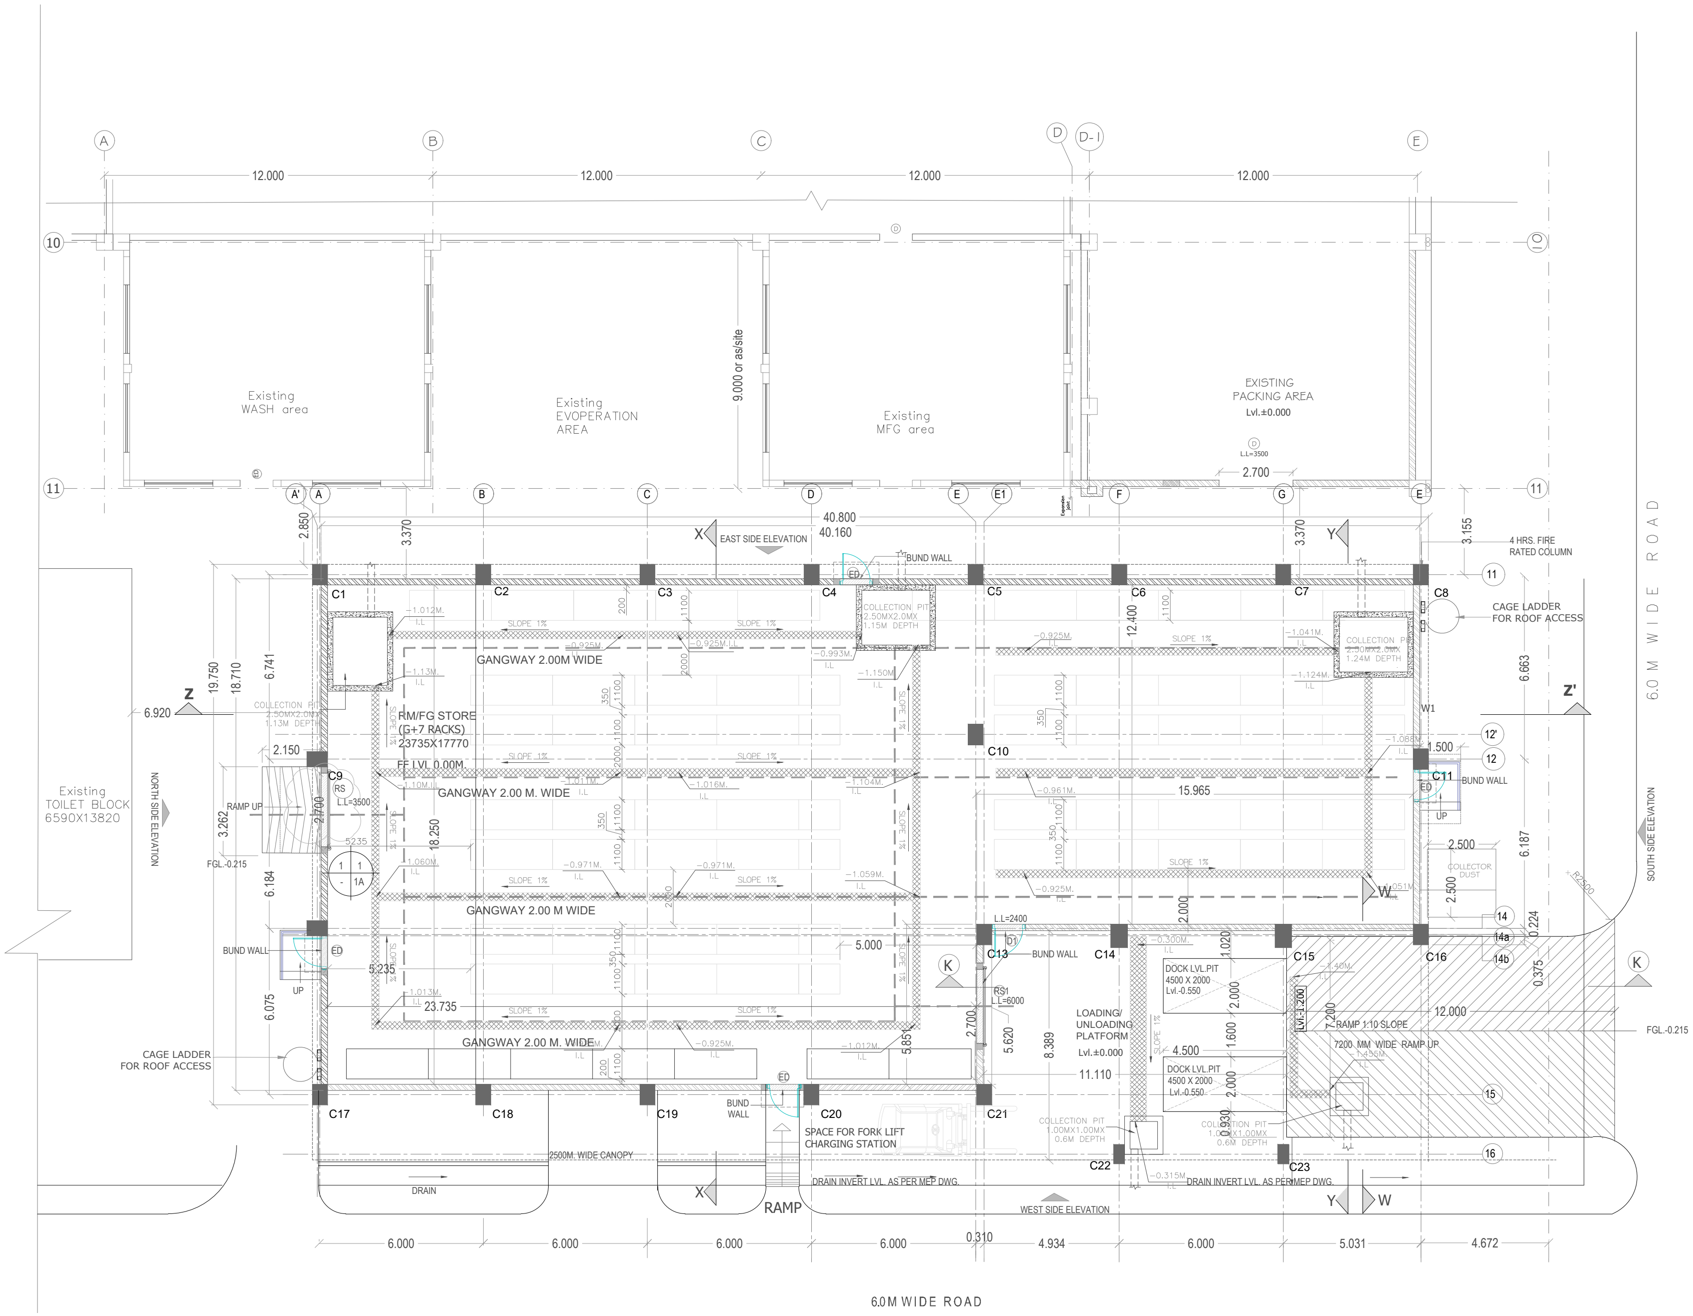
A
B
C
D
D-I
E
12.000
12.000
12.000
12.000
10
11
Existing
WASH area
Existing
EVOPERATION
AREA
9.000 or as/site
Existing
MFG area
EXISTING
PACKING AREA
Lvl.±0.000
L.L=3500
2.700
A'
A
B
C
D
E
E1
Expansion joint
F
G
E
2.850
3.370
40.800
40.160
X
EAST SIDE ELEVATION
BUND WALL
3.370
Y
3.155
4 HRS. FIRE
RATED COLUMN
C1
C2
C3
C4
C5
C6
C7
C8
COLLECTION PIT
2.50MX2.0MX
1.15M DEPTH
CAGE LADDER
FOR ROOF ACCESS
COLLECTION PIT
2.50MX2.0MX
1.24M DEPTH
GANGWAY 2.00M WIDE
SLOPE 1%
−1.012M. I.L
−0.925M. I.L
−0.993M. I.L
−1.150M I.L
−1.041M. I.L
−1.124M. I.L
−1.13M. I.L
19.750
18.710
6.741
12.400
6.663
Z
6.920
COLLECTION PIT
2.50MX2.0MX
1.13M DEPTH
RM/FG STORE
(G+7 RACKS)
23735X17770
FF LVL 0.00M.
C10
W1
Z'
6.0M WIDE ROAD
2.150
C9
RS
L.L=3500
RAMP UP
2.700
3.262
FGL.-0.215
NORTH SIDE ELEVATION
Existing
TOILET BLOCK
6590X13820
GANGWAY 2.00 M. WIDE
−1.10M.I.L
−1.011M. I.L
−1.016M. I.L
−1.104M. I.L
−1.088M. I.L
−0.961M. I.L
12'
1.500
12
C11
BUND WALL
ED
UP
15.965
5235
18.250
2.500
COLLECTOR DUST
6.187
SOUTH SIDE ELEVATION
R2500
1
1
-
1A
−1.060M. I.L
−0.971M. I.L
−1.059M. I.L
−0.925M. I.L
W
1.051M. I.L
2.500
6.184
GANGWAY 2.00 M WIDE
2.000
14
14a
14b
0.224
0.375
BUND WALL
ED
5.235
5.000
L.L=2400
D1
C13
BUND WALL
C14
C15
C16
K
K
−0.300M. I.L
DOCK LVL.PIT
4500 X 2000
Lvl.-0.550
1.020
−1.40M. I.L
UP
RS1
L.L=6000
LOADING/
UNLOADING
PLATFORM
Lvl.±0.000
6.075
−1.013M. I.L
23.735
2.700
5.620
8.389
Lvl.-1.200
7.200
RAMP 1:10 SLOPE
12.000
FGL.-0.215
4.500
1.600
7200 MM WIDE RAMP UP
−1.455M. I.L
GANGWAY 2.00 M. WIDE
−0.925M. I.L
−1.012M. I.L
5.851
11.110
2.000
CAGE LADDER
FOR ROOF ACCESS
200
1100
350
2000
ED
C17
C18
C19
BUND WALL
C20
C21
SPACE FOR FORK LIFT
CHARGING STATION
COLLECTION PIT
1.00MX1.00MX
0.6M DEPTH
C22
0.930
COLLECTION PIT
1.00MX1.00MX
0.6M DEPTH
C23
15
16
2500M. WIDE CANOPY
DRAIN
X
RAMP
DRAIN INVERT LVL. AS PER MEP DWG.
−0.315M. I.L
DRAIN INVERT LVL. AS PER MEP DWG.
WEST SIDE ELEVATION
Y
W
6.000
6.000
6.000
6.000
0.310
4.934
6.000
5.031
4.672
6.0M WIDE ROAD