
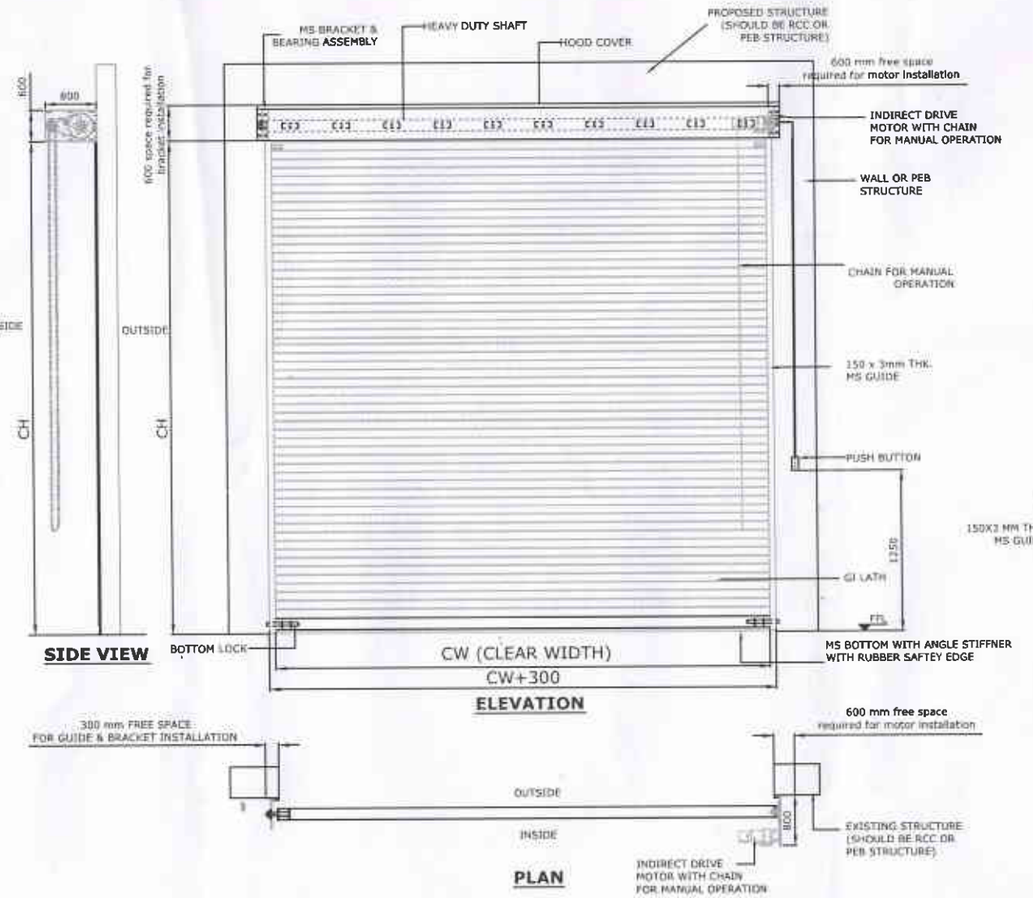


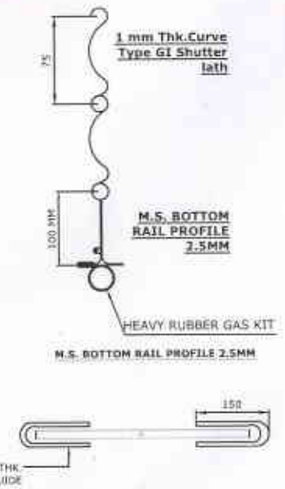

CLEAR WIDTH (CW)	CLEAR HEIGHT (CH)	QUANTITY
5000	5000	01 NOS

DIMENSION :

CLEAR WIDTH	CLEAR HEIGHT	QUANTITY
5000	5000	01 NOS

MATERIAL :

THICKNESS :

NOTE:
1.REQUIRED STRUCTURE FOR ROLLING SHUTTER WILL BE CLIENT'S SCOPE.
2.ONE COAT OF RED OXIDE PRIMER WILL BE GIVEN TO THE SHUTTER.
3.SINGLE PHASE. 3 CORE 1.5 SQ. CABLE REQUIRE AT SITE(CLIENT'S SCOPE).
4. FOR FINAL FINISH CLIENT SHOULD CONFIRM RAL COLOR SHADE.

NIHVA

NIHVA TECHNOLOGIES PVT. LTD. PUNE
Email:- info@nihva.com
Website:- www.nihva.com

NIHVA TECHNOLOGIES PVT. LTD.

TITLE:
MOTORIZED ROLLING SHUTTER

CLIENT'S APPROVAL :
Approved with Comments.

CLIENT : MAHINDRA SUSTEN

PROJECT :

SITE LOCATION : SAHARANPUR, U.P.

DWG. NO. : NIHVA/17-18/0217

SCALE: NTS	WT:	SHEET:1 OF 1
DRAWN BY: OMKAR		DATE: 27-09-2017
CHECKED BY : SHEKHAR		DATE: 27-09-2017
APPROVED BY : SHEKHAR		DATE: 27-09-2017

If any queries contact : projects@nihva.com


NOTE: ALL DIMENSIONS ARE IN mm

THIS DRAWING & DESIGN IS THE PROPERTY OF NIHVA TECHNOLOGIES. NOT TO BE SOLD OR COPIED TO ANY OTHER CONCERNS.

SEMAC CONSULTANTS PRIVATE LIMITED

① Map. Wind load / Resistance to be submitted.
② Shutter dimension to be as per GFC. drawing.

SEMAC CONSULTANTS PRIVATE LIMITED

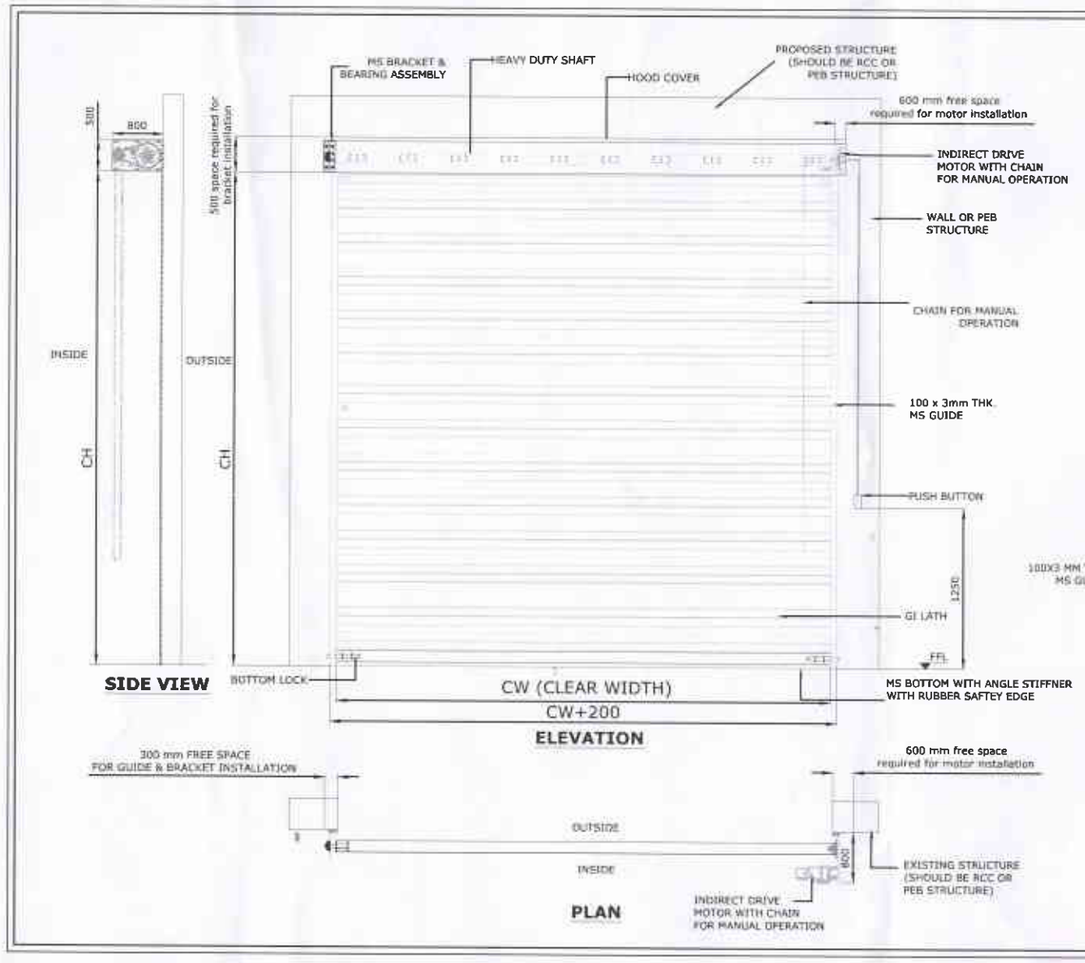

CLEAR WIDTH (CW)	CLEAR HEIGHT (CH)	QUANTITY
3000	3000	02 NOS
3000	4000	01 NOS
4000	4000	01 NOS

DIMENSION :

CLEAR WIDTH	CLEAR HEIGHT	QUANTITY
3000	3000	02 NOS
3000	4000	01 NOS
4000	4000	01 NOS

MATERIAL:

THICKNESS :

NOTE:
1.REQUIRED STRUCTURE FOR ROLLING SHUTTER WILL BE CLIENT'S SCOPE.
2.ONE COAT OF RED OXIDE PRIMER WILL BE GIVEN TO THE SHUTTER.
3.SINGLE PHASE. 3 CORE 1.5 SQ. CABLE REQUIRE AT SITE(CLIENT'S SCOPE).
4. FOR FINAL FINISH CLIENT SHOULD CONFIRM RAL COLOR SHADE.

NIHVA

NIHVA TECHNOLOGIES PVT. LTD.

NIHVA TECHNOLOGIES PVT. LTD. PUNE
Email:- info@nihva.com
Website:- www.nihva.com

TITLE:
MOTORIZED ROLLING SHUTTER

CLIENT'S APPROVAL :
Approved with comments

CLIENT - MAHINDRA SUSTEN

PROJECT -

SITE LOCATION - SAHARANPUR, U.P.

DWG. NO. : NIHVA/17-18/0216

SCALE: NTS	WT:	SHEET:1 OF 1
DRAWN BY: OMKAR		DATE: 27-09-2017
CHECKED BY : SHEKHAR		DATE: 27-09-2017
APPROVED BY : SHEKHAR		DATE: 27-09-2017

If any queries contact : projects@nihva.com


NOTE: ALL DIMENSIONS ARE IN mm

THIS DRAWING & DESIGN IS THE PROPERTY OF NIHVA TECHNOLOGIES. NOT TO BE SOLD OR COPIED TO ANY OTHER CONCERN.


(1) *Max wind load / wind resistance to be submitted.

(2) Shutter dimension to be as per our GFC drawing.


OPTION 1

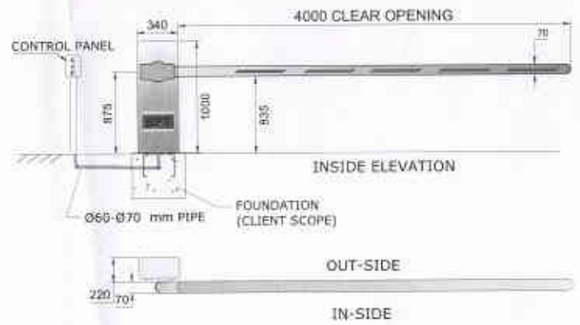


OPTION 2

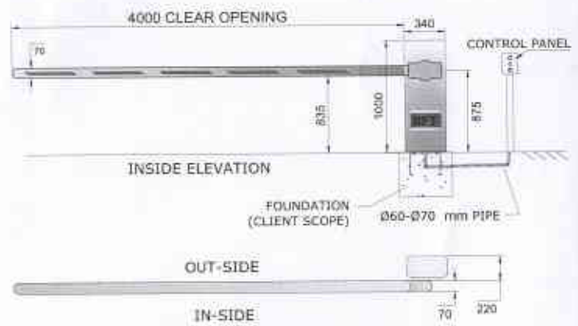


OPTION 3

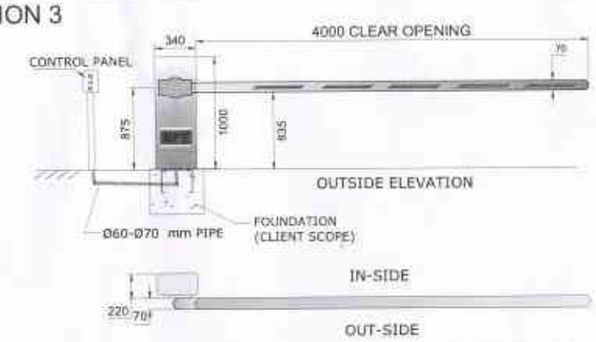

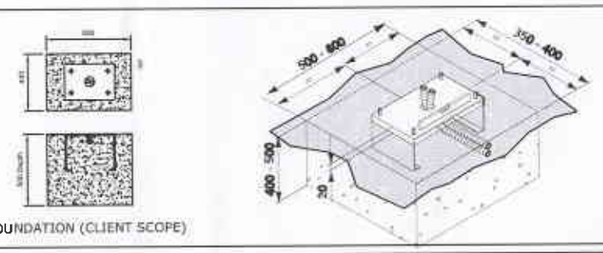

FOUNDATION (CLIENT SCOPE)

OPTION 4

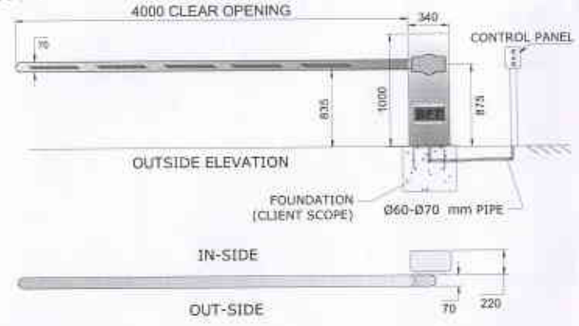


NOTE- CLIENT SHOULD SELECT POSITION OF BOOM BARRIER OUT OF OPTIONS.

This drawing & design is the property of NIHVA TECHNOLOGIES. Not to be sold or copied to any other concern.


TITLE	BOOM BARRIER		NIHVA TECHNOLOGIES PVT. LTD.
	SIGN	DATE	
DRAWN	SURAJ	27/09/2017	CLIENT -MAHINDRA SUSTEN
CHECK	SHEKHAR	27/09/2017	PROJECT -
REV.			SITE LOCATION -SAHARANPUR, U.P
APPROVAL	SHEKHAR	27/09/2017	DWG. NO. : NIHVA/17-18/0214
If any queries contact : projects@nihva.com			SCALE: NTS / WT: / SHEET: 01 OF 01
ALL DIMENSION ARE in mm			

NIHVA TECHNOLOGIES PVT. LTD. PUNE
Tel : 020 66304033
Email:- info@nihva.com
Website:- www.nihva.com


OPTION 1

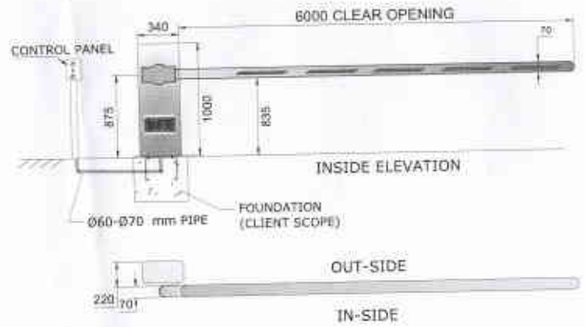


OPTION 2

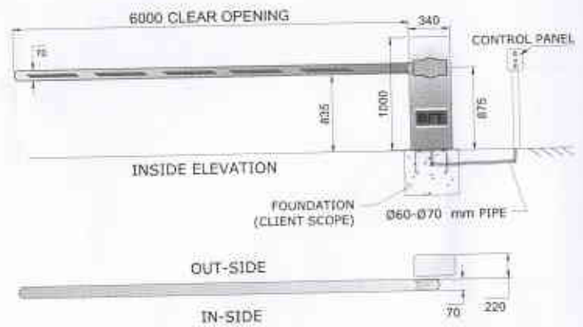


OPTION 3

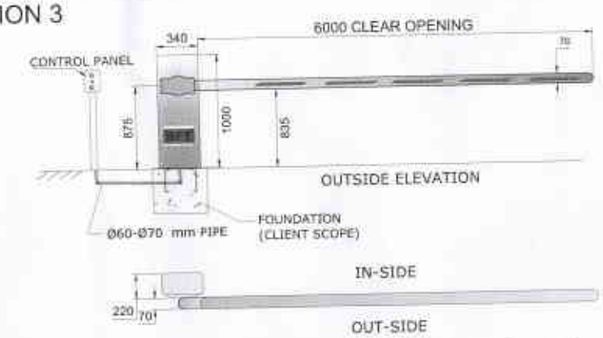

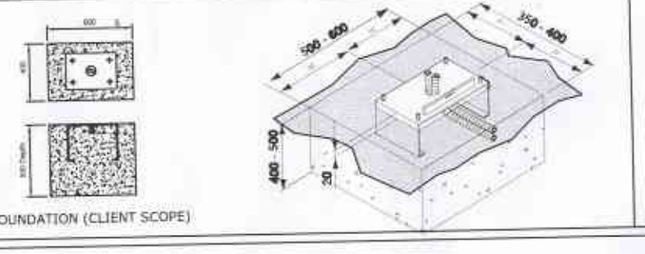

FOUNDATION (CLIENT SCOPE)

OPTION 4

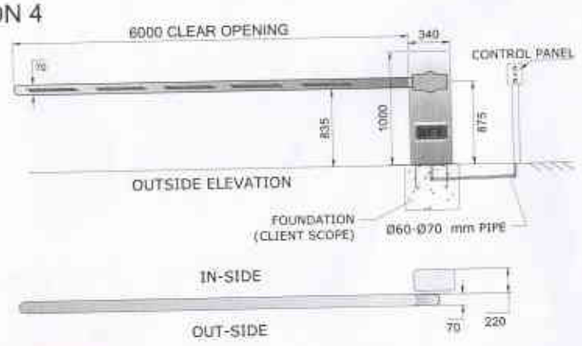

Approved

NOTE- CLIENT SHOULD SELECT POSITION OF BOOM BARRIER OUT OF OPTIONS.

This drawing & design is the property of NIHVA TECHNOLOGIES. Not to be sold or copied to any other concern.

TITLE: BOOM BARRIER			NIHVA TECHNOLOGIES PVT. LTD.
	SIGN	DATE	
DRAWN	SURAJ	27/09/2017	CLIENT :-MAHINDRA SUSTEN
CHECK	SHEKHAR	27/09/2017	PROJECT :-
REV.			SITE LOCATION :-SAHARANPUR, U.P
APPROVAL	SHEKHAR	27/09/2017	DWG. NO. : NIHVA/17-18/0215
If any queries contact : projects@nihva.com			SCALE: NTS | WT. | SHEET: 01 OF 01
ALL DIMENSION ARE IN mm			

NIHVA TECHNOLOGIES PVT. LTD. PUNE
Tel : 020 66304033
Email:- info@nihva.com
Website:- www.nihva.com