


This drawing is the Property of Larsen & Toubro Limited, ECC Construction Group and must not be passed on to any third person or firm not authorised by us, nor be copied / made use of in full or part by such person or firm without our prior permission in writing.

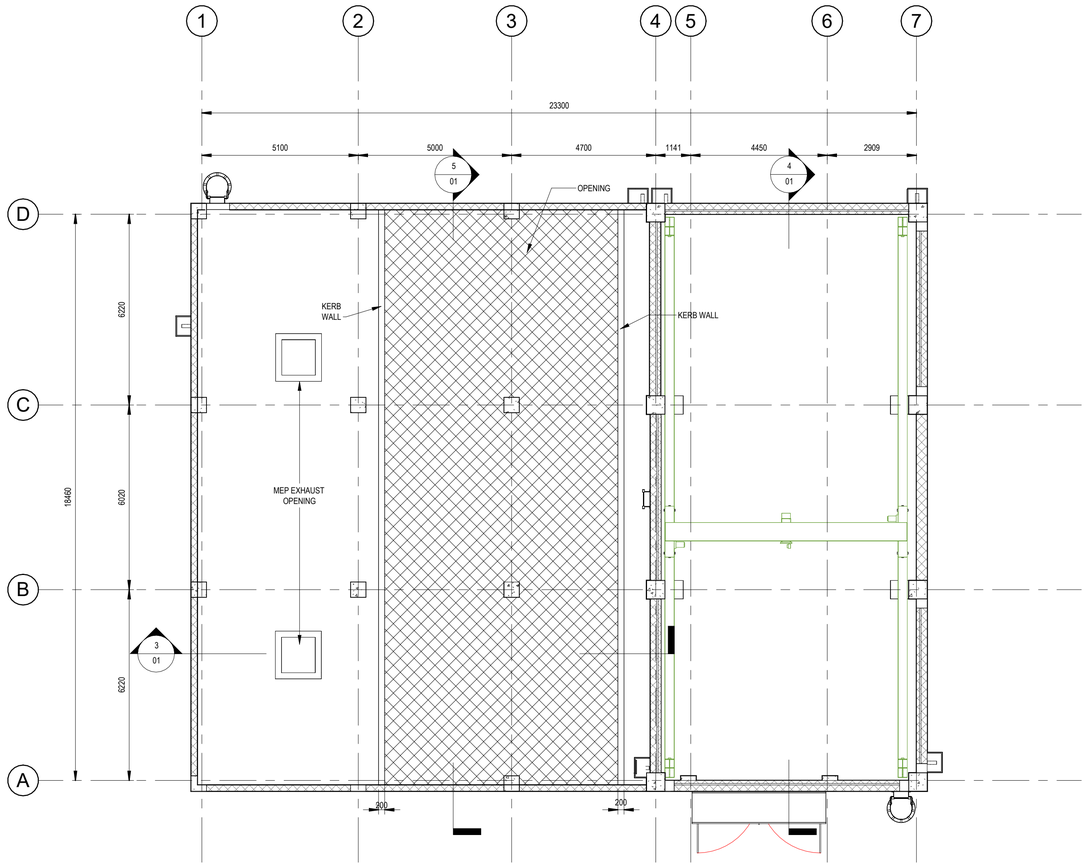


1 / 01 ROOF PLAN @+7.950M
SCALE 1 : 100

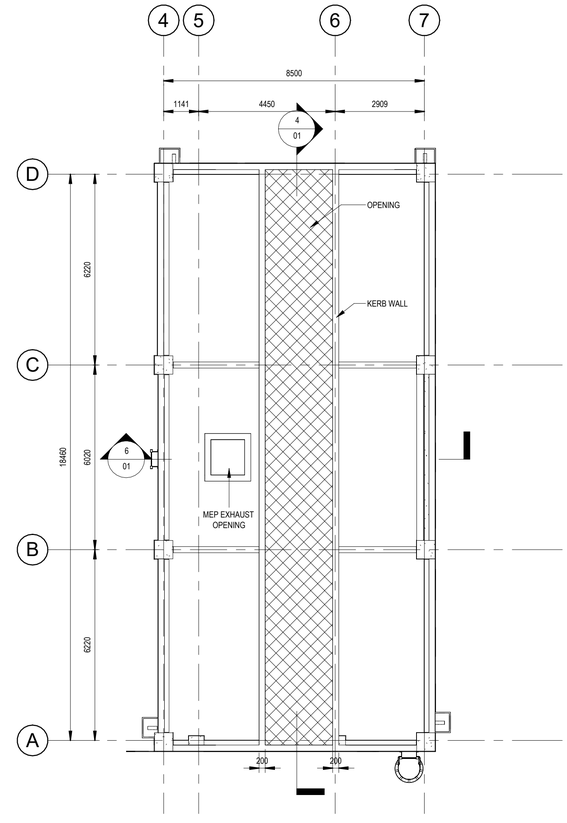


2 / 01 ROOF PLAN @+10.17MM
SCALE 1 : 100

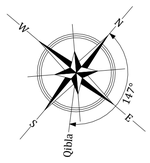


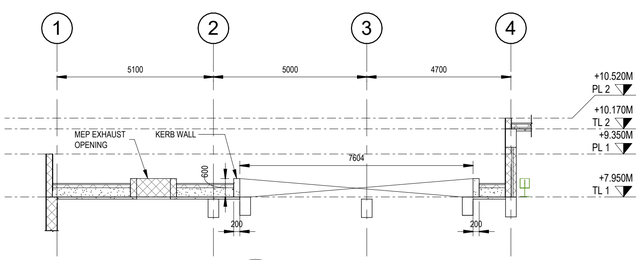


3 / 01 Section 3
SCALE 1 : 100

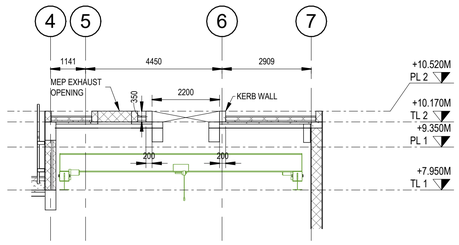


6 / 01 Section 6
SCALE 1 : 100

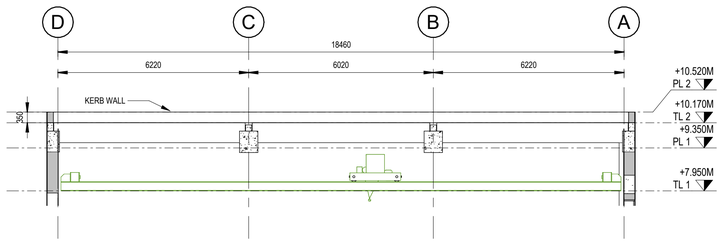

4 / 01 Section 4
SCALE 1 : 100

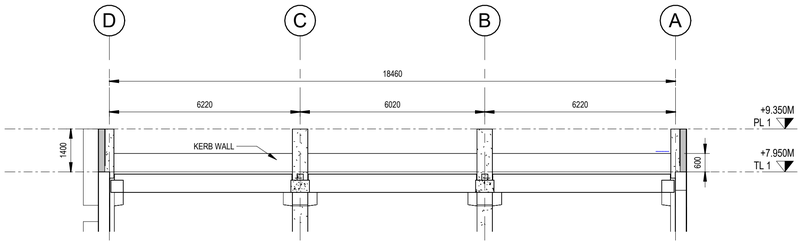

5 / 01 Section 5
SCALE 1 : 100

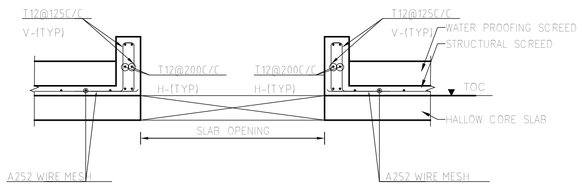

7 / 01 TYP. KERB WALL DETAIL FOR OPENING
SCALE 1 : 25

0 2m 4m 6m 8m 10m
SCALE 1:100

GRAPHIC SCALE

LEGEND

- HANDLING EQUIPMENT CIRCULATION
- STAFF CIRCULATION AREA
- W1 & W2 - WINDOW
- EF - EXHAUST FAN
- COLUMN TERMINATED BELOW AT ROOF SLAB
- dl - START TILE
- HW - HARD WARE
- CHECKERED PLATE
- GRATING
- TECHNICAL FLOOR
- INDICATED SURFACE ELEVATION AS PER MSL (MEAN SEA LEVEL)

RCP - REFLECTED CEILING PLAN
FGL - FINISHED GROUND LEVEL
NTS - NOT TO SCALE
FFL - FINISHED FLOOR LEVEL
UFL - UNFINISHED FLOOR LEVEL
TYP - TYPICAL
BOL - BOTTOM OF LINTEL
TORS - TOP OF ROOF SLAB
RS - ROLLING SHUTTER
TL - TERRACE LEVEL
LVL - LEVEL
PB - PRECAST BLOCK FOR PIPE SUPPORT

℄ - CENTER LINE
RPL - RAISED PLATFORM LEVEL
FRL - FINISH ROOF LEVEL
TOP - TOP OF PARAPET
FCL - FINISHED CEILING LEVEL FROM FFL
- COLUMN
- GRID LINE
D1,D2 & D3 - DOOR
RWDP - RAIN WATER DRAIN PIPE
TOC - TOP OF CONCRETE
daN - DECANEWTON

(+24.30) AS PER MSL (MEAN SEA LEVEL)

REFERENCE DRAWINGS

TITLE	DRAWING NO.
LAYOUT FOR INTAKE	1RI11074-074B01-LNT-03-RO-DWG-WF-11344
SWRO INTAKE PUMP HOUSE - RC DETAILS	1RI11074-074B01-LNT-03-RO-DWG-CI-10206
HVAC LAYOUT FOR SWRO INTAKE PUMP HOUSE	1RI11074-074B01-LNT-03-RO-DWG-ME-07511
OUTDOOR LIGHTING LAYOUT FOR INTAKE PUMP HOUSE	1RI11074-074B01-LNT-03-RO-DWG-EL-10744
CABLE ROUTING LAYOUT FOR SEAWATER INTAKE PUMPS AND SEAWATER SCREENING (SV RO)	1RI11074-074B01-LNT-03-RO-DWG-EL-10621
ASSEMBLY DRAWING FOR SEAWATER INTAKE PUMPS AND SEAWATER SCREENING (SWRO PACKAGE)	1RI11074-074B01-LNT-03-RO-DWG-ME-10220
CIVIL GUIDE DRAWING FOR SEAWATER INTAKE PUMPS AND SEAWATER SCREENING (SWRO PACKAGE)	1RI11074-074B01-LNT-03-RO-DWG-ME-10253
PAINTING COLOR PALLETE FOR ENERGY AND WATER	1RI11074-074B01-LNT-01-GE-SPC-CI-02900
FIRE FIGHTING OVERALL LAYOUT FOR INTAKE PUMPING STATION & SWRO PLANT - SV	1RI11074-074B01-LNT-03-RO-DWG-ME-07589

وزارة الشـــؤون البلدية والقروية
Ministry of Municipal & Rural Affairs

أمانة منطقة تبوك
Municipality Of Tabuk

Off-taker
AMAALA

Project Company
Amaala Sustainable
• COMPANY FOR ENERGY •

Stamp الختم Signature التوقيع

Owner's Consultant
FICHTNER
Consulting Engineers Limited

Stamp الختم Signature التوقيع

Contractor
لارسن أند تبرو ليمتد
LARSEN & TOUBRO LIMITED

Stamp الختم Signature التوقيع

Key Plan

General Notes:

1. ALL DIMENSIONS ARE IN MILLIMETERS & LEVELS ARE IN METERS.
2. ALL ARCHITECTURAL WORKS SHALL BE CARRIED OUT IN CONJUNCTION WITH THE CONTRACT TERMS AND CONDITIONS, TECHNICAL SPECIFICATION AND SCHEDULE OF ITEMS. ANY DIFFERENCE SHALL BE BROUGHT TO THE NOTICE OF ENGINEER-IN-CHARGE.
3. THIS DRAWING IS TO BE READ IN CONJUNCTION WITH THE RELEVANT STRUCTURAL, MECHANICAL AND ELECTRICAL DRAWINGS.
4. WALL OPENINGS SHALL BE VERIFIED WITH RELEVANT APPROVED MECHANICAL, ELECTRICAL, STRUCTURAL AND FIRE-FIGHTING DRAWINGS.
5. HVAC CUT-OUT AND DUCT DETAILS SHALL BE SUBMITTED AS SEPARATE DRAWING.
6. MINOR ADJUSTMENT MAY BE DONE AT SITE IN CONSULTATION WITH ENGINEER IN CHARGE.
7. TOILET / PANTRY / STAIRCASE / RAMP DETAILS TO BE PROVIDED IN A SEPERATE SHEET.
8. THE CONTRACTOR SHALL VERIFY ALL DIMENSIONS, ELEVATIONS, ANGLES AND EXISTING CONDITIONS BEFORE PROCEEDING WITH ANY WORK. PROCEEDING WITH THE WORK, IT IS THE CONTRACTOR'S RESPONSIBILITY TO FOLLOW ALL APPLICABLE SAFETY CODES AND REGULATIONS DURING ALL PHASES OF CONSTRUCTION.
09. TRUE NORTH TO BE CHECKED AT SITE BEFORE STARTING OF WORK.
10. MATERIALS, FINISHES, AND PRECAST DETAILS ARE SUBJECT TO DETAIL IN SHOP DRAWINGS, REQUIRED CONSULTANT'S APPROVAL BEFORE CONSTRUCTION.
11. THE FINAL FGL VALUE SHOULD BE REFERRED WITH SITE GRADING PLAN .
12. REGARDING THE DETAILS OF STRUCTURAL MEMBER PLEASE REFER STRUCTURAL DRAWINGS.
13. DOOR JAMBS ARE 100MM WIDE (TYPICAL) UNLESS OTHERWISE MENTIONED.
14. PLEASE REFER THE ARCHITECTURAL GENERAL NOTES FOR CONTRACTORS SPECIFICATION FOR ALL MATERIALS, FINISHES, CONSTRUCTION METHOD AND PROCESS.
15. THE COORDINATE SYSTEM USED FOR THIS PROJECT LOCATION IS KSA-GRF 17/ UTM ZONE 37N.
16. ALL LEVELS ARE REFERED TO=mMSL
17. HORIZONTAL DATUM IS BASED ON KSA-GRF17 UTM ZONE 37N.

Rev.	Reason For Issue	Date
C0	ISSUED FOR INFROMATION	30-01-2026

Project
AMAALA UTILITES PPP PROJECT

Building Name
INTAKE ELECTRICAL BUILDING

Plot Number

Drawing Title
ROOF WATER PROOFING DETAILS FOR BUILDINGS

Model File Reference
1RI11074-074B01-EFR-03-RO-MOD-AR-10261

Drawn By	Checked By	Approved By
MGN	RB	AK

Project No.	Issue Date	Sheet Size	Scale
1RI11074	30-01-2026	A1	1:100

Project Co. Drawing No:
1RI11074-074B01-EFR-03-RO-DWG-CI-10286

EPC Drawing No: Revision 00 Sheet No 02 of 02
1RI11074-074B01-LNT-03-RO-DWG-CI-10286