


FOR 1 PANEL	
B3	4.2 MTR
B4	13.8 MTR

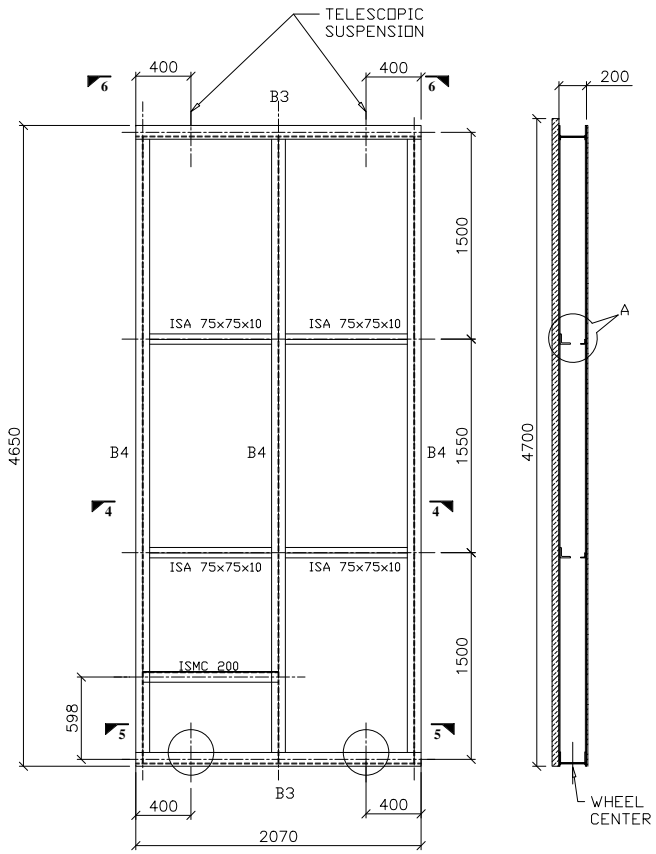


ELEVATION OF DOOR
(SCALE 1:1)

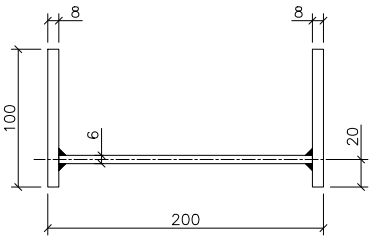


DETAIL OF B-3
(SCALE 1:10)

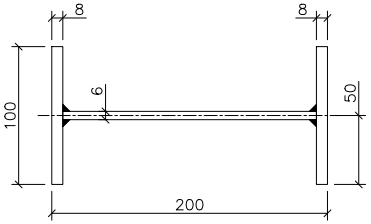


DETAIL OF B-4
(SCALE 1:10)

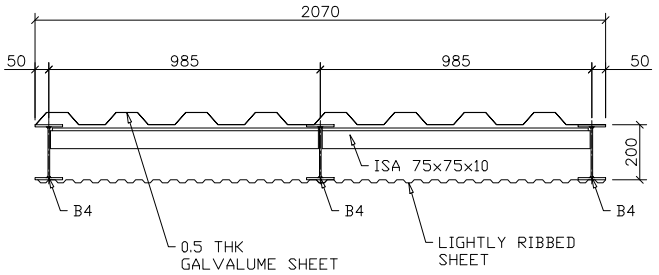


VIEW 4-4
(SCALE 1:2)

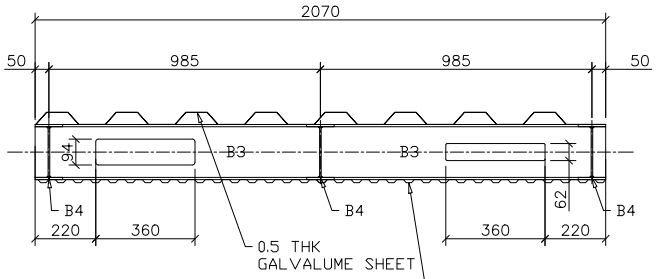

VIEW 5-5
(SCALE 1:2)

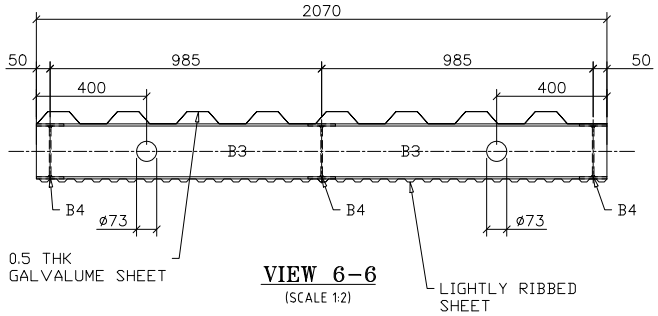

VIEW 6-6
(SCALE 1:2)

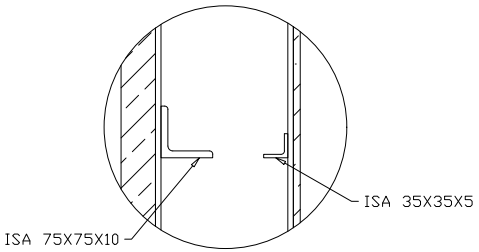

DETAIL OF 'A'
(SCALE 1:5)

PROJECT :- V-TECH, PUNE(5MX20M)

DOOR PANEL ELEVATION (DRIVING)
4650MM X 2070MM X 200MM THK

	SIGN	DATE
DGN		
DRN	VIKRANT	13-10-2023
CHD		
TRD		
APPD		

SCALE - 1:1

ALL DIMENSIONS ARE IN MM, UNLESS OTHERWISE SPECIFED.

SIZE A4 | MATL - -

REV 1 | QTY - 2

KUNTALBIJ ENGINEERS PVT LTD
ANDHERI (W), MUMBAI - 400 053

DRG NO.
HD-VP-A-004