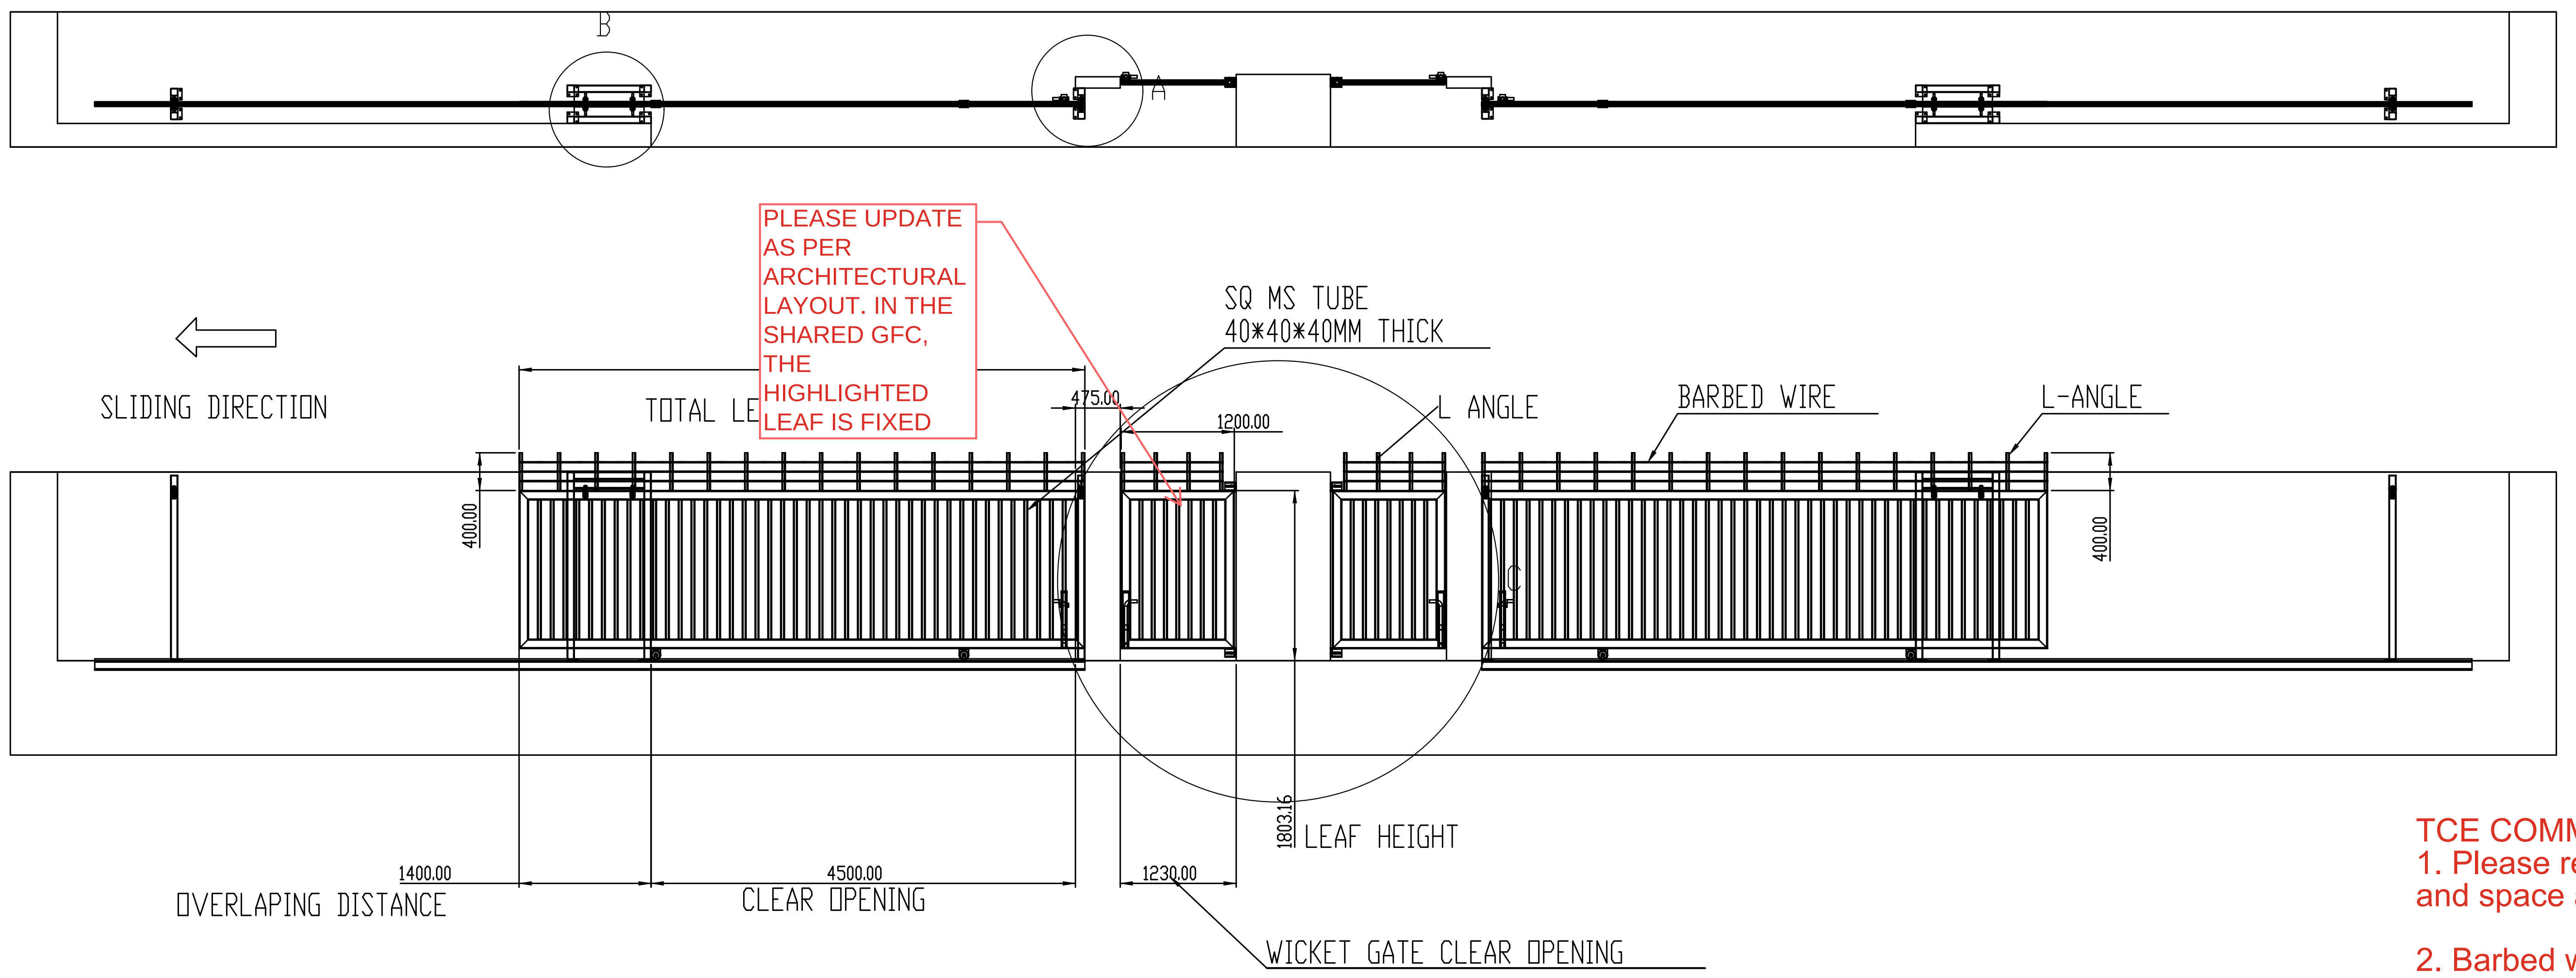

PLEASE UPDATE AS PER ARCHITECTURAL LAYOUT. IN THE SHARED GFC, THE HIGHLIGHTED LEAF IS FIXED

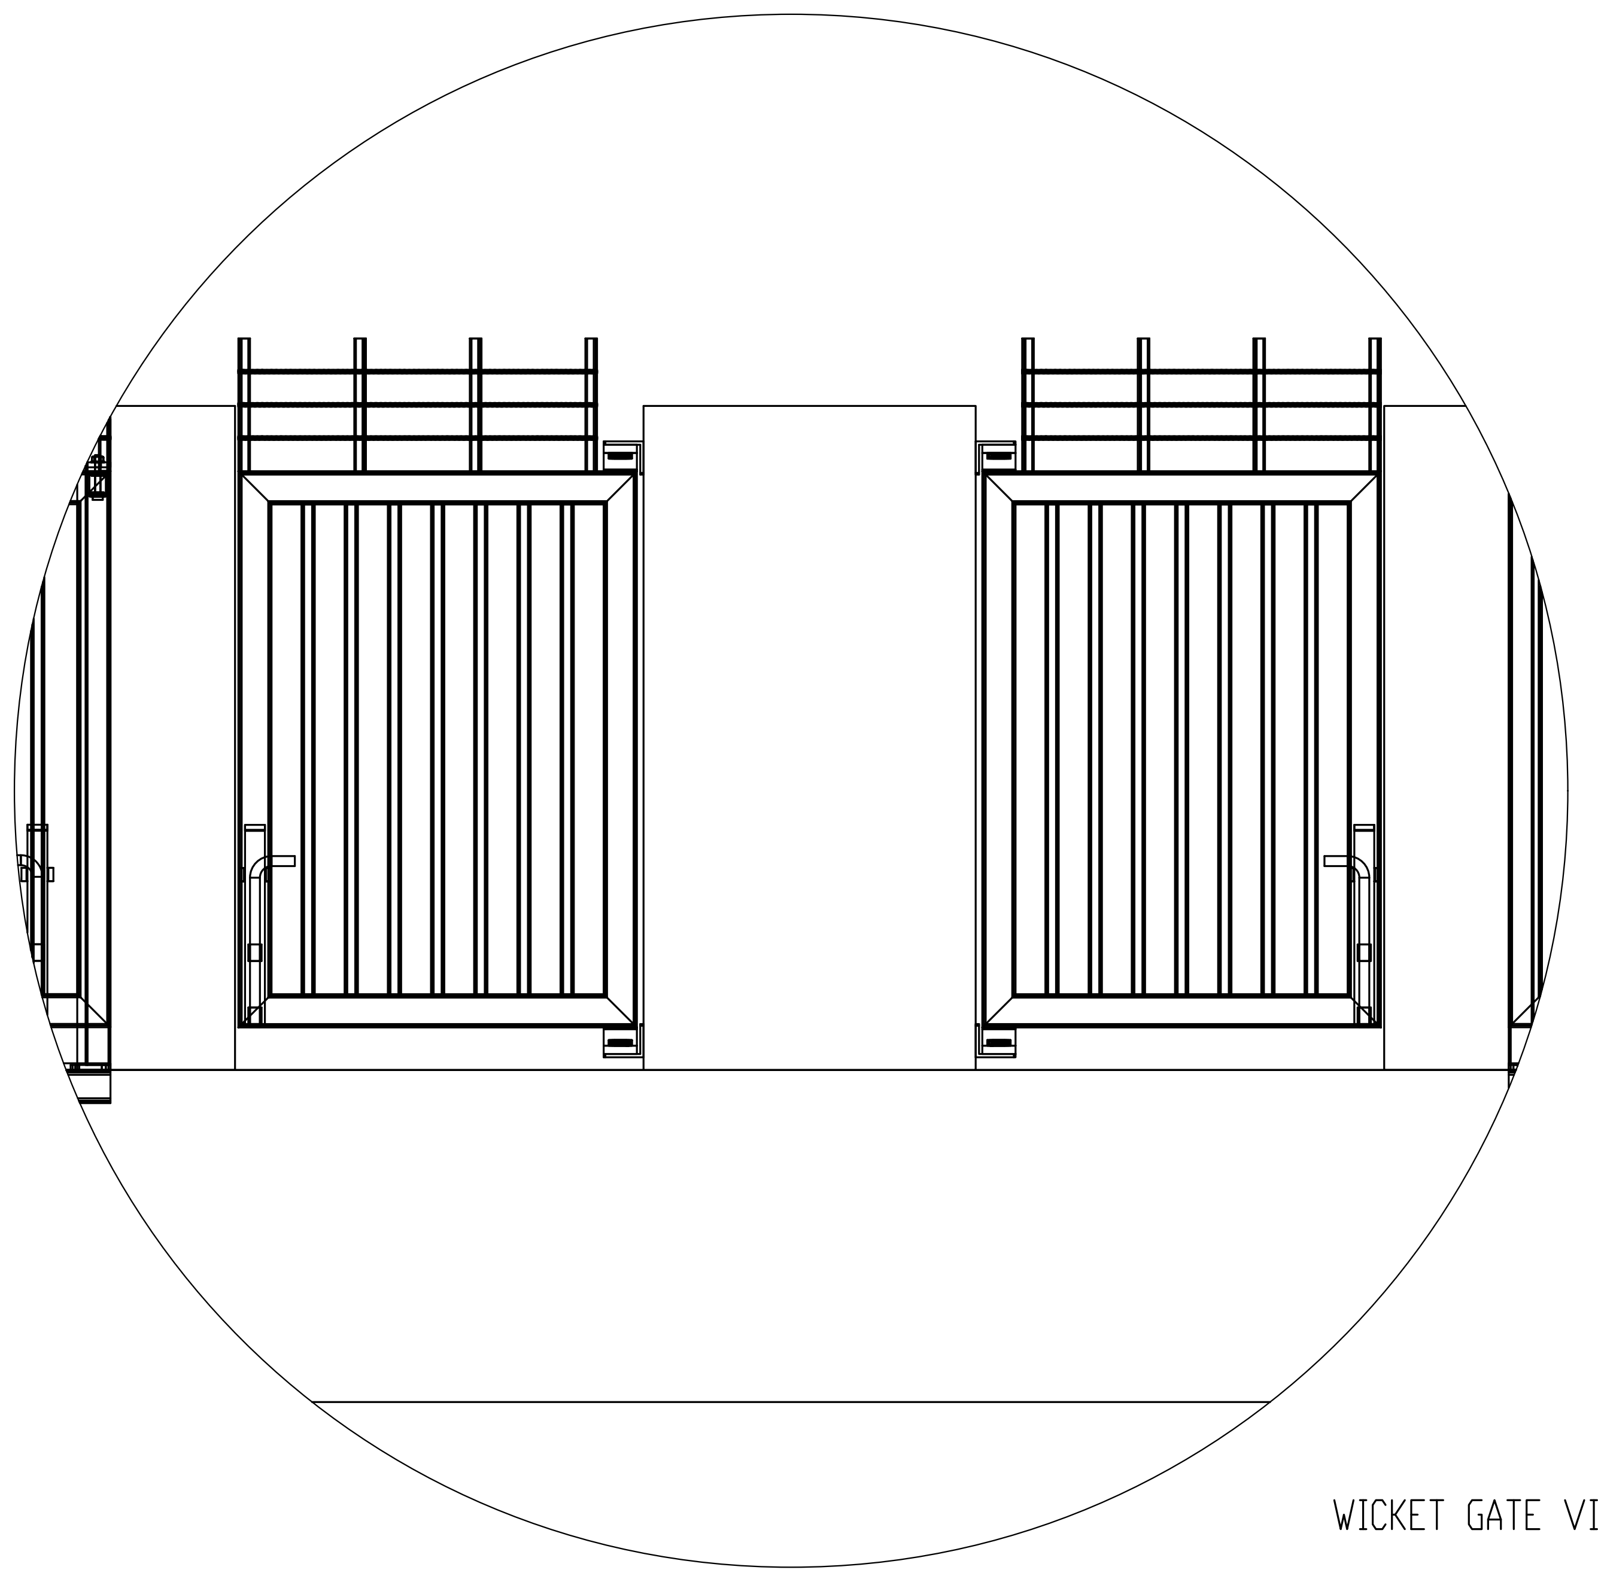

WICKET GATE VIEW

DETAIL C
SCALE 1 : 15

TCE COMMENTS :
1. Please refer to the latest master layout for the exact site dimensions and space availability.

2. Barbed wire fencing above the sliding gate is under finalization with the Air India team. TCE will confirm shortly.

3. Please specify whether the elevation view is from the inside or outside. It is currently unclear.

4. As the door sizes are as per the requirement, kindly consider the weight and design the sections accordingly.
Also, the wheel should be a double wheel, as shown in the architectural layout.
Locking arrangement details are missing from the GA drawing.
5. Kindly update as per the architectural layout: Sliding Gate Type 04 is to be shown without barbed wire fencing.

2B	**Reviewed. Comments enclosed. Incorporate the comments and re-submit for review.**

Anuja Raje
Digitally signed by Anuja Raje
Date: 2025.05.16 11:27:20 +05'30'

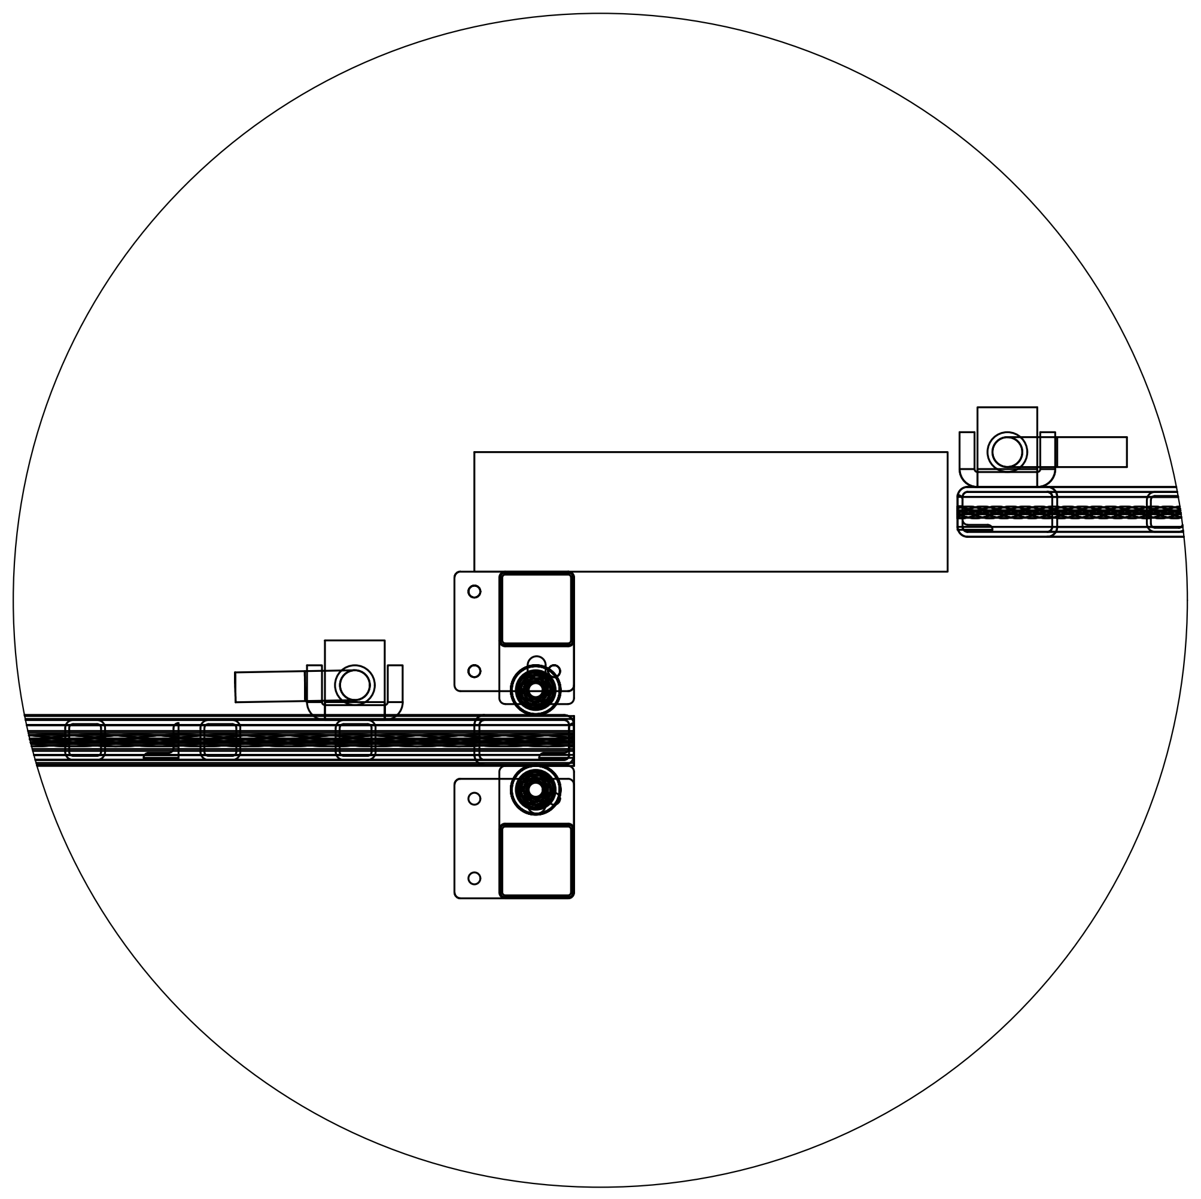

POST 1 AND NYLON
BEARING ASSEM.

DETAIL A
SCALE 1 : 5

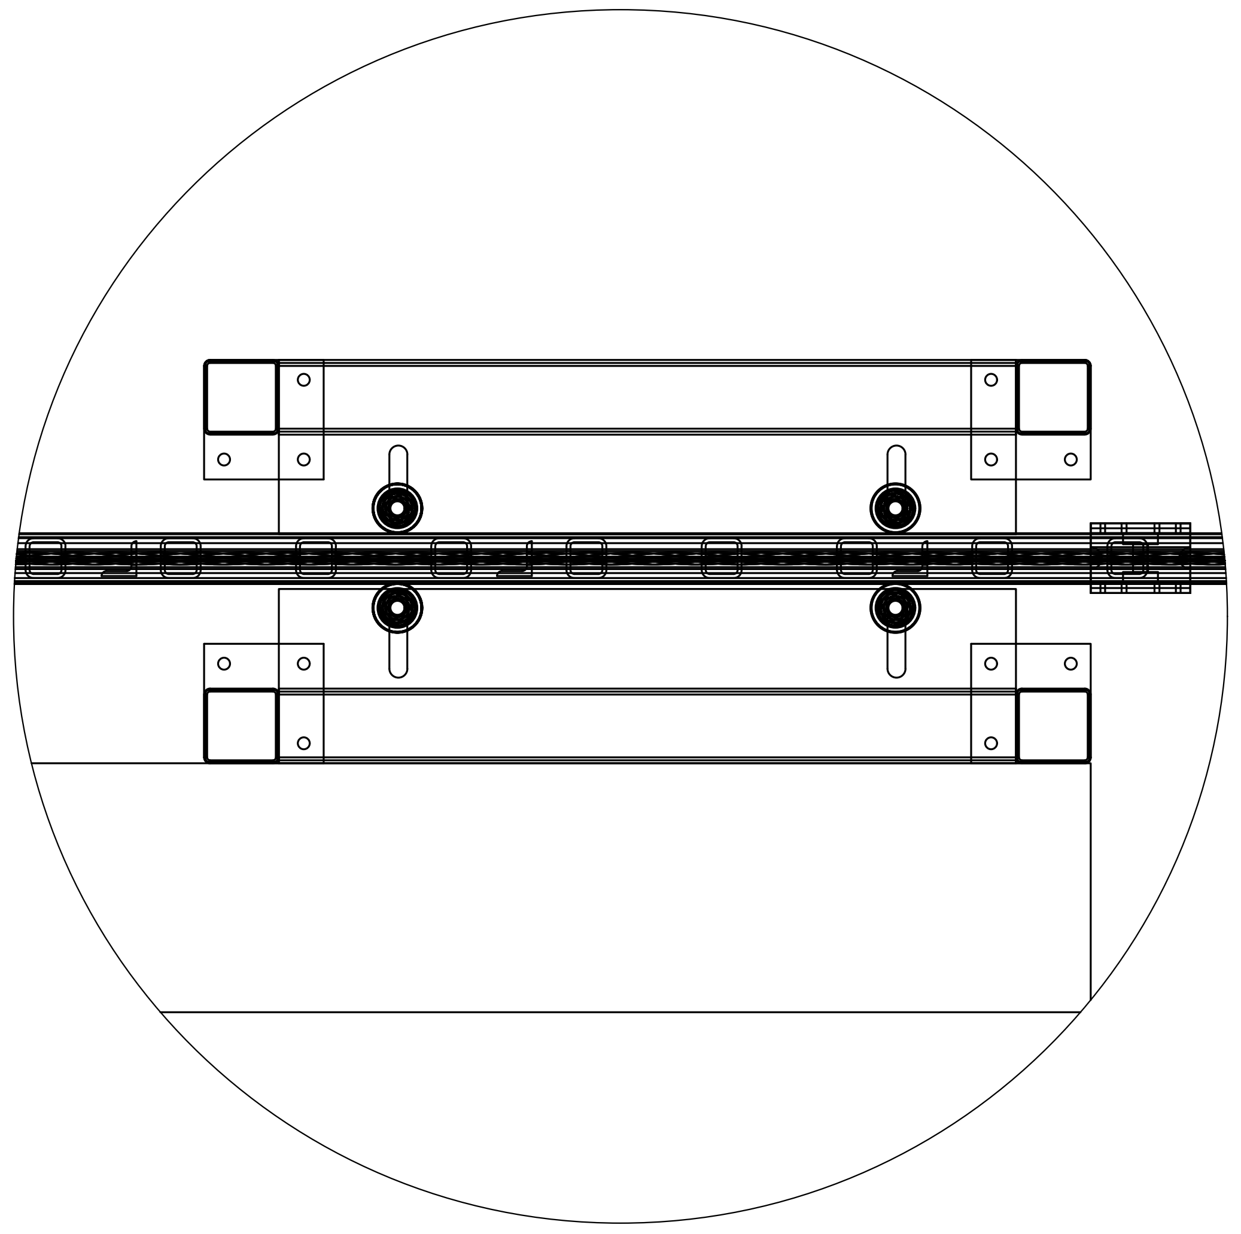

POST 2 AND NYLON
BEARING ASSEM.

DETAIL B
SCALE 1 : 5

UNLESS OTHERWISE SPECIFIED: DIMENSIONS ARE IN MILLIMETERS SURFACE FINISH: TOLERANCES: LINEAR: ANGULAR:			FINISH:		DEBURR AND BREAK SHARP EDGES	NIHVA NIHVA Technologies Pvt. Ltd.
	NAME	SIGNATURE	DATE			TITLE: GA. WIERFRAME DRAWING
DRAWN						
CHK'D						
APPV'D						
MFG						
Q.A				MATERIAL:		DWG NO. A0
				WEIGHT:		SCALE:1:100 SHEET 1 OF 1