




SIDE VIEW

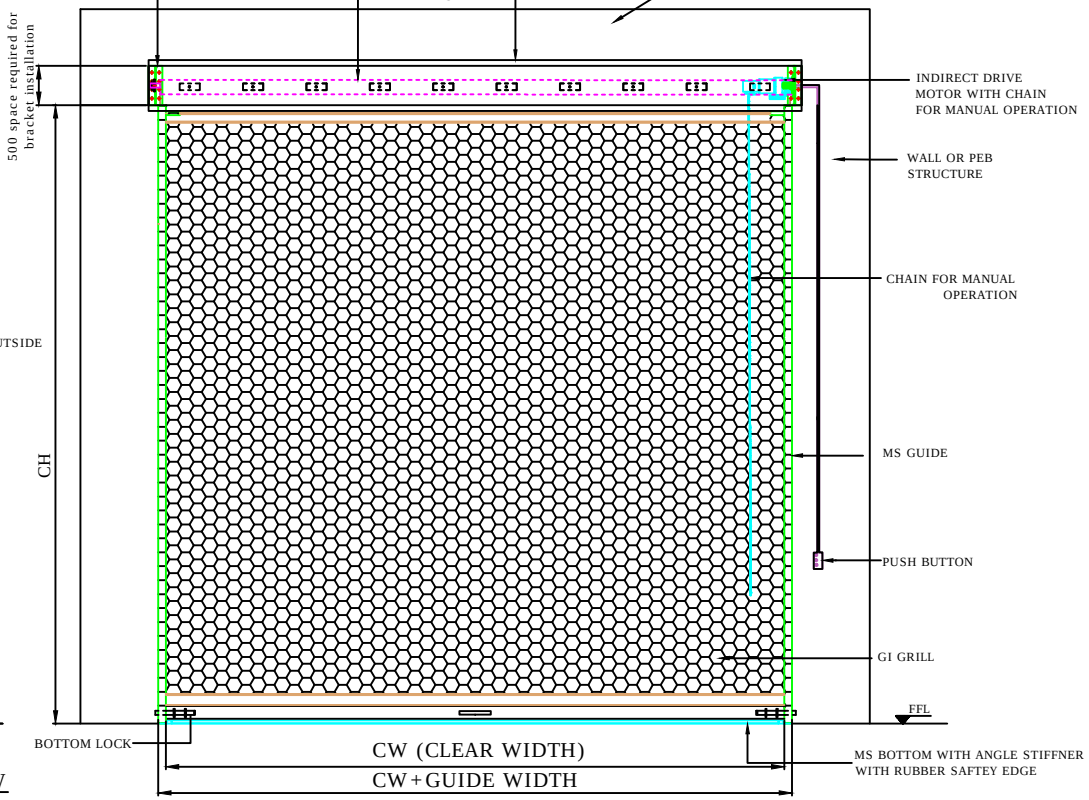


ELEVATION

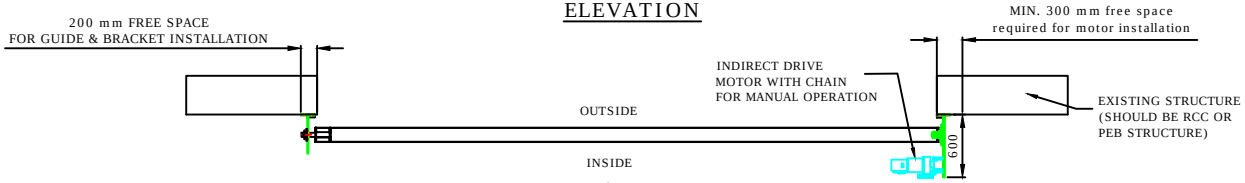



PLAN





75X2.5 MM THK. MS GUIDE

UPTO 5m WIDTH OF SHUTTER

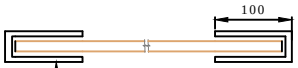



100X3 MM THK. MS GUIDE


ABOVE 5m WIDTH OF SHUTTER

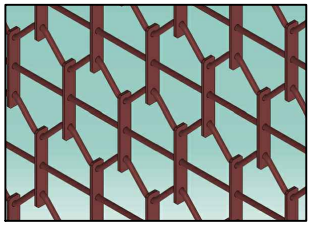


GI GRILL

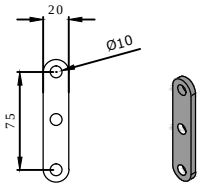


5mm THK. LINK

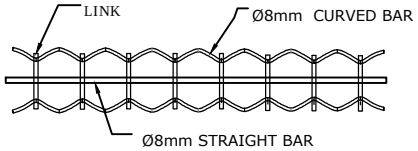

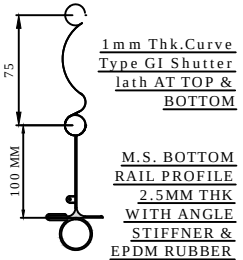
1mm Thk.Curve Type GI Shutter lath AT TOP & BOTTOM

M.S. BOTTOM RAIL PROFILE 2.5MM THK WITH ANGLE STIFFNER & EPDM RUBBER

| DIMENSION : | | |
|---|---|---|
| CLEAR WIDTH | CLEAR HEIGHT | QUANTITY |
| | | |

MATERIAL :

THICKNESS :

NIHVA TECHNOLOGIES PVT. LTD. PUNE
Email:- info@nihva.com
Website:- www.nihva.com

TITLE:

G.A. MOTORIZED GRILLED ROLLING SHUTTER

CLIENT'S APPROVAL :

CLIENT - ADANI

PROJECT - WESTERN HEIGHTS PROJECT

SITE LOCATION - MUMBAI

DWG. NO. : NIHVA/16-17/170/R01

| SCALE: NTS | WT: | SHEET:1 OF 1 |
|---|---|---|
| DRAWN BY: OMKAR | | DATE: 10-03-2017 |
| CHECK : SAGAR P. | | DATE: 10-03-2017 |
| APPROVED : R.K. | | DATE: 10-03-2017 |

If any queries contact : projects@nihva.com

NOTE: ALL DIMENSIONS ARE IN mm

THIS DRAWING & DESIGN IS THE PROPERTY OF NIHVA TECHNOLOGIES. NOT TO BE SOLD OR COPY TO ANY OTHER CONCERN.