
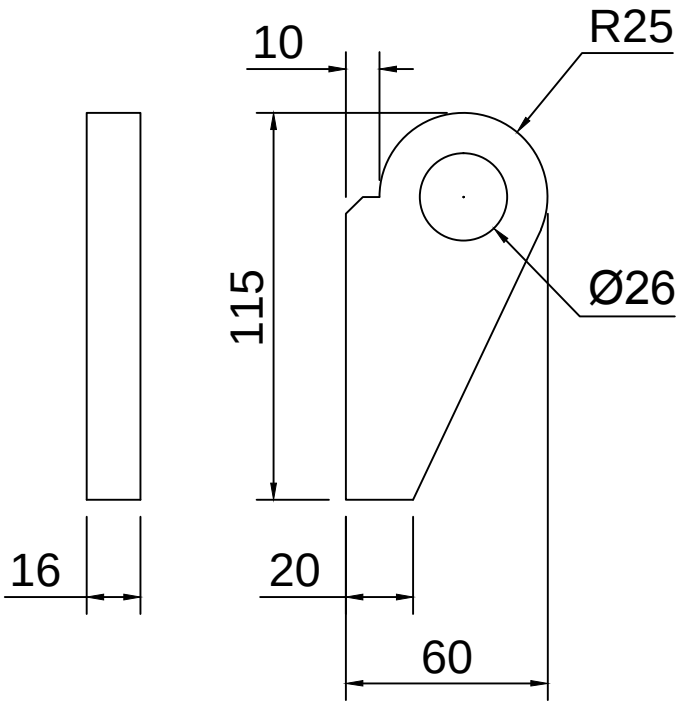


M.S PROFILE
60 X 16 X 115L = 12 NOS

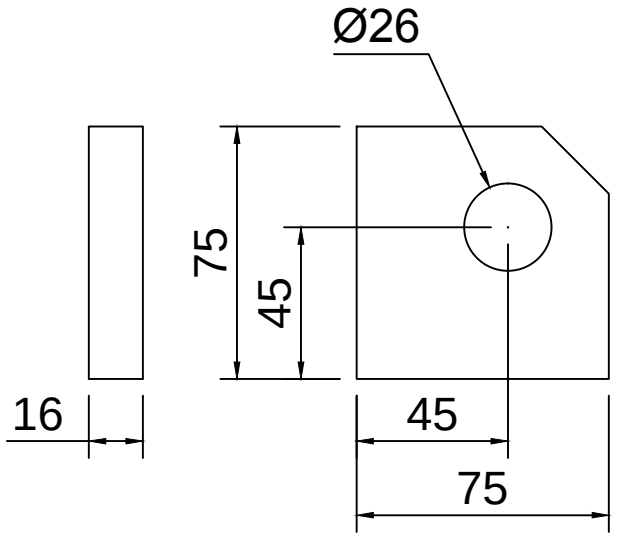

M.S PROFILE
75 X 16 X 75L = 4 NOS

This drawing & design is the property of NIHVA TECHNOLOGIES. Not to be sold or copied to any other concern.

TITLE: PROFILE PLATES				NIHVA TECHNOLOGIES PVT. LTD. PUNE Tel : 020 66304033 Email:- info@nihva.com Website:- www.nihva.com	
	NAME	SIGN	DATE		
DRAWN	P.A		22.10.2019	CLIENT -	
CHECK	G.J		22.10.2019	PROJECT -	
APPRD.				SITE LOCATION -	
If any queries contact : design@nihva.com				DWG. NO. :NIHVA/19-20/VDR/195	REV- R00
ALL DIMENSION ARE IN mm				SCALE: NTS	WT: SHEET: 01 OF 01