



ELEVATION

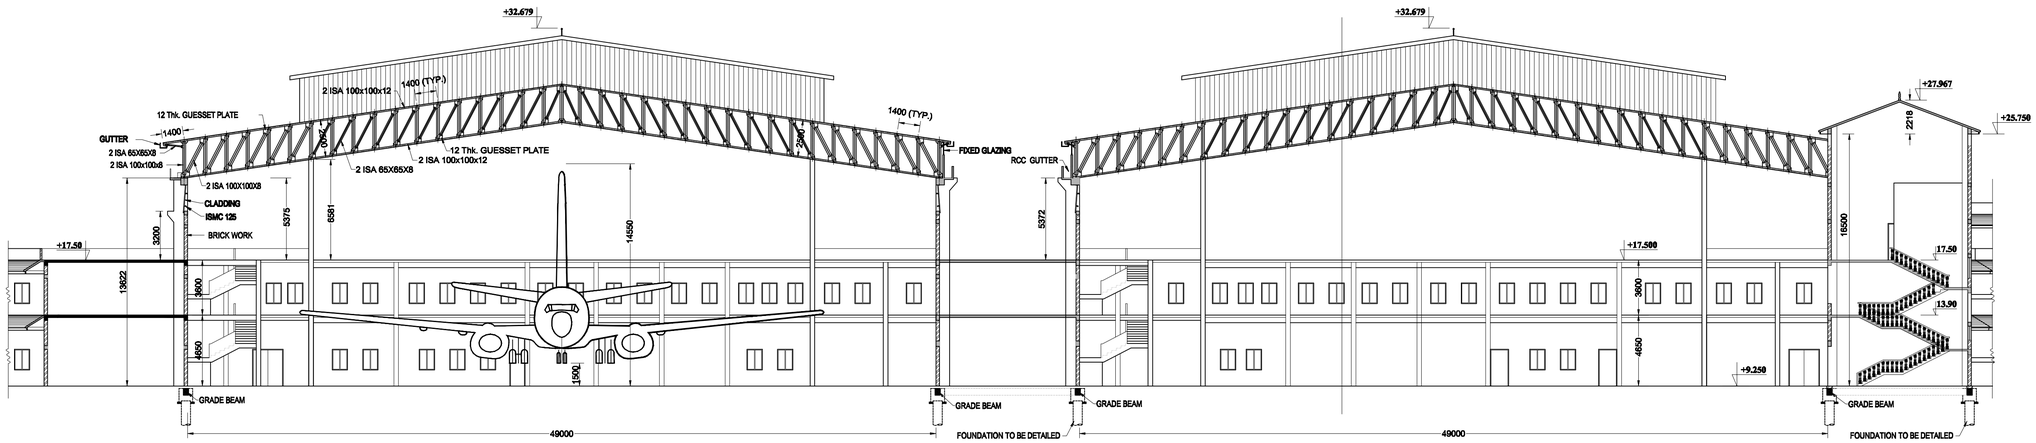

SECTION A-A

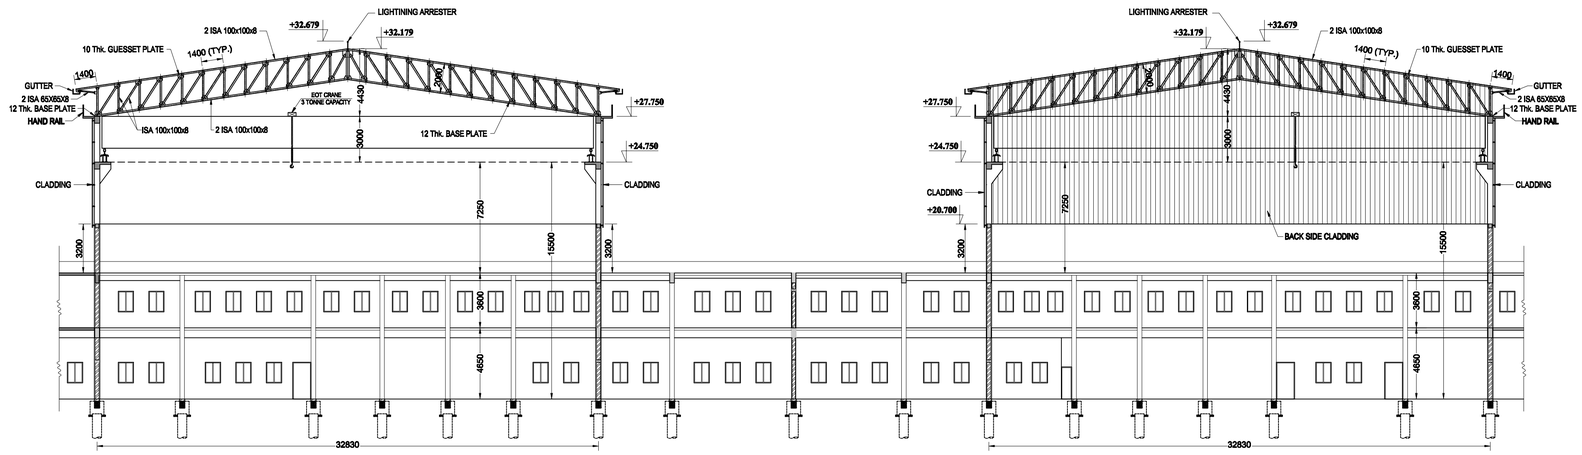

SECTION B-B

FOR TENDER PURPOSE ONLY

NOTES :-

01. ALL DIMENSIONS ARE IN MILLIMETERS AND LEVELS ARE IN METERS.
02. DRAWING IS NOT TO BE SCALED. ONLY WRITTEN DIMENSIONS ARE TO BE FOLLOWED.
03. FINISHED GROUND FLOOR LEVEL CORRESPONDS TO +9.25m LVL.

SL.No.	PARTICULARS	INITIAL	DATE
	REVISION		

This drawing is the property of KITCO Ltd. and is to be used only for the purpose for which it was lent and must not be in any way detrimental to the interest of the company and is subject to return on demand

DESIGNED	
CHECKED	
DRAWN	Boby
CHECKED	
APPROVED	
SCALE	1 : 200
UNIT	mm.
DATE	20.11.2008

KITCO the consultants

KITCO Ltd.
(Estd. in 1972 by IDBI & Govt. of Kerala)
RAVIPURAM, COCHIN - 16

CLIENT: COCHIN INTERNATIONAL AVIATION SERVICE LTD.

PROJECT: PROPOSED AIRCRAFT MAINTENANCE AND AVIATION TRAINING FACILITIES AT CIAL, NEDUMBASSERY

TITLE: ELEVATION, SECTION A-A AND SECTION B-B -: AIRCRAFT MAINTENANCE HANGER :-

DRG NO: DP. 337 DRG. CL. 01 016 | REV. | SHEET NO: 1 OF 1

Z:\Drawings 2008\C I A S L\HANGER HANGER 14.02.2008 PLAN FINAL R16 FOR TRUSS TENDER.dwg — Dec. 01, 2008