
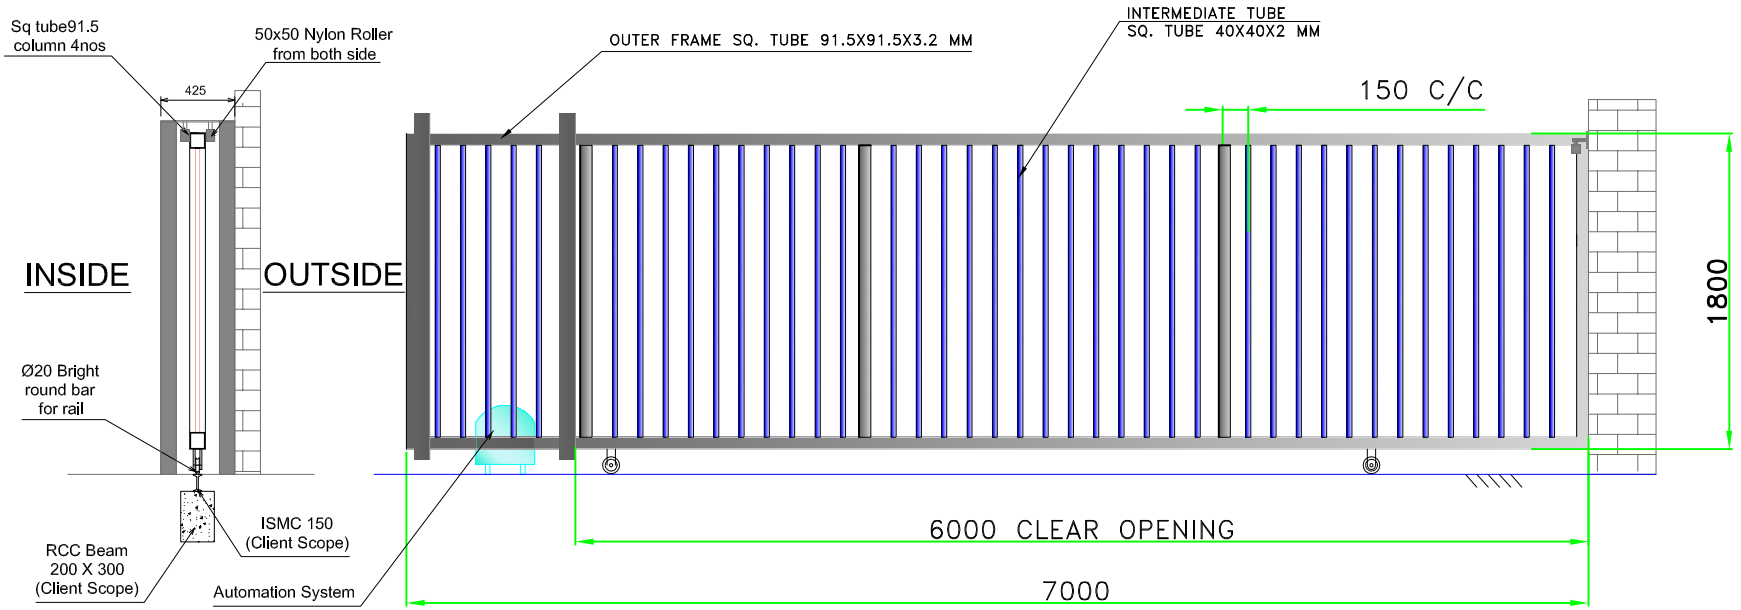


SLIDING GATE DIRECTION

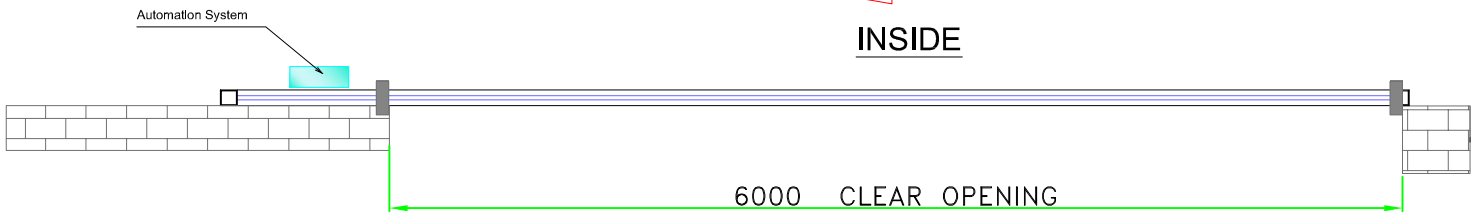

This drawing & designing is the property of NIHVA TECHNOLOGIES. Not be sold or copy to any other concern.

SLIDING GATE SIZE = 7000 (W) X 1800 (H), QTY = 1NOS.
CLEAR OPENING = 6,000 (W) X 1800 (H)
OUTER FRAME = 91.5 X 91.5 X 3.2 mm
INNER FRAME = 40 X 40 X 2 mm
GAP B/W FRAME = 150 c/c
C' COLUMN VERTICAL SUPPORT = 4 NOS.
ALL DIMENSIONS ARE IN MM

TITLE

SLIDING GATE

CLIENT APPROVAL

ALL DIMENSION ARE IN mm

	SIGN	DATE
DRAWN	ABHIJIT	10/11/14
CHECK	ANIL	10/11/14
REV.	04	
APPRD.		
MFG		
Ref. No.		

NIHVA TECHNOLOGIES PVT. LTD.

NIHVA TECHNOLOGY
PVT. LTD. PUNE
Tel : 020 66304033
Email:- info@nihva.com
Website:- www.nihva.com

CLIENT - VALEO
PROJECT - VALEO THERMAL SYSTEM
SITE - SANAND, GUJRAT
DWG. NO. - NVA/JSW/D1/ 2 of 3
SCALE: 01 | WT: | SHEET: 01
If any queries contact : projects@nihva.com