


Revision	Date	By
A Corrected mullion hoist positions, floor pits altered	2022-08-02	EB

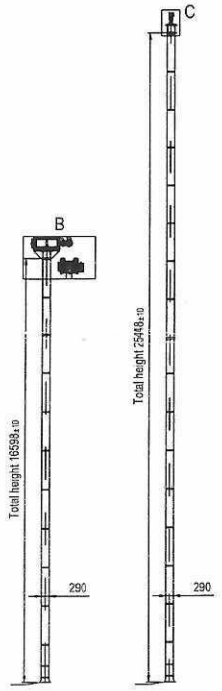


SECTION D-D SECTION E-E

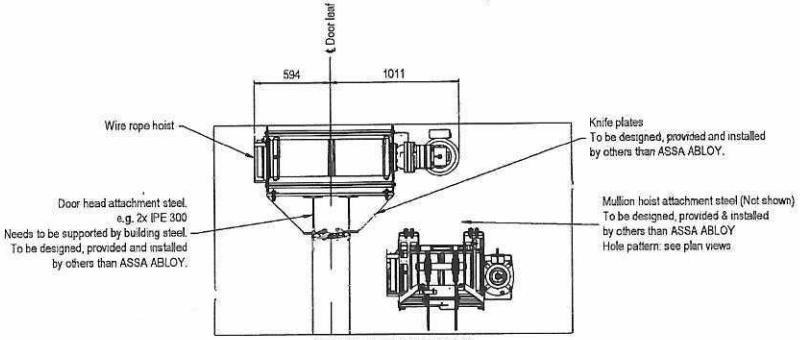


DETAIL B, SCALE (1:20)

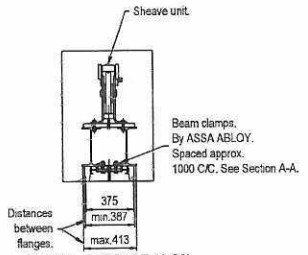


DETAIL C, SCALE (1:20)

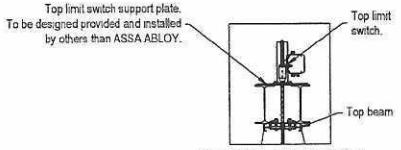


DETAIL D, SCALE (1:20)

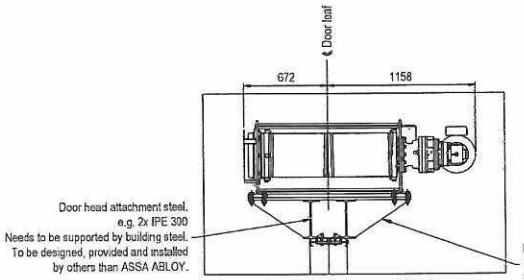

DETAIL E, SCALE (1:20)

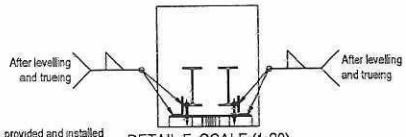


DETAIL F, SCALE (1:20)

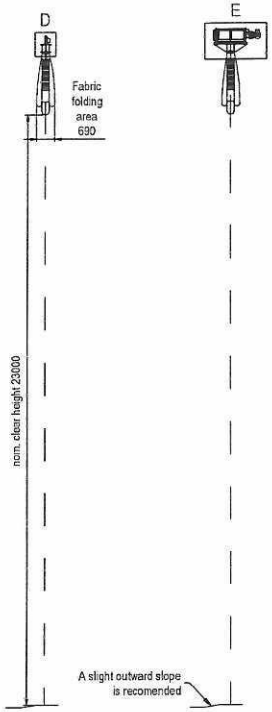


SECTION F-F

SECTION G-G

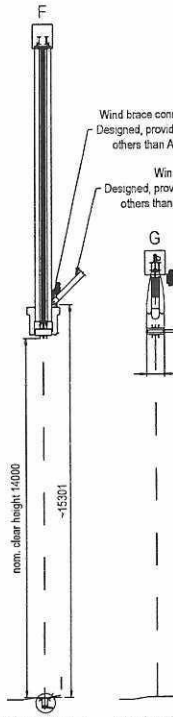


SECTION H-H

SECTION I-I

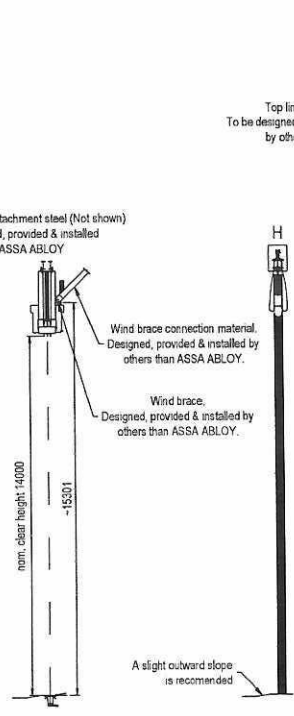


SECTION J-J


SECTION K-K

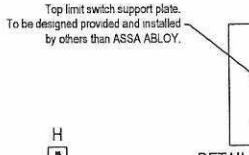

DETAIL G, SCALE (1:20)

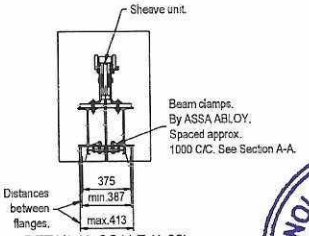

DETAIL H, SCALE (1:20)

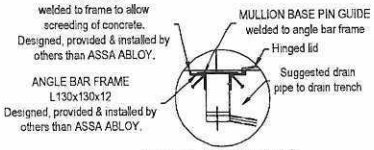

DETAIL I, SCALE (1:20)

NIHAL TECHNOLOGIES PVT. LTD. PUNE

DOOR IDENTITY NUMBER: 84800001

LOAD DIAGRAM & NOTES, ref. to drwng. no. 77446

INTERFACE, PLAN VIEWS ref. to drwng. no. 77444

INTERFACE, ELEVATION ref. to drwng. no. 77443

DESIGNED EB	SIZE A1	SCALE 1:100	GMR Aero Technic Hangar1
CODE 84800	If not otherwise stated		India
ITEM NO	Tolerances ISO 2768-m EN ISO 13920-B		Megadoor 84000x23000/14000
DATE 2022-08-23	Cutting class ISO 9013-442		Interface, sections
ASSA ABLOY	Weld class ISO 5817-C	DRAWING NO 77445	REVISION A
	Surface finish Smooth raw surface		

The document is the property of ASSA ABLOY Entrance Systems AB and may not be copied or otherwise reproduced or used in whole or in part by or made available to any other unauthorized person.