


PRODUCED BY AN AUTODESK EDUCATIONAL PRODUCT

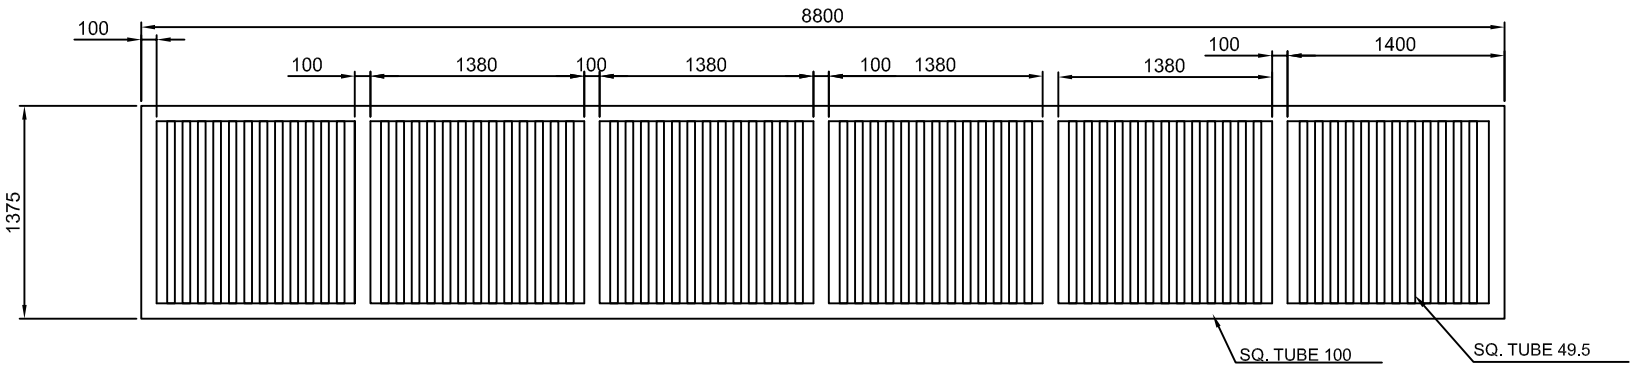

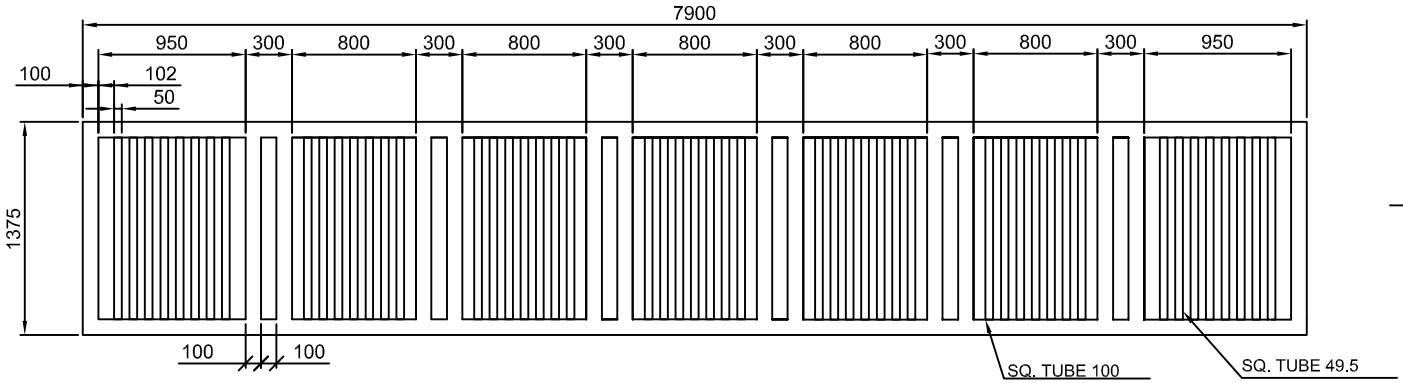

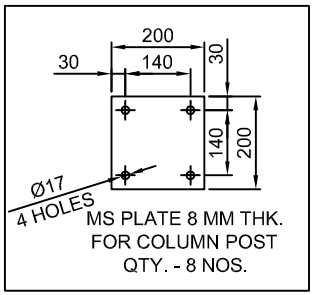

MS PLATE 8 MM THK.
FOR COLUMN POST
QTY. - 8 NOS.

NOTE-
1. ALL REQUIRED CIVIL WORK WILL BE IN CLIENTS SCOPE.
3.GATE LEAF WILL BE IN TWO PARTS FOR TRANSPORTATION & WILL BE WELD TOGETHER ON SITE.

TOLERANCE - ±10mm

CLEAR WIDTH	CLEAR HEIGHT	QUANTITY
15000	1500	01 NOS

This drawing & design is the property of NIHVA TECHNOLOGIES. Not to be sold or copied to any other concern.

TITLE
TELESCOPIC
SLIDING GATE

NIHVA
NIHVA TECHNOLOGIES PVT. LTD.

NIHVA TECHNOLOGIES
PVT. LTD. PUNE
Tel : 020 66304033
Email:- info@nihva.com
Website:- www.nihva.com

	NAME	SIGN	DATE
DRAWN	A.K.		18.04.2019
CHECK	P.A.		18.04.2019
APPRD.	R.D.		18.04.2019

CLIENT - ESR PUNE
PROJECT - WANI PROJECTS
SITE LOCATION - CHAKAN, PUNE.
If any queries contact : design@nihva.com
DWG. NO. : NIHVA/19-20/0008
REV- 00
ALL DIMENSION ARE IN mm
SCALE: NTS
WT:
SHEET: 01 OF 01

PRODUCED BY AN AUTODESK EDUCATIONAL PRODUCT