




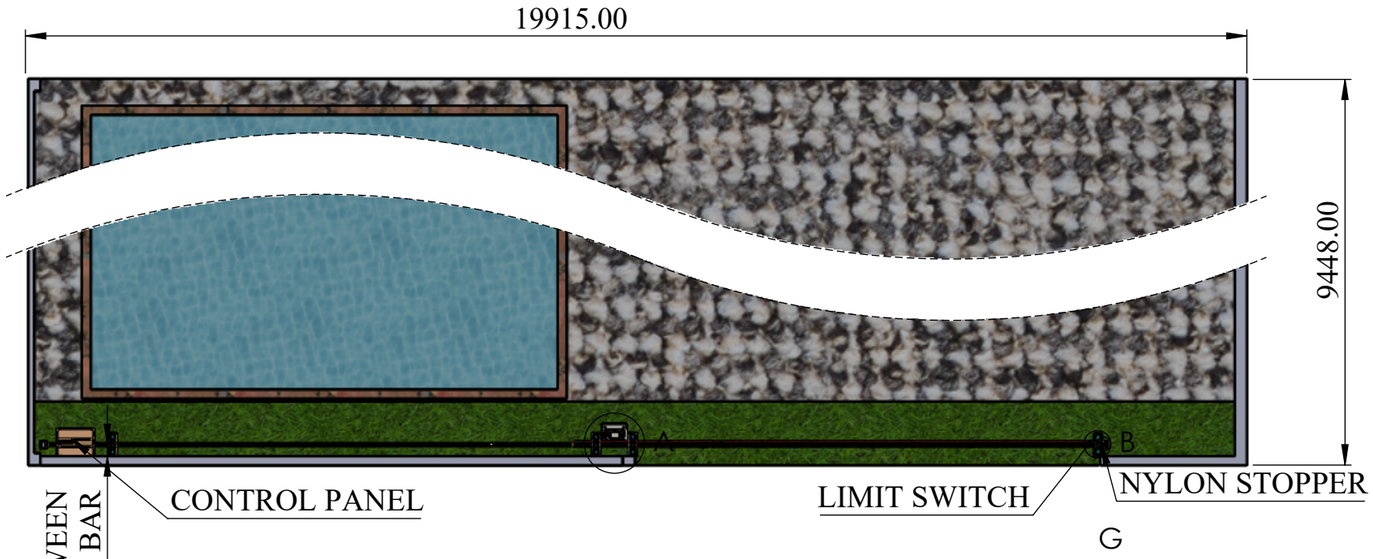

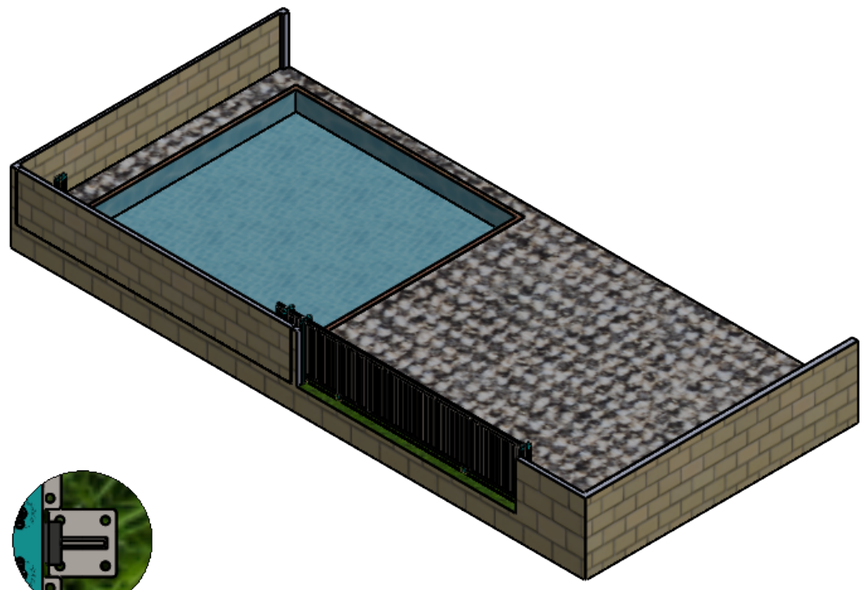


NYLON STOPPER
DETAIL G
SCALE 1 : 10

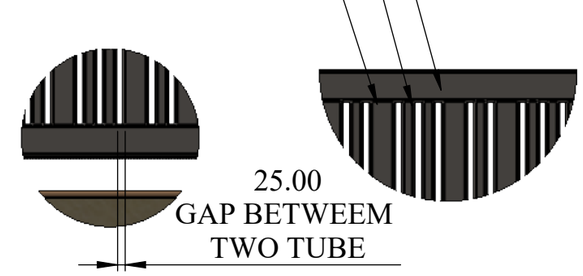

DETAIL D
SCALE 1 : 20


DETAIL E
SCALE 1 : 20

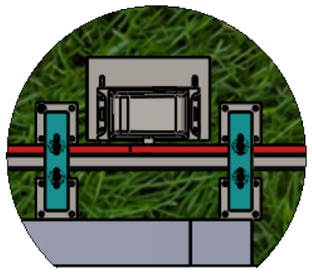

DETAIL A
SCALE 1 : 20



DETAIL B
SCALE 1 : 15

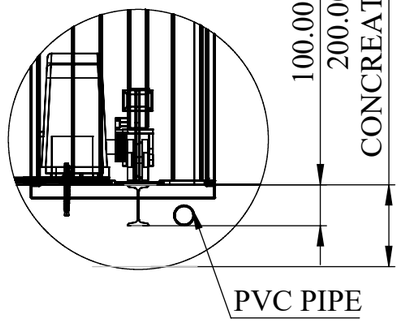



DETAIL C
SCALE 1 : 15


POST AND NYLON ROLLER
BEARING ASM


MOTORISIED SLIDING GATE
SIZE- 8600 (W)X1700(H)
THIS IS DISTANCE CONSIDER FOR MOTOR + MOUNTING DISTANCE

TITLE - GATE AUTOMATION				NIHVA TECHNOLOGIES PVT.LTD.PUNE	
DWG NO - NTPL-283-PM-001-00-00-00				Website - www.nihva.com	
	NAME	SIGNATURE	DATE	PROJECT NO - NTPL-283-PM	
DRAWN	V.B		15-07-2025	PRODUCT -MOTOR. SLIDING GATE	REVISION -01
CHK'D	S.W.		15-07-2025	SITE LOCATION - LUCKNOW	WEIGHT -
APPV'D	V.T.		15-07-2025	MATRIAL -	QTY - 1
if any queries contact - supportautomation@nihva.com				PROJECTION METHOD:	SCALE :
ALL DIMENSION ARE IN mm			A3		SHEET 1 OF 13

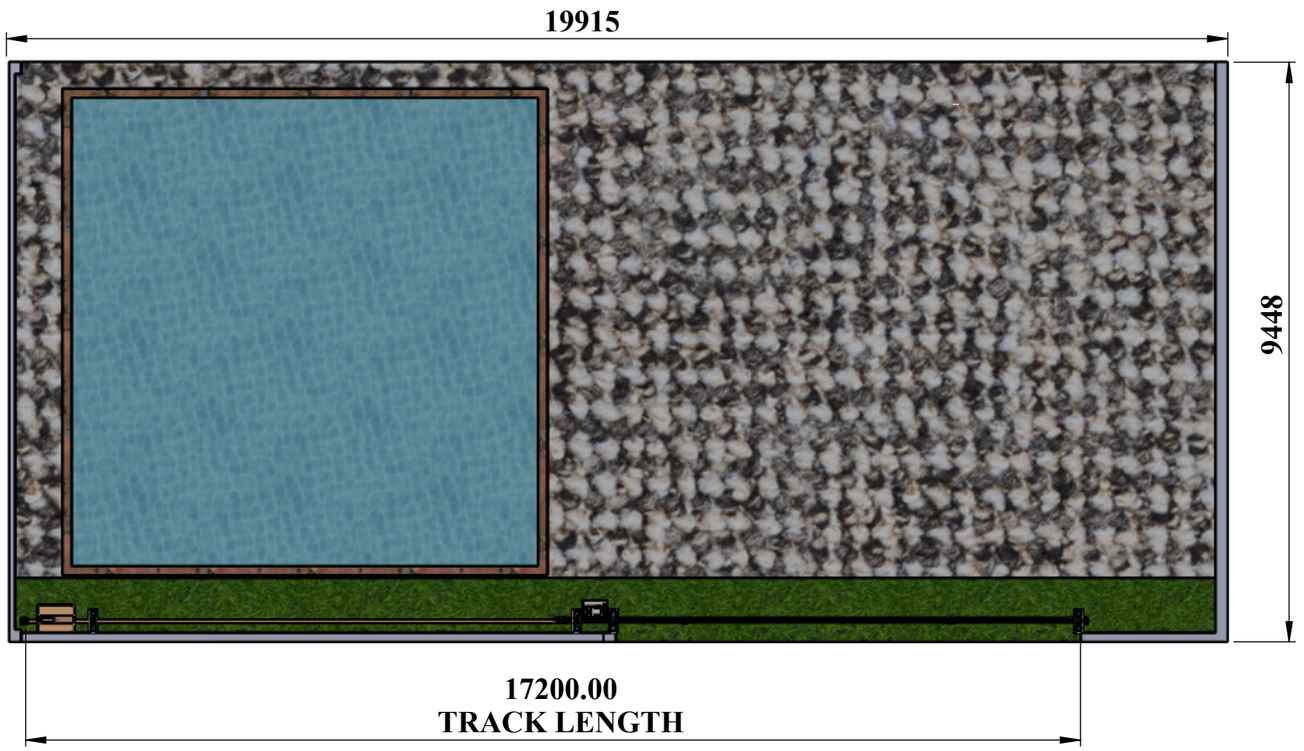

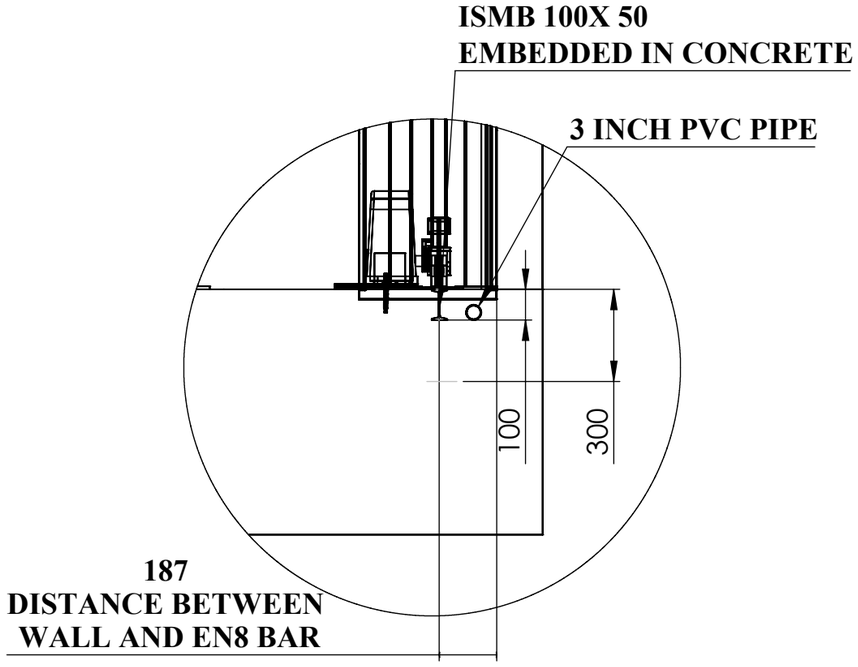

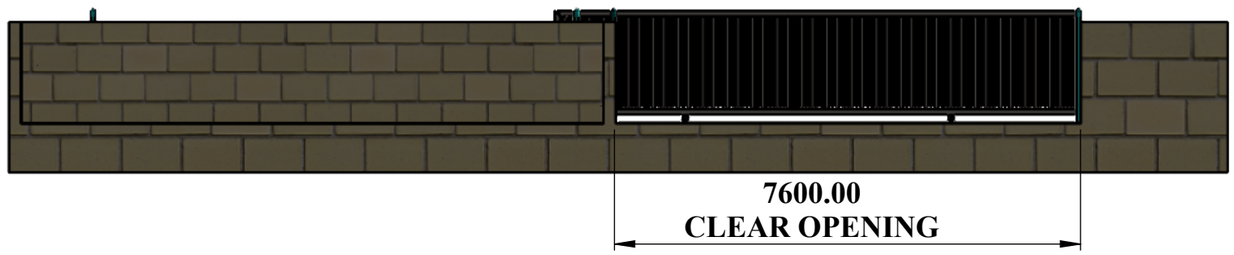

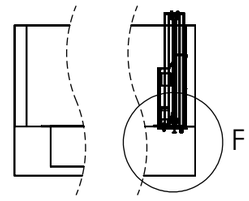

DETAIL F
SCALE 1 : 20

MOTORIZED SLIDING GATE

PARKING AREA IS 8.6M

NOTE:


1) CIVIL AREA IS CLIENT SCOPE


2) WIRING POINT IS DESIDED ON CLIENT SITE AS PER GATE LOCATION


3) RAL CODE NOT CONSIDER


TITLE - GATE AUTOMATION				NIHVA TECHNOLOGIES PVT.LTD.PUNE	
DWG NO - NTPL-283-PM-002-00-00-00				Website - www.nihva.com	
	NAME	SIGNATURE	DATE	PROJECT NO - NTPL-283-PM	
DRAWN	V.B.		15-07-2025	PRODUCT -MOTOR. SLIDING GATE	REVISION - 01
CHK'D	S.W.		15-07-2025	SITE LOCATION -LUCKNOW	WEIGHT -
APPV'D	V.T.		15-07-2025	MATRIAL -	QTY - 1
if any queries contact - supportautomation@nihva.com				PROJECTION METHOD:	SCALE :
ALL DIMENSION ARE IN mm			A3		SHEET 2 OF 13

ITEM NO.	PART NUMBER	DESCRIPTION	QTY.
1	CIVIL AREA	19915 (L)X9449(W)	1
2	EN 8 BAR AND ISMB 1	OD- 20 MM,19200MM LONG	1
3	LEAF ASM	8600 W X 1700 H	1
4	Post asm	320 L X1850 H	4
5	MS WHEEL	100X 50	2
8	NYLON ROLLER AND BOLT ASM	75 L X50 OD	8
9	MOTOR	MOTOR NAME:- RUN 1500	1
10	RACK ASM	M4 MODULE 4 1M STD SIZE	8.6
11	MOTOR PLATE	270X400X6 MM THK	3
12	NYLON STOPPER ASM	110 X 110 X 6MM THK	2
13	PVC PIPE	3 INCH X 7800MM L	1
14	ROLLER LIMIT SWITCH		2
15	CONTROL PANEL		1
16	M12 ANCHOR ASSY	M12X220	32

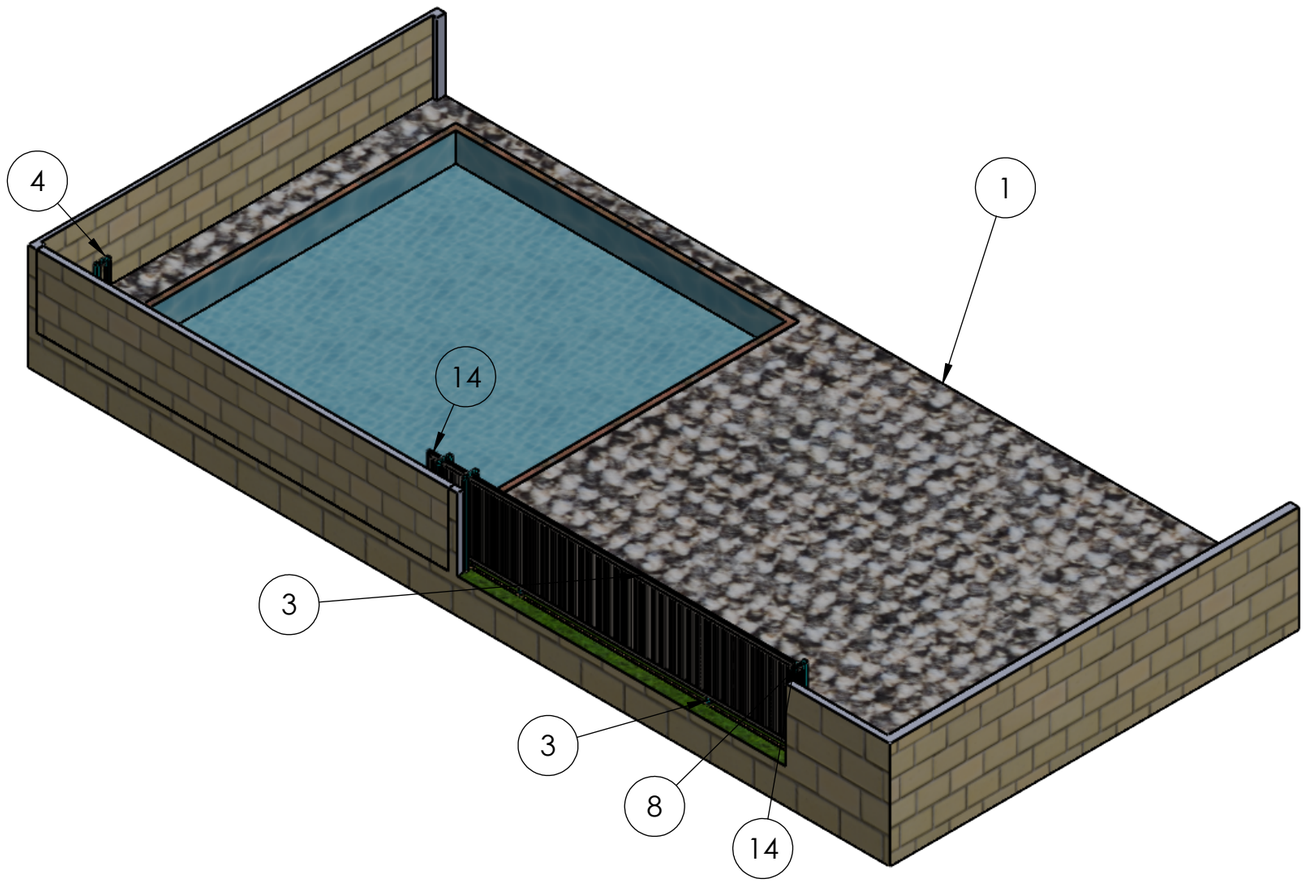


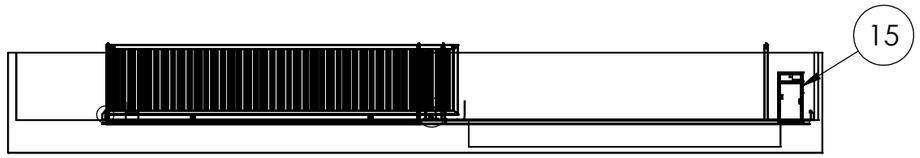

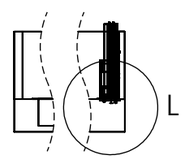


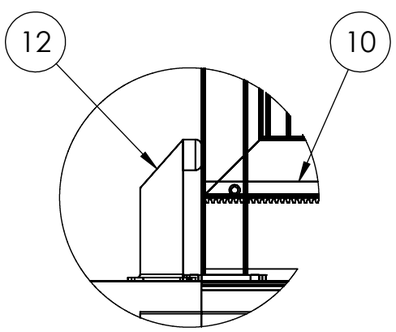

DETAIL H
SCALE 1 : 10

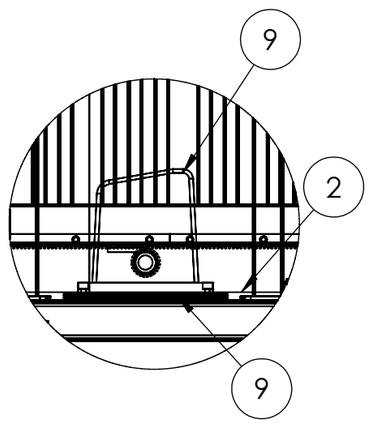

DETAIL J
SCALE 1 : 15

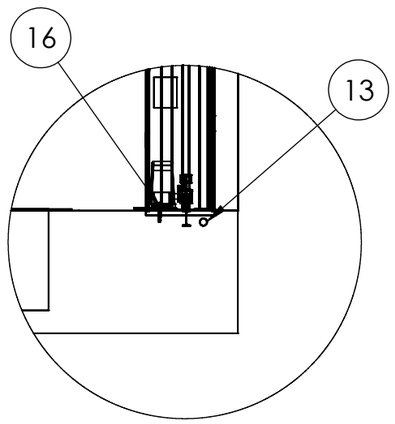


DETAIL L
SCALE 1 : 40


Purpose of 1000 mm Overlapping-


1. **Ensures full Opening Clearance.**
2. **motor and Guide Support Positioning**
3. **structural Stability**
4. **space For Gate Travel**
5. **1000 mm is Perfectly Within Safe and Practical Design Range.**

TITLE - GATE AUTOMATION				NIHVA TECHNOLOGIES PVT.LTD.PUNE	
DWG NO - NTPL-283-PM-003-00-00-00				Website - www.nihva.com	
	NAME	SIGNATURE	DATE	PROJECT NO - NTPL-283-PM	
DRAWN	V.B.		15-07-2025	PRODUCT - MOTO. SLIDING GATE	REVISION -01
CHK'D	S.W.		15-07-2025	SITE LOCATION -LUCKNOW	WEIGHT -
APPV'D	V.T.		15-07-2025	MATRIAL -	QTY - 1
if any queries contact - supportautomation@nihva.com				PROJECTION METHOD:	SCALE :
ALL DIMENSION ARE IN mm			A3		SHEET 3 OF 13

ITEM NO.	PART NUMBER	DESCRIPTION	QTY.
1	SLIDING GATE	8600(L)X1700 (H)	1
2	WHEEL AND PLATE ASM	4 INCH WHEEL	2

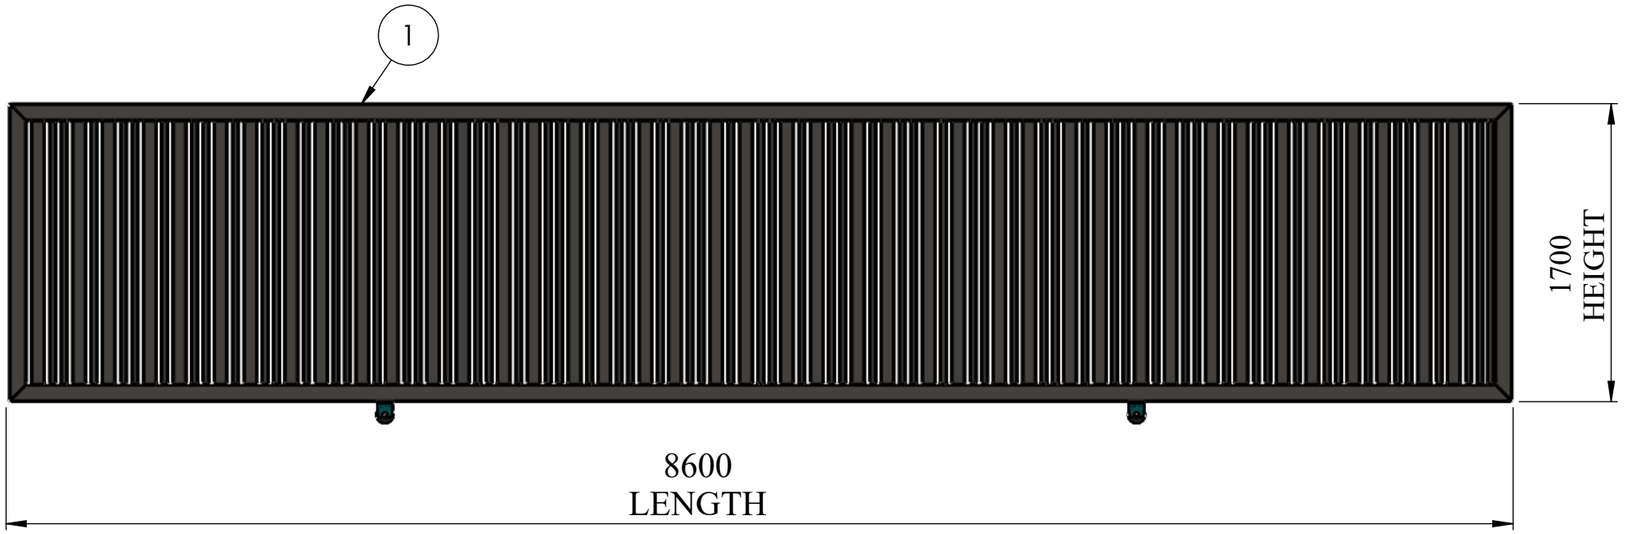

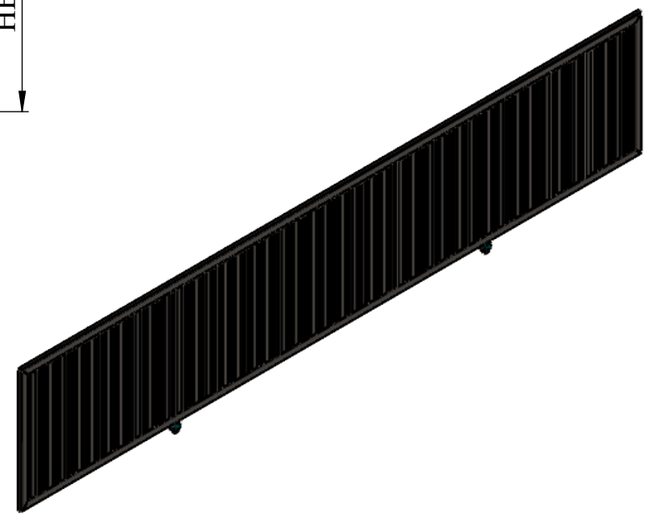


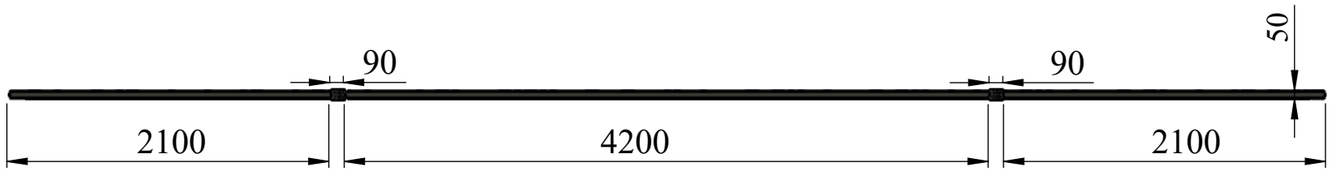


SLIDING LEAF:-1NOS

TITLE - GATE AUTOMATION				NIHVA TECHNOLOGIES PVT.LTD.PUNE
DWG NO -NTPL-283-PM-003-01-00-00				Website - www.nihva.com
	NAME	SIGNATURE	DATE	PROJECT NO - NTPL-283-PM
DRAWN	V.B.		15-07-2025	PRODUCT -MOTORISIED SLIDING GATE
CHK'D	S.W.		15-07-2025	SITE LOCATION - LUCKNOW
APPV'D	V.T.		15-07-2025	
if any queries contact - supportautomation@nihva.com				REVISION -
ALL DIMENSION ARE IN mm			A3	SCALE - SHEET 4 OF 13

ITEM NO.	PART NUMBER	DESCRIPTION	QTY.
	OUTER FRAME	100X50X3 THK	4
	VERTICAL INNER TUBE	80X40X3 THK	41
	VERTICAL INNER TUBE	40X 40X3 THK	63

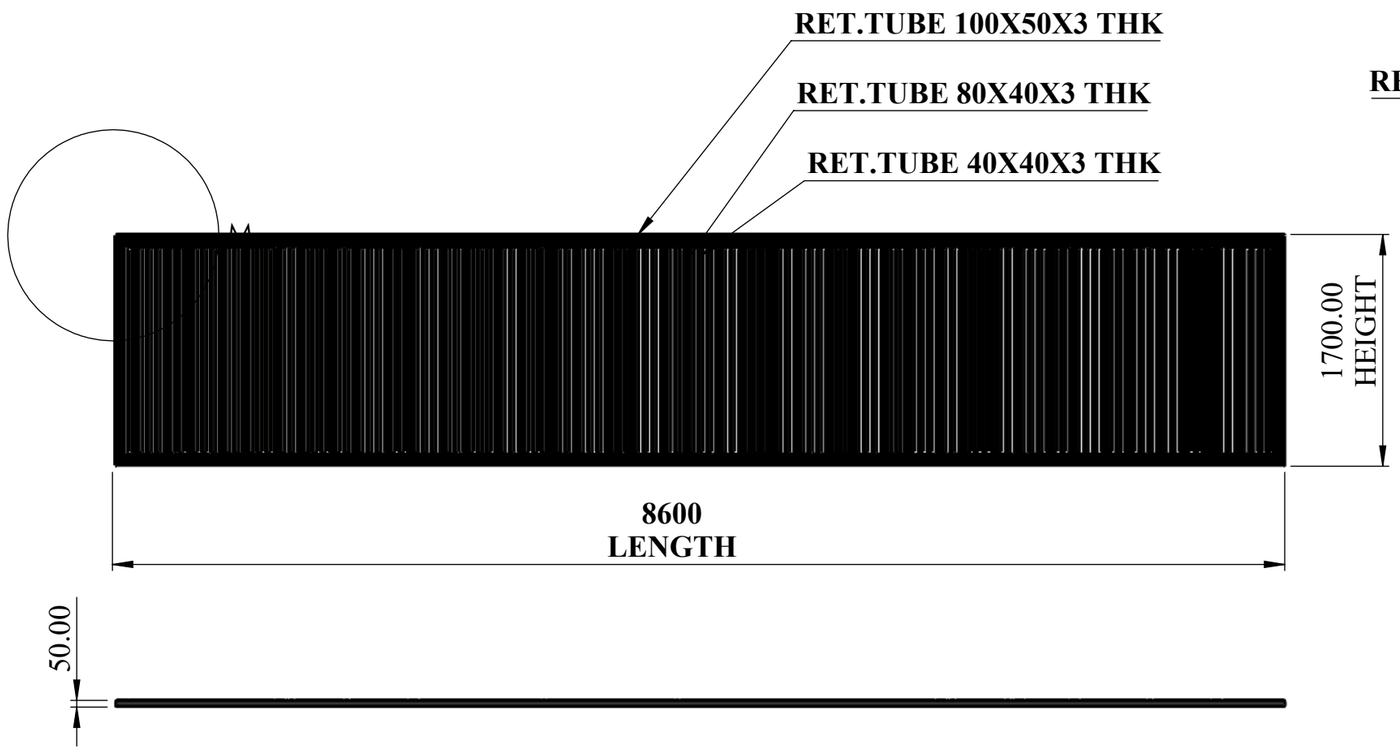

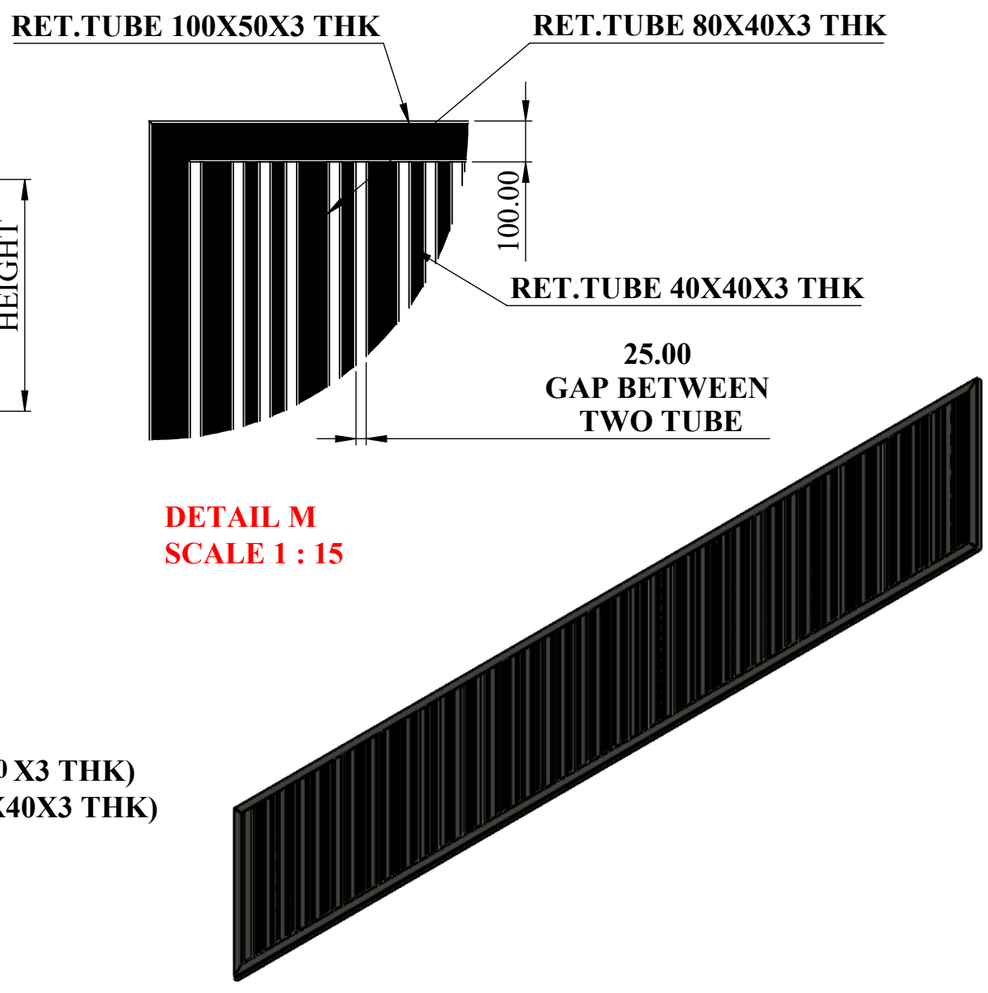


DETAIL M
SCALE 1 : 15


SUPPORT TUBE
QTY- 41 NOS (RET.TUBE 80X40 X3 THK)
63 NOS (RET.TUBE 40 X40X3 THK)

SR.NO.	REVISION
1	INNER TUBE SIZE CHANGE-80X50X3 TO 80X40X3 THK
2	INNER TUBE SIZE 40X50X3 TO 40X40X3 THK

TITLE - GATE AUTOMATION				NIHVA TECHNOLOGIES PVT.LTD.PUNE
DWG NO - NTPL-283-PM			QTY - 1	Website - www.nihva.com
	NAME	SIGNATURE	DATE	PROJECT NO - NTPL-283-PM
DRAWN	V.B.		15-07-2025	PRODUCT - MOTORISIED SLIDING GATE
CHK'D	S.W.		15-07-2025	SITE LOCATION - LUCKNOW
APPV'D	V.T.		15-07-2025	
if any queries contact - supportautomation@nihva.com				REVISION -
ALL DIMENSION ARE IN mm			A3	SCALE - SHEET 5 OF 13

ITEM NO.	PART NUMBER	DESCRIPTION	QTY.
1	VERTICAL SQ TUBE	75.00 X 75.00 X 3.00	8
2	ROLLER SUPPORT PLATE	320X75X10	4
3	BOTTOM PLATE	135X135X10	8

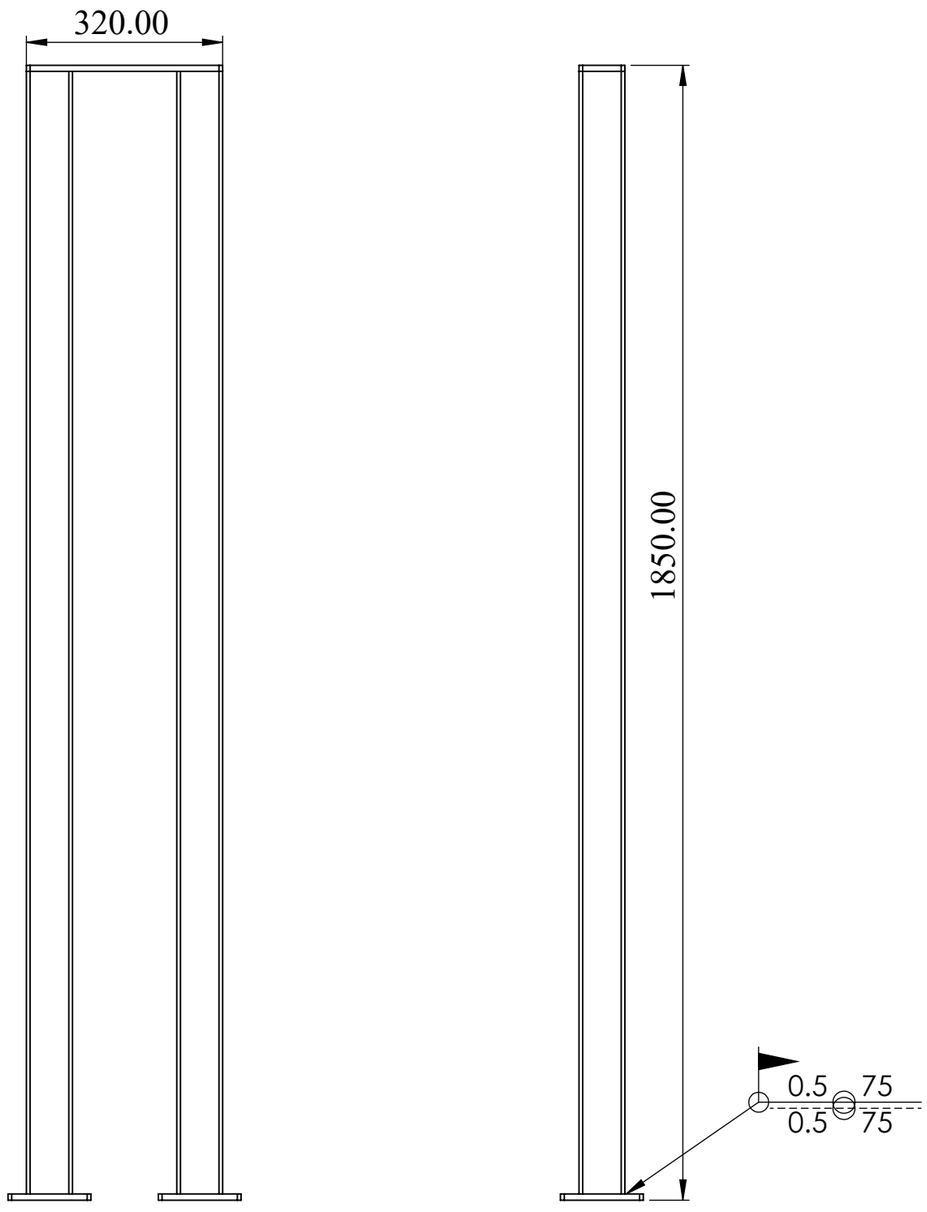


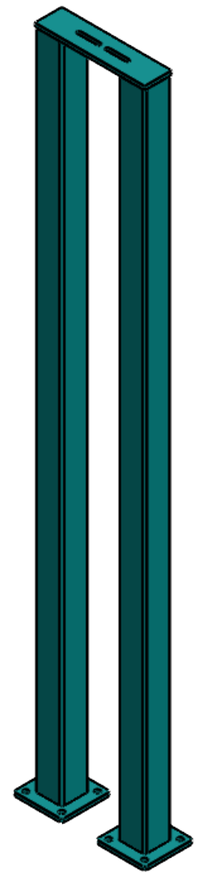



POST 1 ASM
QTY- 4 NOS

TITLE - GATE AUTOMATION				NIHVA TECHNOLOGIES PVT.LTD.PUNE Website - www.nihva.com
DWG NO - NTPL-283-PM			QTY - 1	
	NAME	SIGNATURE	DATE	PROJECT NO - NTPL-283-PM
DRAWN	V.B.		15-07-2025	PRODUCT - MOTORISIED SLIDING GATE
CHK'D	S.W.		15-07-2025	SITE LOCATION - LUCKNOW
APPV'D	V.T.		15-07-2025	
if any queries contact - supportautomation@nihva.com				REVISION -
ALL DIMENSION ARE IN mm			A3	SCALE - SHEET 6 OF 13

ITEM NO.	PART NUMBER	DESCRIPTION	QTY.
1	ROLLER SUPPORT PLATE	320X75X10 THK	4

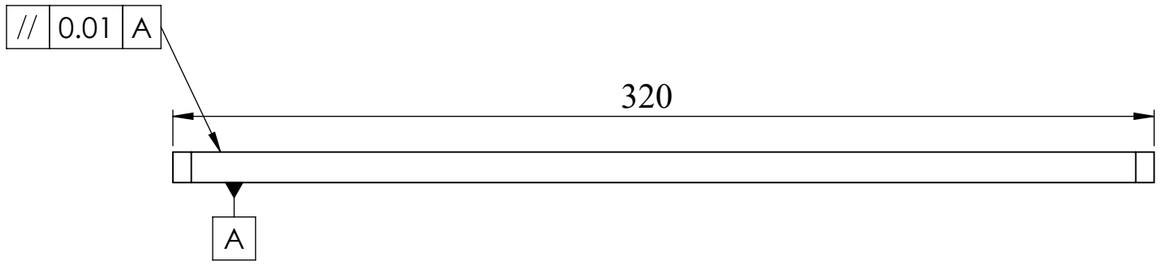

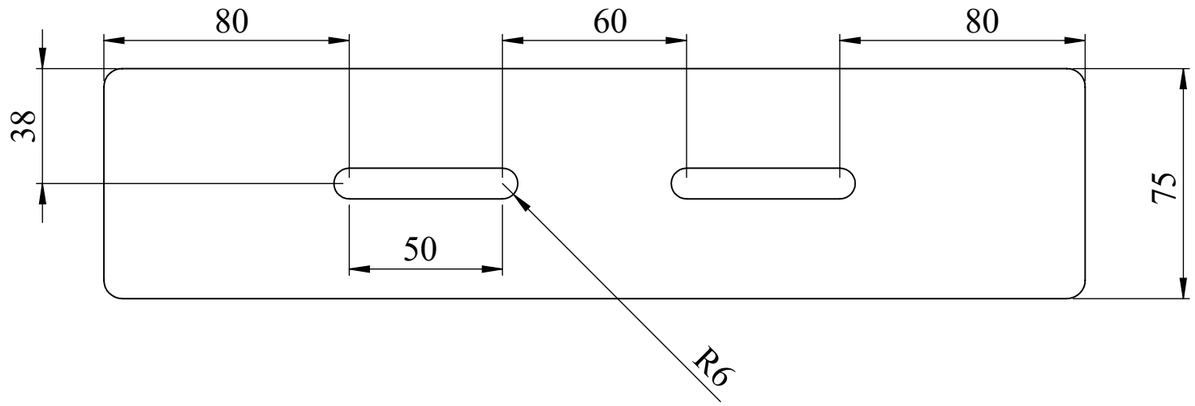

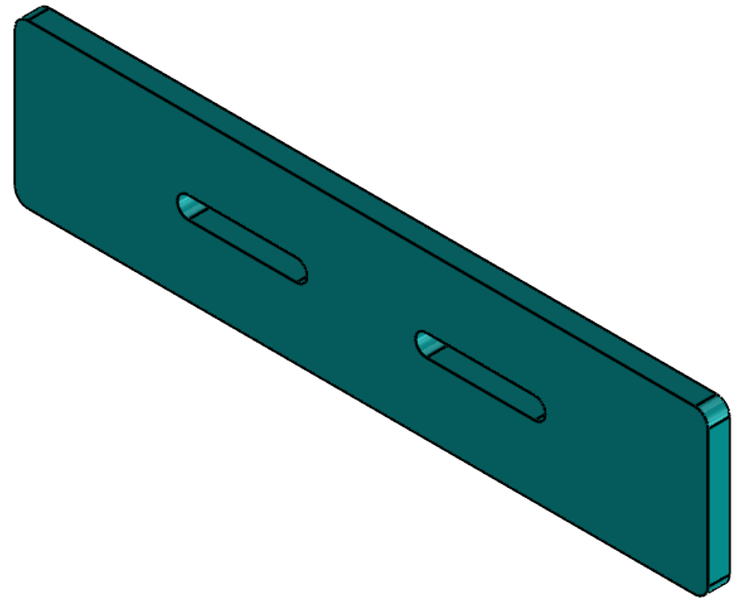


POST ROLLER SUPPORT PLATE

320X75X10 THK

QTY : 4 NOS

TITLE - GATE AUTOMATION				NIHVA TECHNOLOGIES PVT.LTD.PUNE
DWG NO - NTPL-283-PM			QTY - 1	Website - www.nihva.com
	NAME	SIGNATURE	DATE	PROJECT NO - NTPL-283-PM
DRAWN	V.B.		15-07-2025	PRODUCT - MOTORISIED SLIDING GATE
CHK'D	S.W.		15-07-2025	SITE LOCATION - LUCKNOW
APPV'D	V.T.		15-07-2025	
if any queries contact - supportautomation@nihva.com				REVISION -
ALL DIMENSION ARE IN mm			A3	SCALE - SHEET 7 OF 13

ITEM NO.	PART NUMBER	DESCRIPTION	QTY.
1	VERTICAL SQ TUBE	75.00 X 75.00 X 3.00	8

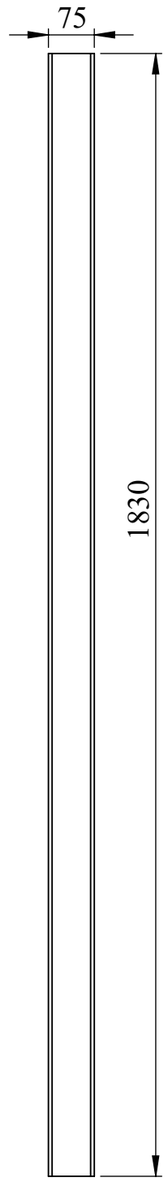





POST VERTICAL SQ. TUBE
75X75X3 THK
QTY : 8NOS

TITLE - GATE AUTOMATION				NIHVA TECHNOLOGIES PVT.LTD.PUNE Website - www.nihva.com
DWG NO - NTPL-283-PM			QTY - 1	
	NAME	SIGNATURE	DATE	PROJECT NO - NTPL-283-PM
DRAWN	V.B.		15-07-2025	PRODUCT - MOTORISIED SLIDING GATE
CHK'D	S.W.		15-07-2025	SITE LOCATION - LUCKNOW
APPV'D	V.T.		15-07-2025	
if any queries contact - supportautomation@nihva.com				REVISION -
ALL DIMENSION ARE IN mm			A3	SCALE - SHEET 8 OF 13

ITEM NO.	PART NUMBER	DESCRIPTION	QTY.
1	BOTTOM PLATE FOR POST	135X135X10 THK	8

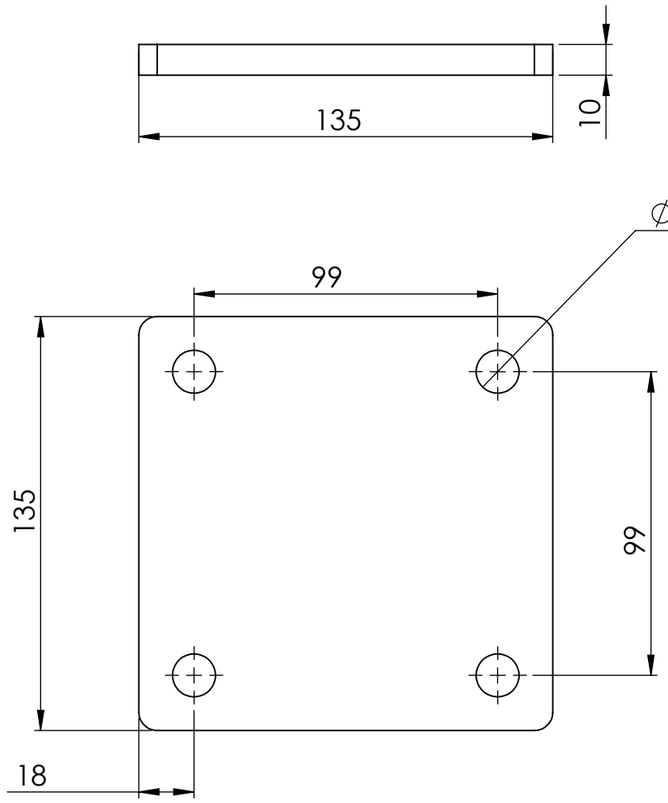

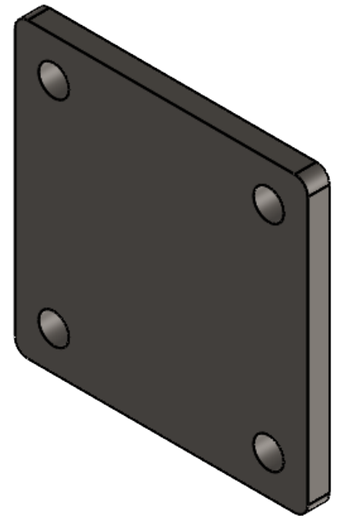

NOTE:


POST BOTTOM PLATE
MS 135X135X10 THK


THIS BOTTOM PLATE
USED SAME FOR POST 2

QTY:- 8 NOS

TITLE - GATE AUTOMATION				NIHVA TECHNOLOGIES PVT.LTD.PUNE
DWG NO - NTPL-283-PM			QTY - 1	Website - www.nihva.com
	NAME	SIGNATURE	DATE	PROJECT NO - NTPL-283-PM
DRAWN	V.B.		15-07-2025	PRODUCT - MOTORISIED SLIDING GATE
CHK'D	S.W.		15-07-2025	SITE LOCATION - LUCKNOW
APPV'D	V.T.		15-07-2025	
if any queries contact - supportautomation@nihva.com				REVISION -
ALL DIMENSION ARE IN mm			A3	SCALE - SHEET 9 OF 13


ITEM NO.	PART NUMBER	DESCRIPTION	QTY.
1	EN8 BAR	OD- 20 MM	1
	ISMB BEAM	SIZE- 100 X 8 17200 MM (L)	1

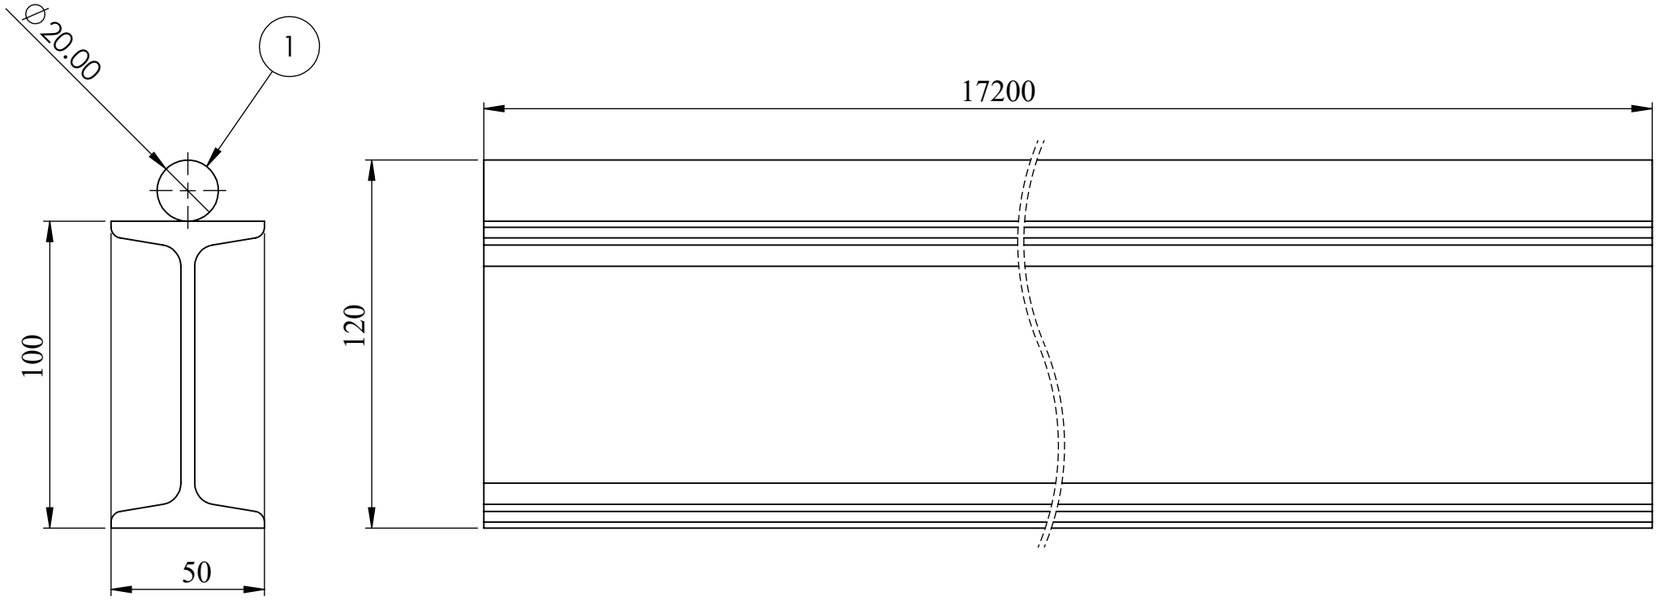

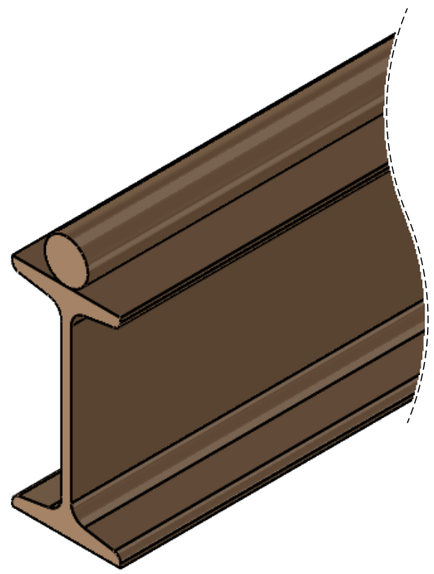



GATE TRACK
QTY-1NOS

TITLE - GATE AUTOMATION				NIHVA TECHNOLOGIES PVT.LTD.PUNE Website - www.nihva.com
DWG NO - NTPL-283-PM			QTY - 1	
	NAME	SIGNATURE	DATE	PROJECT NO - NTPL-283-PM
DRAWN	V.B.		15-07-2025	PRODUCT - MOTORISIED SLIDING GATE
CHK'D	S.W.		15-07-2025	SITE LOCATION - LUCKNOW
APPV'D	V.T.		15-07-2025	
if any queries contact - supportautomation@nihva.com				REVISION -
ALL DIMENSION ARE IN mm			A3	SCALE - SHEET 10 OF 13

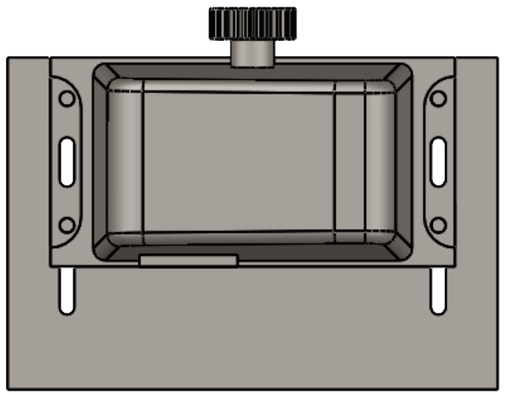

SR NO.	DESCRIPTION	TECHNICAL SPECIFICATION
1	PINION	Z- 4 ,module-4,Pitch-12.6mm
2	maximum inrush Torque	35mm
3	Nominal Torque	20mm
4	No- load speed	0.25 m/s
5	max. frequency of Operation in cycles/hour	60
6	Application limits	the Run Devices are generallly able to automate gates with weight and length within the limits
7	maximum peak power input	400 W
8	Dimensions and Weight	400x255 h 390; 19 kg

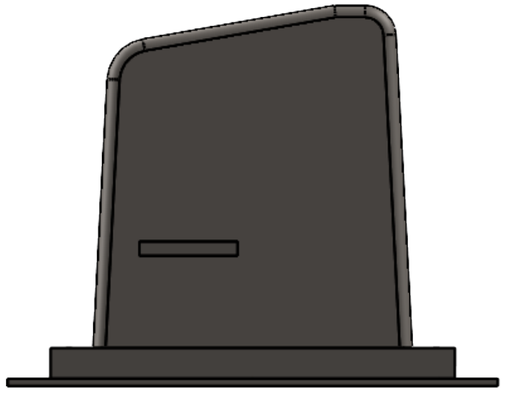


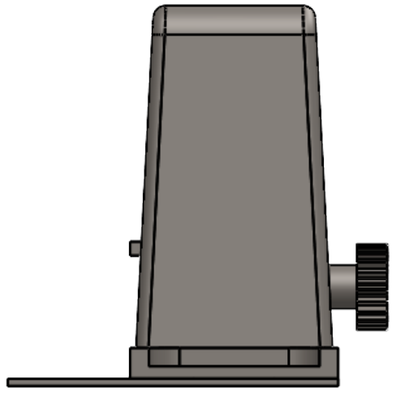



Motor - Run1500

TITLE - GATE AUTOMATION				NIHVA TECHNOLOGIES PVT.LTD.PUNE	
DWG NO - NTPL-283-PM-001-00-00-00				Website - www.nihva.com	
	NAME	SIGNATURE	DATE	PROJECT NO - NTPL-283-PM	
DRAWN	V.B.		15-07-2025	PRODUCT -MOTOR. SLIDING GATE	REVISION -
CHK'D	S.W.		15-07-2025	SITE LOCATION - LUCKNOW	WEIGHT -
APPV'D	V.T.		15-07-2025	MATRIAL -	QTY - 1
if any queries contact - supportautomation@nihva.com				PROJECTION METHOD:	SCALE :
ALL DIMENSION ARE IN mm			A3		SHEET 11 OF 1

ITEM NO.	PART NUMBER	DESCRIPTION	QTY.
1	M12 ANCHOR	M12X220	32

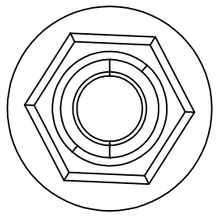

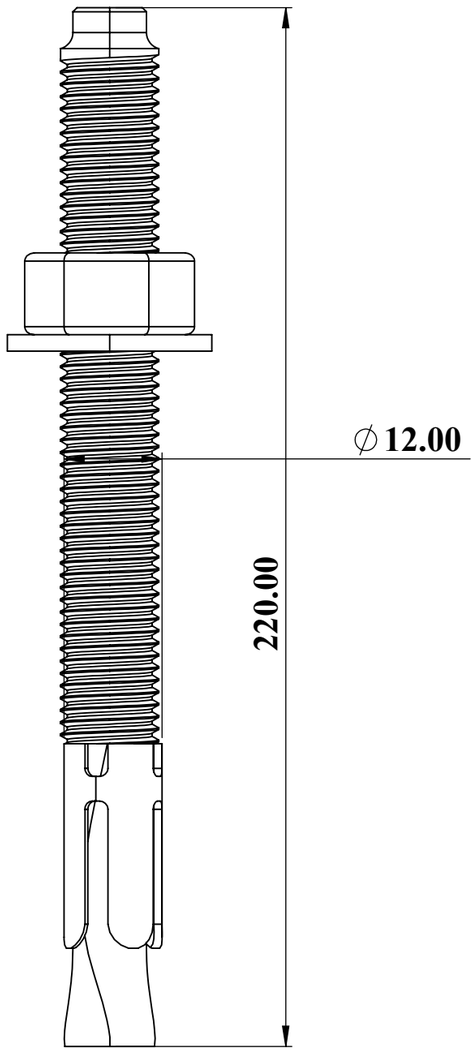


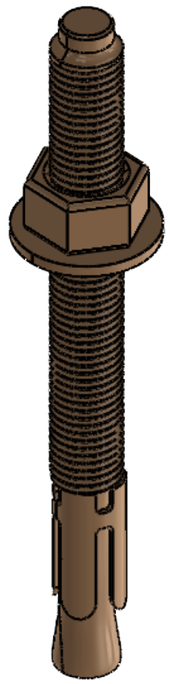


NOTE -
M12 X 220 MM ANCHOR BOLT
QTY- 32 NOS

TITLE -GATE AUTOMATION				NIHVA TECHNOLOGIES PVT.LTD.PUNE Website - www.nihva.com
DWG NO - NTPL283-PM			QTY - 1	
	NAME	SIGNATURE	DATE	PROJECT NO - NTPL283-PM- AD
DRAWN	V.B.		15-07-2025	PRODUCT - MOTORISIED SLIDING GATE
CHK'D	S.W.		15-07-2025	SITE LOCATION - LUCKNOW
APPV'D	V.T.		15-07-2025	
if any queries contact - supportautomation@nihva.com				REVISION -
ALL DIMENSION ARE IN mm			A3	SCALE - SHEET 12 OF 13

ITEM NO.	PART NUMBER	DESCRIPTION	QTY.
1	MOTOR BOTTOM PLATE	MS	3

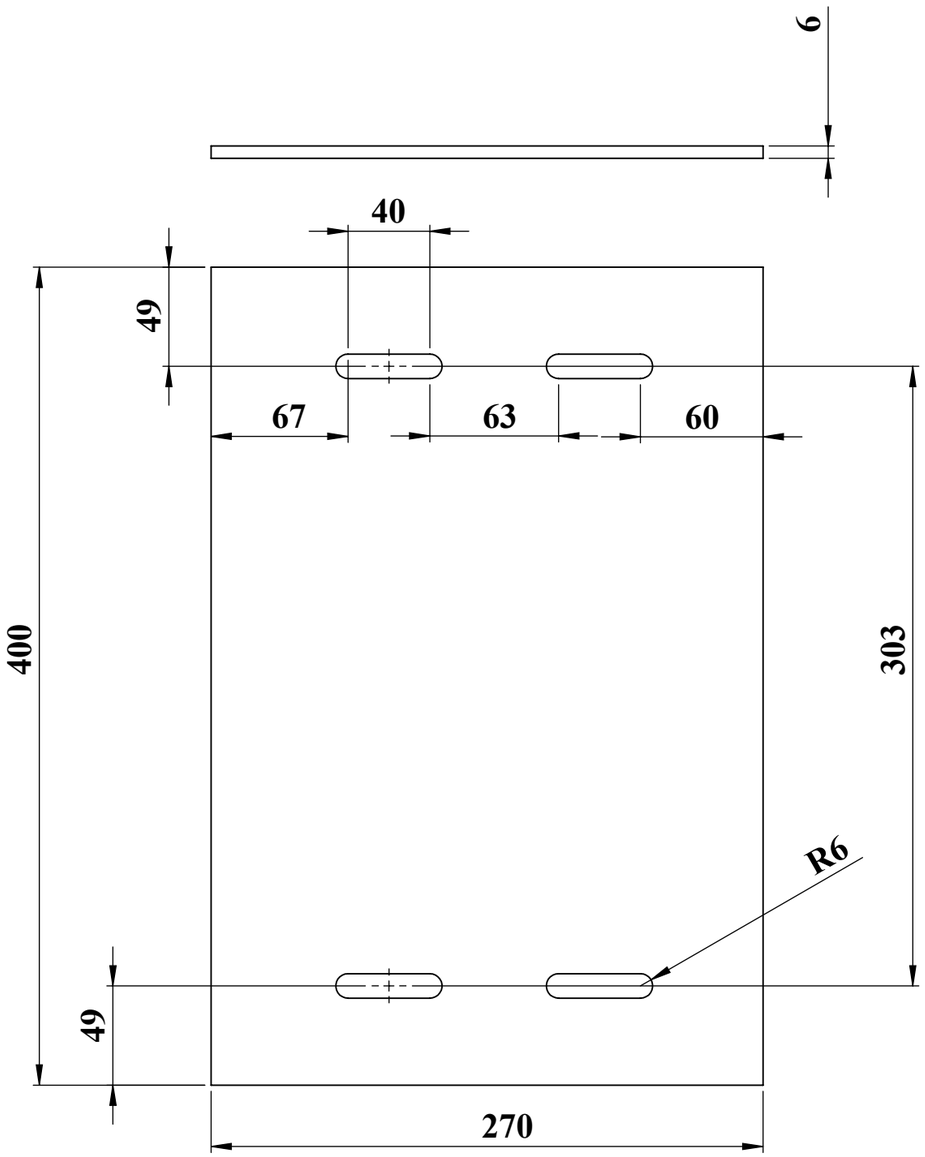

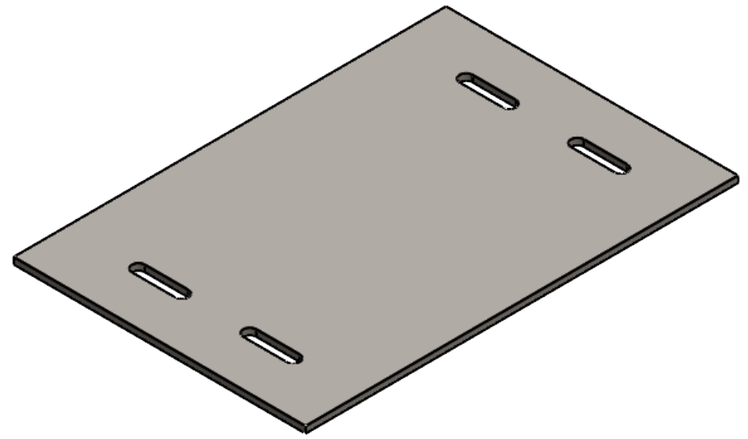

MOTOR BOTTOM PLATE-
SIZE-270 (W) X 400 (H) X 6 MM THK
QTY-3NOS

TITLE - GATE AUTOMATION				NIHVA TECHNOLOGIES PVT.LTD.PUNE Website - www.nihva.com
DWG NO - NTPL-283-PM			QTY - 1	
	NAME	SIGNATURE	DATE	PROJECT NO - NTPL-283-PM- AD
DRAWN	V.B.		17-07-2025	PRODUCT - MOTO. SLIDING GATE
CHK'D	S.W.		17-07-2025	SITE LOCATION - LUCKNOW
APPV'D	V.T.		17-07-2025	
if any queries contact - supportautomation@nihva.com				REVISION -
ALL DIMENSION ARE IN mm			A3	SCALE - SHEET 13 OF 13