

Abbrevation's:
WOW-Wall Opening Width
WOH-Wall Opening Height
UC-Under Cut
FFL-Finished Floor Level

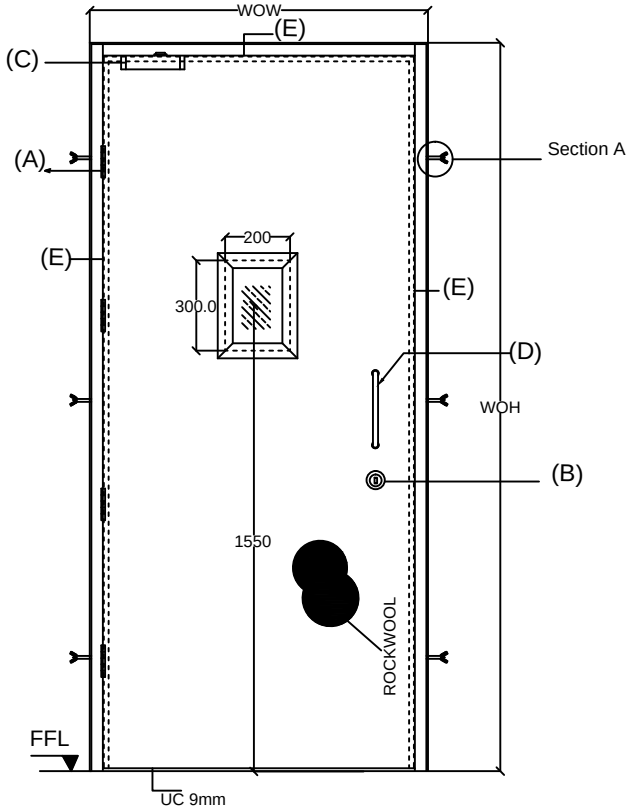

ELEVATION



TOP VIEW

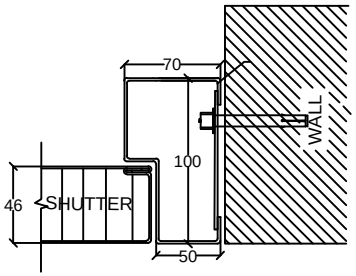

Section A

ASSESORIES DETALES

(A) HINGES: DORMA MAKE

(B) LOCK : DORMA MAKE.

(C) DOOR CLOSER: DORMA MAKE.

(D) HANDLE : 'D' HANDLE (BOTH SIDE) dia 200mmX22mm
DORMA MAKE.

Shutter thickness : 46 mm
Frame Sheet thick : 1.5mm
Shutter sheet thick : 1.2mm
Fixing : On Solid Brick plastered wall with Anchors

NOTE:- *All Dimensions are in mm.
*Tolerance:-All Linear Dimensions ±3mm,Others ±0.5mm.
*The Drawing Is For Location of Hardware only. Drawing Does Not Represent The Hardware For More Clarity, Please Go Through Hardware Broucher.

NOTE- 1. CLIENT SHOULD MENTION COLOR FOR DOOR.

COLOR
1.TRAFFIC WHITE (RAL 9016)
2.LIGHT GREY (RAL 7035)
3.GENTION BLUE (RAL 5010)

Steel door size		
WOW	WOH	QUANTITY
1000mm	2200mm	02 NOS

NOTE - 1. POLYCARBONET SHEET VISION PANEL REQ.

This drawing & designing is the property of NIHVA TECHNOLOGIES. Not be sold or copy to any other concern.

TITLE: STEEL DOOR (SINGLE LEAF)

	NAME	SIGN.	DATE
DRAWN	P.V.A		17.07.19
CHECK	V.M.T		17.07.19
APPRD.			

NIHVA TECHNOLOGIES PVT. LTD.
NIHVA TECHNOLOGY PVT. LTD. PUNE
Tel : 020 66304033
Email:- info@nihva.com
Website:-www.nihva.com

CLIENT -
PROJECT -
SITE -
If any queries contact: design@nihva.com
DWG. NO. - NIHVA/19-20/VDR/106 REV.:-R00
ALL DIMENSION ARE IN mm
SCALE: NTS WT: SHEET: 01 OF 01