
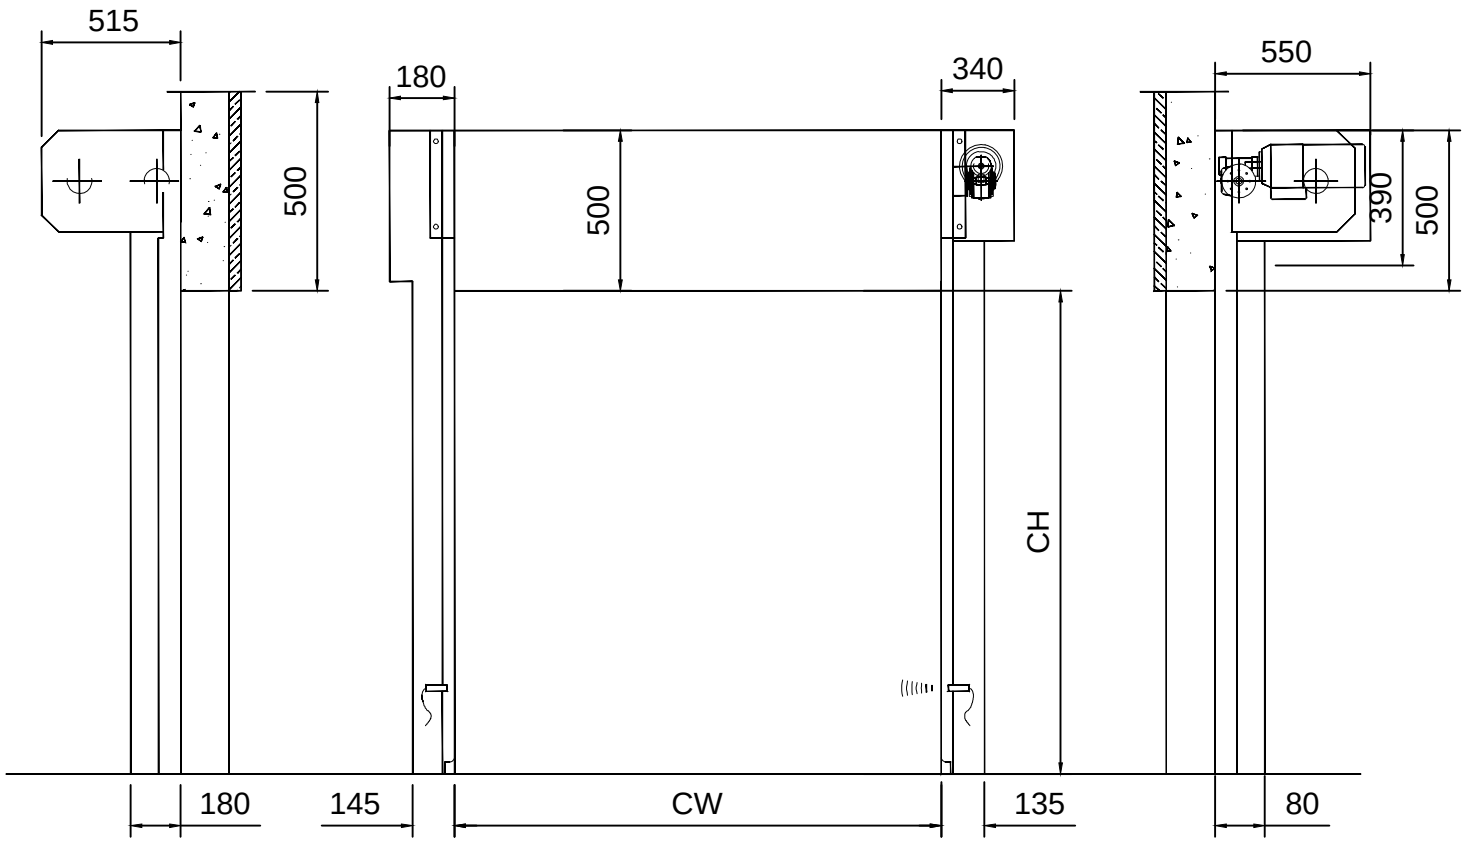


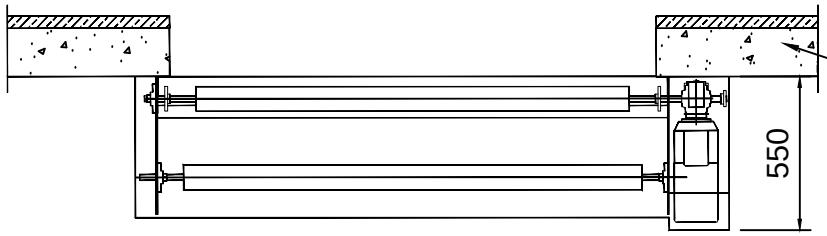

PLEASE CONFIRM
RCC / PEB STRUCTURE
FOR MOUNTING OF DOOR

SR NO	DOOR SIZE	QTY
2	3000W X 3000L	3 NOS
1	2500W X 4000L	4 NOS

This drawing & design is the property of NIHVA TECHNOLOGIES. Not to be sold or copied to any other concern.

TITLE
HIGH SPEED DOOR HS9010PFR

	NAME	SIGN	DATE
DRAWN	P.V.A		23.08.19
CHECK	V.M.T		23.08.19

If any queries contact : projects@nihva.com

ALL DIMENSION ARE IN mm

NIHVA TECHNOLOGIES PVT. LTD.
NIHVA TECHNOLOGIES PVT. LTD. PUNE
Tel : 020 66304033
Email:- info@nihva.com
Website:- www.nihva.com

CLIENT - MHD LOGISTICS
PROJECT - GOVT. POULTRY FARM PROJECT
SITE - OMAN
DWG. NO. : NIHVA/19-20/0081
SCALE: NTS | WT: | SHEET: 01 OF 01