Revision		Date	By
A	Corrected mullion hoist positions, floor pits altered	2022-09-02	EB
B	New measurements, doors redrawn	2022-10-11	EB

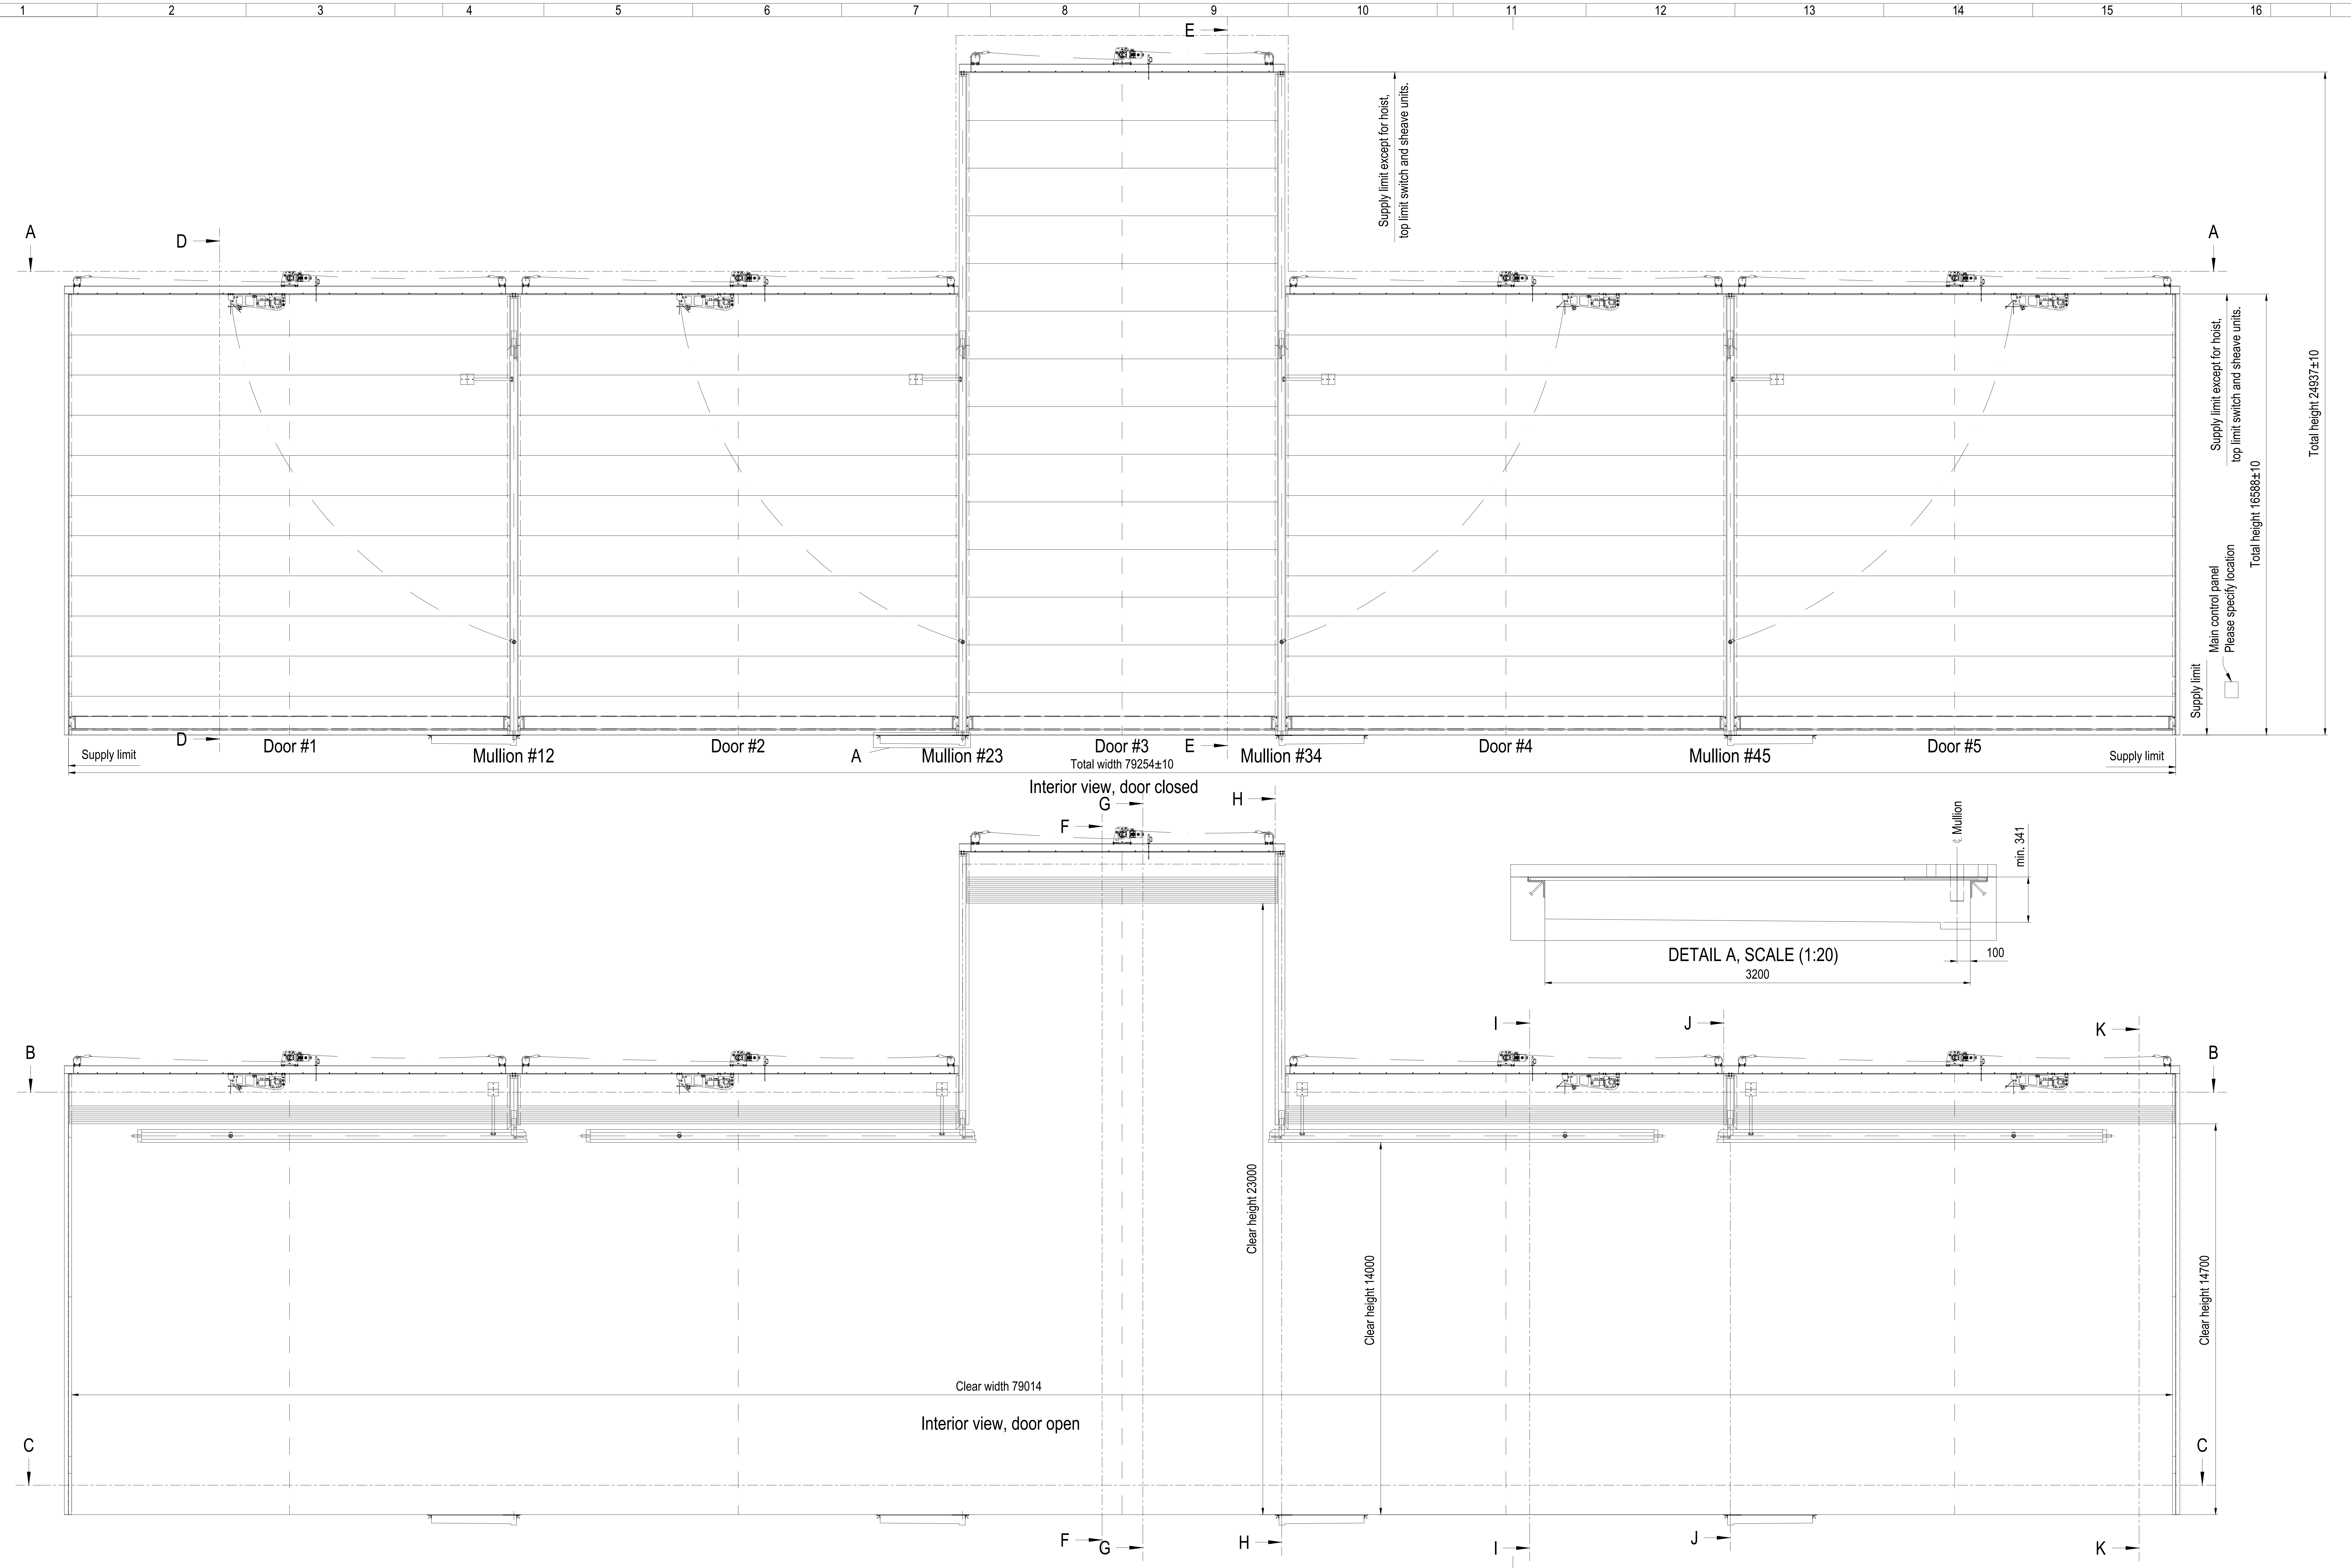

Interior view, door closed

Interior view, door open

DETAIL A, SCALE (1:20)

5.9T/27 Door #3

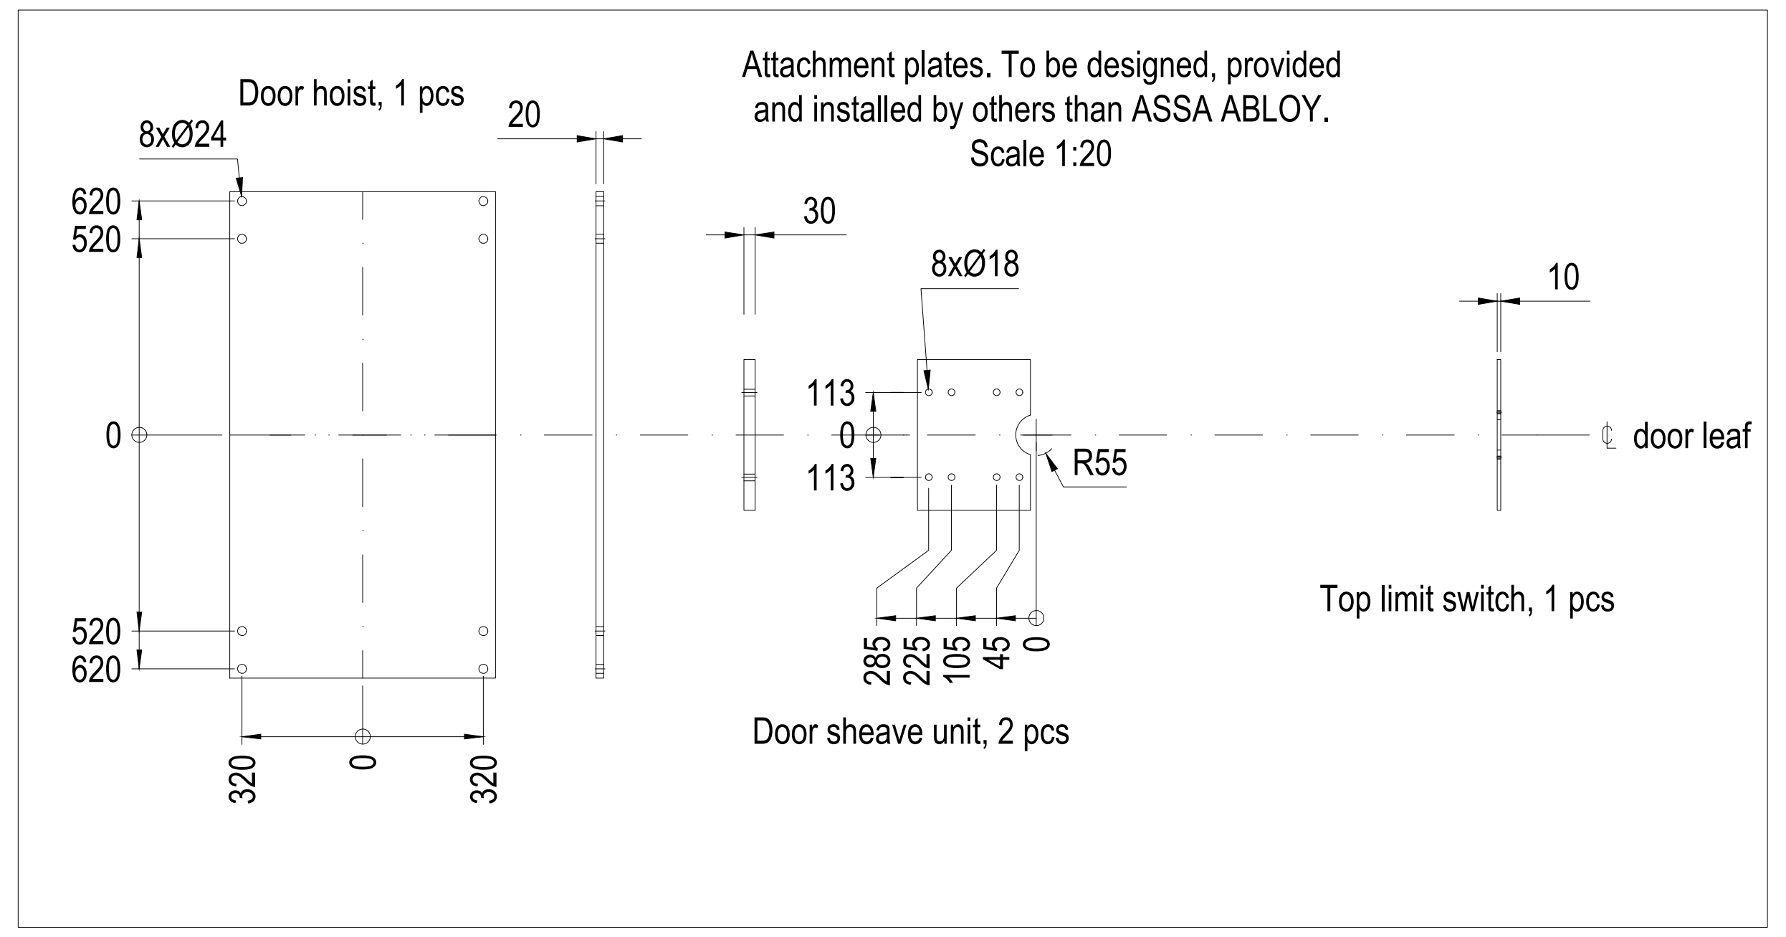

Attachment plates. To be designed, provided and installed by others than ASSA ABLOY. Scale 1:20

4.9T/27 Door #1, 2, 4 & 5

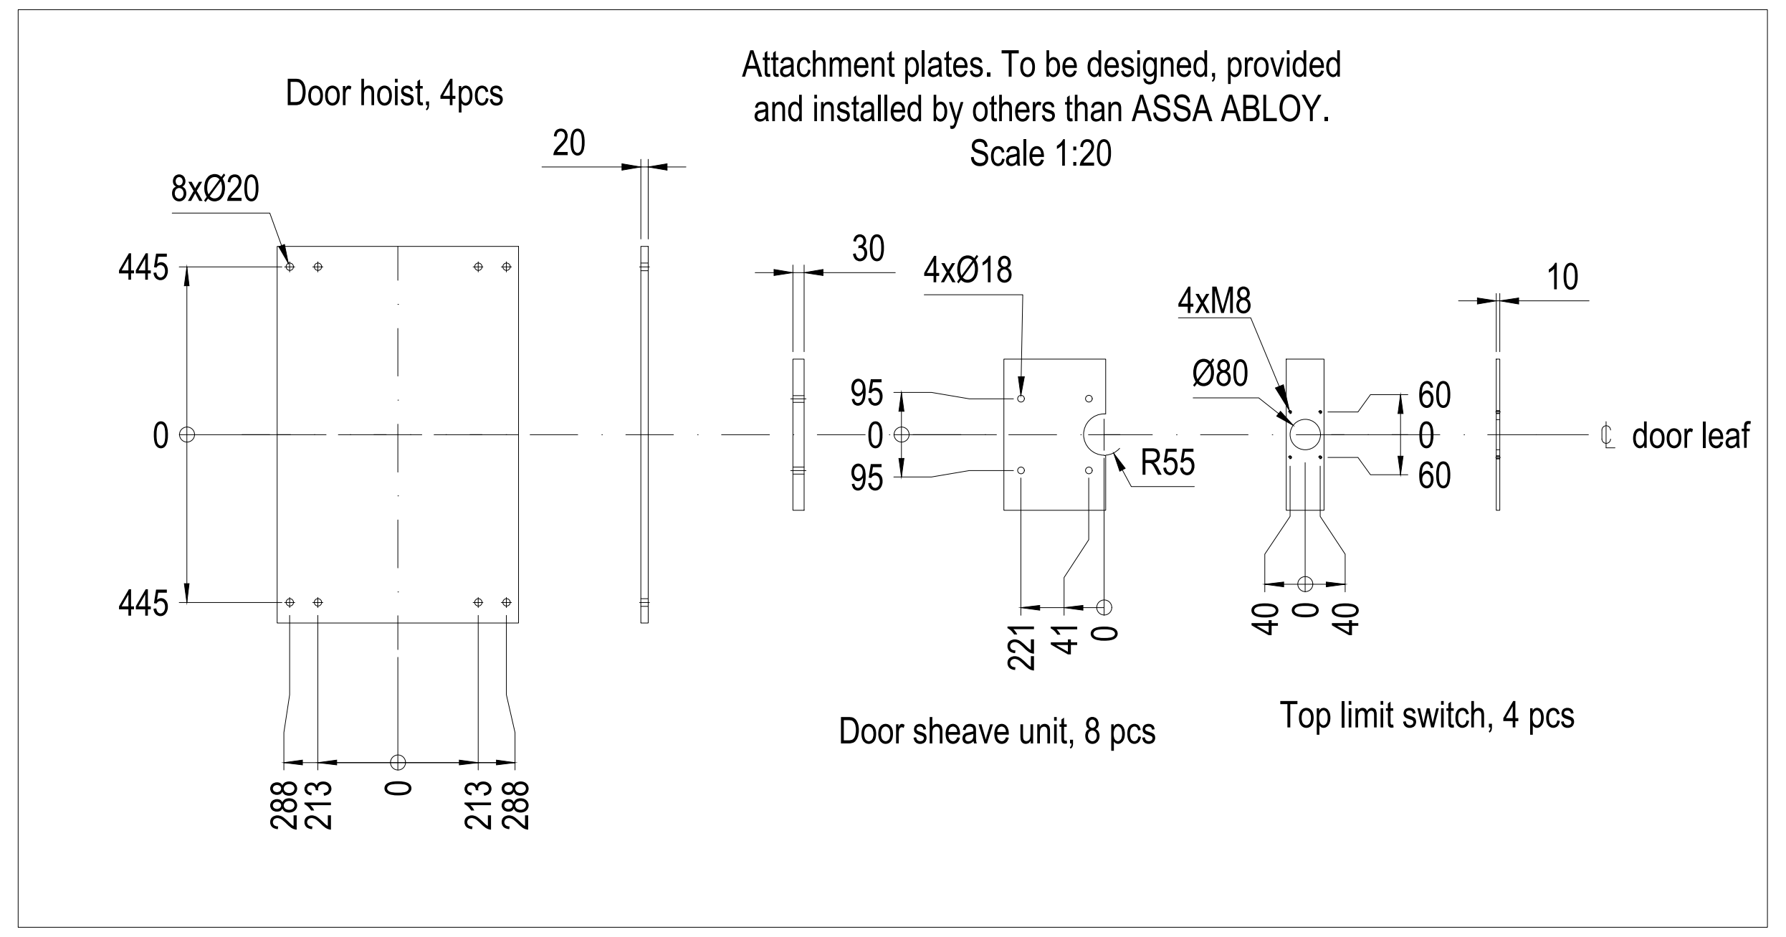

Attachment plates. To be designed, provided and installed by others than ASSA ABLOY. Scale 1:20

DOOR IDENTITY NUMBER: 84800001

LOAD DIAGRAM & NOTES, ref. to drwng. no. 77446

INTERFACE, SECTIONS ref. to drwng. no. 77445

INTERFACE, PLAN VIEWS ref. to drwng. no. 77444

DESIGNED	SIZE	SCALE	
EB	A1F	1:100	GMR Aero Technic Hangar1 India Megadoor 79014x23000/14000 Interface, Elevation
CODE 84800	If not otherwise stated:		PLOT DATE
ITEM NO	Tolerances ISO 2768-m EN ISO 13920-B		
DATE 2022-08-23	Cutting class ISO 9013-442 Weld class ISO 5817-C		
ASSA ABLOY	Surface finish Smooth raw surface	DRAWING NO 77443	REVISION B

This document is the property of ASSA ABLOY Entrance Systems AB and shall not without our written permission be copied, imparted to a third party or used for any other unauthorized purpose.