




ELEVATION

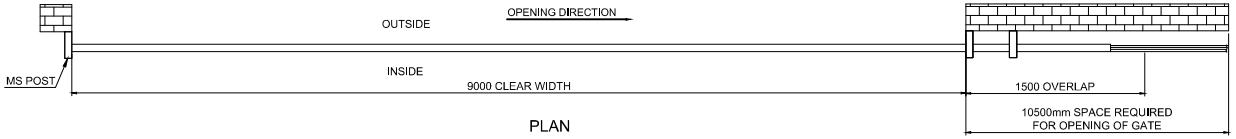

PLAN

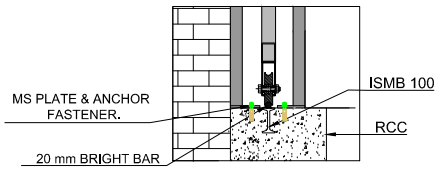

DETAIL VIEW OF A

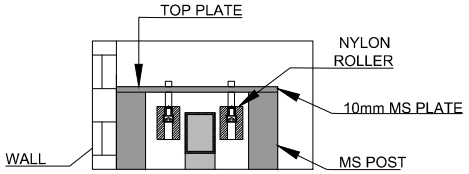

DETAIL VIEW OF B

REV.	DESCRIPTION	DRAWN	DATE
R01	GATE TYPE CHANGE	A.K.K.	06.05.2019

SR.NO	RAL CODE	RAL COLOR
04	RAL 7035	LIGHT GREY
03	RAL 5002	ULTRAMARINE BLUE
02	RAL 9002	GREY WHITE
01	RAL 1004	GOLDEN YELLOW

DIMENSION :

CLEAR WIDTH	CLEAR HEIGHT	QUANTITY
9000 mm	1800mm	1 NOS

MATERIAL: MS

THICKNESS :

NOTE-
1. ALL REQUIRED CIVIL WORK WILL BE IN CLIENTS SCOPE.
2. IN NECESSARY GATE LEAF WILL BE IN TWO PARTS FOR TRANSPORTATION AND WILL BE WELDED TOGETHER ON SITE.

TOLERANCE:- ± 05mm

NIHVA TECHNOLOGIES PVT. LTD.
NIHVA TECHNOLOGIES PVT. LTD. PUNE
Website:- www.nihva.com
Email:- info@nihva.com
TEL :020 66304033

TITLE:

MANUAL SINGLE LEAF SLIDING GATE

CLIENT'S APPROVAL :

CLIENT - INDAMER TECHNICS PVT. LTD.

PROJECT -

SITE LOCATION -

DWG. NO. : NIHVA/18-19/0197/R01		REV. : 01
SCALE: NTS	WT:	SHEET:1 OF 1

DRAWN	SURAJ		08-12-2018
CHECK	PRADEEP		08-12-2018
APPROVED	R.D		08-12-2018

IF ANY QUERIES CONTACT:- design@nihva.com

NOTE: ALL DIMENSIONS ARE IN mm

THIS DRAWING & DESIGN IS THE PROPERTY OF NIHVA TECHNOLOGIES. NOT TO BE SOLD OR COPIED TO ANY OTHER CONCERN.