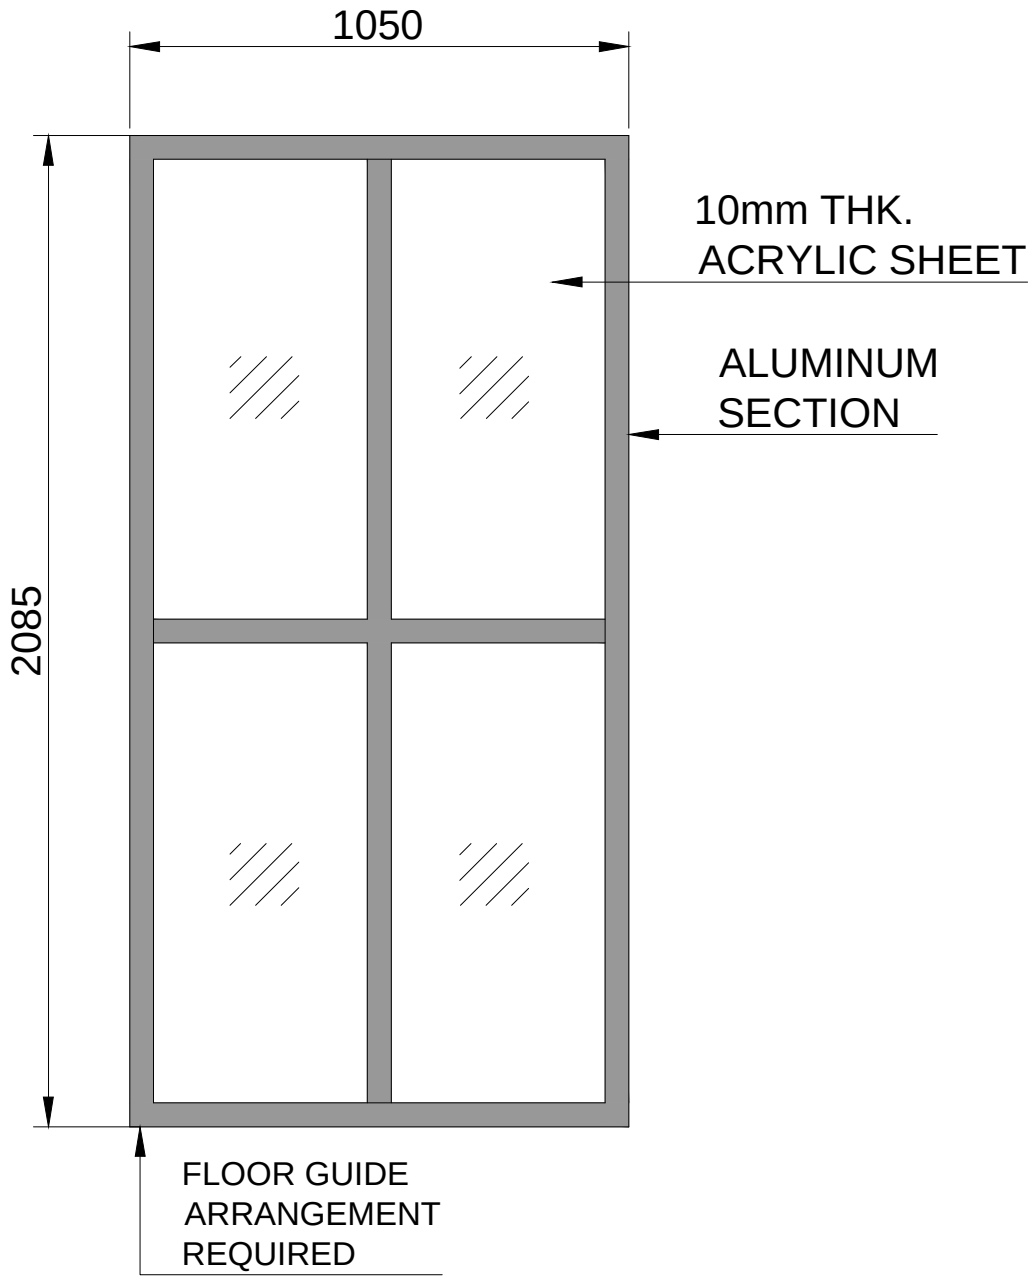

This drawing & design is the property of NIHVA TECHNOLOGIES. Not to be sold or copied to any other concern.

TITLE

SLIDING DOOR LEAF

CLIENT APPROVAL

ALL DIMENSION ARE IN mm

	SIGN	DATE
DRAWN	OMKAR	08/11/17
CHECK	SHEKHAR	08/11/17
REV.		
APPRD.	SHEKHAR	08/11/17
MFG		
Ref. No.		

NIHVA TECHNOLOGIES PVT. LTD.

NIHVA TECHNOLOGIES PVT. LTD. PUNE
Tel : 020 66304033
Email:- info@nihva.com
Website:- www.nihva.com

CLIENT -

PROJECT -

SITE -

DWG. NO. - NIHVA/17-18/VDR/0176 | REV-0

SCALE: NTS | WT: | SHEET: 01 OF 01

If any queries contact : projects@nihva.com