

230 V & 50 Hz
Single phase supply
Required near left side
of Operator.

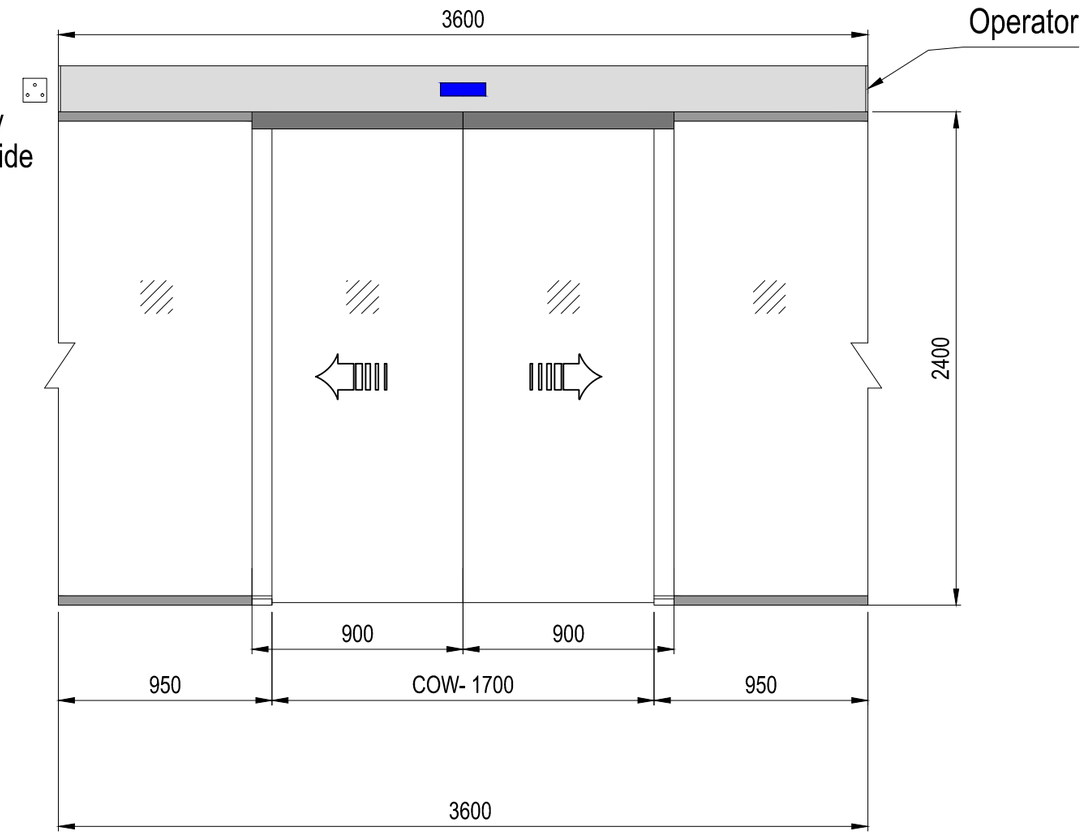

Inside Elevation

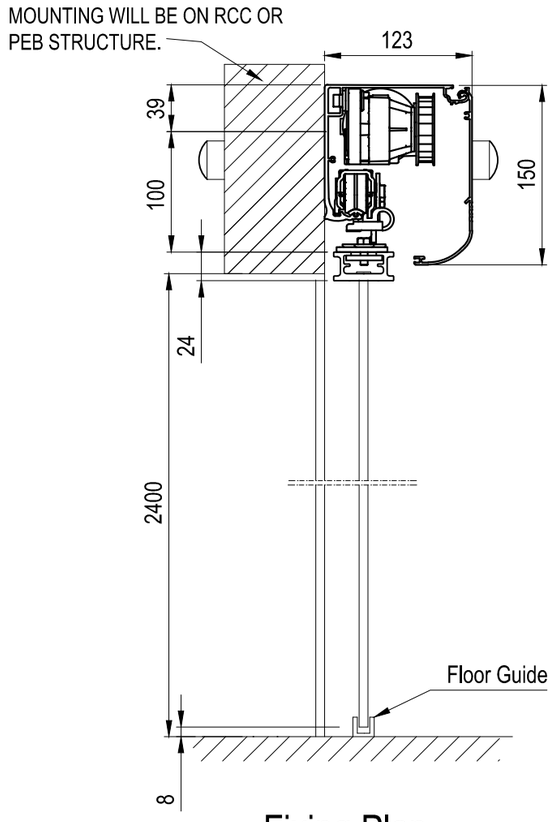

Fixing Plan

Glass Type- 10mm Toughened

Door Size				
Sr. No.	Total Width	Clear Width	Clear Height	Quantity
1	3600	1700	2400	1

This drawing & designing is the property of NIHVA TECHNOLOGIES. Not to be sold or copied to any other concern.

TITLE	AUTOMATIC SLIDING GLASS DOOR		
	Name	SIGN	DATE
DRAWN	Suraj		26-12-18
CHECK	Vikrant		26-12-18
APPROVAL	R.D		26-12-18
If any queries contact : design@nihva.com			
ALL DIMENSION ARE IN mm			

NIHVA TECHNOLOGIES PVT. LTD.
NIHVA TECHNOLOGIES PVT. LTD. PUNE
Tel : 020 66304033
Email:- info@nihva.com
Website:- www.nihva.com

CLIENT - RAJSHREE CONSTRUCTION CONSORTIUM.
PROJECT- WALLMART
SITE - NIJAMABAD
DWG. NO. : NIHVA/18-19/0219 REV.=00
SCALE: NTS WT: SHEET: 01 OF 01