

DRAWING

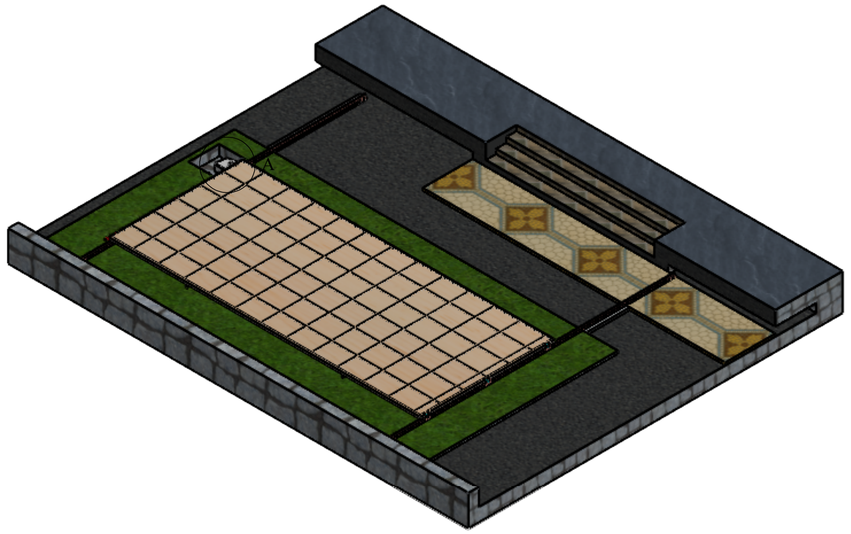






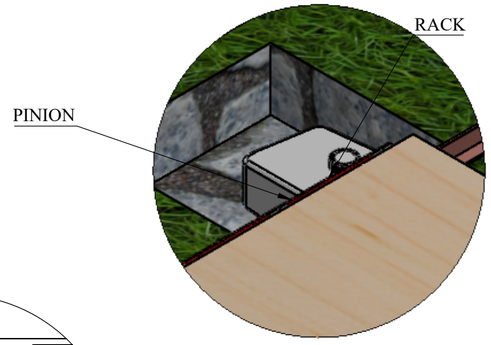

DETAIL A
SCALE 1 : 10

MOTOR
PINION+RACK

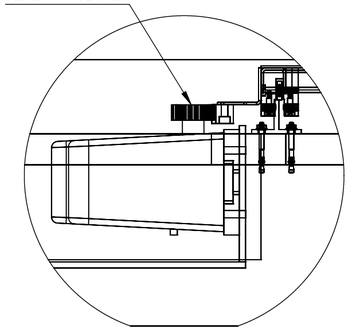

DETAIL B
SCALE 1 : 7



REV DESCRIPTION	DATE	REV NO
	25-08-2025	REV 00
1.		

NOTE :

Main Assembly

SPECIAL INSTRUCTION'S :

TITLE - SWIMMING POOL ENCLOSER

DWG NO - NTPL-294-PM-001-00-00-00

NIHVA TECHNOLOGIES PVT.LTD.PUNE
Website - www.nihva.com

	NAME	SIGNATURE	DATE
DRAWN	V.W.		25-08-2025
CHK'D	B.S.		29-08-2025
APPV'D	V.T.		30-08-2025

PRODUCT - SWIMMING POOL DECK

PROJECT NO - NTPL-294-PM | REVISION - 00

SITE LOCATION - PUNE | WEIGHT -

MATRIAL - | QTY - 1

If any queries contact - Design@nihva.com


PROJECTION METHOD:


SCALE :

ALL DIMENSION ARE IN mm | A2

DRAWING

ITEM NO.	PART NUMBER	DESCRIPTION	QTY.
1	LIFT TRACK -(T GUIDE) , SIZE -50X50X8 MM THK		2
2	PANEL ASM WITH BEARING BLOCK		1
3	closing sheet...		2
4	CLOSING SHEET 2...		2
5	Chemical Anchor Bolt_M8x100 MM L	Anker_M8x80	16
6	MOTOR MOUNTING ASM		1
7	50 mm Caster Wheel - Copy - Copy		4
8	CIVIL BASE.._.		1

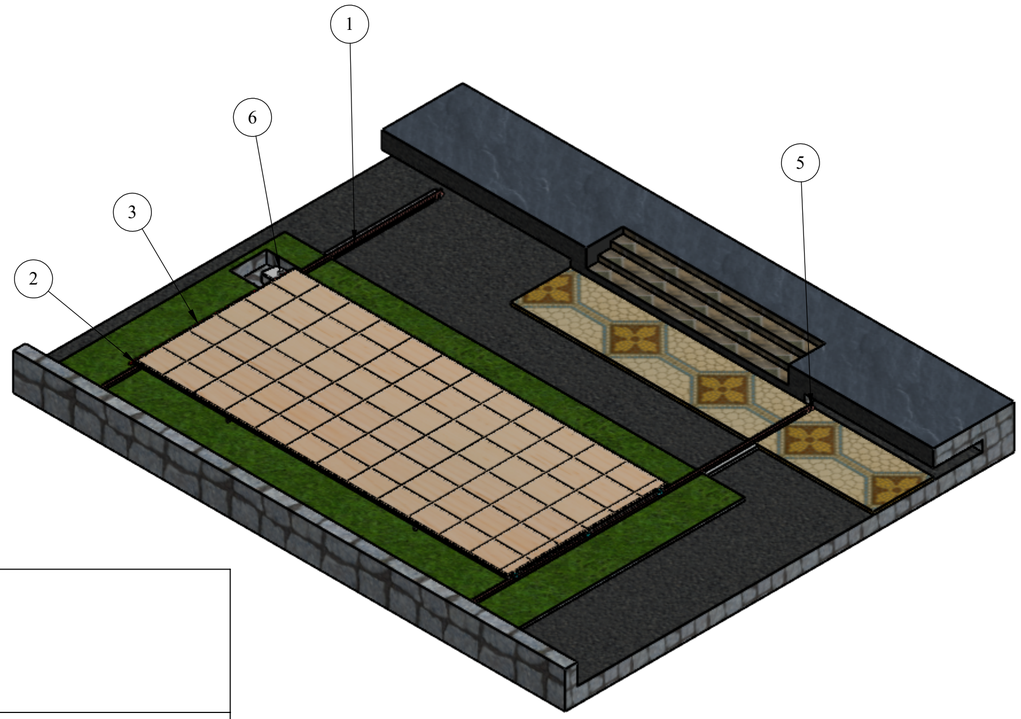

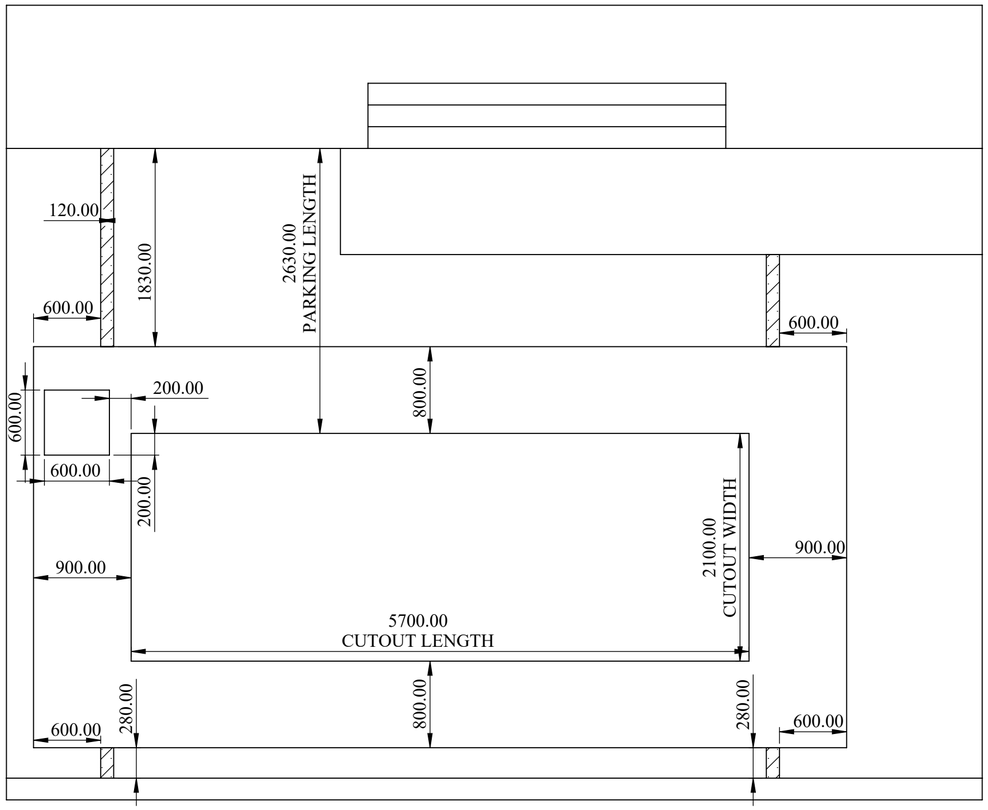

REV DESCRIPTION	DATE	REV NO
	25-08-2025	REV 00
1.		

NOTE :

Main Assembly

SPECIAL INSTRUCTION'S :

TITLE - SWIMMING POOL ENCLOSER

DWG NO - NTPL-294-PM-001-00-00-00

NIHVA Technologies Pvt. Ltd.

NIHVA TECHNOLOGIES PVT.LTD.PUNE
Website - www.nihva.com

	NAME	SIGNATURE	DATE
DRAWN	V.W.		25-08-2025
CHK'D	B.S.		29-08-2025
APPV'D	V.T.		30-08-2025

PRODUCT - SWIMMING POOL DECK

PROJECT NO - NTPL-294-PM | REVISION - 00

SITE LOCATION - PUNE | WEIGHT -

MATRIAL - | QTY - 1


If any queries contact - Design@nihva.com


ALL DIMENSION ARE IN mm | A2

PROJECTION METHOD:


SCALE :

DRAWING

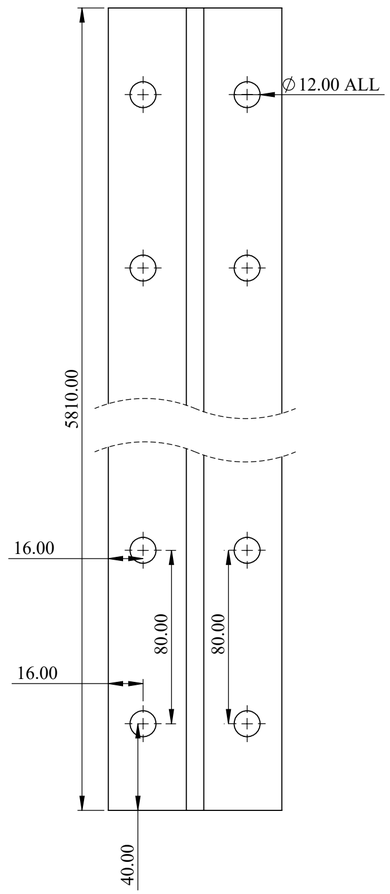

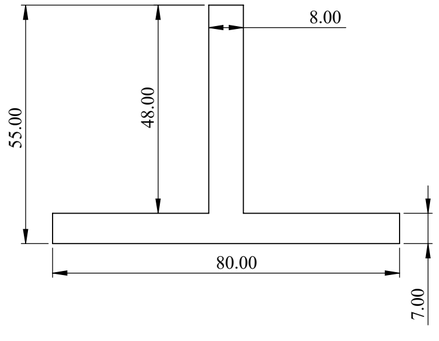

ITEM NO.	PART NUMBER	DESCRIPTION	QTY.
1	LIFT TRACK -(T GUIDE) , SIZE - 50X50X8 MM THK		2

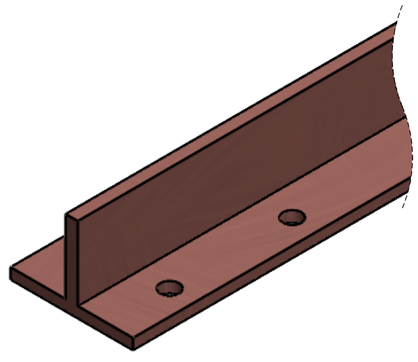

REV DESCRIPTION	DATE	REV NO
	25-08-2025	REV 00
1.		

NOTE :

Name: Lift Track
Size : T-GUIDE, 80x55x8 mm
Mtl : SS
Qty : 02 No's

SPECIAL INSTRUCTION'S :

TITLE - SWIMMING POOL ENCLOSER

DWG NO - NTPL-294-PM-001-00-00-00

NIHVA Technologies Pvt. Ltd.


NIHVA TECHNOLOGIES PVT.LTD.PUNE
Website - www.nihva.com

	NAME	SIGNATURE	DATE
DRAWN	V.W.		25-08-2025
CHK'D	B.S.		29-08-2025
APPV'D	V.T.		30-08-2025

PRODUCT - SWIMMING POOL DECK
PROJECT NO - NTPL-294-PM | REVISION - 00
SITE LOCATION - PUNE | WEIGHT -
MATRIAL - | QTY - 1
If any queries contact - Design@nihva.com | PROJECTION METHOD: | SCALE :
ALL DIMENSION ARE IN mm | A2 | SHEET 3 OF 19

DRAWING

ITEM NO.	PART NUMBER	DESCRIPTION	QTY.
1	PANEL...	SS	1
2	BEARING BLOCK ASM - T45-A		6
3	SS PLATE 6100 X 2630 X 3 MM THK...	SS	1
4	RACK...	STD (M4 RACK, 30x8x1000 mm, ZINC COATED WITH SPACERS AND SCREWS.)	2
5	RACK CUT PART...	STD (M4 RACK, 30x8x1000 mm, ZINC COATED WITH SPACERS AND SCREWS.)	1
6	RACK SUPPORT PLATE 50x87.85x4mm thk	ss	8

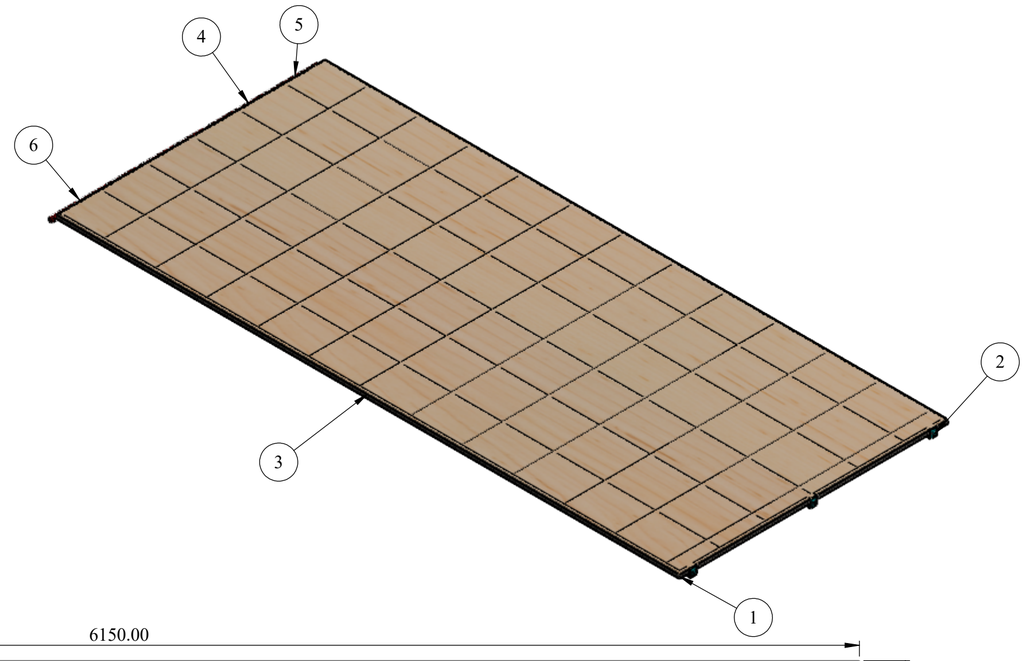



REV DESCRIPTION	DATE	REV NO
	25-08-2025	REV 00
1.		

NOTE :

Name : Panel ASM

SPECIAL INSTRUCTION'S :

TITLE - SWIMMING POOL ENCLOSER

DWG NO - NTPL-294-PM-001-00-00-00

NIHVA Technologies Pvt. Ltd.

NIHVA TECHNOLOGIES PVT.LTD.PUNE
Website - www.nihva.com

	NAME	SIGNATURE	DATE
DRAWN	V.W.		25-08-2025
CHK'D	B.S.		29-08-2025
APPV'D	V.T.		30-08-2025

PRODUCT - SWIMMING POOL DECK

PROJECT NO - NTPL-294-PM | REVISION - 00

SITE LOCATION - PUNE | WEIGHT -

MATRIAL - | QTY - 1

If any queries contact - Design@nihva.com

ALL DIMENSION ARE IN mm | A2


PROJECTION METHOD:

SCALE :

DRAWING

ITEM NO.	PART NUMBER	DESCRIPTION	QTY.
1	PANEL...	SS	1

REV DESCRIPTION	DATE	REV NO
	25-08-2025	REV 00
1.		

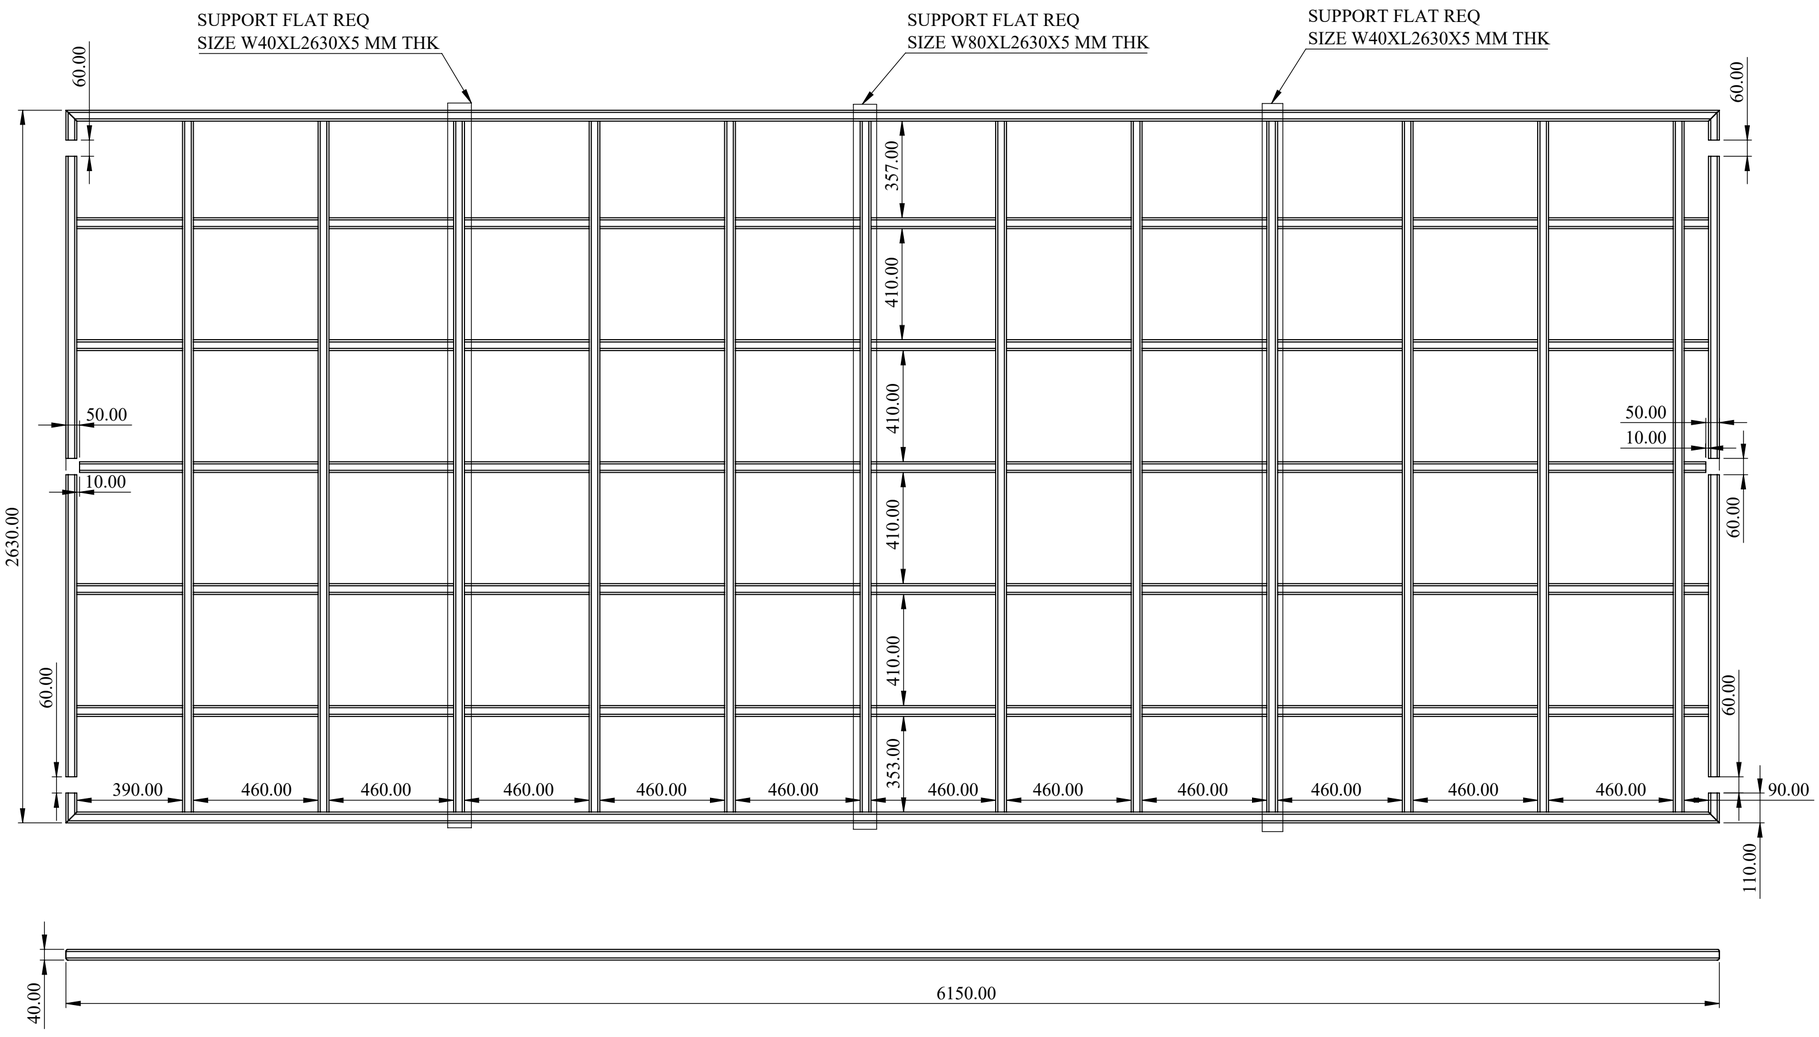

NOTE :

Name : Deck Panel
Mtl : SS
Size : 2630X6100 mm L

SPECIAL INSTRUCTION'S :

TITLE - SWIMMING POOL ENCLOSER

DWG NO - NTPL-294-PM-001-00-00-00

NIHVA Technologies Pvt. Ltd.

NIHVA TECHNOLOGIES PVT.LTD.PUNE
Website - www.nihva.com

	NAME	SIGNATURE	DATE	
				PRODUCT - SWIMMING POOL DECK
DRAWN	V.W.		25-08-2025	PROJECT NO - NTPL-294-PM / REVISION - 00
CHK'D	B.S.		29-08-2025	SITE LOCATION - PUNE / WEIGHT -
APPV'D	V.T.		30-08-2025	MATRIAL - / QTY - 1


If any queries contact - Design@nihva.com

ALL DIMENSION ARE IN mm | A2


PROJECTION METHOD:


SCALE :


DRAWING

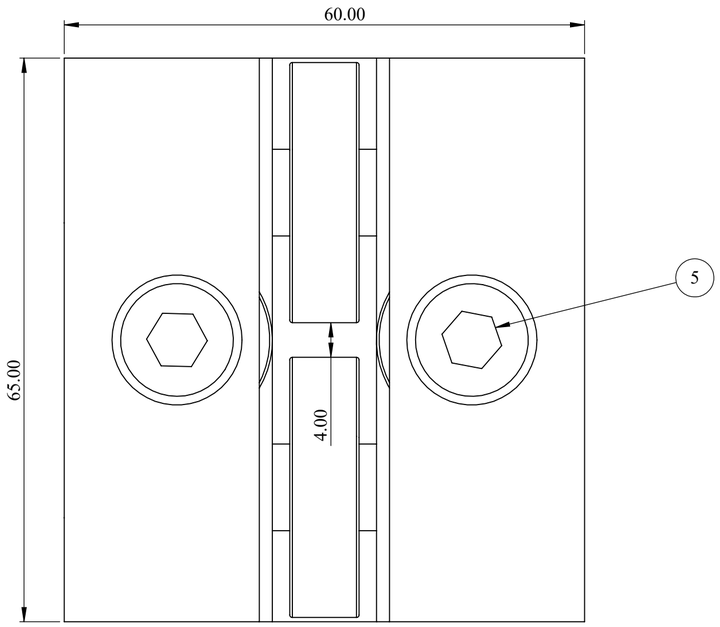

ITEM NO.	PART NUMBER	DESCRIPTION	QTY.
1	BEARING BLOCK (T-GUIDE)	68X60X50 MM (VMC PART)	1
2	SKF BALL BEARING SKF 6000-2Z/C3		2
3	SHOULDER BOLT 10 X 50 MM L	SS	2
4	SKF BALL BEARING 8 SIZE 8X19X7 MM THK	SS	2
5	SHOULDER BOLT 8 X 40 MM L	SS	2

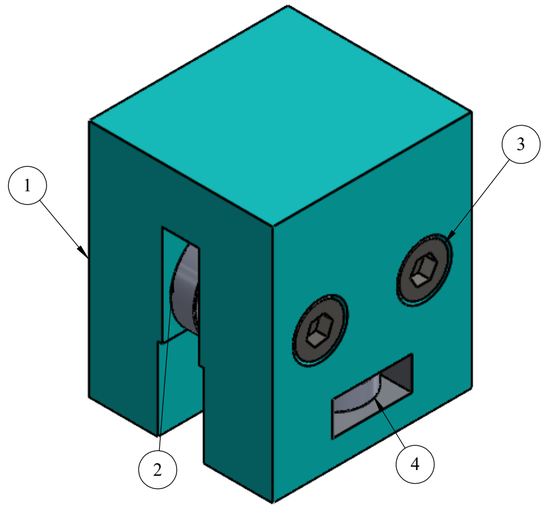

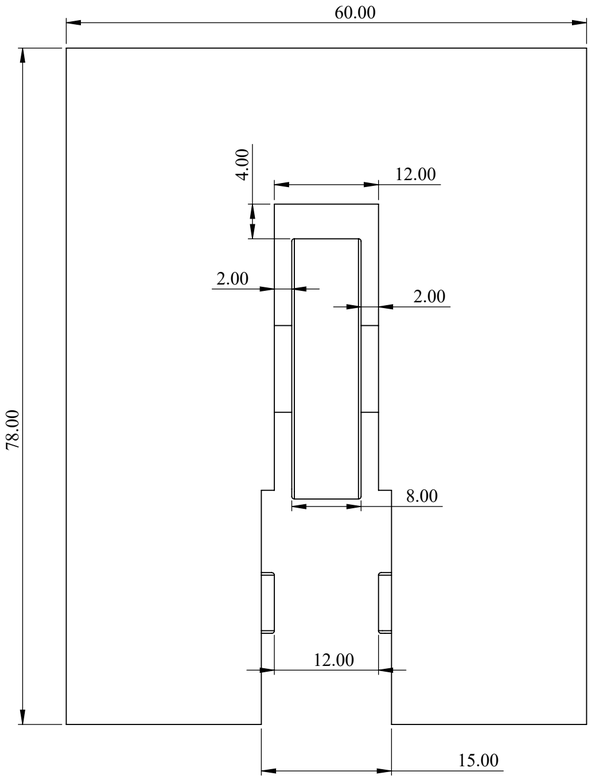

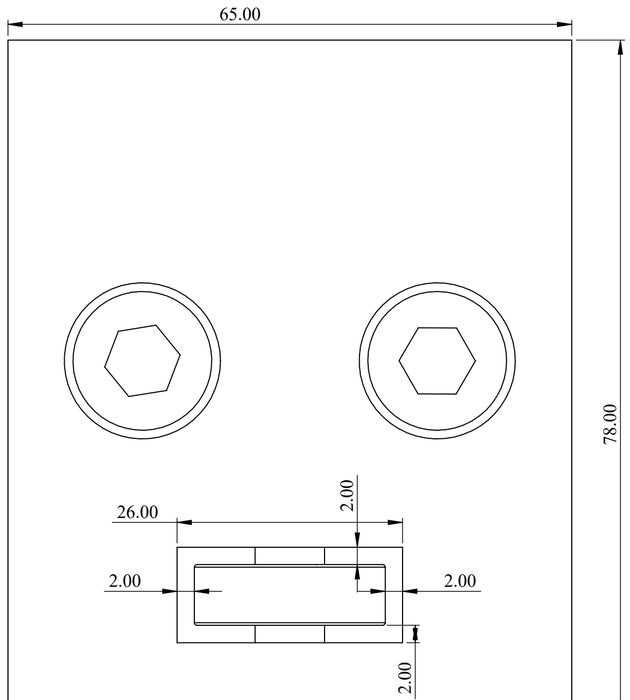

REV DESCRIPTION	DATE	REV NO
	25-08-2025	REV 00
1.		

NOTE :

Name : Bearing Block ASM
Qty : 06 No's

SPECIAL INSTRUCTION'S :

TITLE - SWIMMING POOL ENCLOSER

DWG NO - NTPL-294-PM-001-00-00-00


NIHVA TECHNOLOGIES PVT.LTD.PUNE
Website - www.nihva.com


	NAME	SIGNATURE	DATE
DRAWN	V.W.		25-08-2025
CHK'D	B.S.		29-08-2025
APPV'D	V.T.		30-08-2025

PRODUCT - SWIMMING POOL DECK
PROJECT NO - NTPL-294-PM
REVISION - 00
SITE LOCATION - PUNE
WEIGHT -
MATRIAL -
QTY - 1
SCALE :
PROJECTION METHOD:

If any queries contact - Design@nihva.com
ALL DIMENSION ARE IN mm
A2

DRAWING

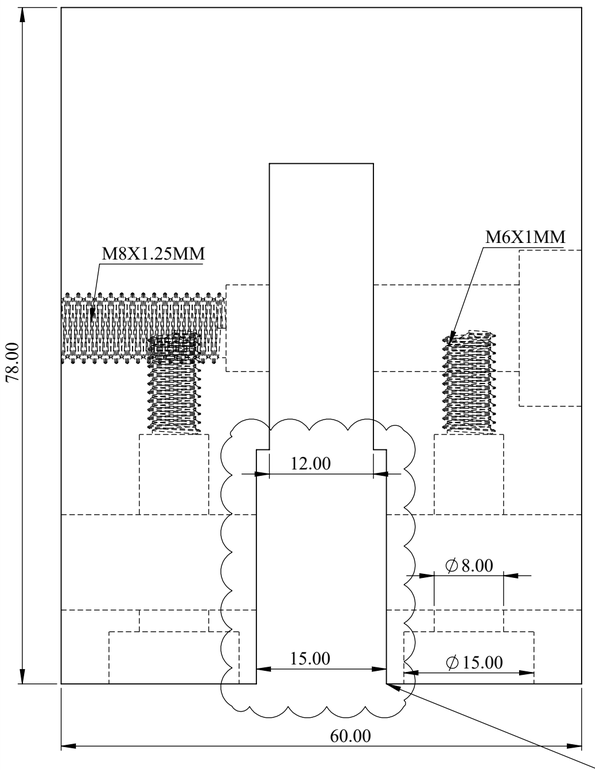


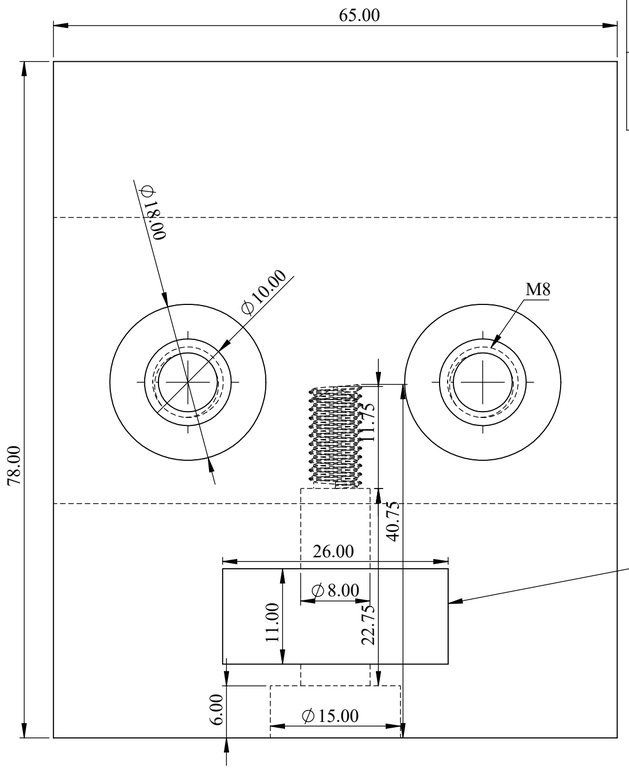

POCKET WIDTH CHANGE


SLOT SIZE INCRESED
12 MM TO 15 MM

OVERALL DIMENSIONS
INCRESED 50X60X68 MM TO
60X65X78

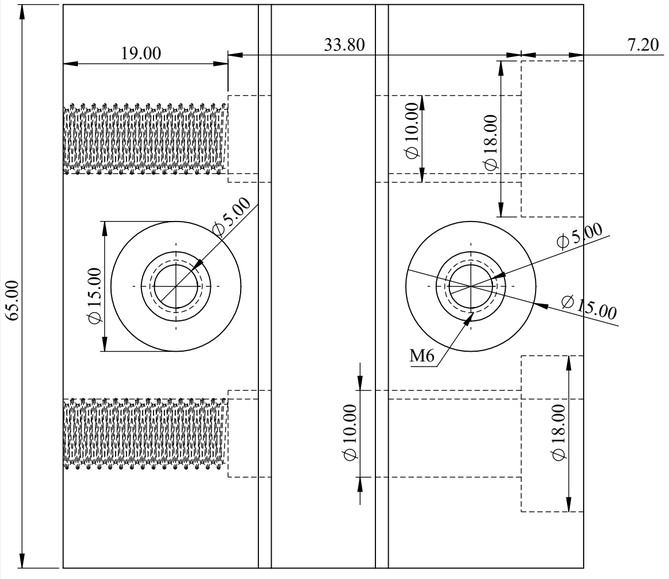

ITEM NO.	PART NUMBER	DESCRIPTION	QTY.
1	BEARING BLOCK (T-GUIDE)	68X60X50 MM (VMC PART)	06

REV DESCRIPTION	DATE	REV NO
	25-08-2025	REV 00
1.		

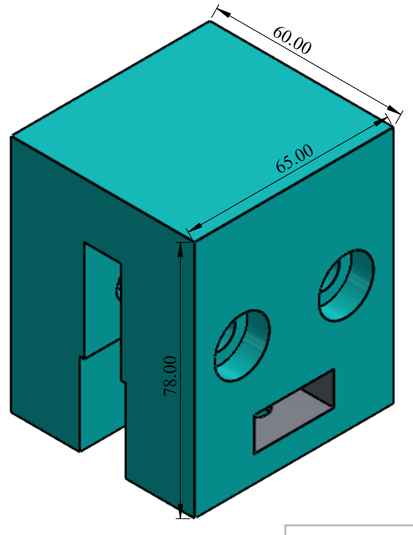

NOTE :

Name: Bearing Block
Size : 68X60X50 (VMC MACHININING)
Mtl : SS
Qty : 06 no's.

SPECIAL INSTRUCTION'S :

TITLE - SWIMMING POOL ENCLOSER

DWG NO - NTPL-294-PM-001-00-00-00

NIHVA TECHNOLOGIES PVT.LTD.PUNE
Website - www.nihva.com


	NAME	SIGNATURE	DATE	
				PRODUCT - SWIMMING POOL DECK
DRAWN	V.W.		25-08-2025	PROJECT NO - NTPL-294-PM / REVISION - 00
CHK'D	B.S.		29-08-2025	SITE LOCATION - PUNE / WEIGHT -
APPV'D	V.T.		30-08-2025	MATRIAL - / QTY - 1

If any queries contact - Design@nihva.com
ALL DIMENSION ARE IN mm | A2
PROJECTION METHOD:
SCALE :

DRAWING

ITEM NO.	PART NUMBER	DESCRIPTION	QTY.
1	SKF BALL BEARING SKF 6000-2Z/C3		8

REV DESCRIPTION	DATE	REV NO
	25-08-2025	REV 00
1.		

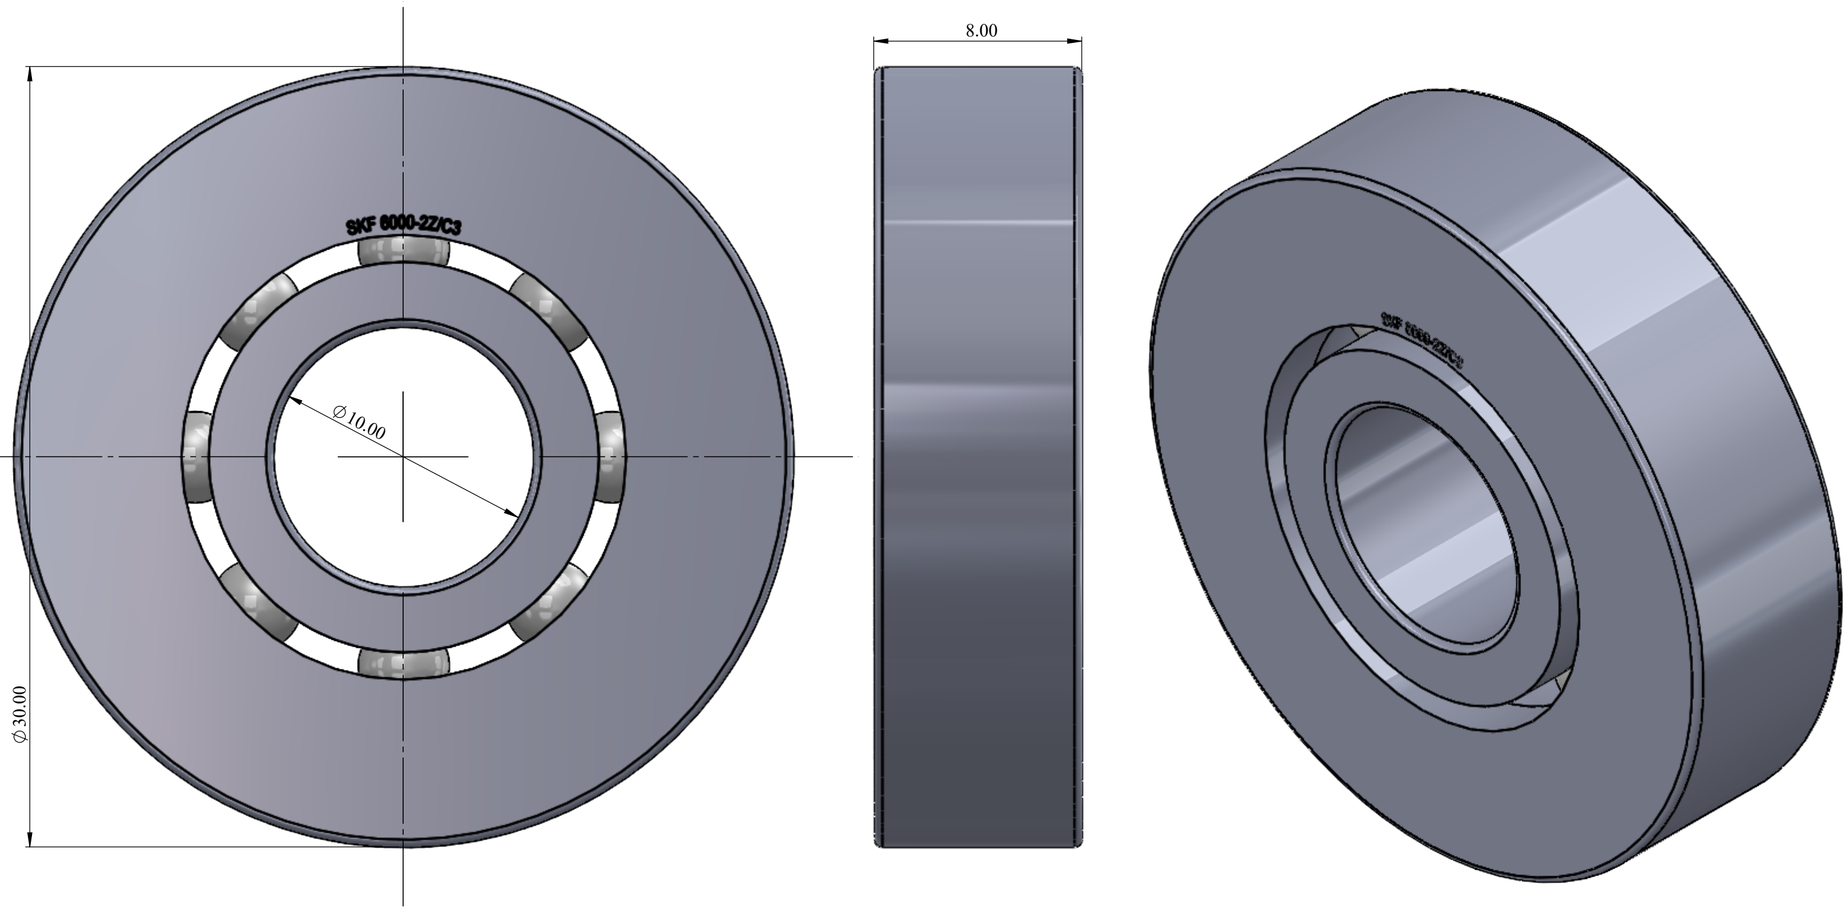

NOTE :

Name: SKF 6000-2Z/C3
Size : 10X26X8 MM THK
Qty : 12 No's.

SPECIAL INSTRUCTION'S :

TITLE - SWIMMING POOL ENCLOSER

DWG NO - NTPL-294-PM-001-00-00-00


NIHVA TECHNOLOGIES PVT.LTD.PUNE
Website - www.nihva.com


	NAME	SIGNATURE	DATE		
DRAWN	V.W.		25-08-2025	PRODUCT - SWIMMING POOL DECK	
CHK'D	B.S.		29-08-2025	PROJECT NO - NTPL-294-PM	REVISION - 00
APPV'D	V.T.		30-08-2025	SITE LOCATION - PUNE	WEIGHT -
				MATRIAL -	QTY - 1
If any queries contact - Design@nihva.com				PROJECTION METHOD:	SCALE :
ALL DIMENSION ARE IN mm			A2		SHEET 8 OF 19


DRAWING

REV DESCRIPTION	DATE	REV NO
	25-08-2025	REV 00
1.		

ITEM NO.	PART NUMBER	DESCRIPTION	QTY.
1	SHOULDER BOLT 10 X 50 MM L	SS	8

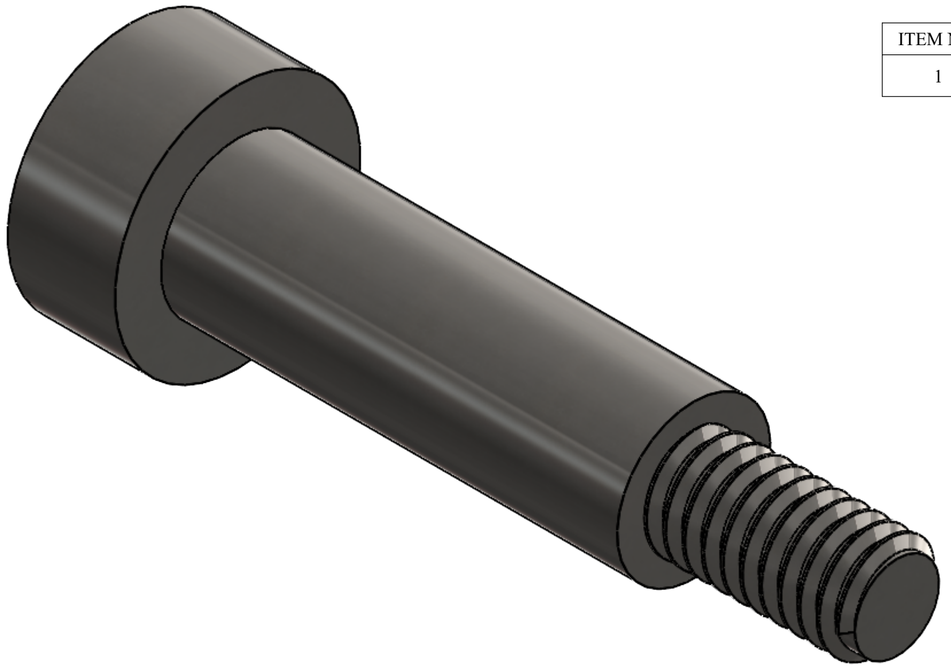

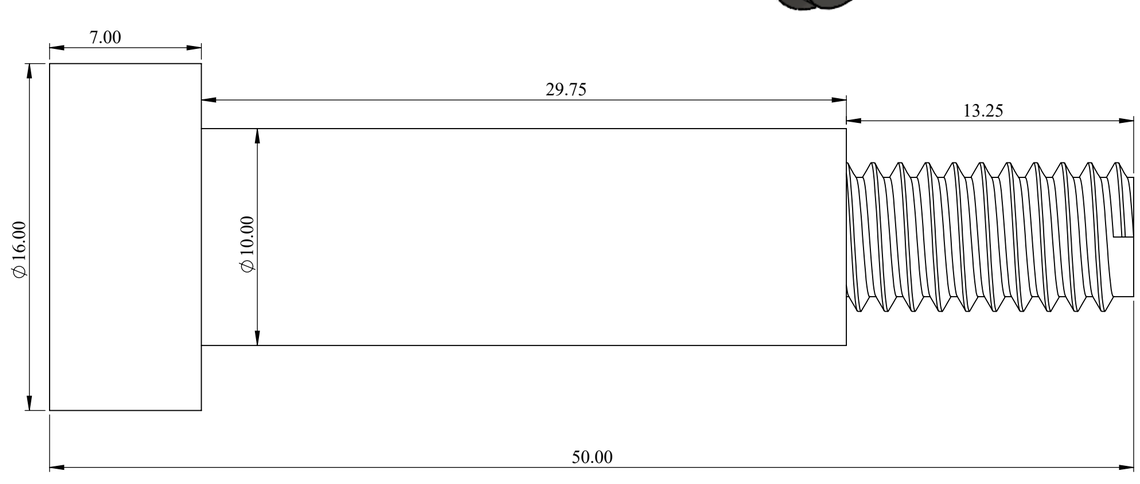

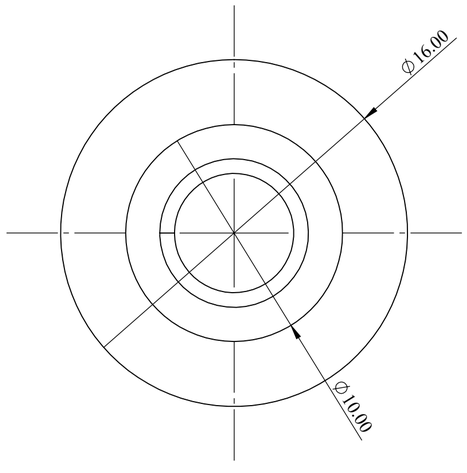

NOTE :

Name: Shoulder Bolt NATR 10
Size : 10x50 mm L & Thread length 13.25mm
Mtl : SS
Qty : 12 No's.

SPECIAL INSTRUCTION'S :

TITLE - SWIMMING POOL ENCLOSER

DWG NO - NTPL-294-PM-001-00-00-00

NIHVA TECHNOLOGIES PVT.LTD.PUNE
Website - www.nihva.com


	NAME	SIGNATURE	DATE
DRAWN	V.W.		25-08-2025
CHK'D	B.S.		29-08-2025
APPV'D	V.T.		30-08-2025

PRODUCT - SWIMMING POOL DECK
PROJECT NO - NTPL-294-PM
REVISION - 00
SITE LOCATION - PUNE
WEIGHT -
MATRIAL -
QTY - 1
SCALE :
PROJECTION METHOD:
If any queries contact - Design@nihva.com
ALL DIMENSION ARE IN mm
A2


DRAWING

ITEM NO.	PART NUMBER	DESCRIPTION	QTY.
1	SKF BALL BEARING 8 SIZE 8X19X7 MM THK	SS	8

REV DESCRIPTION	DATE	REV NO
	25-08-2025	REV 00
1.		

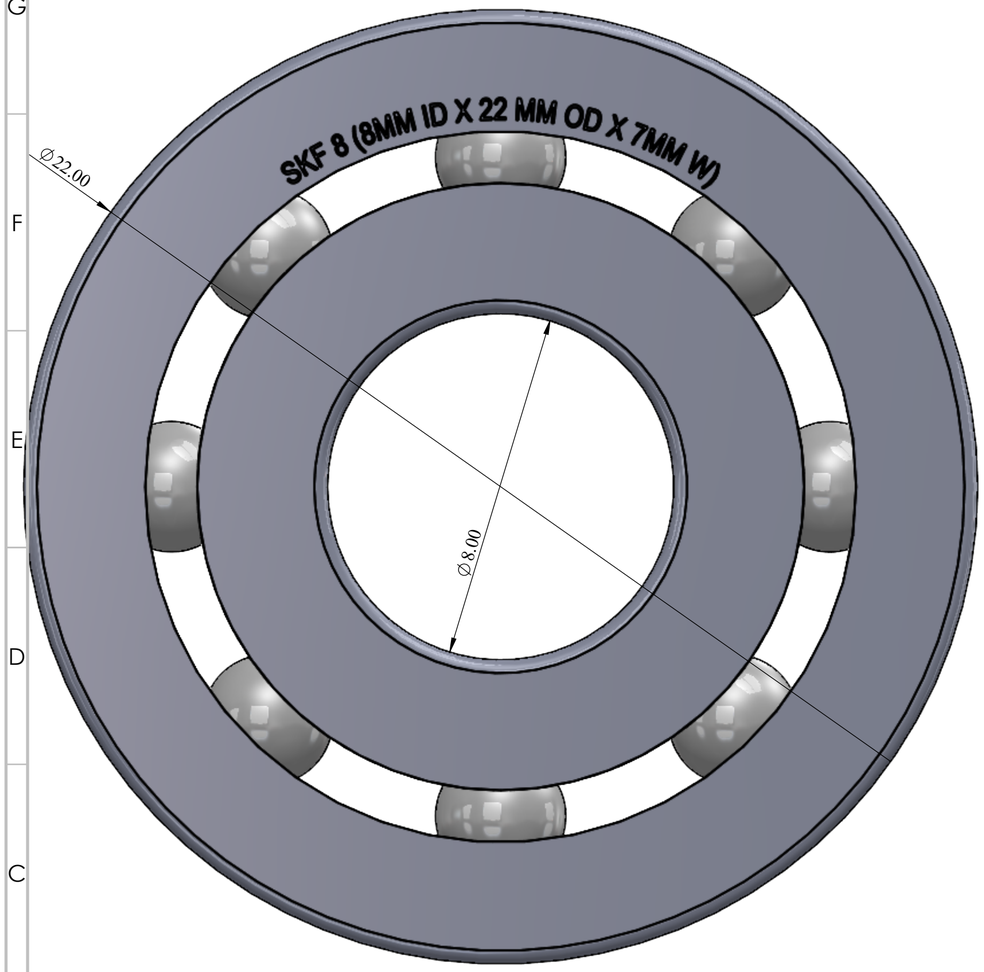



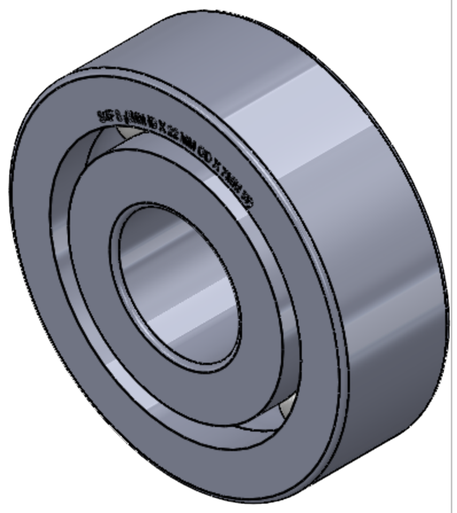

NOTE :

Name: SKF Bearing 8
Size : 8X19X7 MM THK
Qty : 12 No's

SPECIAL INSTRUCTION'S :

TITLE - SWIMMING POOL ENCLOSER

DWG NO - NTPL-294-PM-001-00-00-00

NIHVA Technologies Pvt. Ltd.


NIHVA TECHNOLOGIES PVT.LTD.PUNE
Website - www.nihva.com

	NAME	SIGNATURE	DATE
DRAWN	V.W.		25-08-2025
CHK'D	B.S.		29-08-2025
APPV'D	V.T.		30-08-2025

PRODUCT - SWIMMING POOL DECK
PROJECT NO - NTPL-294-PM
REVISION - 00
SITE LOCATION - PUNE
WEIGHT -
MATRIAL -
QTY - 1
SCALE :
PROJECTION METHOD:
SHEET 10 OF 19


If any queries contact - Design@nihva.com
ALL DIMENSION ARE IN mm
A2


DRAWING

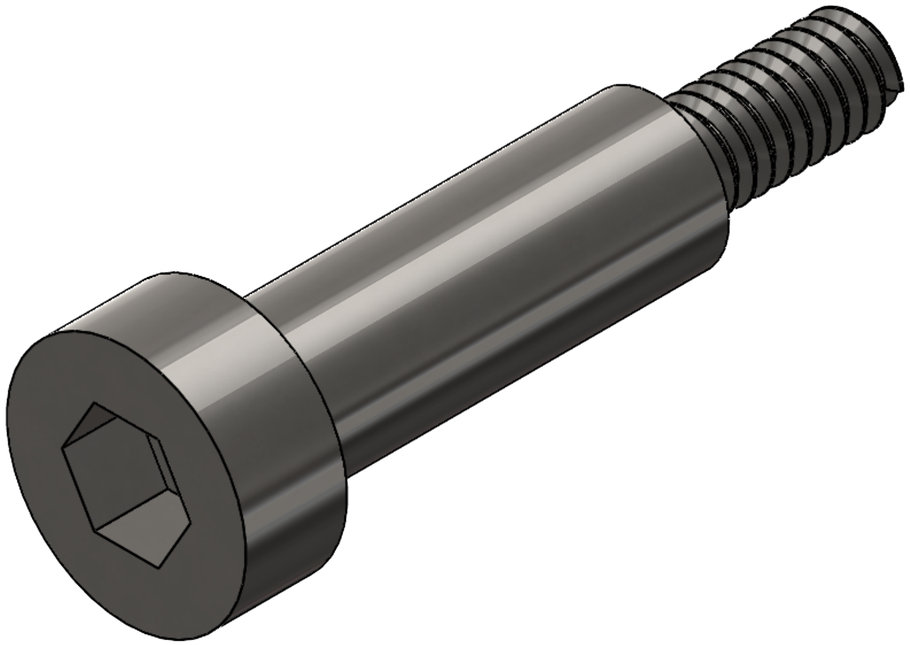

ITEM NO.	PART NUMBER	DESCRIPTION	QTY.
1	SHOULDER BOLT 8 X 40 MM L	SS	8

REV DESCRIPTION	DATE	REV NO
	25-08-2025	REV 00
1.		

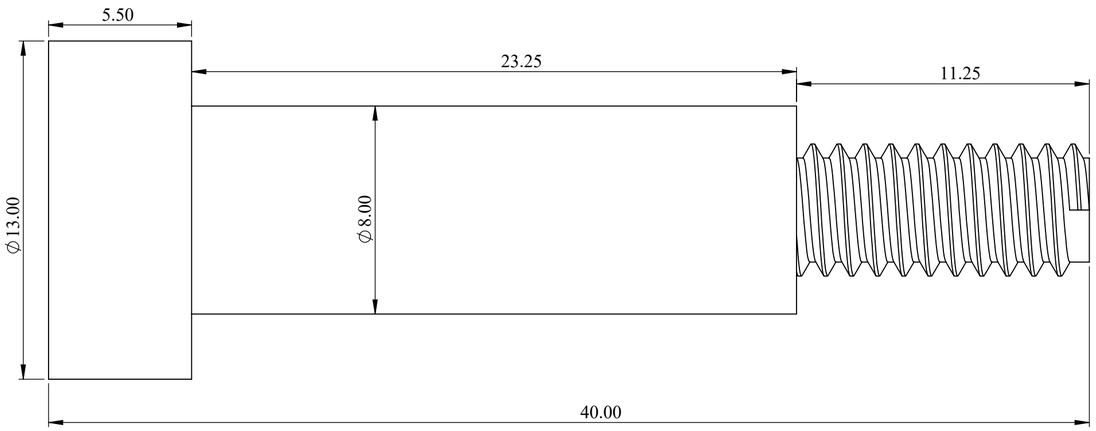

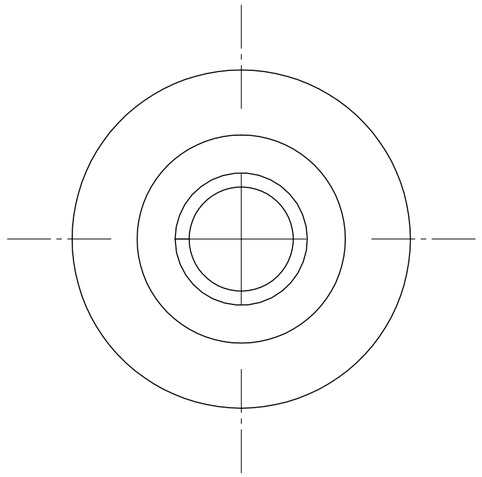

NOTE :

Name: Shoulder Bolt NATR 8
Size :8x40 mm L & Thread length 11.25mm
Mtl : SS
Qty : 12 No's.

SPECIAL INSTRUCTION'S :

TITLE - SWIMMING POOL ENCLOSER

DWG NO - NTPL-294-PM-001-00-00-00

NIHVA Technologies Pvt. Ltd.

NIHVA TECHNOLOGIES PVT.LTD.PUNE
Website - www.nihva.com


	NAME	SIGNATURE	DATE
DRAWN	V.W.		25-08-2025
CHK'D	B.S.		29-08-2025
APPV'D	V.T.		30-08-2025

PRODUCT - SWIMMING POOL DECK
PROJECT NO - NTPL-294-PM | REVISION - 00
SITE LOCATION - PUNE | WEIGHT -
MATRIAL - | QTY - 1

If any queries contact - Design@nihva.com
ALL DIMENSION ARE IN mm | A2
PROJECTION METHOD:
SCALE :

DRAWING

ITEM NO.	PART NUMBER	DESCRIPTION	QTY.
1	SS PLATE 6100 X 2630 X 3 MM THK...	SS	1

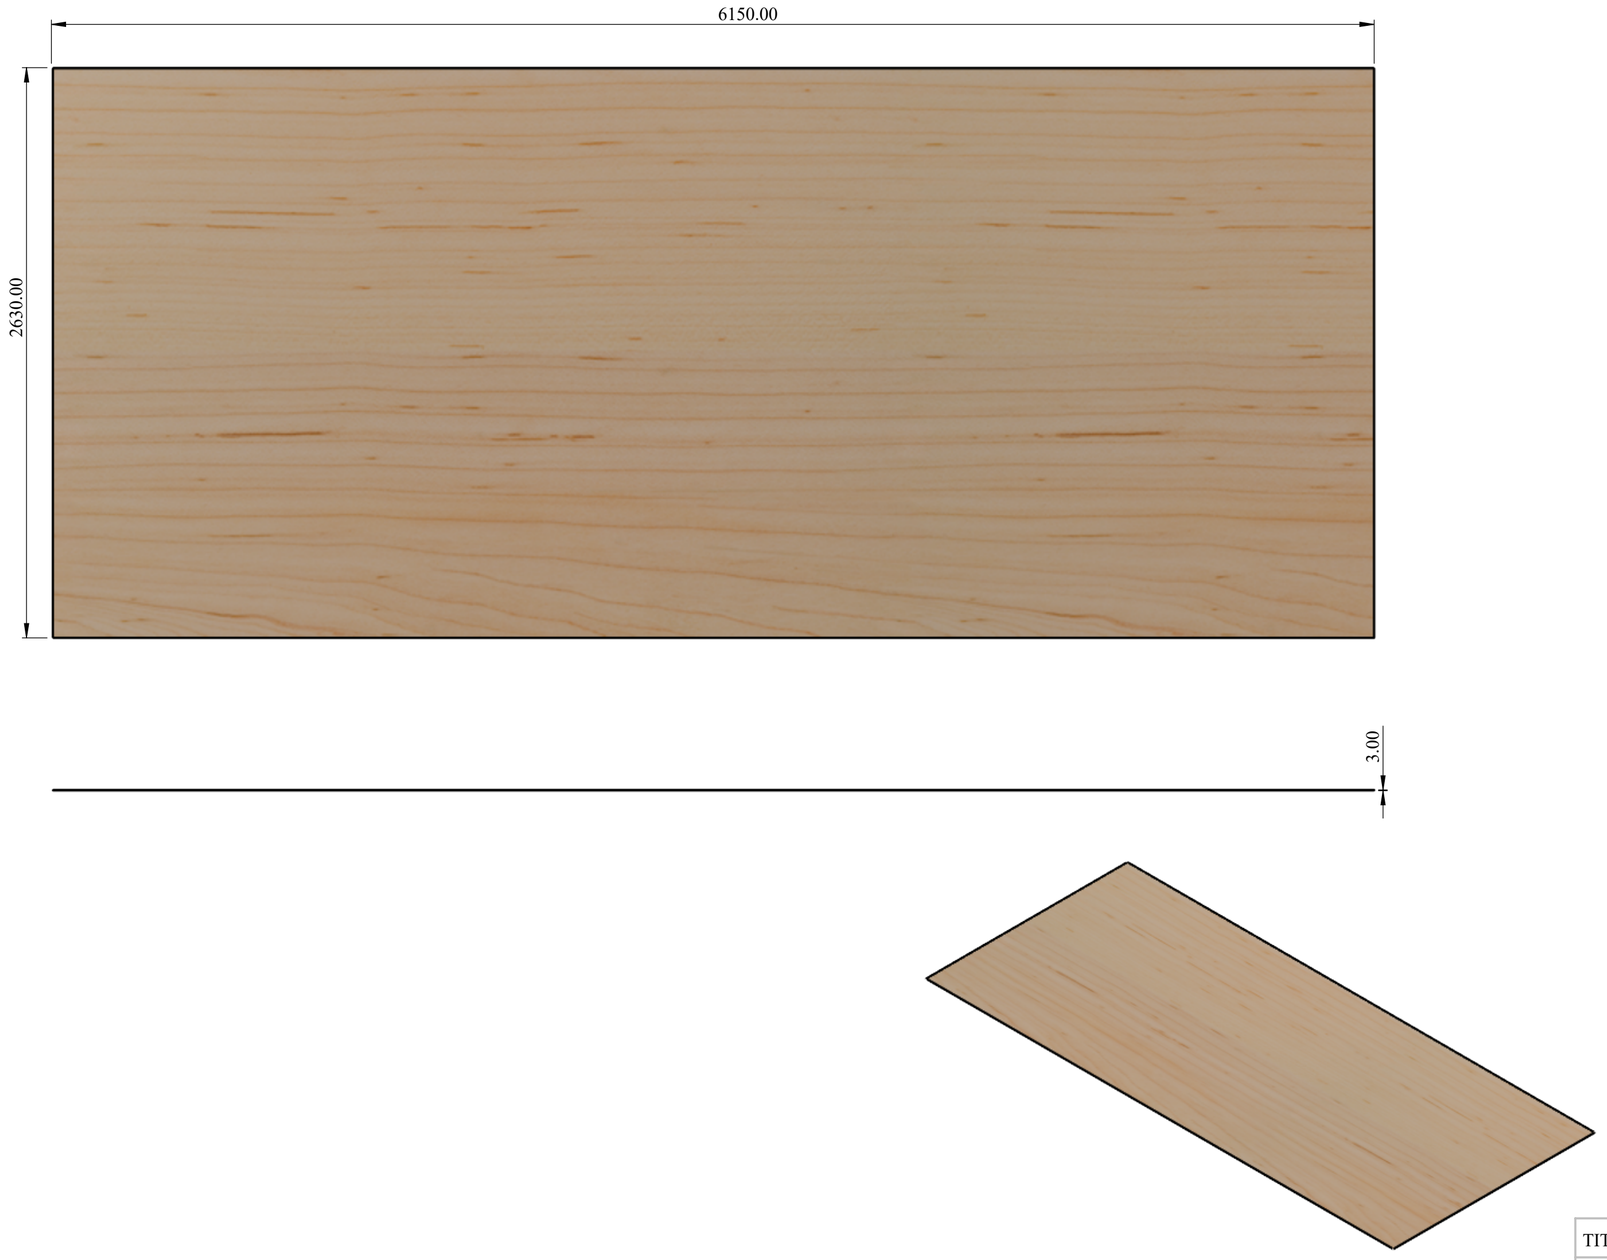

REV DESCRIPTION	DATE	REV NO
	25-08-2025	REV 00
1.		

NOTE :

Name: Covering Plate
Size : 2630x6100 mm
Thk : 3 mm
Mtl : SS
Qty : 1 No's.

SPECIAL INSTRUCTION'S :

TITLE - SWIMMING POOL ENCLOSER

DWG NO - NTPL-294-PM-001-00-00-00

NIHVA TECHNOLOGIES PVT.LTD.PUNE
Website - www.nihva.com


	NAME	SIGNATURE	DATE
DRAWN	V.W.		25-08-2025
CHK'D	B.S.		29-08-2025
APPV'D	V.T.		30-08-2025


PRODUCT - SWIMMING POOL DECK
PROJECT NO - NTPL-294-PM | REVISION - 00
SITE LOCATION - PUNE | WEIGHT -
MATRIAL - | QTY - 1
If any queries contact - Design@nihva.com | PROJECTION METHOD: | SCALE :
ALL DIMENSION ARE IN mm | A2 | SHEET 12 OF 19

DRAWING

REV DESCRIPTION	DATE	REV NO
	25-08-2025	REV 00
1.		

ITEM NO.	PART NUMBER	DESCRIPTION	QTY.
1	RACK...	STD (M4 RACK, 30x8x1000 mm, ZINC COATED WITH SPACERS AND SCREWS.)	3

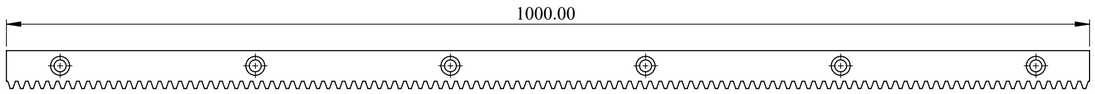

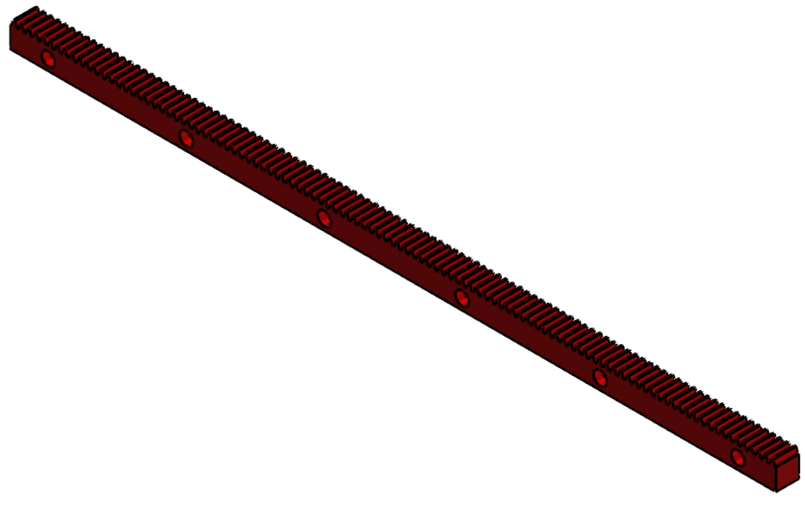

NOTE :

Name : Rack
Qty : 03 No's.

SPECIAL INSTRUCTION'S :

TITLE - SWIMMING POOL ENCLOSER

DWG NO - NTPL-294-PM-001-00-00-00

NIHVA Technologies Pvt. Ltd.

NIHVA TECHNOLOGIES PVT.LTD.PUNE
Website - www.nihva.com

	NAME	SIGNATURE	DATE
DRAWN	V.W.		25-08-2025
CHK'D	B.S.		29-08-2025
APPV'D	V.T.		30-08-2025

PRODUCT - SWIMMING POOL DECK

PROJECT NO - NTPL-294-PM | REVISION - 00

SITE LOCATION - PUNE | WEIGHT -

MATRIAL - | QTY - 1

If any queries contact - Design@nihva.com

PROJECTION METHOD:


SCALE :


ALL DIMENSION ARE IN mm | A2


DRAWING

REV DESCRIPTION	DATE	REV NO
	25-08-2025	REV 00
1.		

ITEM NO.	PART NUMBER	DESCRIPTION	QTY.
1	RACK SUPPORT PLATE	SIZE140.07X70X3 MM THK	08

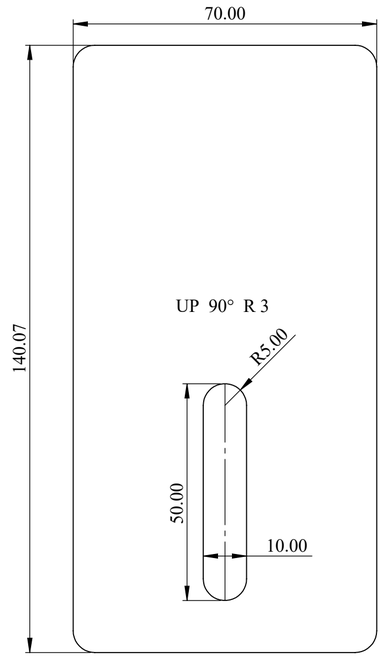

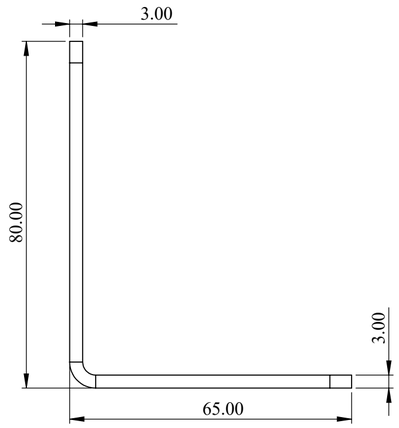

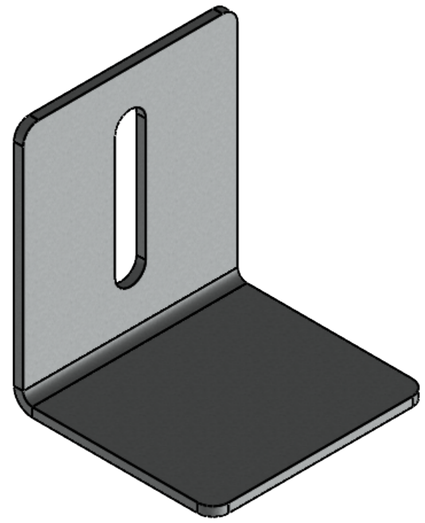

NOTE :

Name : Rack Support Plate
Size : 140.07X70X3 MM
Mtl : SS
Thk :3MM
Qty : 08 No's

SPECIAL INSTRUCTION'S :

TITLE - SWIMMING POOL ENCLOSER

DWG NO - NTPL-294-PM-001-00-00-00

NIHVA TECHNOLOGIES PVT.LTD.PUNE
Website - www.nihva.com

	NAME	SIGNATURE	DATE	PRODUCT - SWIMMING POOL DECK	
DRAWN	V.W.		25-08-2025	PROJECT NO - NTPL-294-PM	REVISION - 00
CHK'D	B.S.		29-08-2025	SITE LOCATION - PUNE	WEIGHT -
APPV'D	V.T.		30-08-2025	MATRIAL -	QTY - 1

If any queries contact - Design@nihva.com

ALL DIMENSION ARE IN mm | A2


PROJECTION METHOD:


SCALE :


DRAWING

REV DESCRIPTION	DATE	REV NO
	25-08-2025	REV 00
1.		

ITEM NO.	PART NUMBER	DESCRIPTION	QTY.
1	Anchor Bolt M10x100 MM L	STD	32

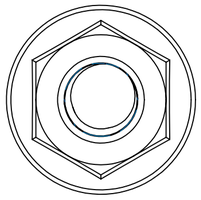

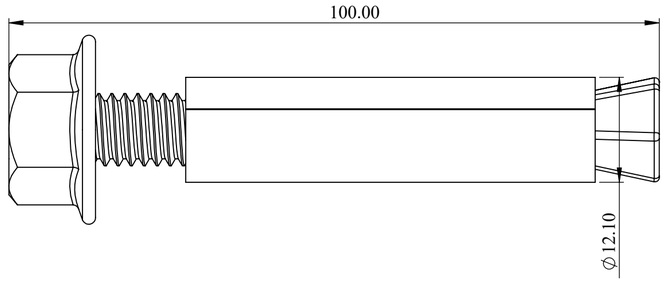

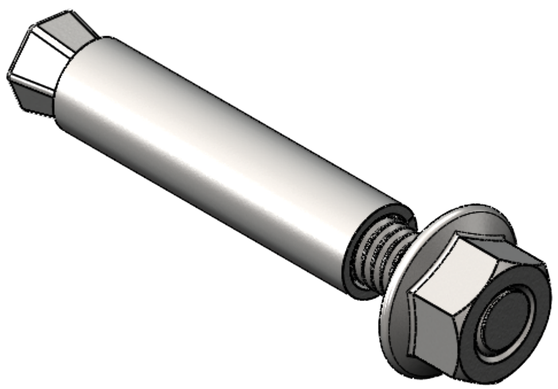

NOTE :

Name : Chemical Anchor Bolt
Size : M10X100 L
Mtl : SS
Qty : 32 No's.

SPECIAL INSTRUCTION'S :

TITLE - SWIMMING POOL ENCLOSER

DWG NO - NTPL-294-PM-001-00-00-00

NIHVA Technologies Pvt. Ltd.


NIHVA TECHNOLOGIES PVT.LTD.PUNE
Website - www.nihva.com

	NAME	SIGNATURE	DATE
DRAWN	V.W.		25-08-2025
CHK'D	B.S.		29-08-2025
APPV'D	V.T.		30-08-2025


PRODUCT - SWIMMING POOL DECK
PROJECT NO - NTPL-294-PM
REVISION - 00
SITE LOCATION - PUNE
WEIGHT -
MATRIAL -
QTY - 1
SCALE :
PROJECTION METHOD:
If any queries contact - Design@nihva.com
ALL DIMENSION ARE IN mm
A2


DRAWING

REV DESCRIPTION	DATE	REV NO
	25-08-2025	REV 00
1.		

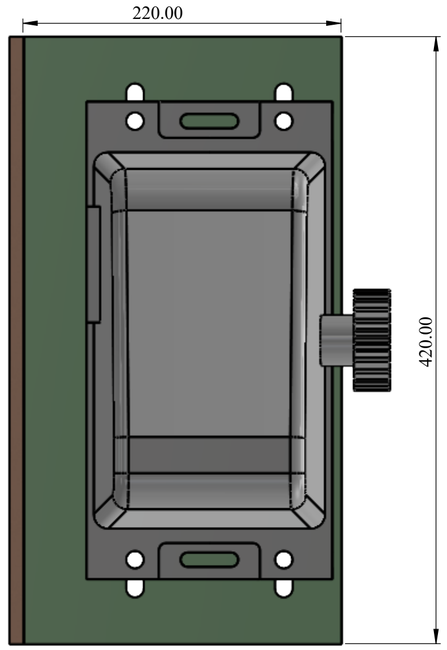

ITEM NO.	PART NUMBER	DESCRIPTION	QTY.
1	POST MOTOR BASE PLATE...		1
2	.Rev_02_MOTOR BRACKET.		1
3	.Rev_02_Nice RB1000.		1

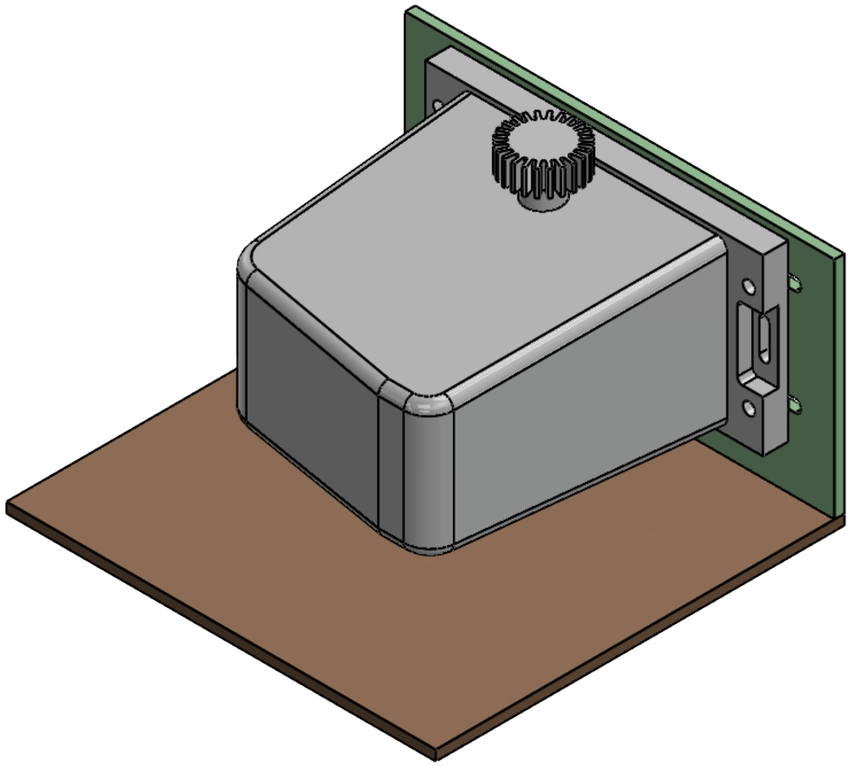

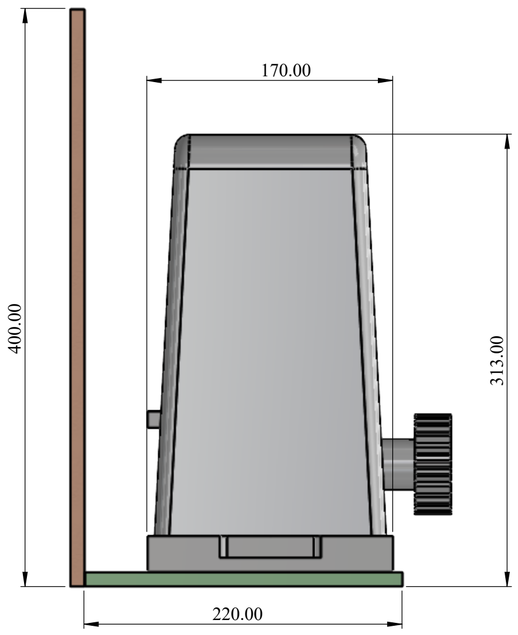

NOTE :

MOTOR MOUNTING ASM
MOTOR - NICE RB 1000
QTY - 1NOS

SPECIAL INSTRUCTION'S :

TITLE - SWIMMING POOL ENCLOSER

DWG NO - NTPL-294-PM-001-00-00-00

NIHVA Technologies Pvt. Ltd.

NIHVA TECHNOLOGIES PVT.LTD.PUNE
Website - www.nihva.com

	NAME	SIGNATURE	DATE
DRAWN	V.W.		25-08-2025
CHK'D	B.S.		29-08-2025
APPV'D	V.T.		30-08-2025


PRODUCT - SWIMMING POOL DECK
PROJECT NO - NTPL-294-PM | REVISION - 00
SITE LOCATION - PUNE | WEIGHT -
MATRIAL - | QTY - 1

If any queries contact - Design@nihva.com
ALL DIMENSION ARE IN mm | A2
PROJECTION METHOD:
SCALE :
SHEET 16 OF 19

DRAWING

ITEM NO.	PART NUMBER	DESCRIPTION	QTY.
1	.Rev_02_MTR MTG PLT.	380X220X16	1

REV DESCRIPTION	DATE	REV NO
	25-08-2025	REV 00
1.		

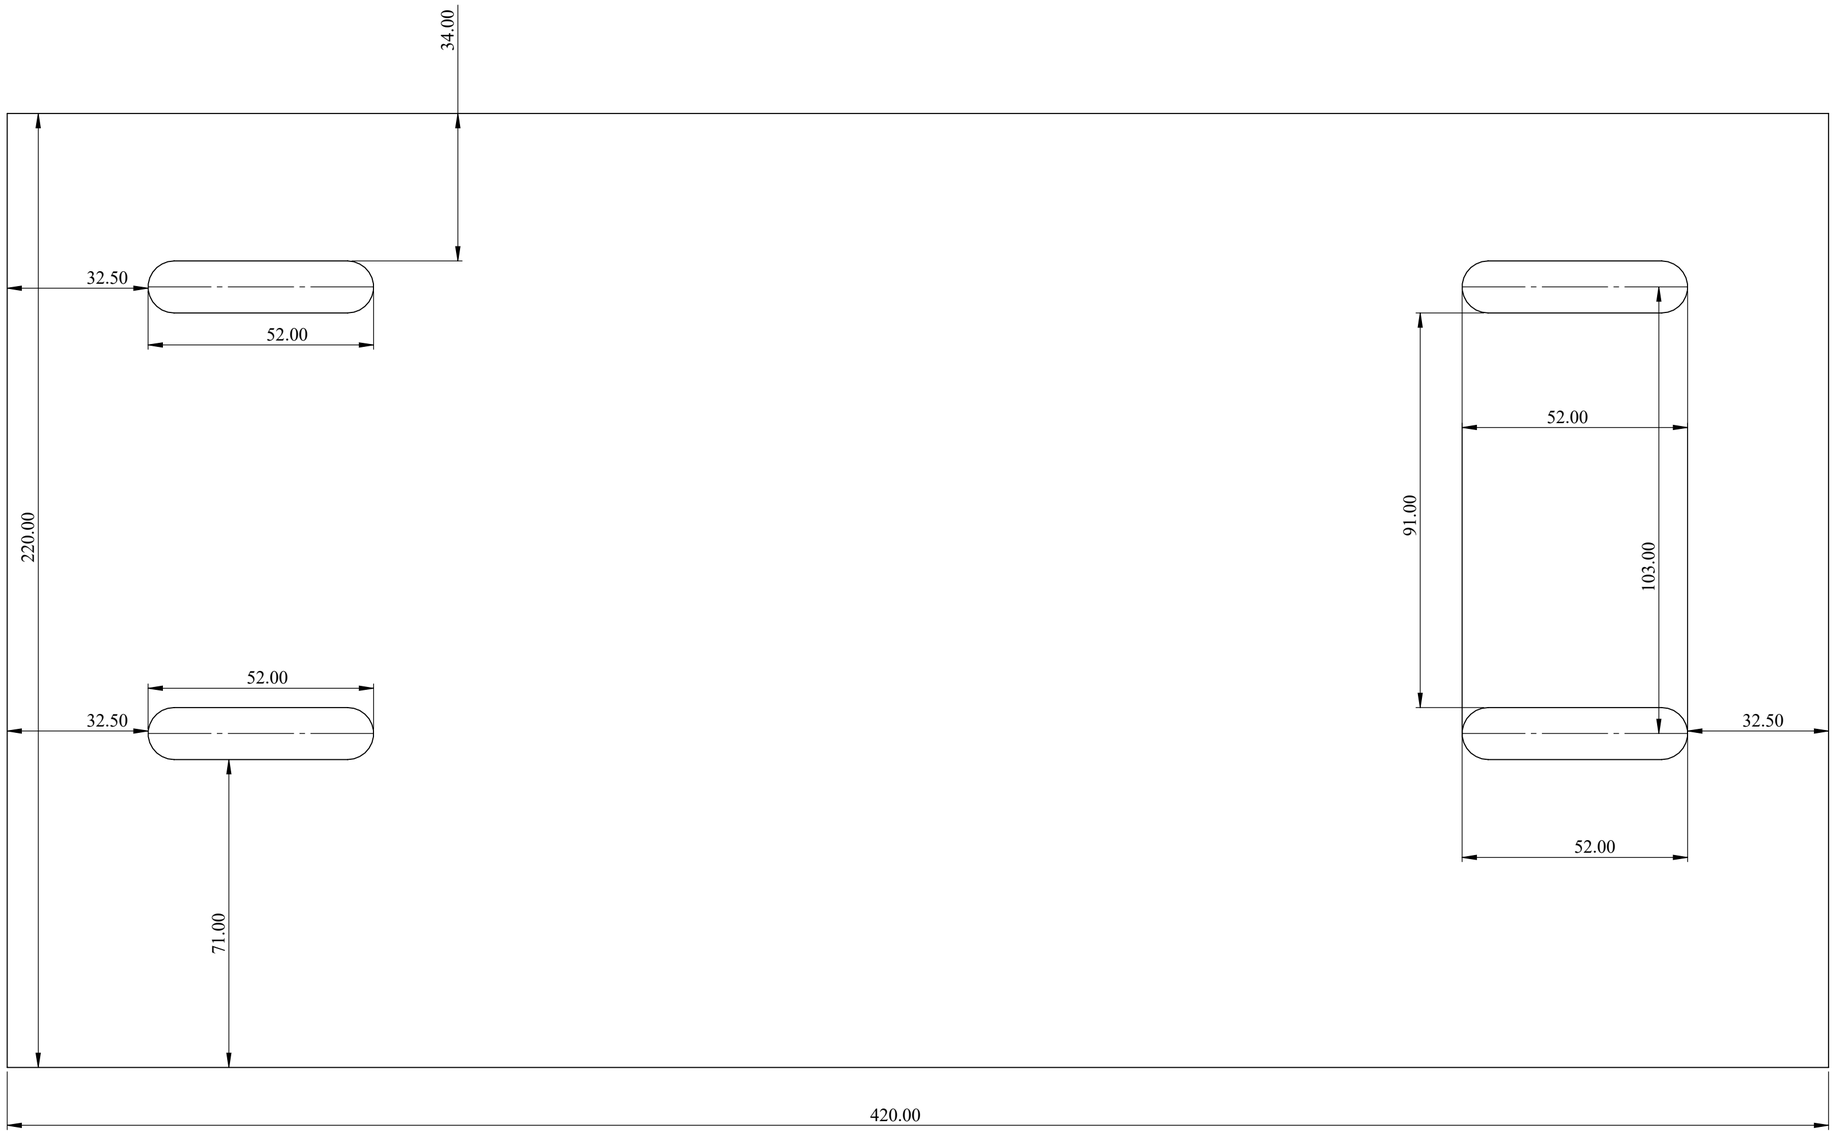

NOTE :

MOTOR MOUNTING PLATE 1
MTL - MS
THK - 10 MM
QTY - 1

SPECIAL INSTRUCTION'S :

TITLE - SWIMMING POOL ENCLOSER

DWG NO - NTPL-294-PM-001-00-00-00

NIHVA Technologies Pvt. Ltd.

NIHVA TECHNOLOGIES PVT.LTD.PUNE
Website - www.nihva.com


	NAME	SIGNATURE	DATE
DRAWN	V.W.		25-08-2025
CHK'D	B.S.		29-08-2025
APPV'D	V.T.		30-08-2025


PRODUCT - SWIMMING POOL DECK
PROJECT NO - NTPL-294-PM | REVISION - 00
SITE LOCATION - PUNE | WEIGHT -
MATRIAL - | QTY - 1
If any queries contact - Design@nihva.com | PROJECTION METHOD: | SCALE :
ALL DIMENSION ARE IN mm | A2 | SHEET 17 OF 19


DRAWING

REV DESCRIPTION	DATE	REV NO
	25-08-2025	REV 00
1.		

ITEM NO.	PART NUMBER	DESCRIPTION	QTY.
1	POST MOTOR BASE PLATE...		1

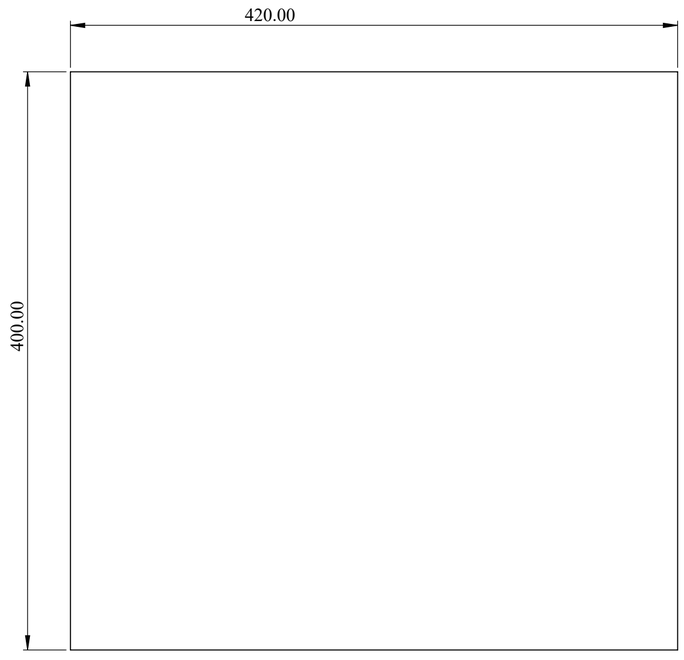

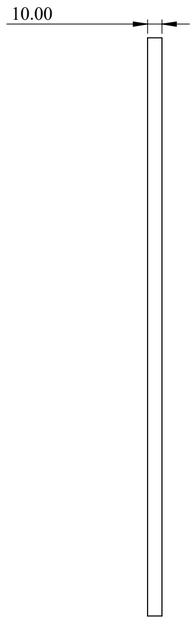

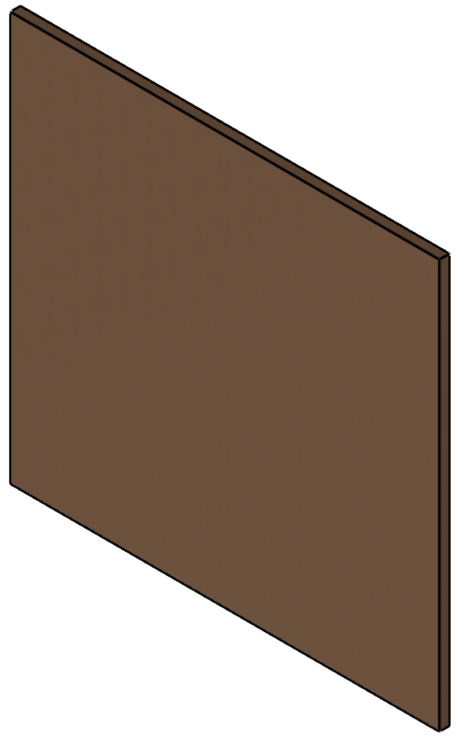

NOTE :

MOTOR MOUNTING PLATE 2
MTL - MS
QTY - 1 NOS
THK -10 MM

SPECIAL INSTRUCTION'S :

TITLE - SWIMMING POOL ENCLOSER

DWG NO - NTPL-294-PM-001-00-00-00

NIHVA TECHNOLOGIES PVT.LTD.PUNE
Website - www.nihva.com


	NAME	SIGNATURE	DATE
DRAWN	V.W.		25-08-2025
CHK'D	B.S.		29-08-2025
APPV'D	V.T.		30-08-2025


PRODUCT - SWIMMING POOL DECK
PROJECT NO - NTPL-294-PM | REVISION - 00
SITE LOCATION - PUNE | WEIGHT -
MATRIAL - | QTY - 1
If any queries contact - Design@nihva.com | PROJECTION METHOD: | SCALE :
ALL DIMENSION ARE IN mm | A2 | SHEET 18 OF 19

DRAWING

REV DESCRIPTION	DATE	REV NO
	25-08-2025	REV 00
1.		

ITEM NO.	PART NUMBER	DESCRIPTION	QTY.
1	Link Plate		1
2	Rivet Link Plate		1
3	Clamp		1
4	Screw		1
5	Wheel		1
6	Connection Pin		1

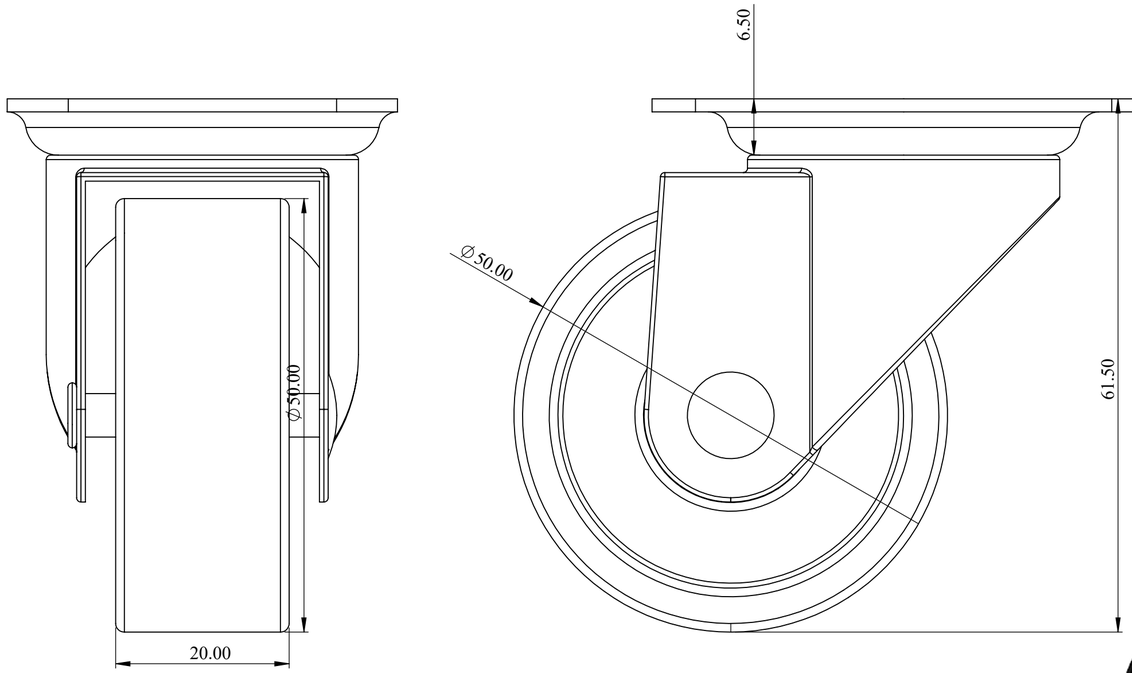

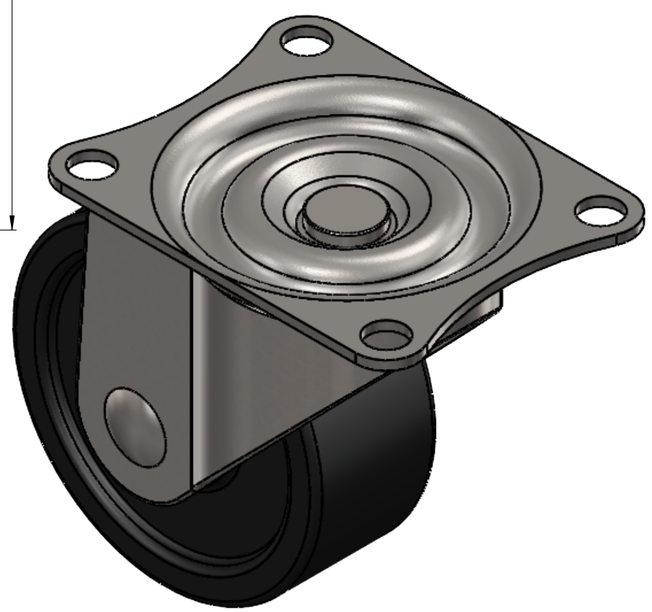

NOTE :

Name : Caster Wheel
Qty : 04 No's

SPECIAL INSTRUCTION'S :

TITLE - SWIMMING POOL ENCLOSER

DWG NO - NTPL-294-PM-001-00-00-00

NIHVA Technologies Pvt. Ltd.

NIHVA TECHNOLOGIES PVT.LTD.PUNE
Website - www.nihva.com

	NAME	SIGNATURE	DATE
DRAWN	V.W.		25-08-2025
CHK'D	B.S.		29-08-2025
APPV'D	V.T.		30-08-2025

PRODUCT - SWIMMING POOL DECK
PROJECT NO - NTPL-294-PM | REVISION - 00
SITE LOCATION - PUNE | WEIGHT -
MATRIAL - | QTY - 1
If any queries contact - Design@nihva.com | PROJECTION METHOD: | SCALE :
ALL DIMENSION ARE IN mm | A2 | SHEET 19 OF 19