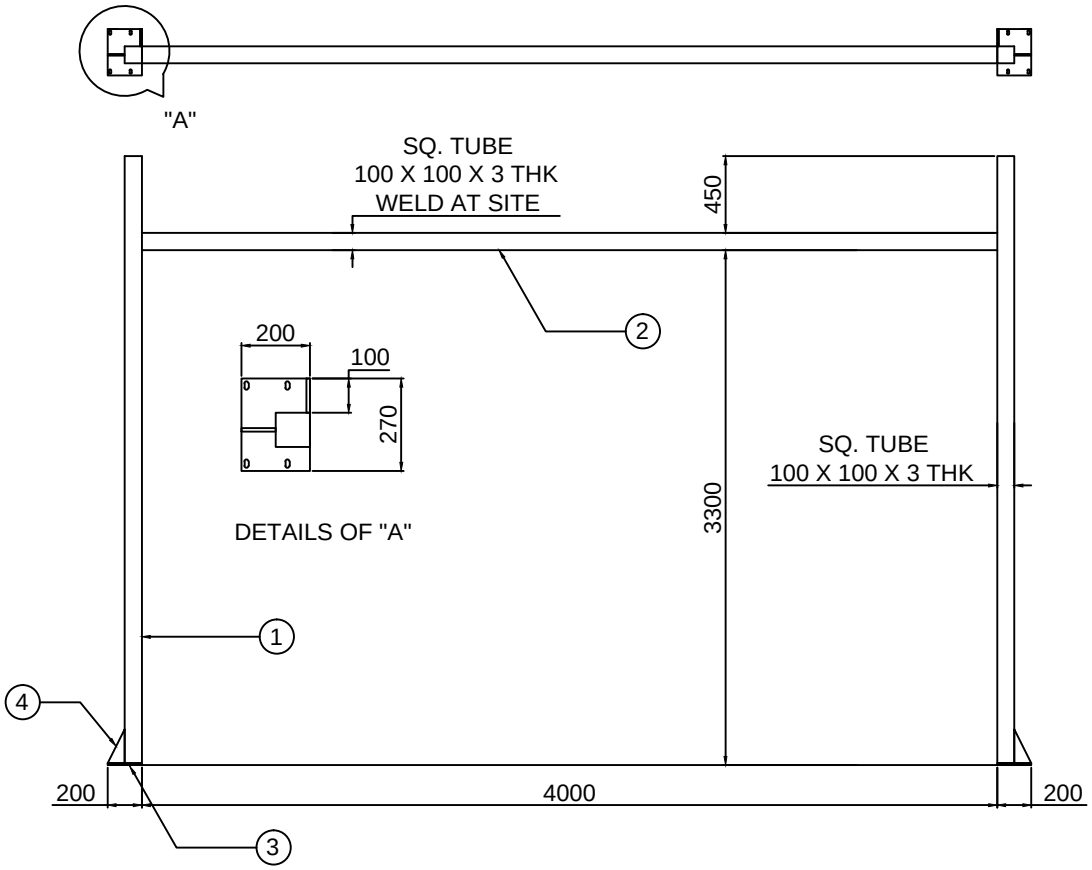

STRUCTURE QTY : 4 NOS

SR NO	DESCRIPTION	SPECIFICATION	QTY
4	RIBS	100 X 10 X 200L	4 NOS
3	PROFILE	200 X 10 X 270L	2 NOS
2	SQ. TUBE	100 X 100 X 3 X 4000L	1 NO
1	SQ. TUBE	100 X 100 X 3 X 3850L	2 NOS

This drawing & design is the property of NIHVA TECHNOLOGIES. Not to be sold or copied to any other concern.

TITLE
STRUCTURE DRAWING

NIHVA TECHNOLOGIES PVT. LTD.
NIHVA TECHNOLOGIES PVT. LTD. PUNE
Tel : 020 66304033
Email:- info@nihva.com
Website:- www.nihva.com

	NAME	SIGN	DATE
DRAWN	P.A		13.01.20
CHECK	G.J		13.01.20
APPV'ED			

CLIENT :-
PROJECT :-
LOCATION :-

If any queries contact : design@nihva.com

DWG. NO. :- NIHVA/19-20/VDR/282 REV.:-R00

ALL DIMENSION ARE IN mm

SCALE: NTS WT: SHEET: 01 OF 01