


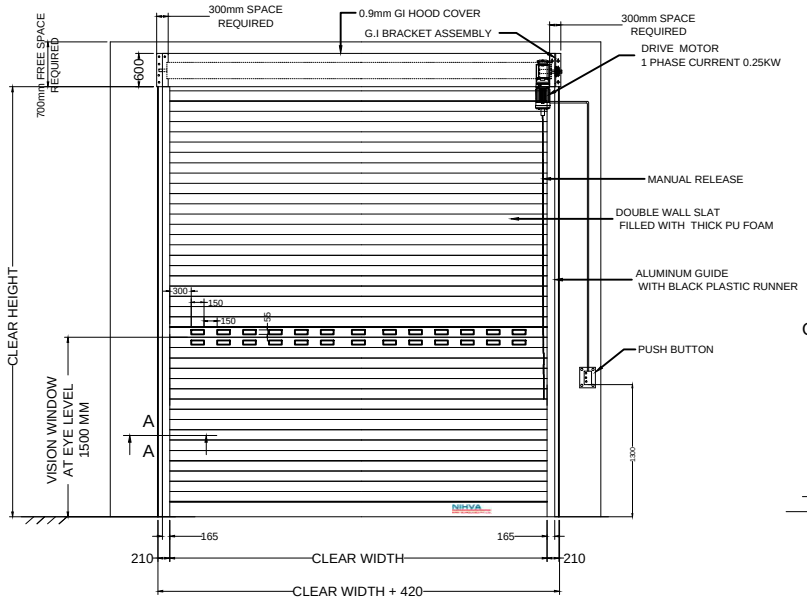


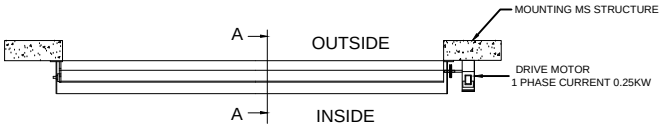


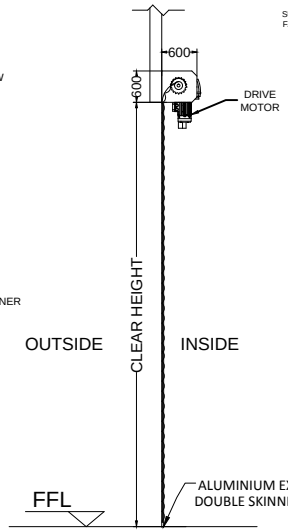

Section A-A

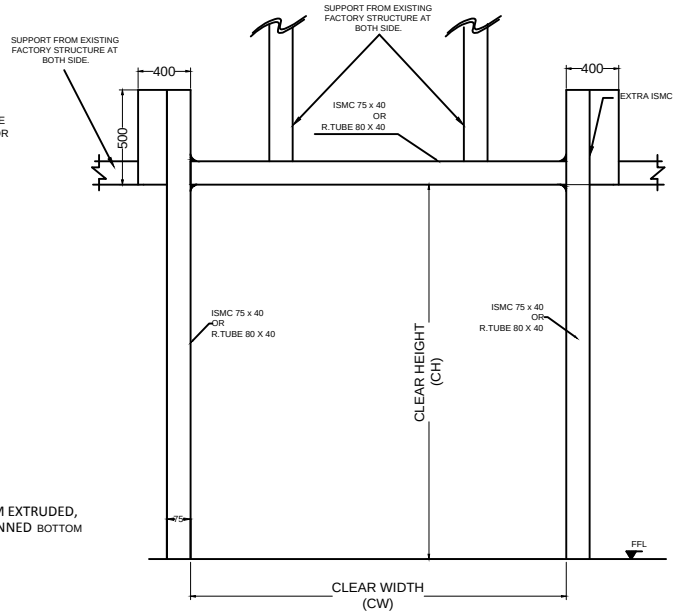

STRUCTURE

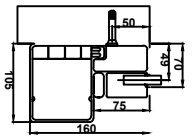


SECTION DETAIL

MAIN SLATS

DOUBLE WALL ROLLING SHUTTER



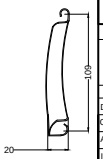

STANDARD COLOR OF SLATS & SHUTTER -RAL9002 (GRAY WHITE)		
5000 mm	3560mm	1 NO
CLEAR WIDTH	CLEAR HEIGHT	QUANTITY

CLIENT SCOPE

1) 16A 3 PIN INDUSTRIAL TYPE FEMALE SOCKET 230V, 50HZ,
WITH EARTH AROUND 1/2 METER FROM CONTROLLER/OPERATOR.
2) ALL CIVIL WORK WILL BE CLIENT'S SCOPE.
3) TECHNICAL MS STRUCTURE REQUIRED FOR SHUTTER IS IN CLIENT'S SCOPE.

REV NO	DATE	DRAWN	REMARK
R01	09.10.2020	P.A	1. CLEAR HEIGHT CHANGE.

NOTE : DOOR TO BE FIXED FROM INSIDE ONLY

This drawing & design is the property of NIHVA TECHNOLOGIES. Not to be sold or copied to any other concern.

TITLE DOUBLE WALL ROLLING SHUTTER

NIHVA TECHNOLOGIES PVT. LTD.

NIHVA TECHNOLOGIES PVT. LTD. PUNE
Tel : 020 66304033
Email:- info@nihva.com
Website:- www.nihva.com

	NAME	SIGN	DATE
DRAWN	S.S.		6.10.2020
CHECK	P.A		6.10.2020
APPRD.			

CLIENT - M A ENGINEERING

PROJECT - JOHN DEERE INDIA PVT LTD

SITE LOCATION - PUNE

If any queries contact : projectsupport @nihva.com

DWG. NO. : NIHVA/20-21/0058/R01 REV- R01

ALL DIMENSION ARE IN mm

SCALE: NTS WT: SHEET: