

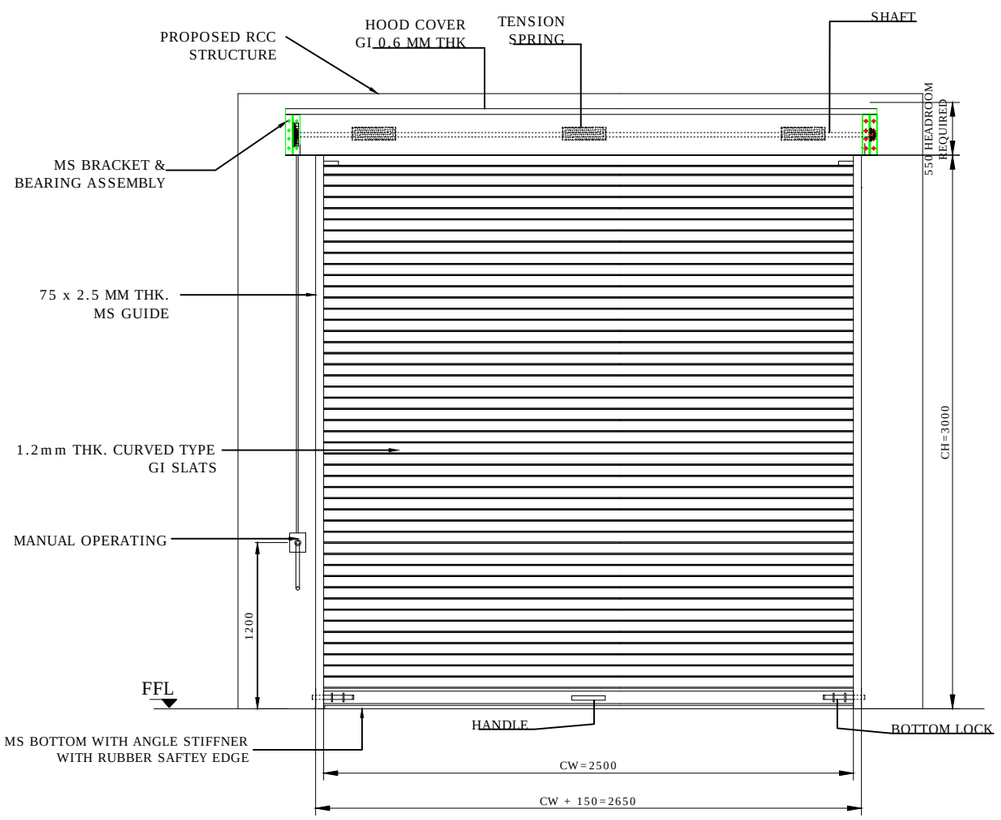



OUTSIDE ELEVATION

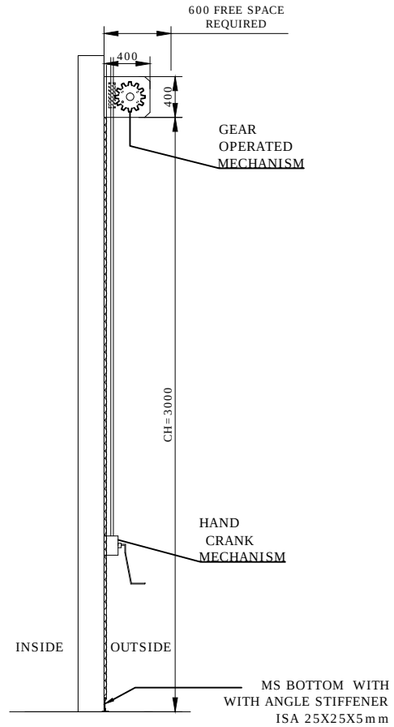


SIDE VIEW

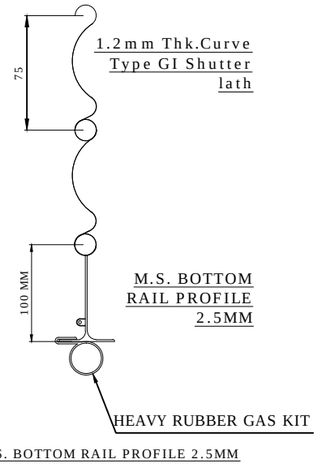

M.S. BOTTOM RAIL PROFILE 2.5MM

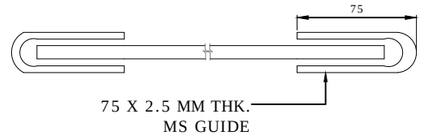

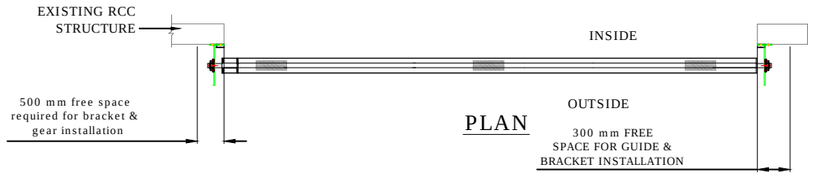

PLAN

RAL CODE	RAL COLOR	APPROVED
RAL 9010	Pure White	
RAL 9002	Grey White	
RAL 7035	Light Grey	
RAL 5002	Ult. M. Blue	
RAL 7040	Window Grey	Approved

SR NO	(CW) CLEAR WIDTH	(CH) CLEAR HEIGHT	QUANTITY
1	2500	3000	02 NO

NOTE-
1. ALL CIVIL WORK WILL BE CLIENT'S SCOPE.
2. IF STRUCTURE REQUIRED FOR SHUTTER IS IN CLIENT'S SCOPE.
3. SURFACE FINISH: POWDER COATING OF APPROVED RAL CODE.
4. MOUNTING ON OUTSIDE CONCRETE STRUCTURE.
5. MOUNTING OF LEVER WILL BE ON LEFT SIDE.

REV 01 (05-03-2022)
1. MENTIONED APPROVED RAL CODE ON DRAWING

TOLERANCE - ±10mm

This drawing & design is the property of NIHVA TECHNOLOGIES. Not to be sold or copied to any other concern.

TITLE: GEAR OPERATED ROLLING SHUTTER

	NAME	SIGN	DATE
DRAWN	G.I.P		22.02.2022
CHECK	A.K.		22.02.2022
APPRD.	V.T.		22.02.2022

If any queries contact : design@nihva.com

ALL DIMENSION ARE IN mm

NIHVA TECHNOLOGIES PVT. LTD.
NIHVA TECHNOLOGIES PVT. LTD. PUNE
Tel : 020 66304033
Website:- www.nihva.com
Email:- info@nihva.com

CLIENT - QUALITY INFRASTRUCTURE PVT LTD

PROJECT -GEAR OPERATED ROLLING SHUTTER

SITE LOCATION -GUJARAT

DWG. NO. : NIHVA/21-22/CLT/355 | REV- R1

SCALE: NTS | WT: | SHEET: 01 OF 01