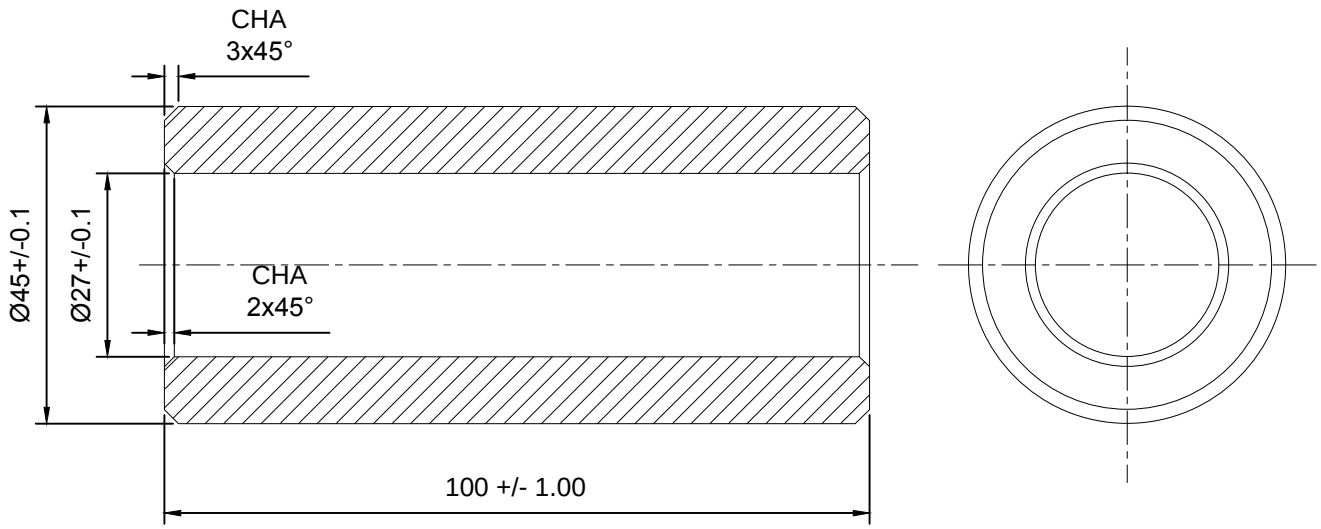



NOTE:~ MTL : MS

BUSH Ø45 X 103L = 21 NOS

NOTE : ~ PLEASE MAINTAIN 7 MM GAP BETWEEN TWO LIP BUSHES.

This drawing & design is the property of NIHVA TECHNOLOGIES. Not to be sold or copied to any other concern.

| TITLE | | | | |
|---|---|---|---|---|
| LIP MOUNTING BUSH | | | | NIHVA TECHNOLOGIES PVT. LTD. PUNE<br>Tel : 020 66304033<br>Email:- info@nihva.com<br>Website:- www.nihva.com |
| | NAME | SIGN | DATE | |
| DRAWN | P.V.A | | 06.03.2019 | CLIENT - |
| CHECK | V.M.T | | 06.03.2019 | PROJECT - NDL 385 & 386 |
| APPRD. | | | | SITE LOCATION - |
| If any queries contact : design@nihva.com | | | | DWG. NO. : NIHVA/18-19/VDR/423 |
| ALL DIMENSION ARE IN mm | | | | SCALE: NTS / WT: / REV- 0 |