




PLAN

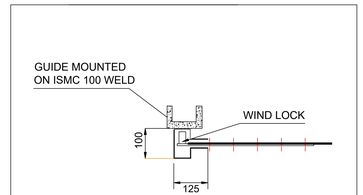

" T " TYPE GUIDE

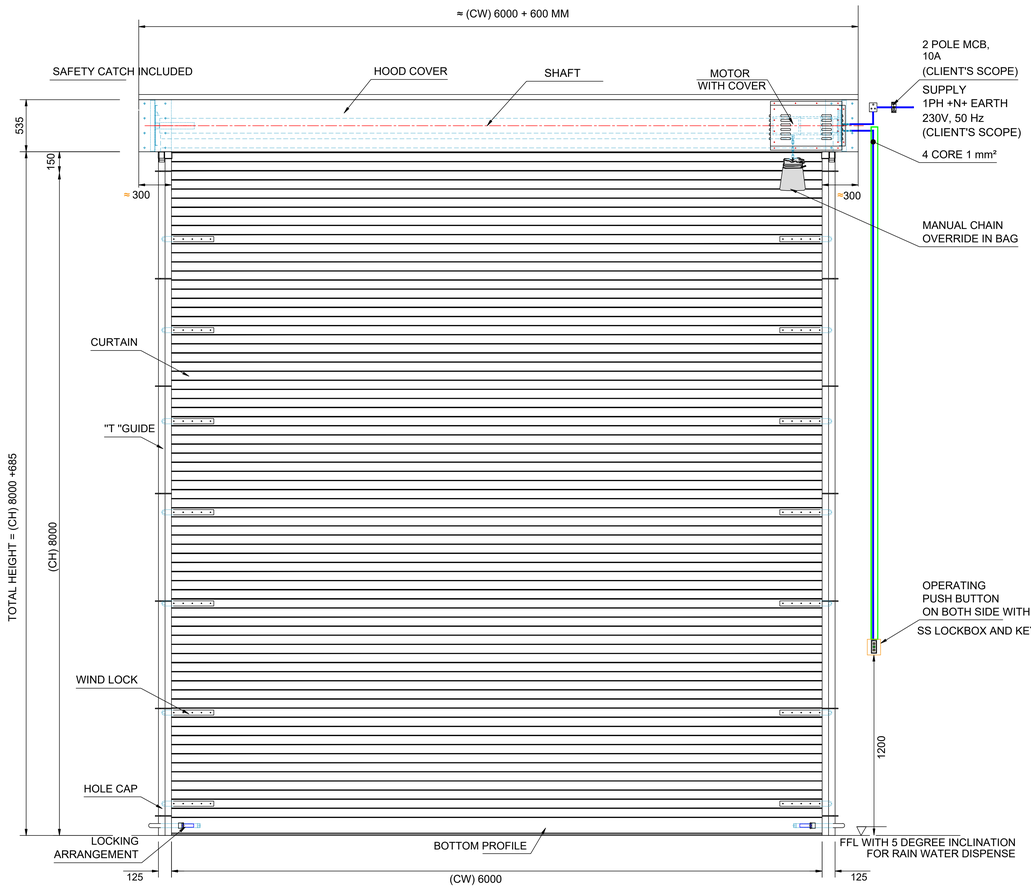

INSIDE ELEVATION

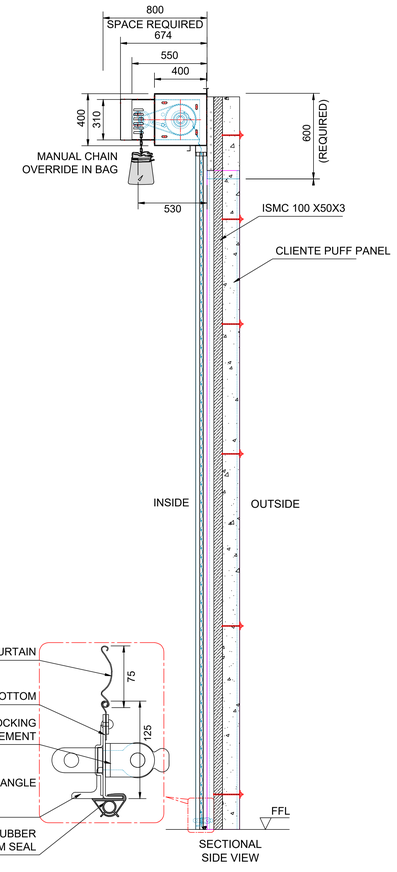

TECHNICAL SPECIFICATION:-

SR.	SPECIFICATION	DETAILS
1.	Description & Drive	Motorised Rolling Shutter (Indirect Drive) with Manual Chain Arrangment
2.	Location Area	Inside / Outside
3.	Mounting Surface	Side Brackets: Optional / Structure
4.	Slat	Curved 75 mm PPGI Sheet - 1.2 mm Thk. & Windlock Considered
5.	Bottom Profile	MS Plate 125 x 2 mm thick with Angle Stiffner & Rubber Seal
6.	Guide Profile	M.S." T " Shape profile 125 x 3 mm Thk.
7.	Hood Cover & Motor Cover	Made of GI Sheet Thickness 0.9 mm
8.	Accessories	Safety Catch,Push Button On Both SIde

Scope :-

SR.	WORK CONTAINT	SCOPE
01.	All Cables & Ele.Conduits upto Control Box of Shutter	NIHVA
02.	All Cables & Ele.Conduits Above Control Box of Shutter	Client

SHUTTER SIZES :-

SR.	CLEAR WIDTH	CLEAR HEIGHT	QTY.
01	6000	8000	01


This drawing & designing is the property of NIHVA TECHNOLOGIES. Not to be sold or copied to any other concern.

TITLE :-
MOTORISED ROLLING
SHUTTER


NIHVA TECHNOLOGIES PVT. LTD.
NIHVA TECHNOLOGIES
PVT. LTD. PUNE
Tel : 020 66304033
Email:- info@nihva.com
Website:- www.nihva.com

	NAME	DATE
DRAWN	J.S.	19/01/2024
CHECK	A.K.	19/01/2024
APPROVAL	V.T.	19/01/2024


CLIENT - RINAC
PROJECT -ROLLING SHUTTER
FORMAT NO - NIHVA-DD-F-03
DWG. NO. : NIHVA/23-24/101 REV-00
SCALE: NTS WT: SHEET: 01 OF 01
ALL DIMENSION ARE IN mm
If any queries contact : design@nihva.com

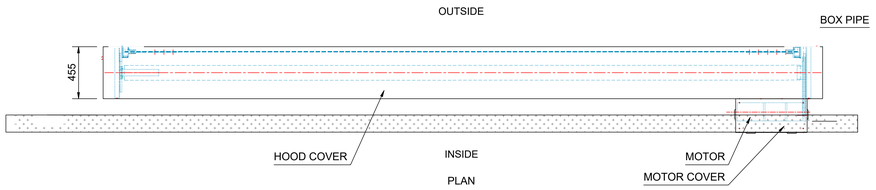


PLAN

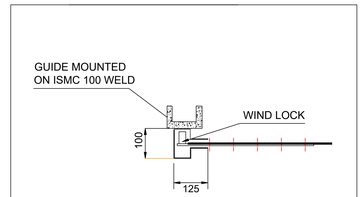

" T " TYPE GUIDE

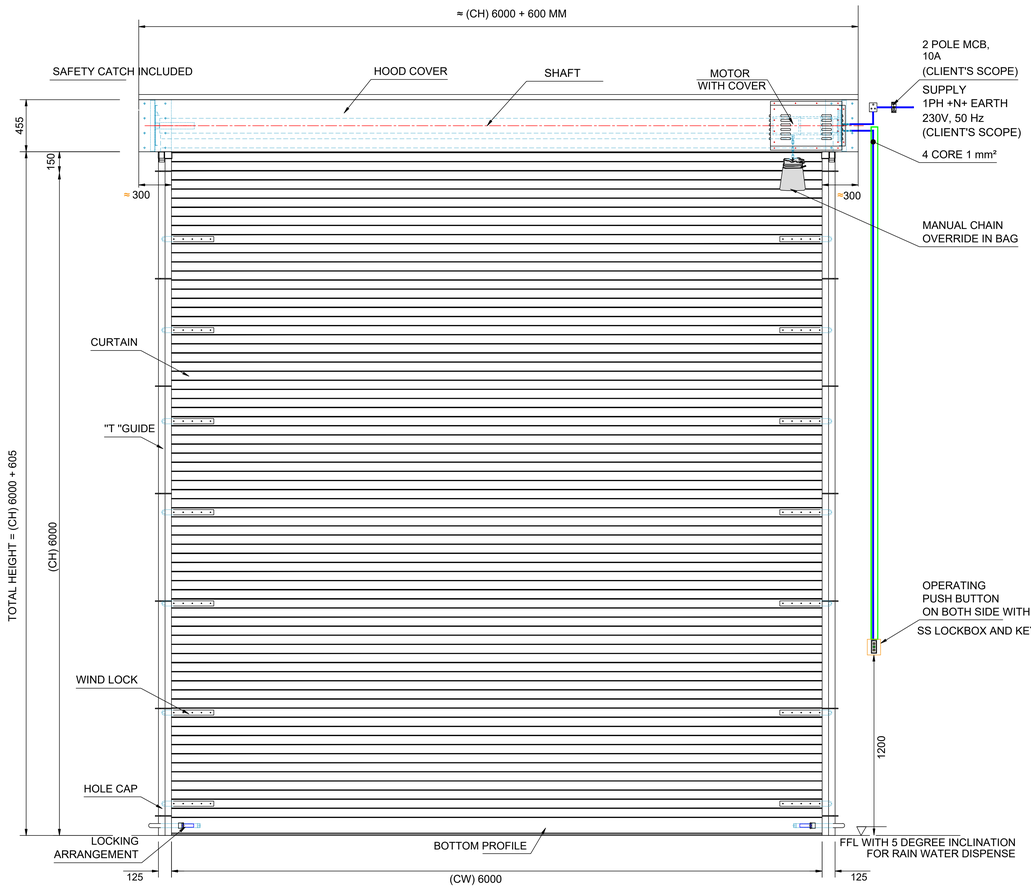

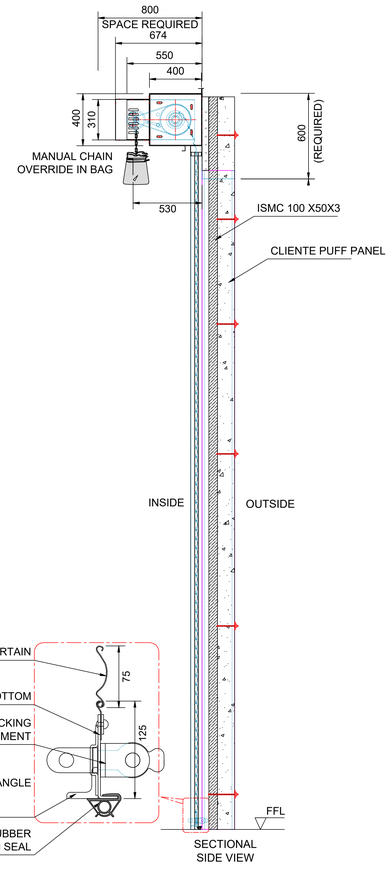

INSIDE ELEVATION

TECHNICAL SPECIFICATION:-

SR.	SPECIFICATION	DETAILS
1.	Description & Drive	Motorised Rolling Shutter (Indirect Drive) with Manual Chain Arrangment
2.	Location Area	Inside / Outside
3.	Mounting Surface	Side Brackets: Optional / Structure
4.	Slat	Curved 75 mm PPGI Sheet - 1.2 mm Thk. & Windlock Considered
5.	Bottom Profile	MS Plate 125 x 2 mm thick with Angle Stiffner & Rubber Seal
6.	Guide Profile	M.S." T " Shape profile 125 x 3 mm Thk.
7.	Hood Cover & Motor Cover	Made of GI Sheet Thickness 0.9 mm
8.	Accessories	Safety Catch,Push Button On Both SIde

Scope :-

SR.	WORK CONTAINT	SCOPE
01.	All Cables & Ele.Conduits upto Control Box of Shutter	NIHVA
02.	All Cables & Ele.Conduits Above Control Box of Shutter	Client

SHUTTER SIZES :-

SR.	CLEAR WIDTH	CLEAR HEIGHT	QTY.
01	6000	6000	02


This drawing & designing is the property of NIHVA TECHNOLOGIES. Not to be sold or copied to any other concern.


TITLE :-
MOTORISED ROLLING
SHUTTER

NIHVA TECHNOLOGIES PVT. LTD.
NIHVA TECHNOLOGIES
PVT. LTD. PUNE
Tel : 020 66304033
Email:- info@nihva.com
Website:- www.nihva.com


	NAME	DATE
DRAWN	J.S.	19/01/2024
CHECK	A.K.	19/01/2024
APPROVAL	V.T.	19/01/2024


CLIENT - RINAC
PROJECT -ROLLING SHUTTER
FORMAT NO - NIHVA-DD-F-03
DWG. NO. :NIHVA/23-24/103 REV-00
SCALE: NTS WT: SHEET: 01 OF 01
ALL DIMENSION ARE IN mm
If any queries contact : design@nihva.com

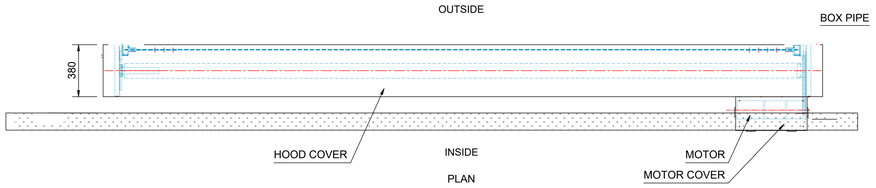

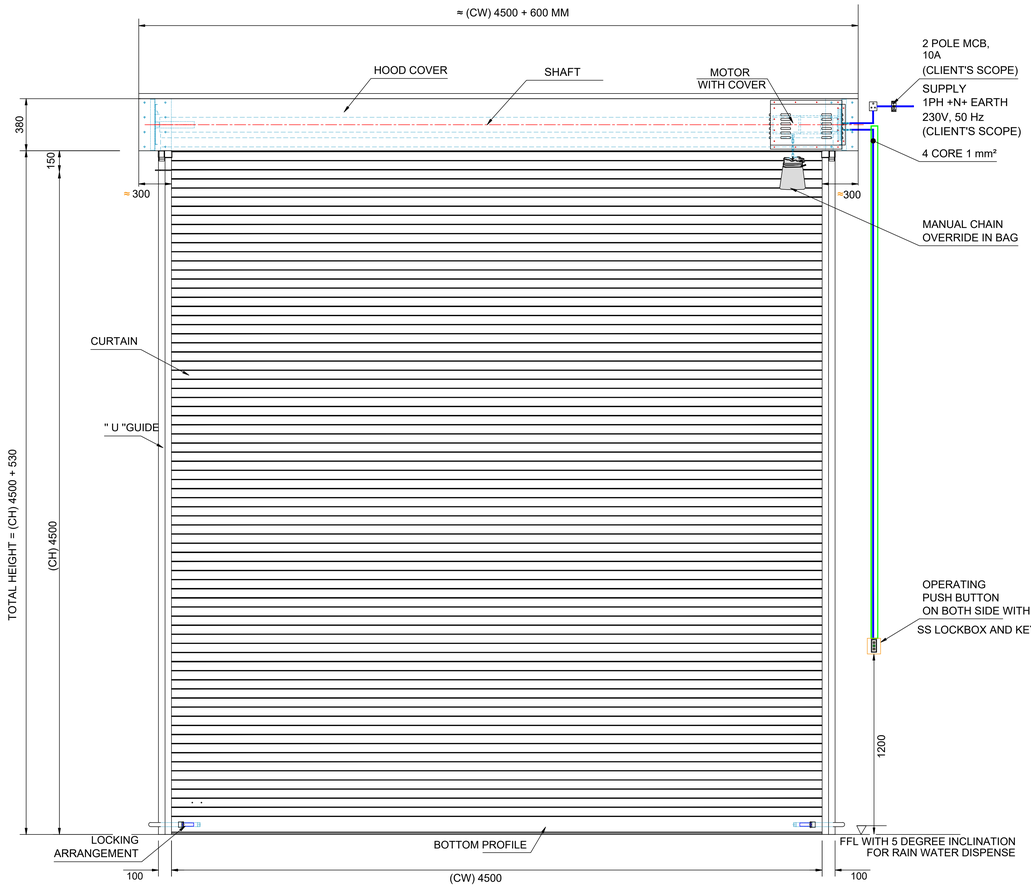

INSIDE ELEVATION

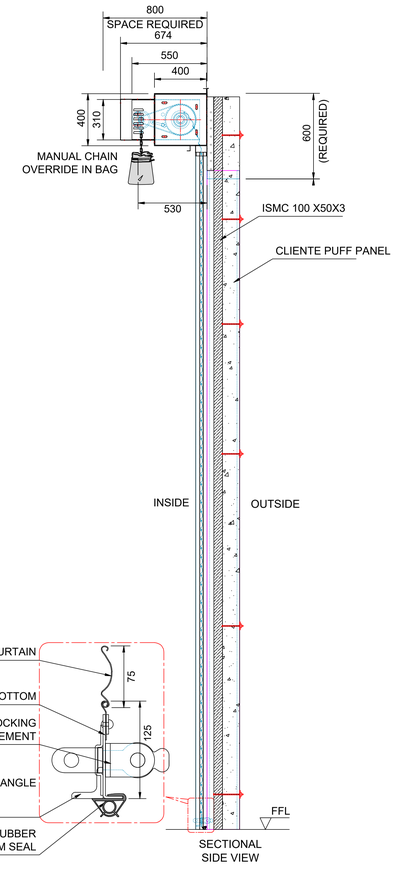

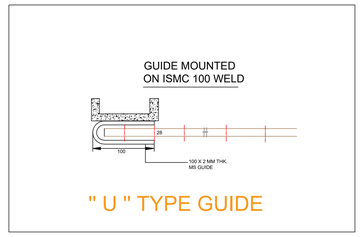

TECHNICAL SPECIFICATION:-

SR.	SPECIFICATION	DETAILS
1.	Description & Drive	Motorised Rolling Shutter (Indirect Drive) with Manual Chain Arrangment
2.	Location Area	Inside / Outside
3.	Mounting Surface	Side Brackets: Optional / Structure
4.	Slat	Curved 75 mm PPGI Sheet - 1.2 mm Thk.
5.	Bottom Profile	MS Plate 125 x 2 mm thick with Angle Stiffner & Rubber Seal
6.	Guide Profile	MS " U " Shape profile 100 X 2 mm Thk.
7.	Hood Cover & Motor Cover	Made of GI Sheet Thickness 0.9 mm
8.	Accessories	Push Button On Both Side

Scope :-

SR.	WORK CONTAINT	SCOPE
01.	All Cables & Ele.Conduits upto Control Box of Shutter	NIHVA
02.	All Cables & Ele.Conduits Above Control Box of Shutter	Client

SHUTTER SIZES :-

SR.	CLEAR WIDTH	CLEAR HEIGHT	QTY.
01	4500	4500	07


This drawing & designing is the property of NIHVA TECHNOLOGIES. Not to be sold or copied to any other concern.


TITLE :-
MOTORISED ROLLING SHUTTER


NIHVA TECHNOLOGIES PVT. LTD.
NIHVA TECHNOLOGIES PVT. LTD. PUNE
Tel : 020 66304033
Email:- info@nihva.com
Website:- www.nihva.com


	NAME	DATE
DRAWN	J.S.	19/01/2024
CHECK	A.K.	19/01/2024
APPROVAL	V.T.	19/01/2024

CLIENT - RINAC
PROJECT -ROLLING SHUTTER
FORMAT NO - NIHVA-DD-F-03
DWG. NO. : NIHVA/23-24/105 REV-00
SCALE: NTS WT: SHEET: 01 OF 01
ALL DIMENSION ARE IN mm
If any queries contact : design@nihva.com

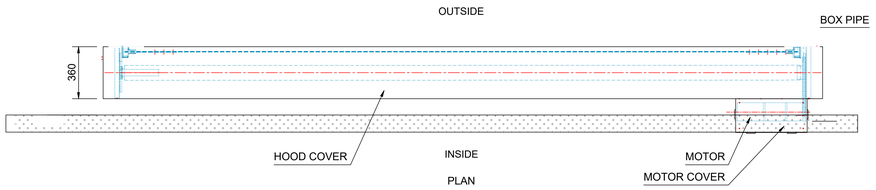

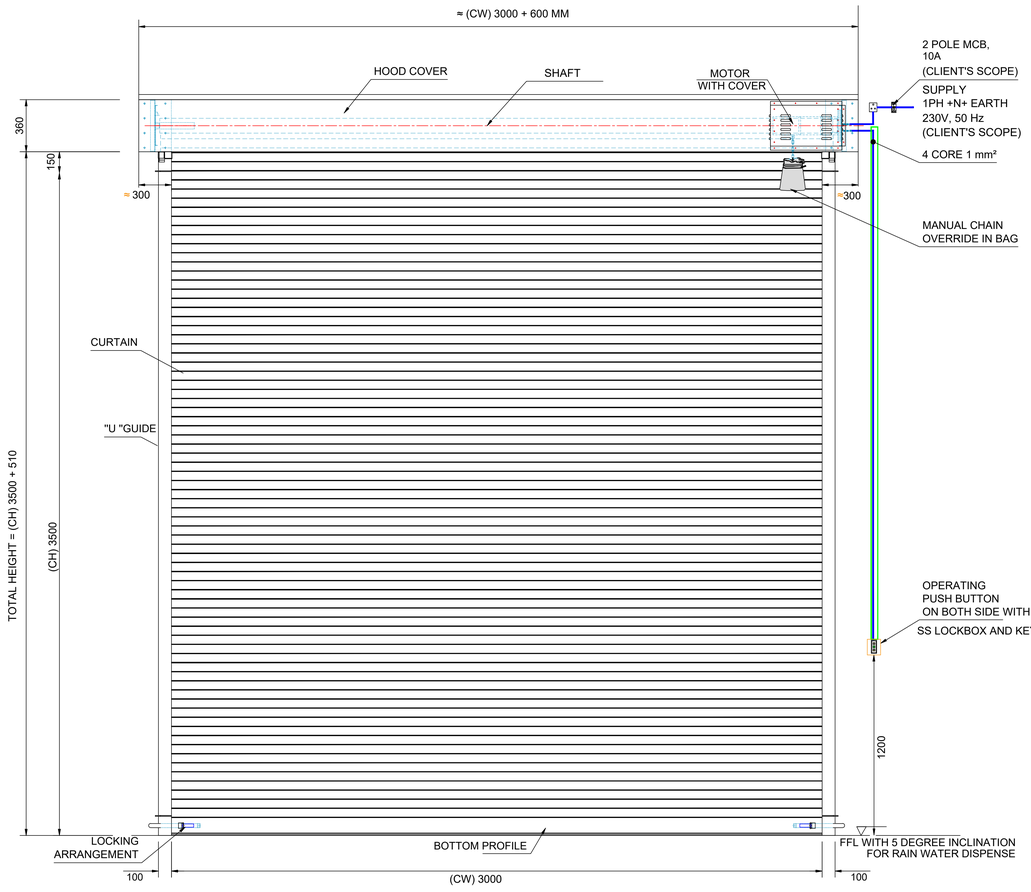

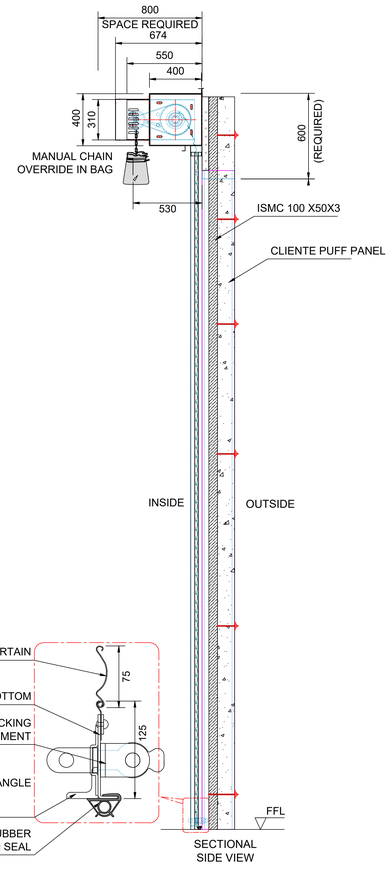

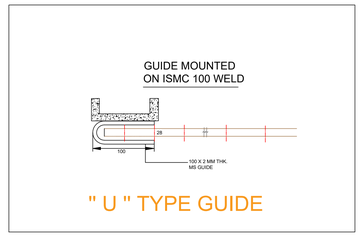

INSIDE ELEVATION

TECHNICAL SPECIFICATION:-

SR.	SPECIFICATION	DETAILS
1.	Description & Drive	Motorised Rolling Shutter (Indirect Drive) with Manual Chain Arrangment
2.	Location Area	Inside / Outside
3.	Mounting Surface	Side Brackets: Optional / Structure
4.	Slat	Curved 75 mm PPGI Sheet - 1.2 mm Thk.
5.	Bottom Profile	MS Plate 125 x 2 mm thick with Angle Stiffner & Rubber Seal
6.	Guide Profile	MS " U " Shape profile 100 X 2 mm Thk.
7.	Hood Cover & Motor Cover	Made of GI Sheet Thickness 0.9 mm
8.	Accessories	Push Button On Both Side

Scope :-

SR.	WORK CONTAINT	SCOPE
01.	All Cables & Ele.Conduits upto Control Box of Shutter	NIHVA
02.	All Cables & Ele.Conduits Above Control Box of Shutter	Client

SHUTTER SIZES :-

SR.	CLEAR WIDTH	CLEAR HEIGHT	QTY.
01	3000	3500	06


This drawing & designing is the property of NIHVA TECHNOLOGIES. Not to be sold or copied to any other concern.


TITLE :-
MOTORISED ROLLING SHUTTER


NIHVA TECHNOLOGIES PVT. LTD.
NIHVA TECHNOLOGIES PVT. LTD. PUNE
Tel : 020 66304033
Email:- info@nihva.com
Website:- www.nihva.com


	NAME	DATE
DRAWN	J.S.	19/01/2024
CHECK	A.K.	19/01/2024
APPROVAL	V.T.	19/01/2024

CLIENT - RINAC
PROJECT -ROLLING SHUTTER
FORMAT NO - NIHVA-DD-F-03
DWG. NO. : NIHVA/23-24/107 REV-00
SCALE: NTS WT: SHEET: 01 OF 01
ALL DIMENSION ARE IN mm
If any queries contact : design@nihva.com

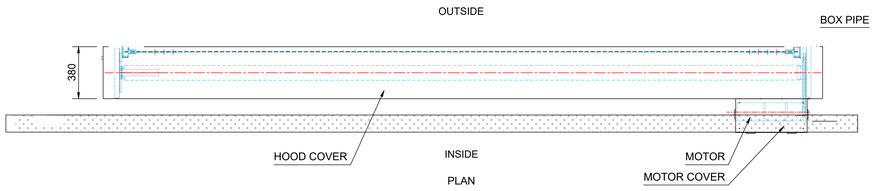

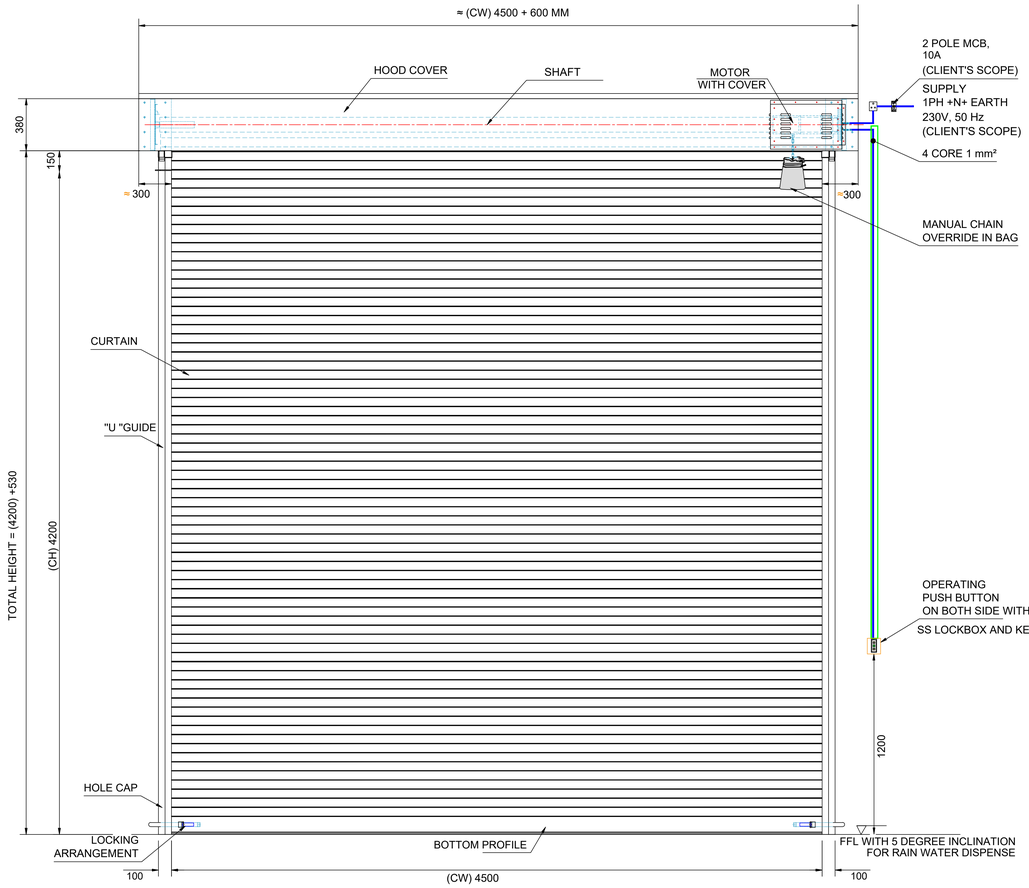

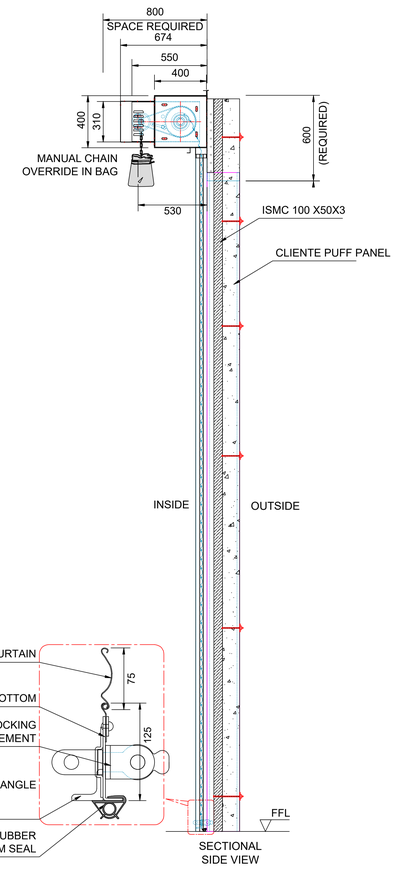

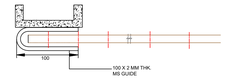

" U " TYPE GUIDE

INSIDE ELEVATION

TECHNICAL SPECIFICATION:-

SR.	SPECIFICATION	DETAILS
1.	Description & Drive	Motorised Rolling Shutter (Indirect Drive) with Manual Chain Arrangment
2.	Location Area	Inside / Outside
3.	Mounting Surface	Side Brackets: Optional / Structure
4.	Slat	Curved 75 mm PPGI Sheet - 1.2 mm Thk.
5.	Bottom Profile	MS Plate 125 x 2 mm thick with Angle Stiffner & Rubber Seal
6.	Guide Profile	MS " U " Shape profile 100 X 2 mm Thk.
7.	Hood Cover & Motor Cover	Made of GI Sheet Thickness 0.9 mm
8.	Accessories	Push Button On Both Side

Scope :-

SR.	WORK CONTAINT	SCOPE
01.	All Cables & Ele.Conduits upto Control Box of Shutter	NIHVA
02.	All Cables & Ele.Conduits Above Control Box of Shutter	Client

SHUTTER SIZES :-

SR.	CLEAR WIDTH	CLEAR HEIGHT	QTY.
01	4500	4200	01

This drawing & designing is the property of NIHVA TECHNOLOGIES. Not to be sold or copied to any other concern.


TITLE :-
MOTORISED ROLLING SHUTTER

	NAME	DATE
DRAWN	J.S.	19/01/2024
CHECK	A.K.	19/01/2024
APPROVAL	V.T.	19/01/2024


ALL DIMENSION ARE IN mm

NIHVA TECHNOLOGIES PVT. LTD.
NIHVA TECHNOLOGIES PVT. LTD. PUNE
Tel : 020 66304033
Email:- info@nihva.com
Website:- www.nihva.com

CLIENT - RINAC
PROJECT -ROLLING SHUTTER
FORMAT NO - NIHVA-DD-F-03
DWG. NO. : NIHVA/23-24/109 REV-00
SCALE: NTS WT: SHEET: 01 OF 01
If any queries contact : design@nihva.com

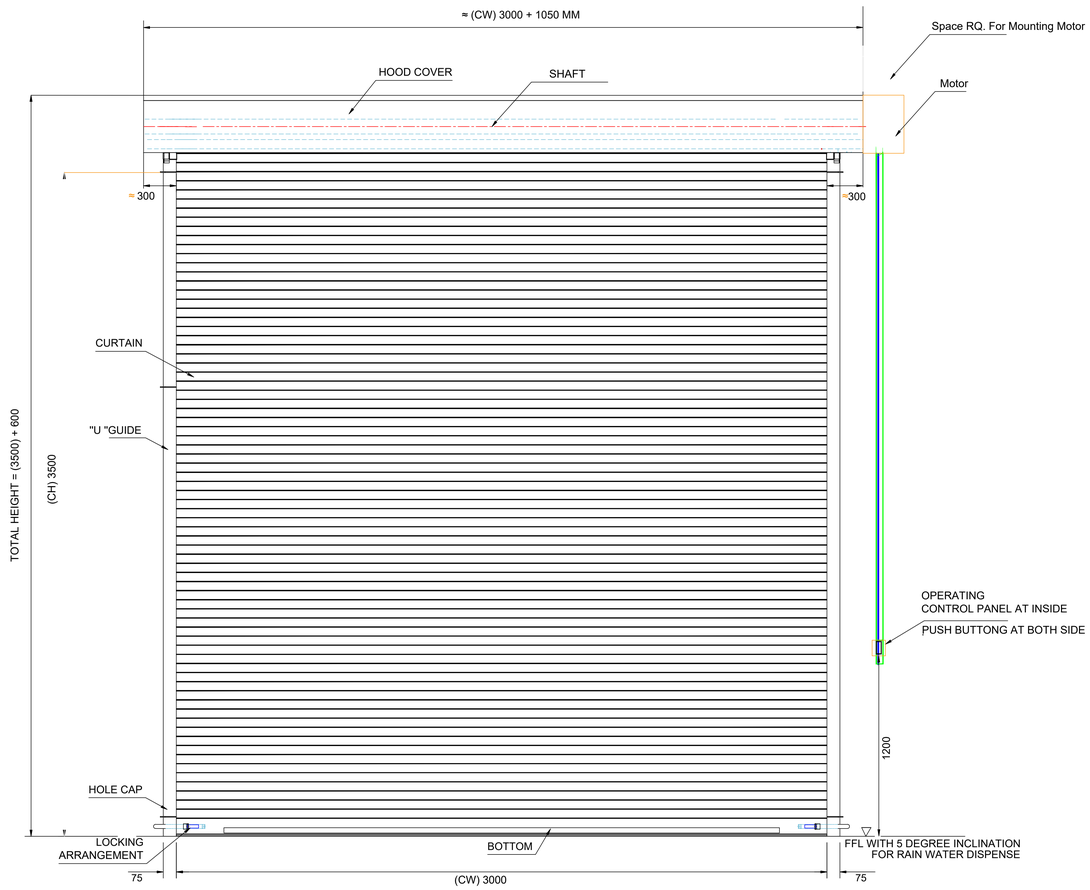

INSIDE ELEVATION

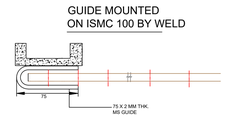

" U " TYPE GUIDE

TECHNICAL SPECIFICATION:-

SR.	SPECIFICATION	DETAILS
1.	Description	Double Wall PUF Insulated Motorised Rolling Shutter
2.	Drive & Motor	Jielong Make GKJS-400/1 1 Phase With Inbuilt Limit Switches.Manual Chain Option In Supply Failure. Torque: 65 Nm , Power :1.1kW
3.	Control Switch	IP 54 Rated Control Card With 3 stage Operating Push Button
4.	Slat	Galvanised Steel - 95 x 19 mm With PUF Filled Inside (THK-0.5 mm TCT)
5.	Density	48 kg /m3 (For Wind Speed 50 m/Sec)
6.	Bottom Profile	MS Plate 118 x 2 mm Thk. with Angle Stiffner With Rubber Seal
7.	Guide Profile	M.S." U " Shape profile 106 x 3 mm Thk.
8.	Hood Cover & Motor Cover	Made of GI Sheet Thickness 0.9 mm
9.	Accessories	Control Panel,Push Button On Both Side,In-Built Limit Switches
10.	Surface Finish	Powder Coating RAL-9006

Scope :-

SR.	WORK CONTAINT	SCOPE
01.	All Cables & Ele.Conduits upto Control Box of Shutter	NIHVA
02.	All Cables & Ele.Conduits Above Control Box of Shutter	Client

SHUTTER SIZES :-

SR.	CLEAR WIDTH	CLEAR HEIGHT	QTY.
01	3000	3500	01

This drawing & designing is the property of NIHVA TECHNOLOGIES. Not to be sold or copied to any other concern.

TITLE :-
DOUBLE WALL PUF INSULATED
MOTORISED ROLLING SHUTTER

	NAME	DATE
DRAWN	J.S.	19/01/2024
CHECK	A.K.	19/01/2024
APPROVAL	V.T.	19/01/2024

NIHVA
NIHVA TECHNOLOGIES PVT. LTD.

NIHVA TECHNOLOGIES
PVT. LTD. PUNE
Tel : 020 66304033
Email:- info@nihva.com
Website:- www.nihva.com

CLIENT - RINAC
PROJECT -ROLLING SHUTTER
FORMAT NO - NIHVA-DD-F-03
DWG. NO. : NIHVA/23-24/104 REV-01
SCALE: NTS WT: SHEET: 01 OF 01
ALL DIMENSION ARE IN mm
If any queries contact : design@nihva.com