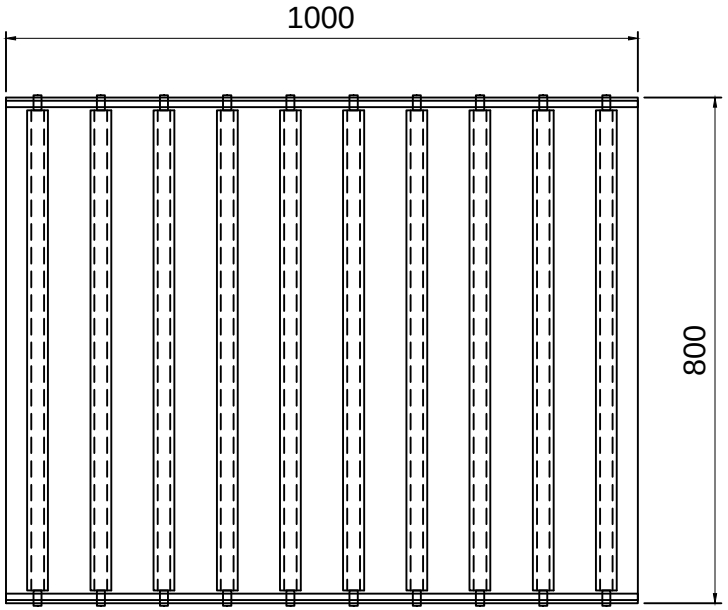

PLAN VIEW

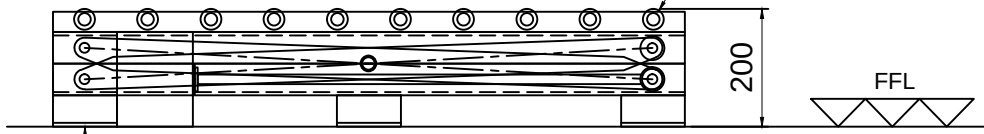

CLOSED POSITION

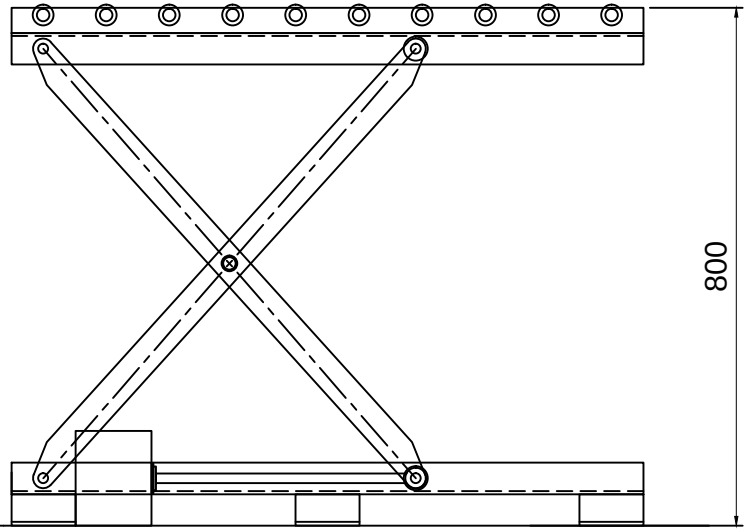

OPEN POSITION

TO BE GROUTED
AT FFL

M.O.C : SS304
(EXCLUDING DRIVE)

This drawing & design is the property of NIHVA TECHNOLOGIES. Not to be sold or copied to any other concern.

TITLE	SEMI ELECTRIC SCISSOR LIFT			NIHVA TECHNOLOGIES PVT. LTD. PUNE Tel : 020 66304033 Email:- info@nihva.com Website:- www.nihva.com	
	NAME	SIGN	DATE		
DRAWN	P.A		03.08.2020	CLIENT - INFINITY AUTOMATED SOLUTION	
CHECK	G.J		03.08.2020	PROJECT -	
APPRD.				SITE LOCATION - PUNE	
If any queries contact : design@nihva.com				DWG. NO. : NIHVA/20-21/0039	
ALL DIMENSION ARE IN mm				SCALE: NTS	WT: REV- 00