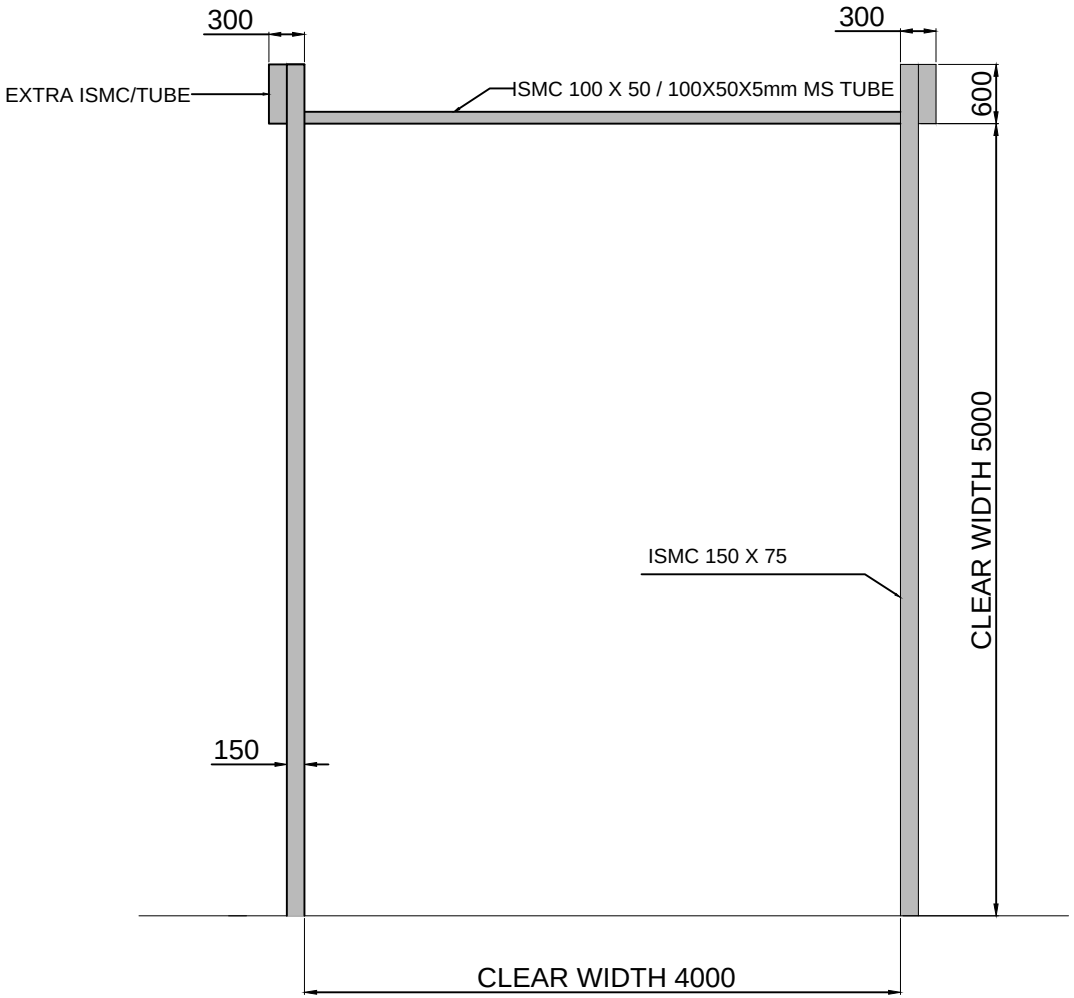


SR NO.	DESCRIPTION	WEIGHT
1.	ISMC 150 X 75 X 12.40 MTR	204.18 KG
2.	ISMC 100 X 50 X 4.00 MTR	38.36 KG
	TOTAL WEIGHT	242.54 KG

CLEAR WIDTH	CLEAR HEIGHT	QUANTITY
4000	5000	02

NOTE :
1. MATERIAL FOR ALL STRUCTURE = M.S

TOLERANCE - ±10mm & 20 kgs

DRAWN NAME	SIGN	REVISION	DATE	REVISION DETAILS

This drawing & design is the property of NIHVA TECHNOLOGIES. Not to be sold or copied to any other concern.

TITLE
STRUCTURE FOR GEAR OPERATED ROLLING SHUTTER

NIHVA TECHNOLOGIES PVT. LTD.

NIHVA TECHNOLOGIES PVT. LTD. PUNE
Tel : 020 66304033
Email:- info@nihva.com
Website:- www.nihva.com

	NAME	SIGN	DATE
DRAWN	SURAJ		17-12-2018
CHECK	PRADEEP		17-12-2018
APPRD.	R.D		17-12-2018

If any queries contact : design@nihva.com

ALL DIMENSION ARE IN mm

CLIENT - SYNERGY

PROJECT-EMBASSY INDUSTRIAL PARKS PVT. LTD.

SITE LOCATION - CHAKAN

DWG. NO. : NIHVA/18-19/0209 | REV- 00

SCALE: NTS | WT: | SHEET: 01 OF 01