



DRAWING

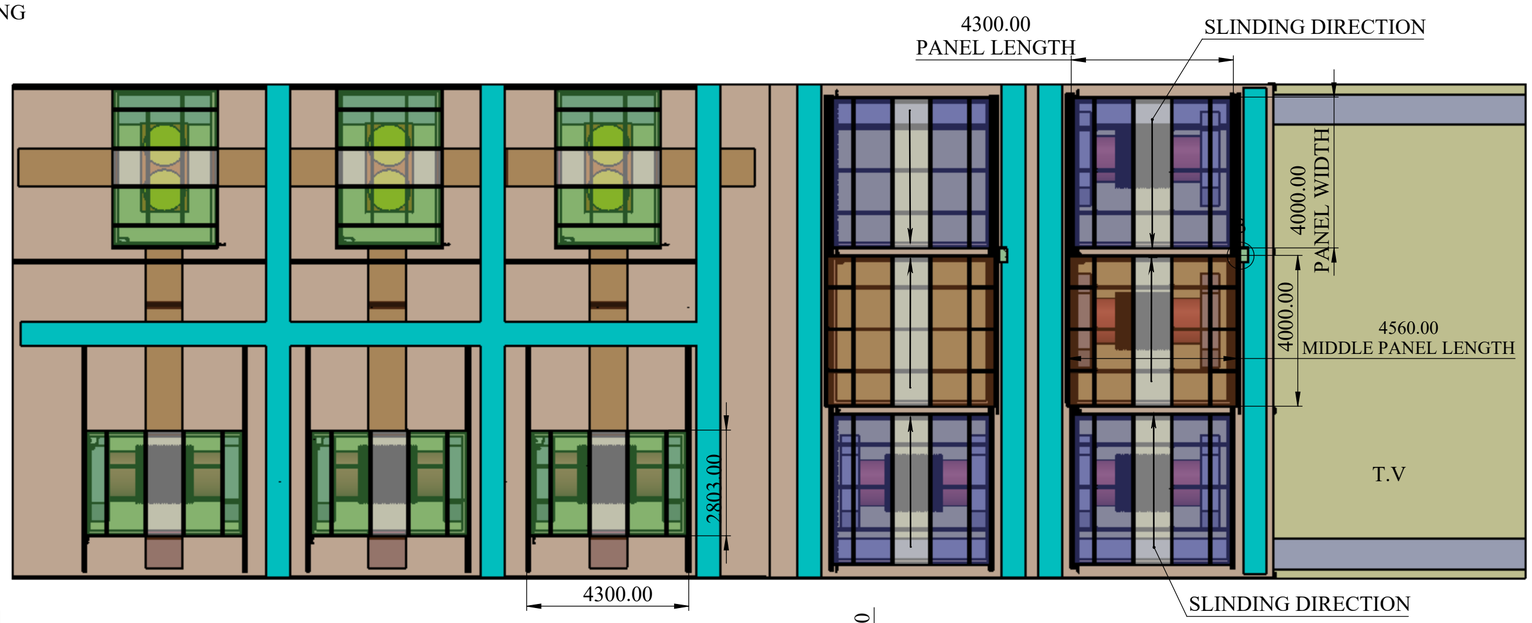

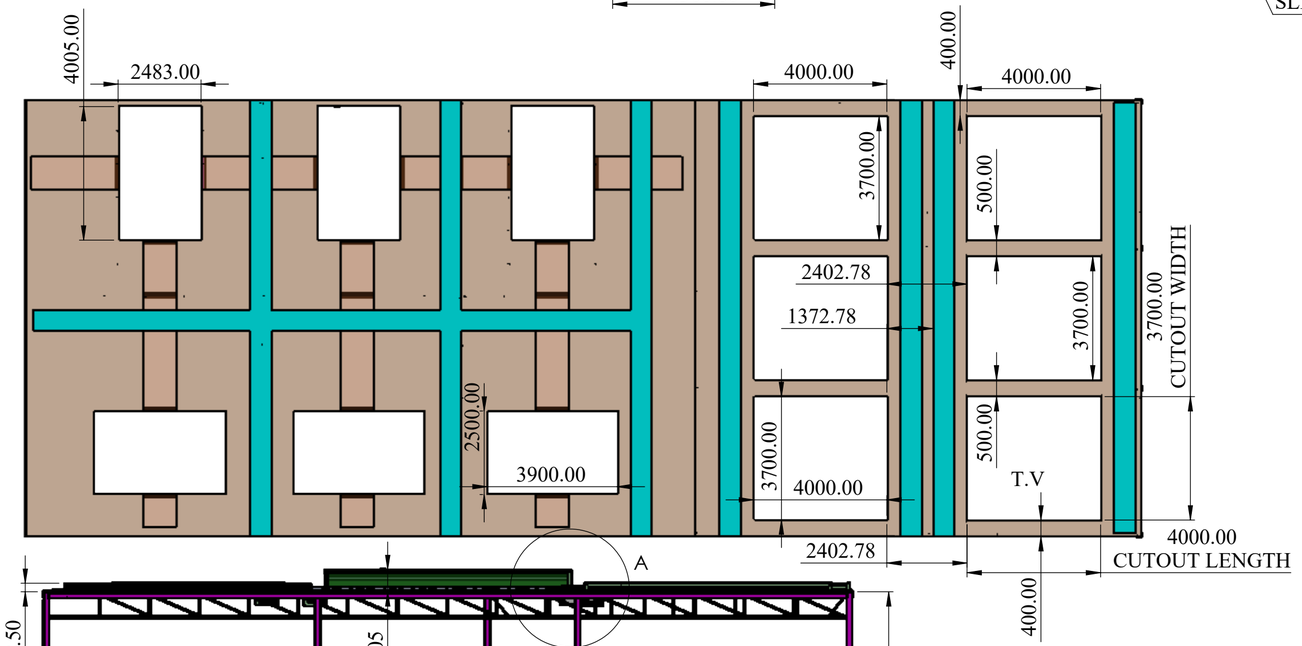


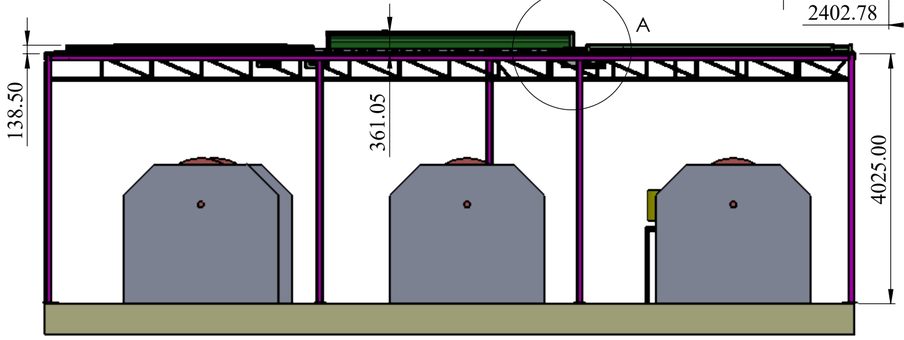

F.V

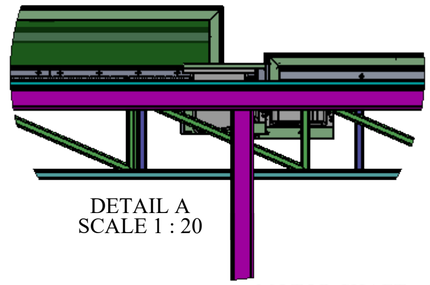

DETAIL A
SCALE 1 : 20

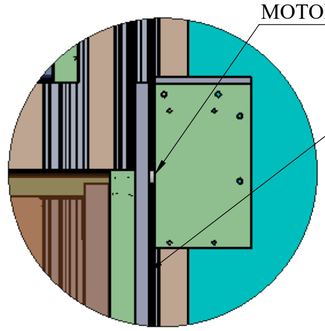

DETAIL B
SCALE 1 : 10

MIDDLE PANEL MOTOR &
RACK ARRANGMRNT

REV DESCRIPTION	DATE	REV NO
03. AIR TIGHTENING & DUST PROOF RUBBERIS ADDED	00-00-2025	REV 03
04. PANEL MODIFICATION	10-07-2025	REV 04
05. SAME UNIT ANTHOER THREE PANEL MODIFICATION	15-07-2025	REV 05

NOTE :

SPECIAL INSTRUCTION'S :

TITLE - ROOF AUTOMATION

DWG NO - NTPL-244-PM-001-00-00-00


NIHVA TECHNOLOGIES PVT.LTD.PUNE
Website - www.nihva.com


	NAME	SIGNATURE	DATE
DRAWN	V.W.		14-07-2025
CHK'D	S.W.		15-07-2025
APPV'D	V.T.		15-07-2025

PRODUCT - RETRACTABLE ROOF
PROJECT NO - NTPL-244-PM | REVISION - 05
SITE LOCATION -AHMADABAD | WEIGHT -
MATRIAL - | QTY - 1
If any queries contact - design.nihva@gmail.com
ALL DIMENSION ARE IN mm | A2
PROJECTION METHOD:
SCALE :
SHEET 1 OF 16

DRAWING

REV DESCRIPTION	DATE	REV NO
	15-07-2025	REV 05
1.		

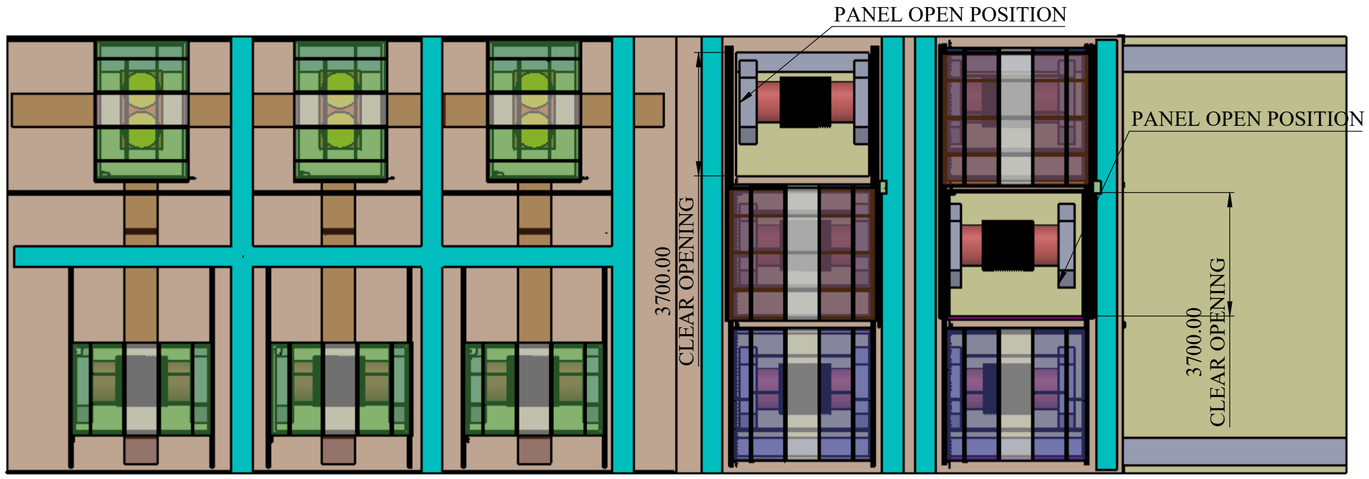

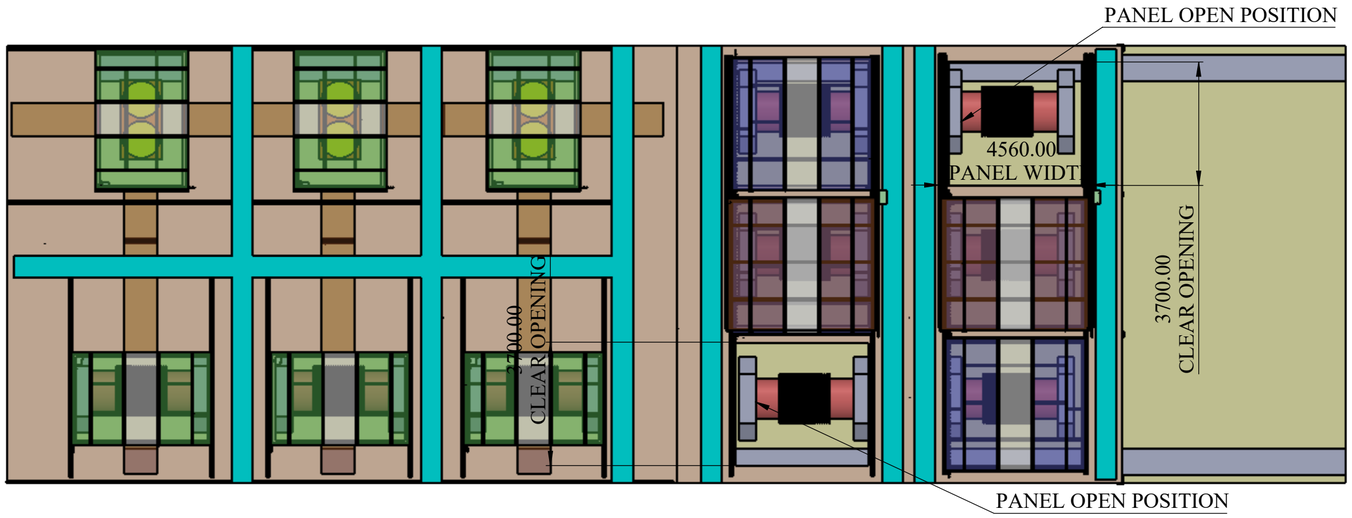

NOTE :

SPECIAL INSTRUCTION'S :

TITLE - ROOF AUTOMATION

DWG NO - NTPL-244-PM-001-00-00-00

NIHVA TECHNOLOGIES PVT.LTD.PUNE
Website - www.nihva.com

	NAME	SIGNATURE	DATE
DRAWN	V.W.		14-07-2025
CHK'D	S.W.		15-07-2025
APPV'D	V.T.		15-07-2025

PRODUCT - RETRACTABLE ROOF

PROJECT NO - NTPL-244-PM | REVISION - 05

SITE LOCATION - | WEIGHT -

MATRIAL - | QTY - 1


If any queries contact - design.nihva@gmail.com


ALL DIMENSION ARE IN mm | A2


PROJECTION METHOD:

SCALE :

DRAWING

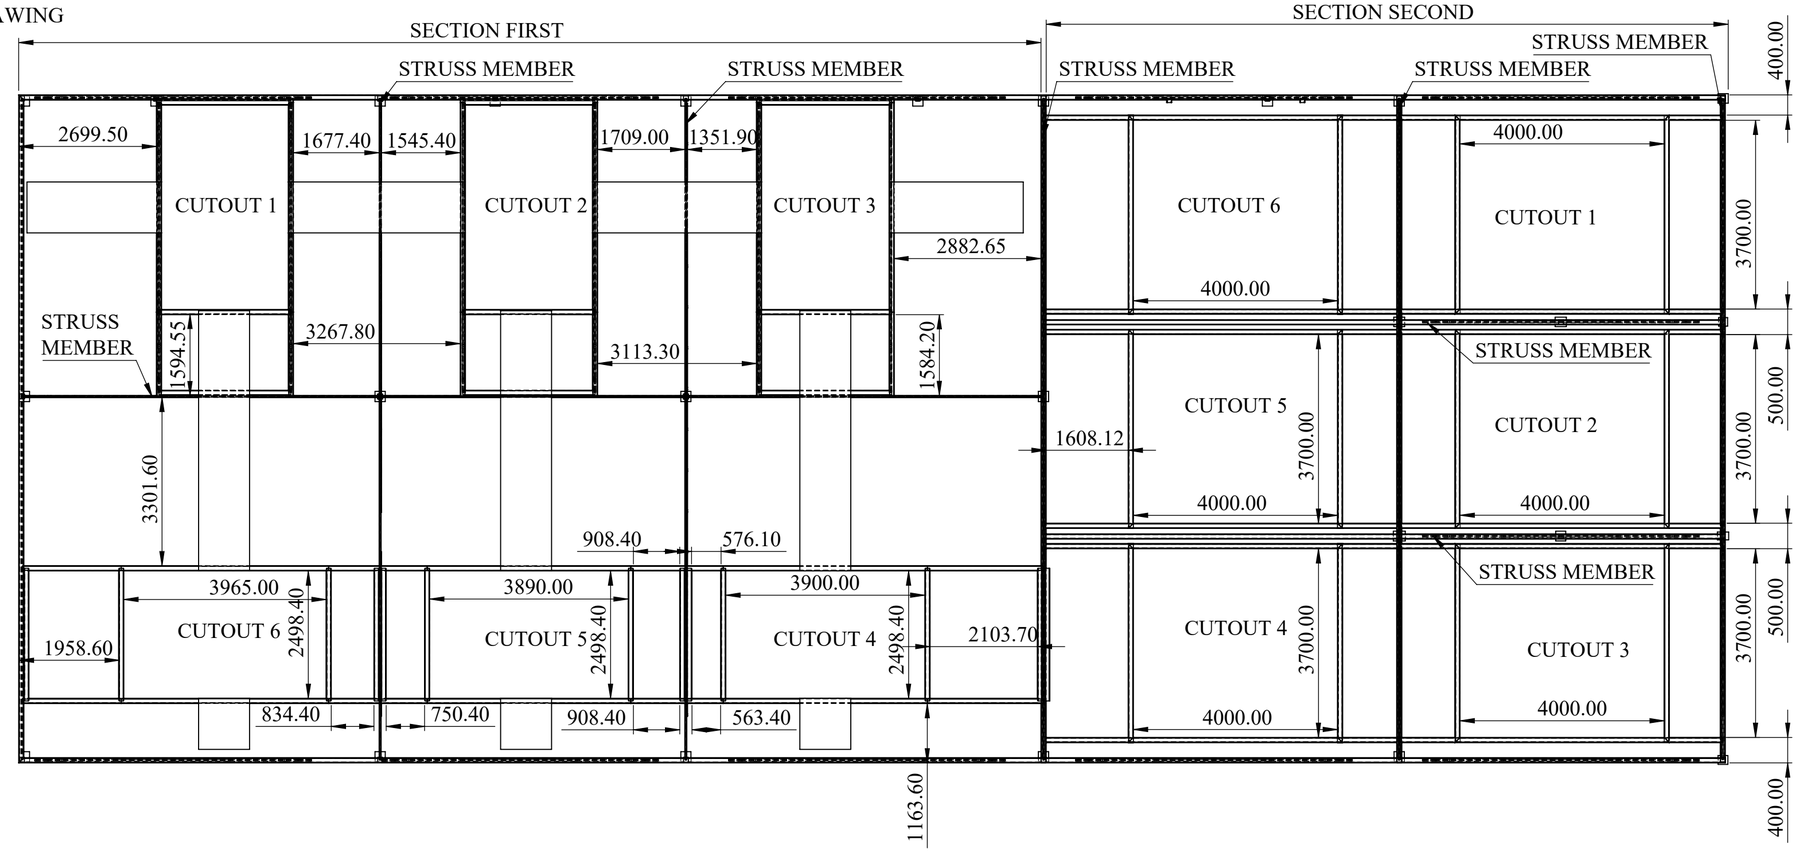

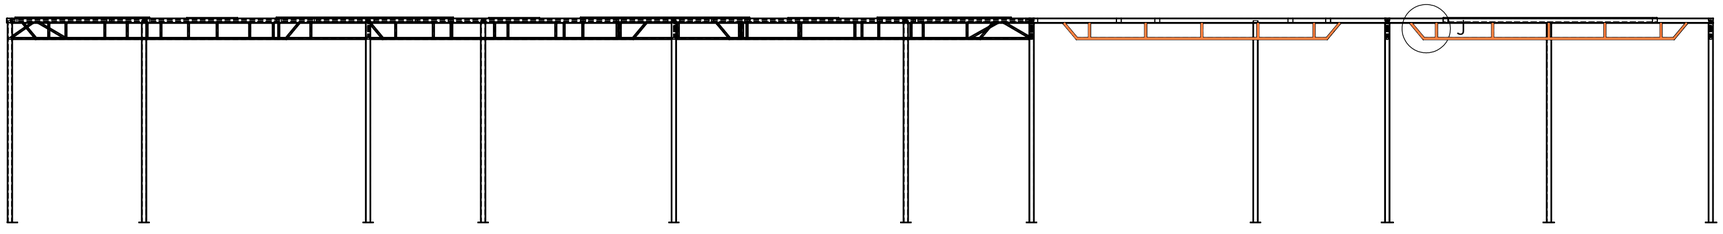

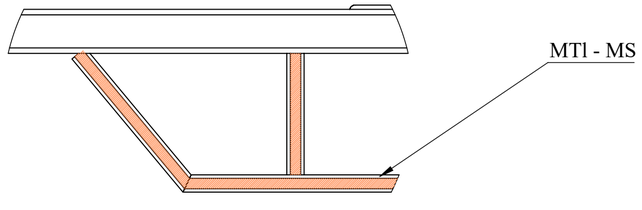

DETAIL J
SCALE 1 : 10

REV DESCRIPTION	DATE	REV NO
	04-07-2025	REV 00
REV_05_A : DIMENSION MENTIONED FROM STRUSS MEMBER	21-07-2025	REV_05_A

NOTE :

All Struss Member & Strengthning Member material - MS

SPECIAL INSTRUCTION'S :

TITLE - ROOF AUTOMATION			
DWG NO - NTPL-244-PM-001-00-00-00			
NIHVA Technologies Pvt. Ltd.	NIHVA TECHNOLOGIES PVT.LTD.PUNE Website - www.nihva.com		
	NAME	SIGNATURE	DATE
DRAWN	V.W.		21-07-2025
CHK'D	S.W.		22-07-2025
APPV'D	V.T.		22-07-2025
PRODUCT - RETRACTABLE ROOF			
PROJECT NO - NTPL-000-PM	REVISION - 05 A		
SITE LOCATION -	WEIGHT -		
MATRIAL -	QTY - 1		
If any queries contact - design.nihva@gmail.com	PROJECTION METHOD:	SCALE :	
ALL DIMENSION ARE IN mm	A2	SHEET 3 OF 16	