
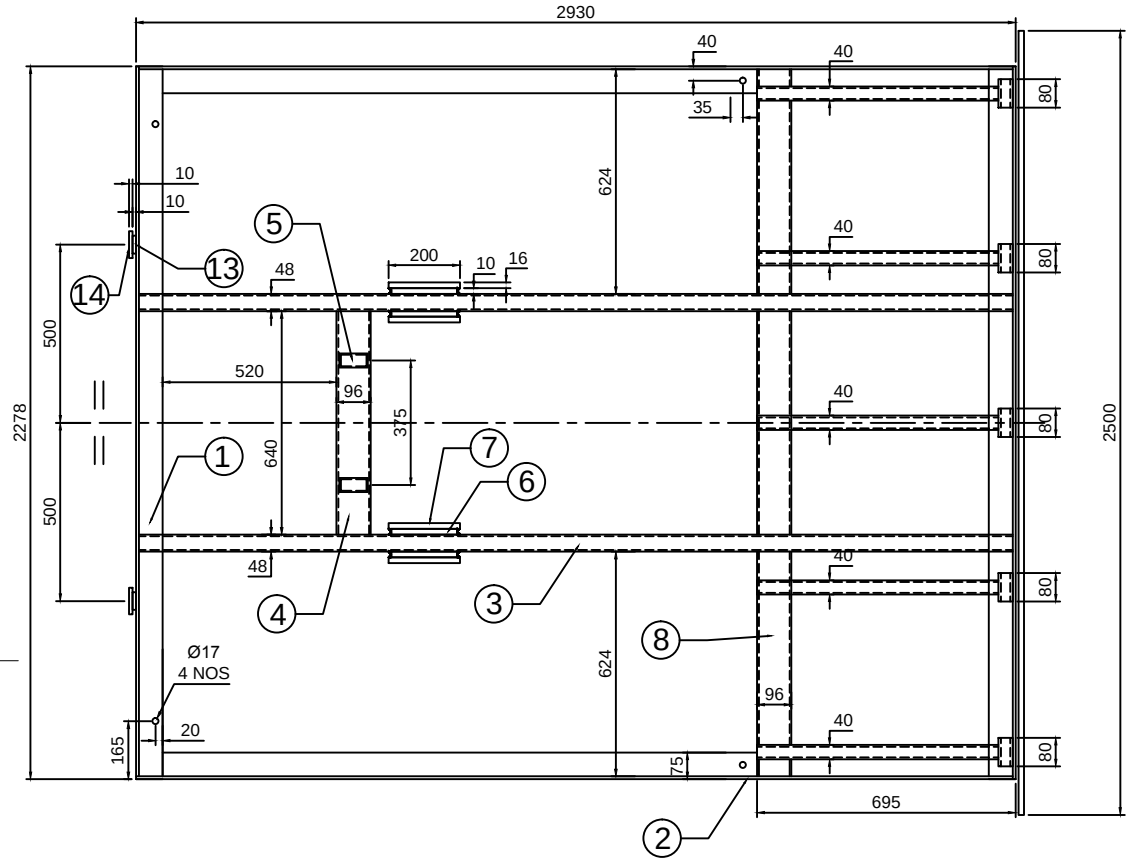


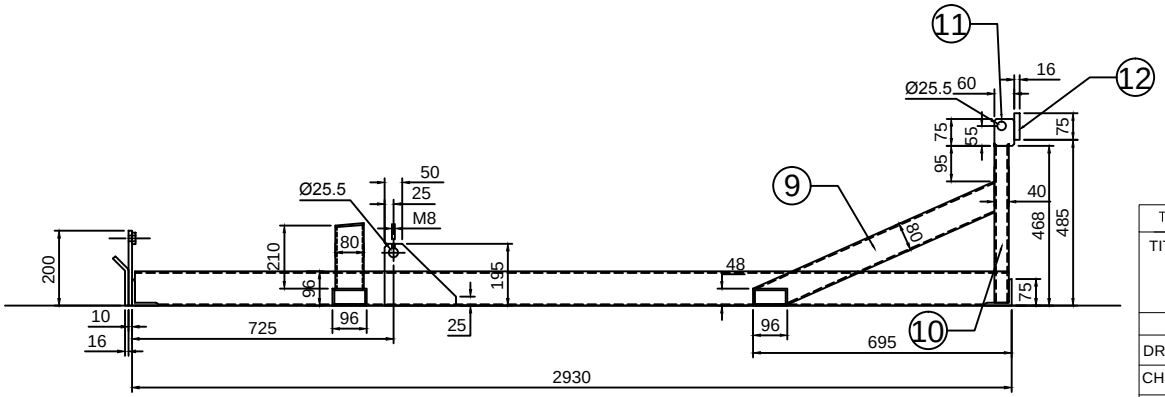

NOTE:~ MTL : MS

PART NO.	PART NAME	DESCRIPTION	QTY
1.	ISA	75 X 75 X 8 X 2258L	2 NOS
2.	ISA	75 X 75 X 8 X 2930L (NOTCH)	2 NOS
3.	R.TUBE	96 X 48 X 4.8 THK X 2915L (NOTCH)	2 NOS
4.	R.TUBE	96 X 48 X 4.8 THK X 640L	2 NOS
5.	R.TUBE	80 X 40 X 4 THK X 220L	2 NOS
6.	FLAT	80 X 10 X 180L	4 NOS
7.	FLAT	195 X 16 X 200L	4 NOS
8.	R.TUBE	96 X 48 X 4.8 THK X 624L (NOTCH)	2 NOS
9.	R.TUBE	80 X 40 X 4 THK X 720L (NOTCH)	5 NOS
10.	R.TUBE	80 X 40 X 4 THK X 460L	5 NOS
11.	SOLID	75 X 60 X 80L	5 NOS
12.	FLAT	75 X 16 X 2500L	1 NO
13.	FLAT	75 X 10 X 200L	2 NOS
14.	FLAT	75 X 16 X 250L	2 NOS

This drawing & design is the property of NIHVA TECHNOLOGIES. Not to be sold or copied to any other concern.

TITLE

BASE FRAME ASSLY

	NAME	SIGN	DATE
DRAWN	P.A		12.12.18
CHECK	P.A		12.12.18
APPRD.	P.A		12.12.18

If any queries contact : design@nihva.com

ALL DIMENSION ARE IN mm

NIHVA TECHNOLOGIES PVT. LTD.

NIHVA TECHNOLOGIES PVT. LTD. PUNE
Tel : 020 66304033
Email:- info@nihva.com
Website:- www.nihva.com

CLIENT -

PROJECT - DLAG1010

SITE LOCATION -

DWG. NO. : NIHVA/18-19/MFG/DLAG1010/004

SCALE: NTS | WT: | REV- 00