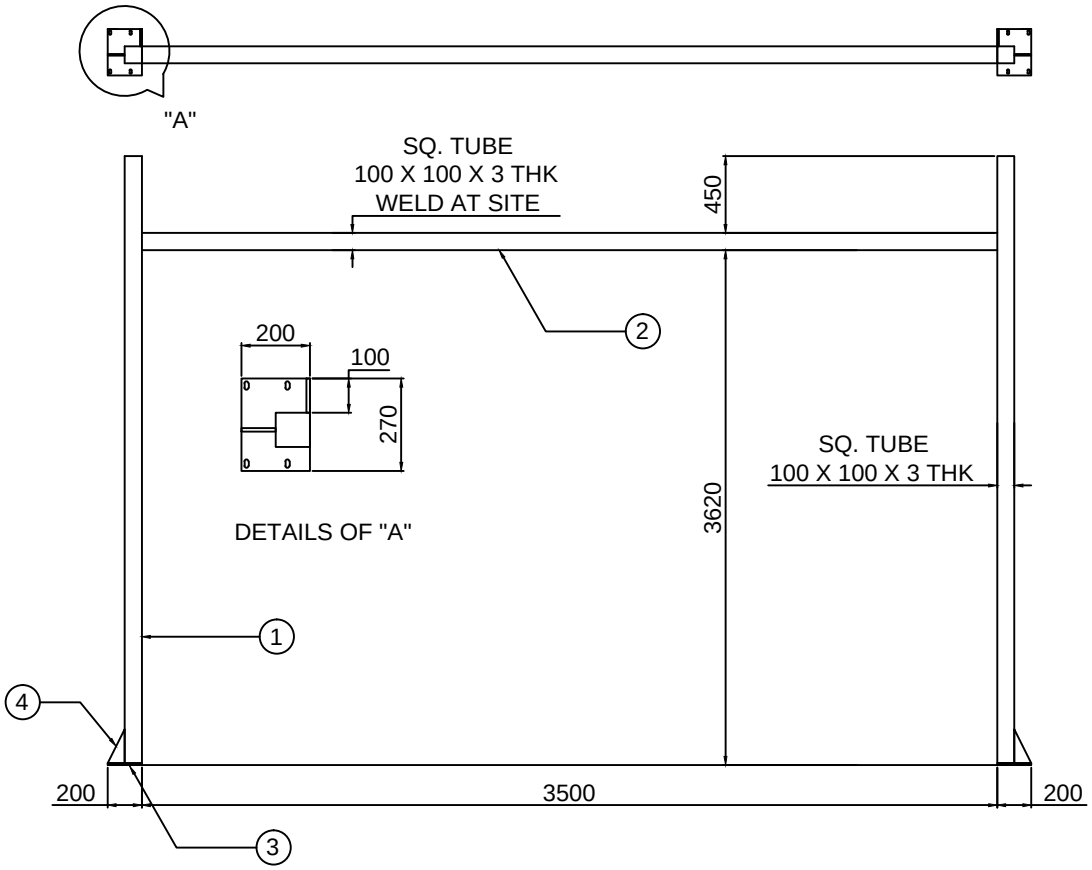


## STRUCTURE QTY : 2 NOS

| SR NO | DESCRIPTION | SPECIFICATION | QTY |
|---|---|---|---|
| 4 | RIBS | 100 X 10 X 200L | 4 NOS |
| 3 | PROFILE | 200 X 10 X 270L | 2 NOS |
| 2 | SQ. TUBE | 100 X 100 X 3 X 3500L | 1 NO |
| 1 | SQ. TUBE | 100 X 100 X 3 X 4170L | 2 NOS |

This drawing & design is the property of NIHVA TECHNOLOGIES. Not to be sold or copied to any other concern.

TITLE
STRUCTURE DRAWING

NIHVA TECHNOLOGIES PVT. LTD.
NIHVA TECHNOLOGIES PVT. LTD. PUNE
Tel : 020 66304033
Email:- info@nihva.com
Website:- www.nihva.com

| | NAME | SIGN | DATE |
|---|---|---|---|
| DRAWN | P.A | | 13.01.20 |
| CHECK | G.J | | 13.01.20 |
| APPV'ED | | | |

CLIENT :-
PROJECT :-
LOCATION :-
If any queries contact : design@nihva.com
DWG. NO. :- NIHVA/19-20/VDR/281
REV.:-R00
ALL DIMENSION ARE IN mm
SCALE: NTS
WT:
SHEET: 01 OF 01