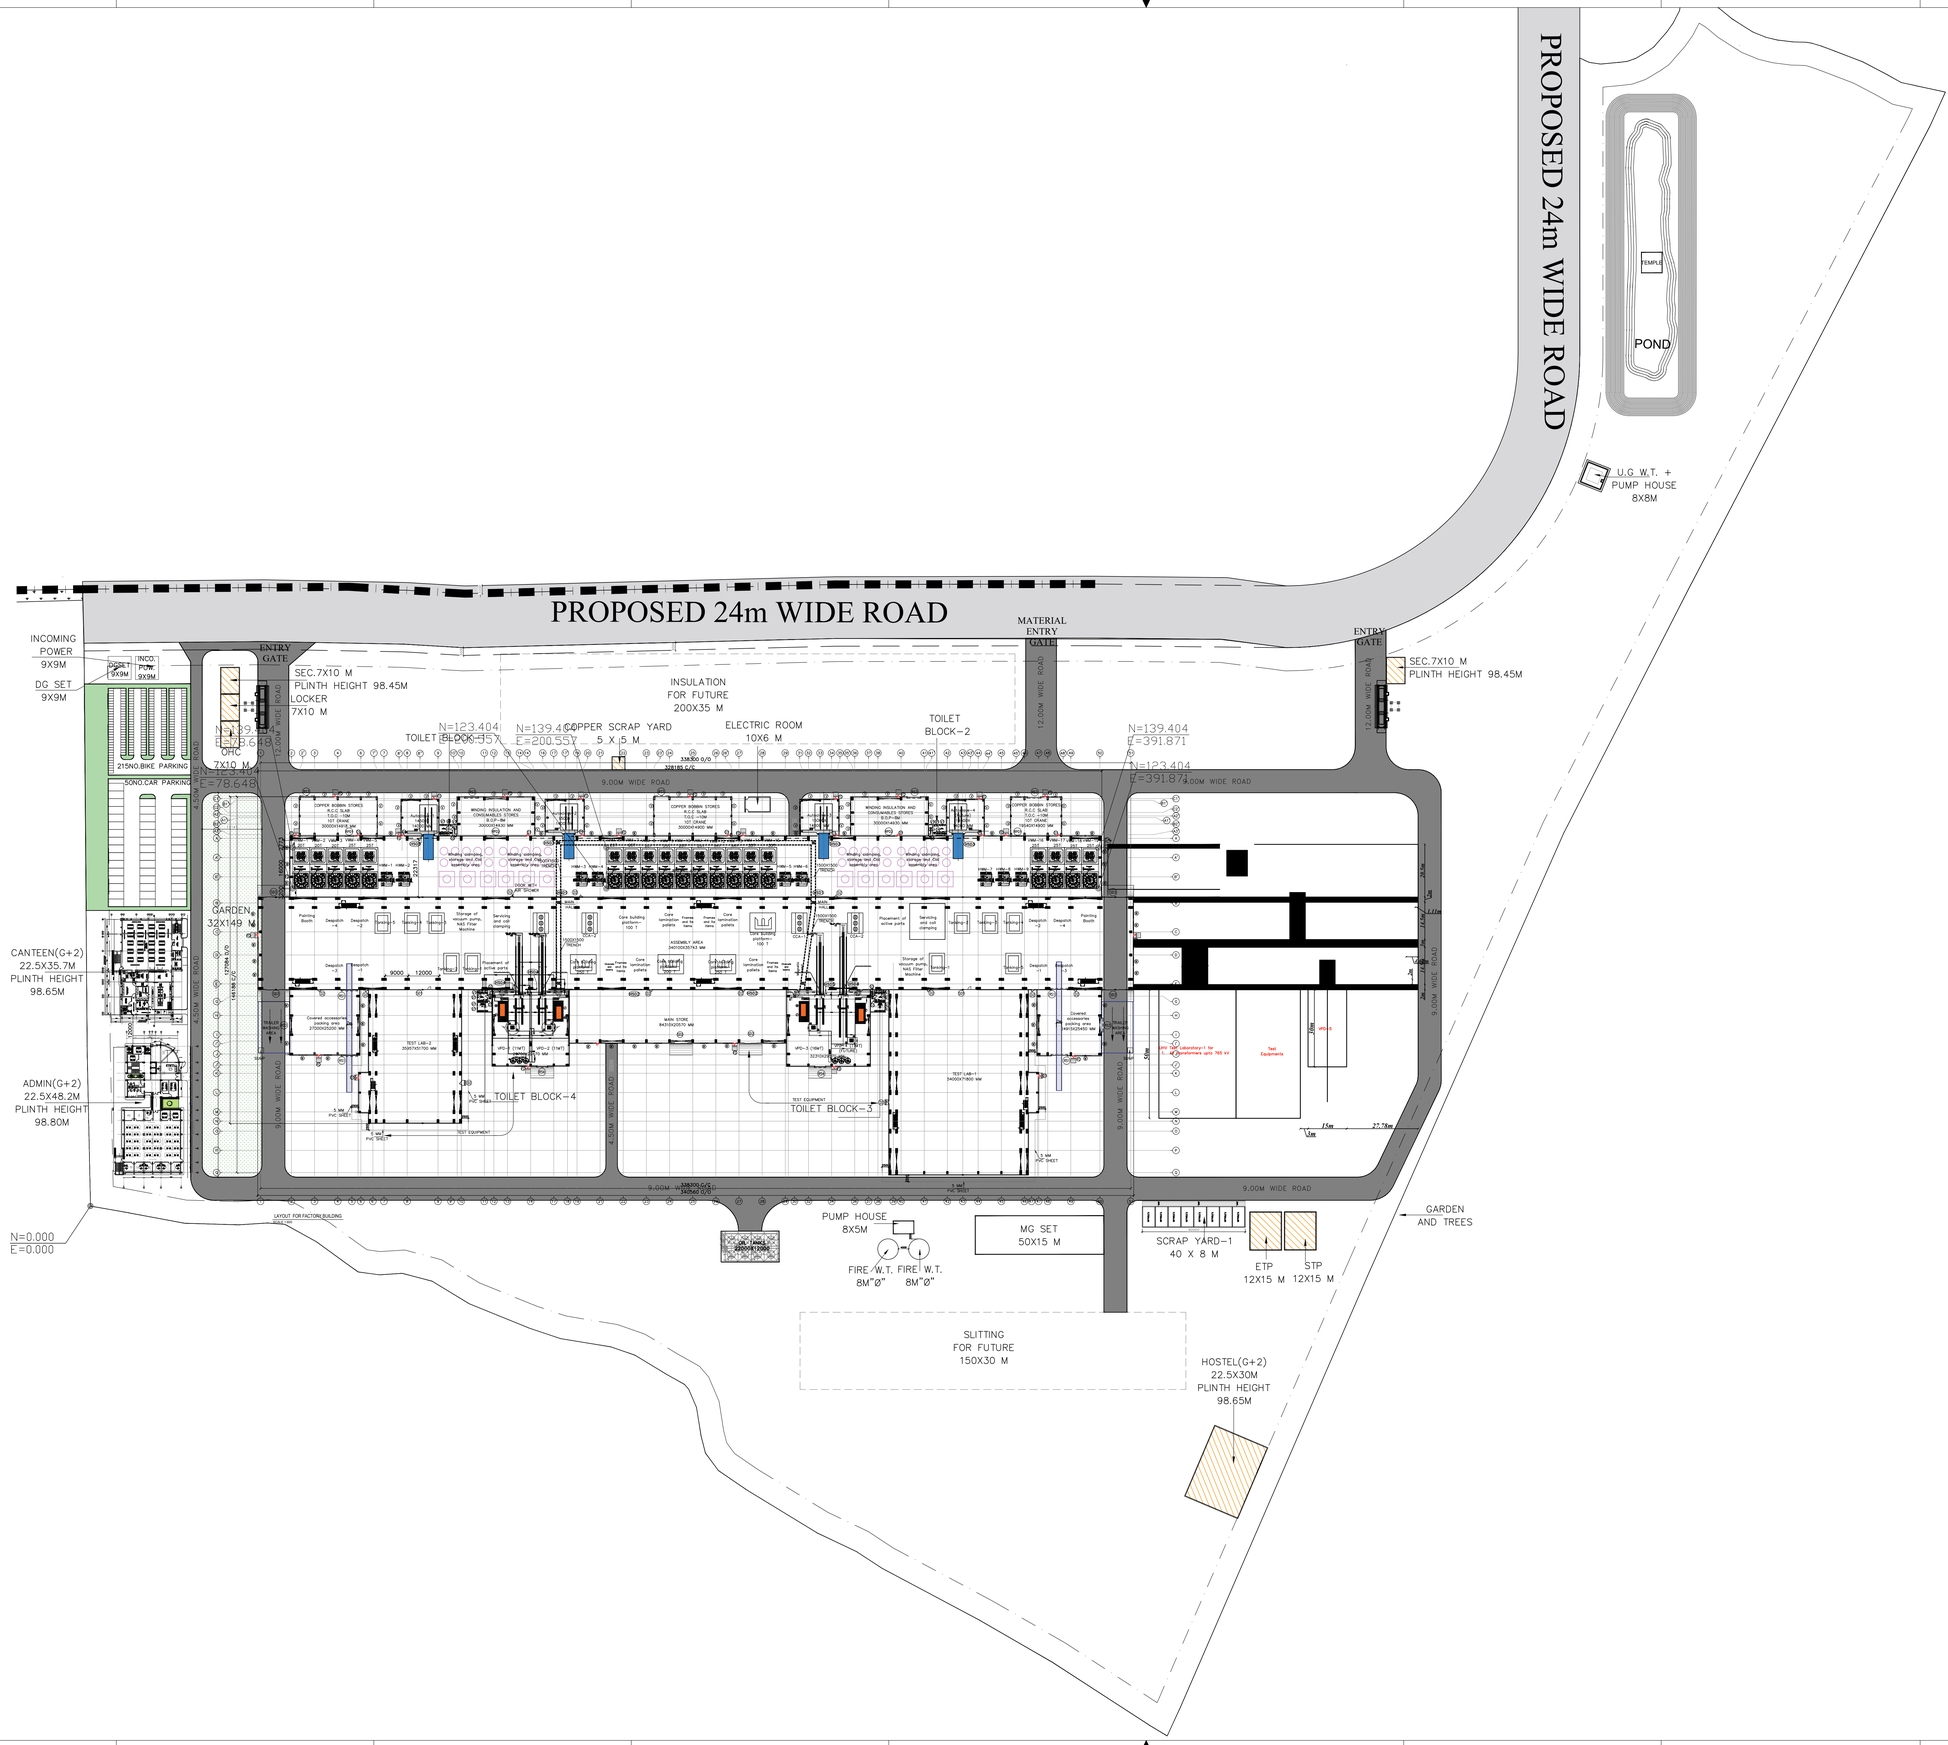


REFERENCE DRAWINGS

SR.NO.	DRAWING TITLE	DRAWING NO.

NOTE :-

1. DO NOT SCALE THE DRAWING. REFER TO WRITTEN DIMENSIONS ONLY. ALL MEASUREMENTS MUST BE CHECKED AND VERIFIED AT SITE. ANY DISCREPANCY FOUND,TO BE NOTIFIED TO THE CONSULTING ENGINEER BEFORE EXECUTION.
2. ALL DIMENSIONS ARE IN MM.& ALL LEVELS ARE IN METERS UNLESS OTHERWISE SPECIFIED.
3. F.G.L & F.R.L AS PER SITE ROAD LAYOUT PLAN.

ABBREVATION :-

N.G.L	= FINISHED GROUND LEVEL
F.G.L.	= FINISHED GROUND LEVEL
F.R.L.	= FINISHED ROAD LEVEL
F.F.L.	= FINISHED FLOOR LEVEL
T.O.C.	= TOP OF CONCRETE
T.O.W.	= TOP OF WALL
B.O.C.	= BOTTOM OF CONCRETE.
P.S.	= PLUMBING SHAFT
U.S.	= UTILITY SHAFT
D.B.	= DISTRIBUTION BOX

LEGEND :-

- 230MM THK. BRICK MASONRY WALL
- 115MM THK. BRICK MASONRY PARTITION WALL
- 200MM / 100MM THK. AAC / CONC. BLOCK MASONRY WALL
- PLATFORM AT TERRACE FFL. LVL. 150MM HIGH
- HOLD
- REVISION

KEY - PLAN :

N

REV.	DATE	DESCRIPTION	DRN.	CHK.	APP.	PRN.
R3	22-12-25	FAC.PLAN OPENING CHANGE	JP	SS	GJT	EMAIL
R3	15-12-25	FAC.PLAN OPENING CHANGE	JP	SS	GJT	EMAIL
R3	08-12-25	ADM. & CAN. BUILD. BETWEEN DIST. 12.00M	RS	SS	GJT	EMAIL
R2	12-11-25	ISSUED FOR APPROVAL (ELECTRICAL ROOM)	JP	GJT	GJT	EMAIL
R2	08-11-25	AS PER DISCUSSION IN MEETING	JP	GJT	GJT	EMAIL
R1	06-11-25	ISSUED FOR APPROVAL	JP	GJT	GJT	EMAIL
R0	01-10-25	ISSUED FOR APPROVAL	JP	GJT	GJT	EMAIL

ISSUED FOR

☐ INFORMATION ☑ APPROVAL ☐ CONSTRUCTION
☐ ENQUIRY ☐ ORDER ☐ REVIEW

CLIENT : **TRANSFORMER FACT (45000 MVA) FOR CG POWER AT JAHANGIRPURA**

PROJECT : 45000 MVA PLANT

CONSULTANT : SHAH & TALATI Design & Engineering

9th FLOOR, KIRTI TOWER, TILAK ROAD, VADODARA-390001, GUJARAT, INDIA.
PHONE : +91-265-2440701 / 2440726
E-MAIL : design@shahntalati.com
WEBSITE : www.shahntalati.com

PROJECT NO. :- **2537**

TITLE :- **SITE LAYOUT**

DRAWN BY	RITESH		R3 22 12 25
CHECKED BY	GJT		
APPROVED BY	GJT		
DRAWING NO.	**2537-GEN-A01-SH1-A1-R3**		SHEET 1 OF 1
SCALE : 1:1200			

THIS DOCUMENT OR DRAWING IS THE PROPERTY OF SHAH & TALATI CONSULTING ENGINEERS AND SHALL NOT, UNDER ANY CIRCUMSTANCES, BE TOTALLY OR PARTIALLY, DIRECTLY OR INDIRECTLY, TRANSFERRED, REPRODUCED, COPIED, DISCLOSED OR USED WITHOUT SHAH & TALATI'S PRIOR WRITTEN CONSENT.

A1