
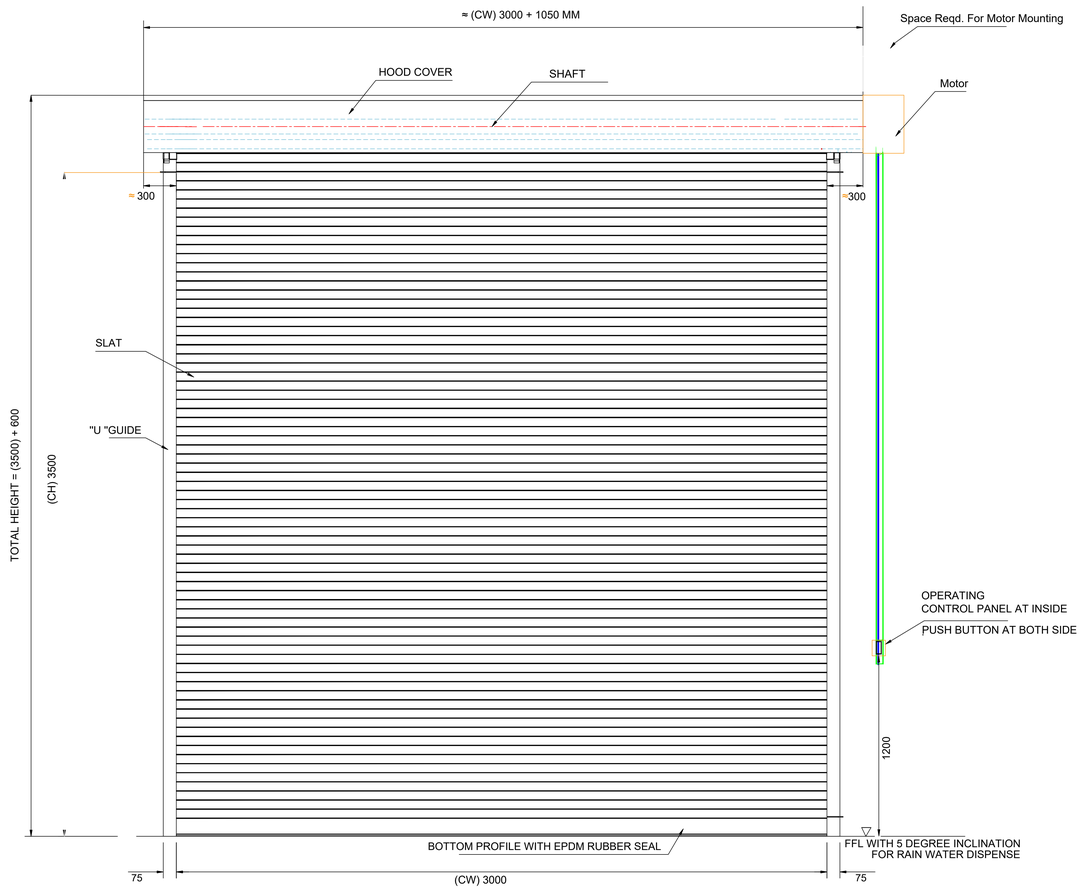


INSIDE ELEVATION

GUIDE MOUNTED
ON ISMC 100 BY WELD

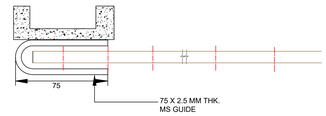

" U " TYPE GUIDE

TECHNICAL SPECIFICATION:-

SR.	SPECIFICATION	DETAILS
1.	Description	Double Wall PUF Insulated Motorised Rolling Shutter
2.	Drive & Motor	Jielong Make GKJS-400/11 3 Phase With Inbuilt Limit Switches.Manual Chain Option In Supply Failure. Torque: 65 Nm , Power :1.1kW
3.	Control Switch	IP 54 Rated Control Card With 3 stage Operating Push Button
4.	Slat	Galvanised Steel - 95 x 19 mm With PUF Filled Inside (THK-0.5 mm TCT)
5.	Density	48 kg /m3 (For Wind Speed 50 m/Sec)
6.	Bottom Profile	MS Plate 100 x 3 mm Thk. with Angle Stiffner
7.	Guide Profile	M.S." U " Shape profile 75 x 2.5 mm Thk.
8.	Hood Cover & Motor Cover	Made of GI Sheet Thickness 0.9 mm
9.	Accessories	Control Panel,Push Button On Both Side,In-Built Limit Switches
10.	Surface Finish	Powder Coating RAL-9006

SHUTTER SIZES :-

SR.	CLEAR WIDTH	CLEAR HEIGHT	QTY.
01	3000	3500	01

This drawing & designing is the property of NIHVA TECHNOLOGIES. Not to be sold or copied to any other concern.

TITLE :-
DOUBLE WALL PUF INSULATED
MOTORISED ROLLING SHUTTER

NIHVA
NIHVA TECHNOLOGIES PVT. LTD.

NIHVA TECHNOLOGIES
PVT. LTD. PUNE
Tel : 020 66304033
Email:- info@nihva.com
Website:- www.nihva.com

	NAME	DATE
DRAWN	J.S.	14/03/2024
CHECK	A.K.	14/03/2024
APPROVAL	V.T.	14/03/2024

CLIENT - RINAC
PROJECT -ROLLING SHUTTER
FORMAT NO - NIHVA-DD-F-03
DWG. NO. : NIHVA/23-24 REV-00
SCALE: NTS WT: SHEET: 01 OF 01
ALL DIMENSION ARE IN mm
If any queries contact : design@nihva.com