



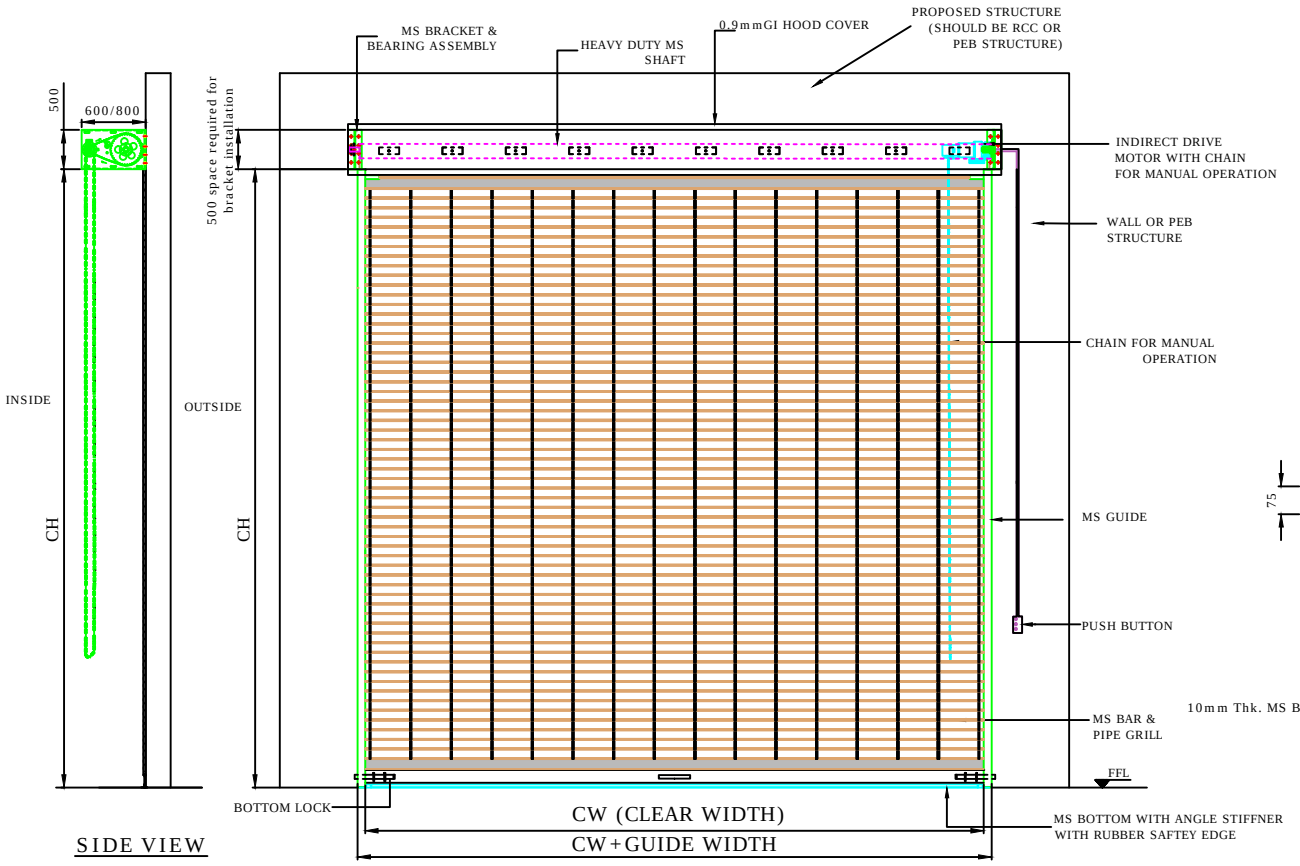


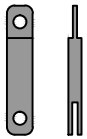

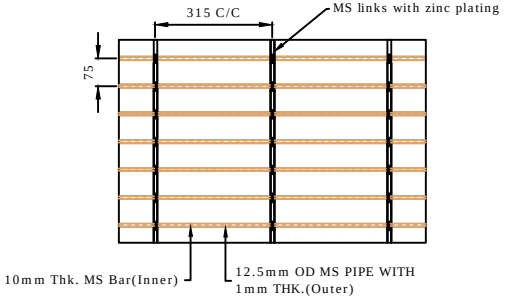

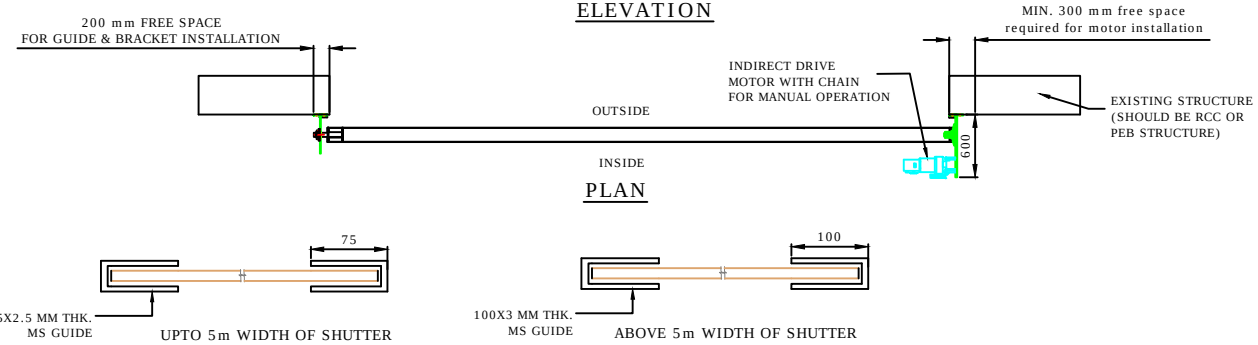

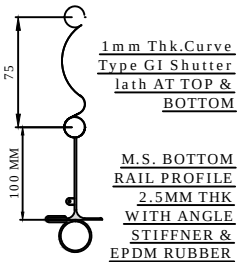

DIMENSION :		
CLEAR WIDTH	CLEAR HEIGHT	QUANTITY

MATERIAL :

THICKNESS :

NOTE- 1.Shutter will be powder coated with approved color shade.
2. Revision 2- Pattern of grill has been revised or changed.

NIHVA TECHNOLOGIES PVT. LTD. PUNE
Email:- info@nihva.com
Website:- www.nihva.com

TITLE:

G.A. MOTORIZED GRILLED ROLLING SHUTTER

CLIENT'S APPROVAL :

CLIENT - ADANI

PROJECT - WESTERN HEIGHTS PROJECT

SITE LOCATION - MUMBAI

DWG. NO. : NIHVA/16-17/170/R02

SCALE: NTS	WT:	SHEET:1 OF 1
DRAWN BY: OMKAR	DATE: 10-03-2017	
CHECK : SAGAR P.	DATE: 10-03-2017	
APPROVED : R.K.	DATE: 10-03-2017	

If any queries contact : projects@nihva.com

NOTE: ALL DIMENSIONS ARE IN mm

THIS DRAWING & DESIGN IS THE PROPERTY OF NIHVA TECHNOLOGIES. NOT TO BE SOLD OR COPY TO ANY OTHER CONCERN.