


DRAWING

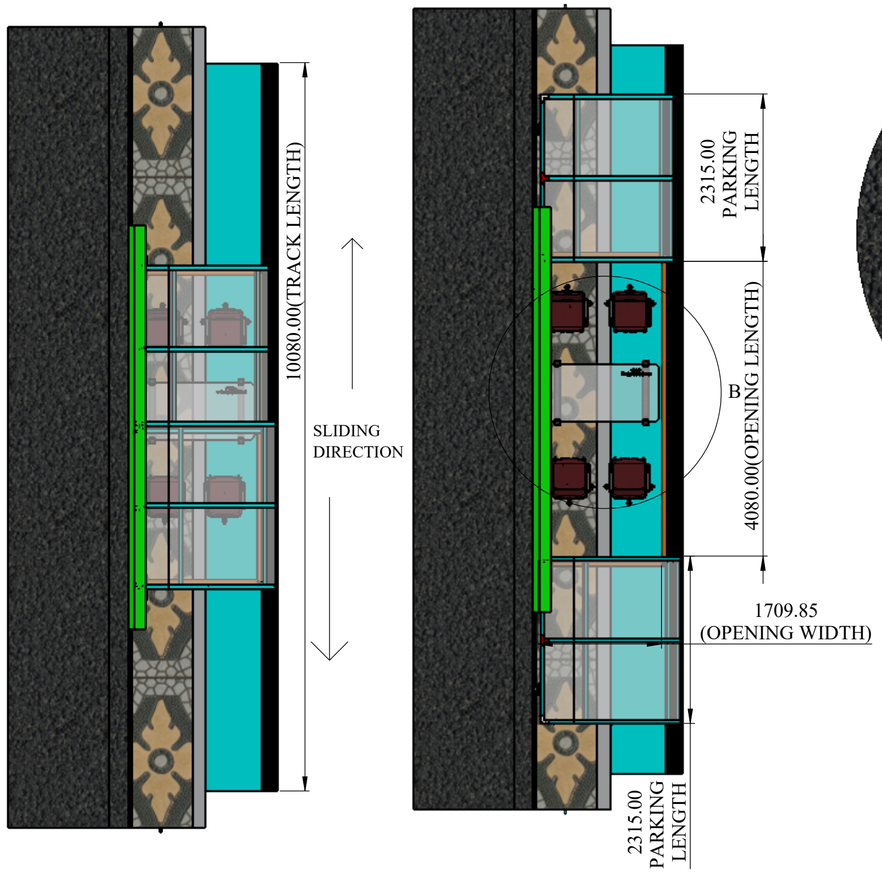


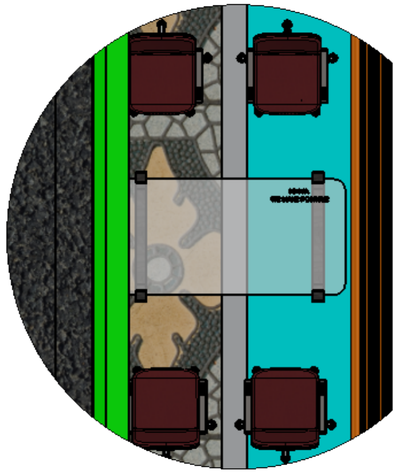

DETAIL B
SCALE 1 : 30

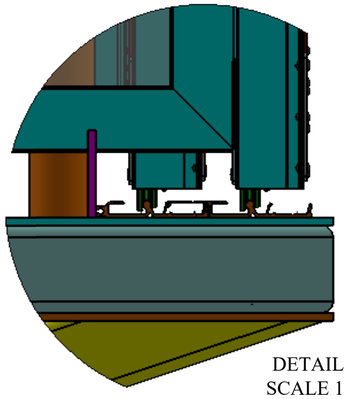


DETAIL A
SCALE 1 : 4

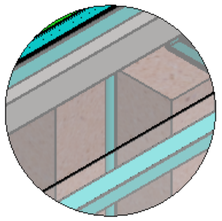



DETAIL C
SCALE 1 : 10
GUTTER ARRANGEMENT


TRACK MOUNTING

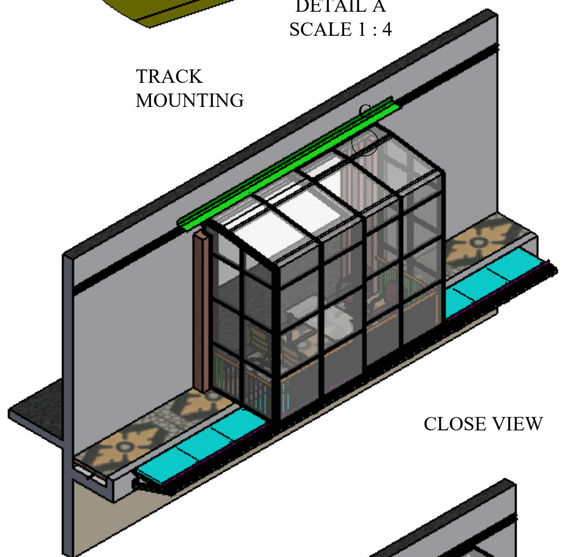

CLOSE VIEW

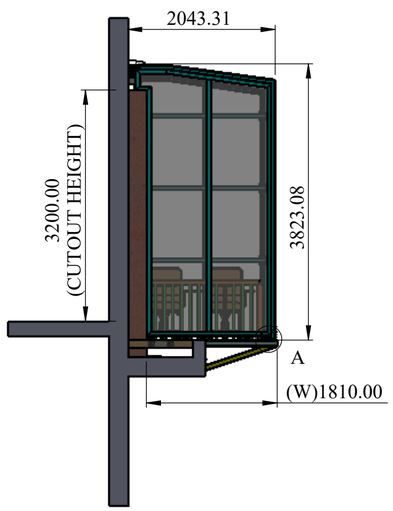

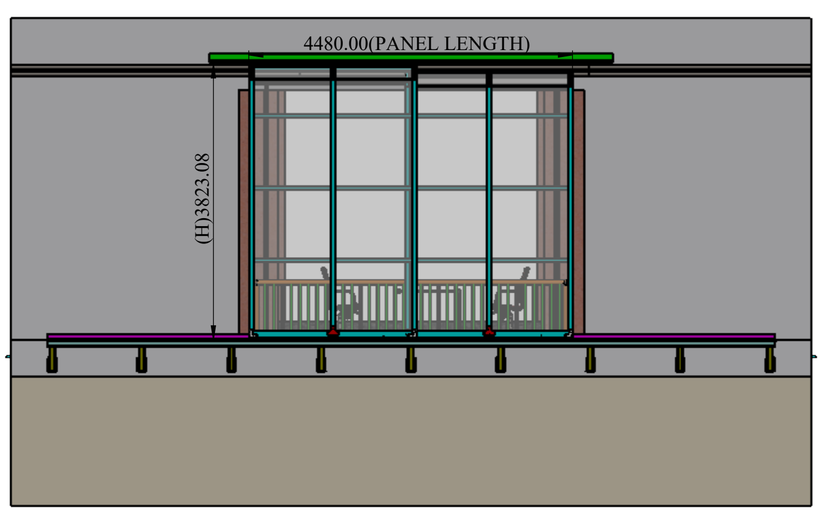

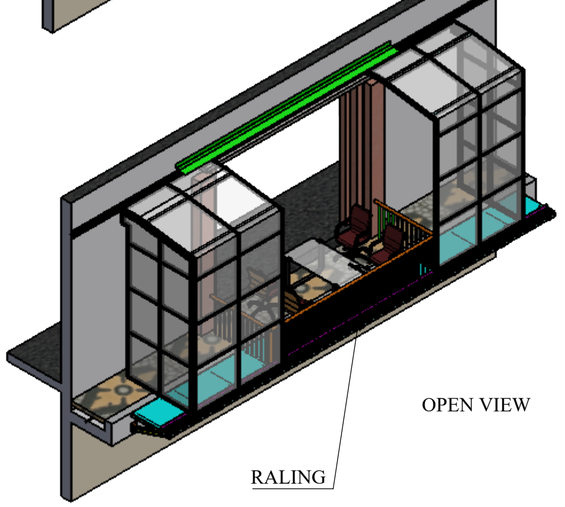

OPEN VIEW

RALING

REV DESCRIPTION	DATE	REV NO
	18-07-2026	REV 00
1.		

NOTE :

GA DRAWING
THIS DRAWING IS FOR CLIENT APPROVAL.
RALING IN CLINT SCOPE.

SPECIAL INSTRUCTION'S :

This drawing & design is the property of NIHVA TECHONOLOGIES PVT. LTD. Not to be sold or copied to any other concern

TITLE -


DWG NO - NTPL-


NIHVA TECHNOLOGIES PVT.LTD.PUNE
Website - www.nihva.com


	NAME	SIGNATURE	DATE
DRAWN	V.W.		18-07-2026
CHK'D	S.P.		20-07-2026
APPV'D	V.T.		20-07-2026

PRODUCT - RETRACTABLE ROOF
CLIENT NAME - ADVIK HI TECH PVT.LTD.
SITE LOCATION - AUNDH
MATRIAL -
QTY - 1
If any queries contact - info@nihva.com
PROJECTION METHOD:
SCALE :
ALL DIMENSION ARE IN mm
A2

DRAWING

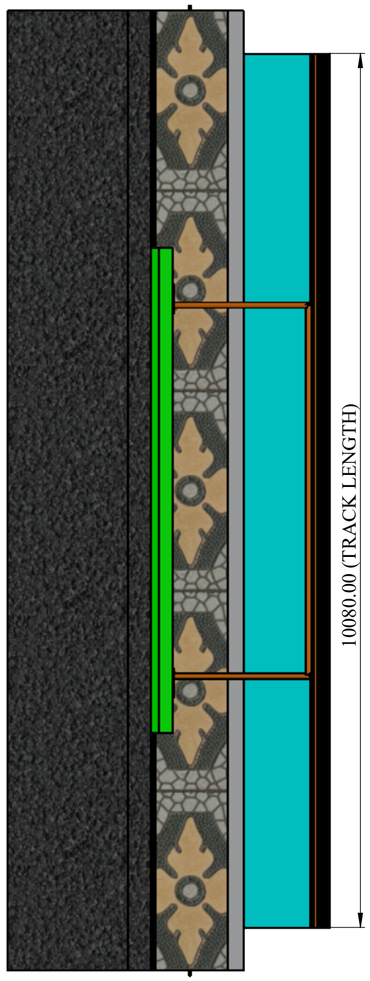

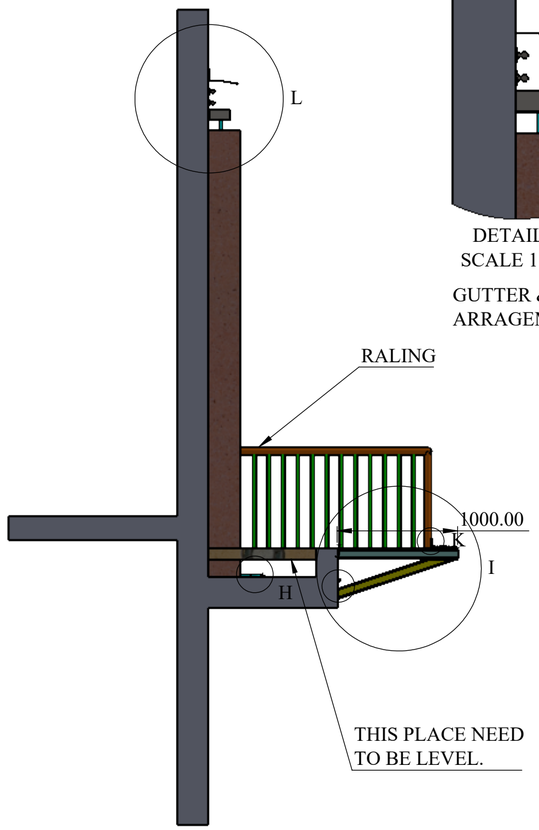


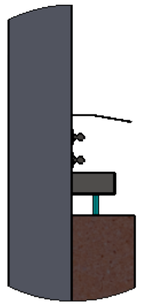


DETAIL L
SCALE 1 : 18


GUTTER & TRACK
ARRAGEMENT

DETAIL E
SCALE 1 : 25

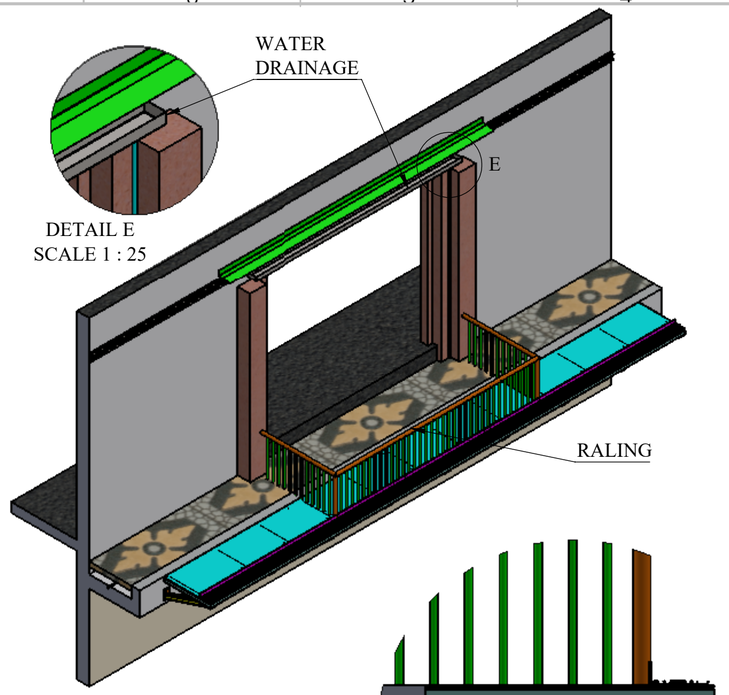


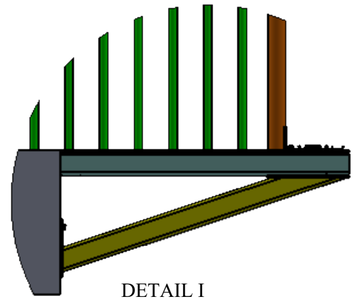


DETAIL I
SCALE 1 : 15

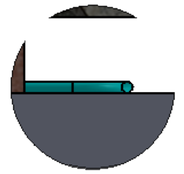


DETAIL H
SCALE 1 : 8

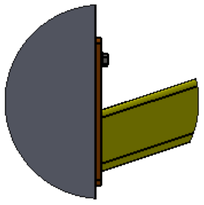

DETAIL J
SCALE 1 : 6

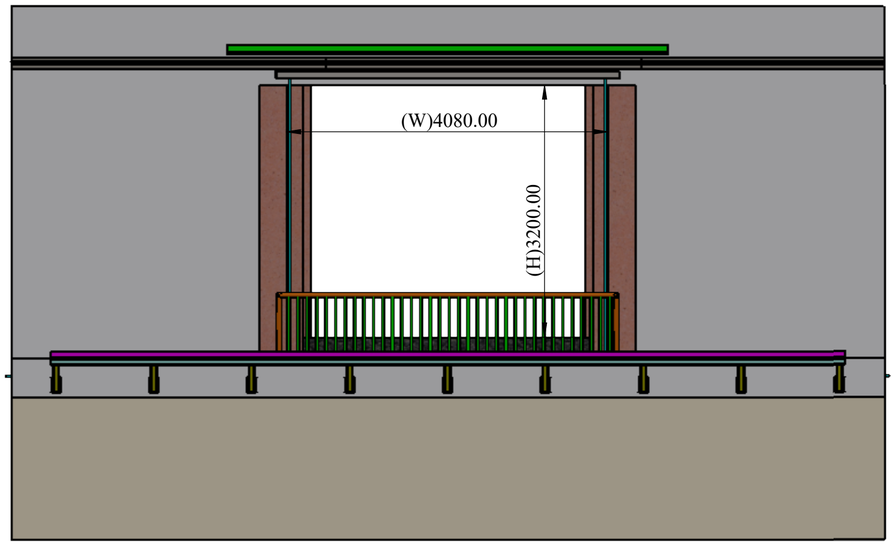

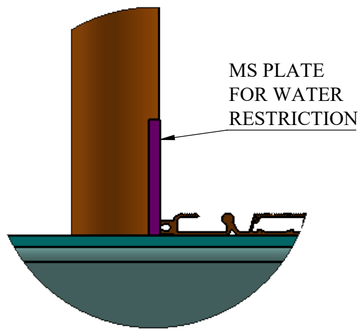

DETAIL K
SCALE 1 : 3

REV DESCRIPTION	DATE	REV NO
	18-07-2026	REV 00
1.		

NOTE :

RAILING IN CLIENT SCOPE.
GUTTER IN NIHVA SCOPE.

SPECIAL INSTRUCTION'S :

This drawing & design is the property of NIHVA TECHONOLOGIES PVT. LTD. Not to be sold or copied to any other concern

TITLE -

DWG NO - NTPL-

NIHVA Technologies Pvt. Ltd.

NIHVA TECHNOLOGIES PVT.LTD.PUNE
Website - www.nihva.com

	NAME	SIGNATURE	DATE
DRAWN	V.W.		18-07-2026
CHK'D	S.P.		20-07-2026
APPV'D	V.T.		20-07-2026

PRODUCT - RETRACTABLE ROOF

CLIENT NAME - ADVIK HI TECH PVT.LTD.

SITE LOCATION - AUNDH

MATRIAL -

QTY - 1

If any queries contact - info@nihva.com

PROJECTION METHOD:

SCALE :

ALL DIMENSION ARE IN mm

A2