
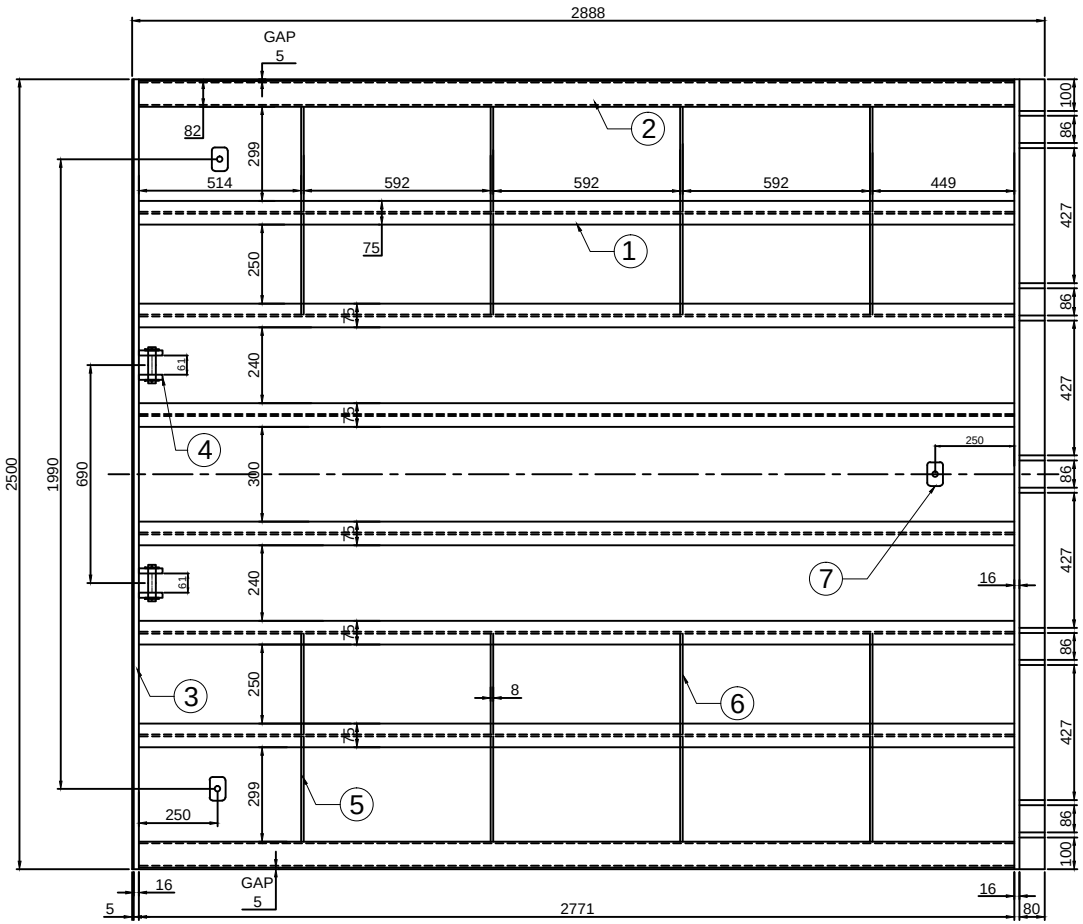


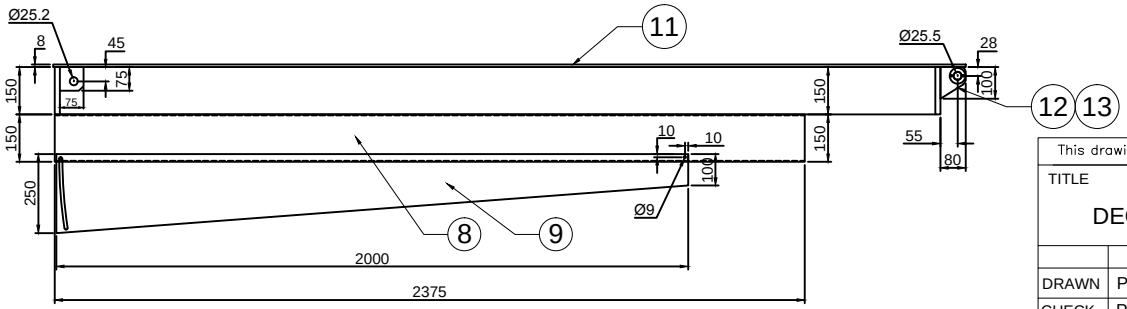

NOTE:~ MTL : MS

PART NO.	PART NAME	DESCRIPTION	QTY
1.	ISMB	150 X 75 X 2770L	6 NOS
2.	R.TUBE	145 X 82 X 4.8THK X 2770L	2 NOS
3.	FLAT	150 X 16 X 2500L	2 NOS
4.	FLAT	75 X 16 X 75L	4 NOS
5.	FLAT	150 X 8 X 332L	8 NOS
6.	FLAT	150 X 8 X 318L	8 NOS
7.	FLAT	50 X 16 X 75L	3 NOS
8.	BEND	150 X 3THK X 2375L	2 NOS
9.	SIDE COVER	250 X 3THK X 2000L	2 NOS
10.	LIP STOPER	Ø25 X 53L	4 NOS
11.	CHEQ.SHEET	2500 X 8 THK X 2888L	1 NO
12.	PROFILE	80 X 16 THK X 100L	10 NOS
13.	PROFILE	50 X 5 THK	2 NOS

This drawing & design is the property of NIHVA TECHNOLOGIES. Not to be sold or copied to any other concern.

TITLE

DECK DETAILS

	NAME	SIGN	DATE
DRAWN	P.A		12.12.18
CHECK	P.A		12.12.18
APPRD.	P.A		12.12.18

If any queries contact : design@nihva.com

ALL DIMENSION ARE IN mm

NIHVA TECHNOLOGIES PVT. LTD.

NIHVA TECHNOLOGIES PVT. LTD. PUNE
Tel : 020 66304033
Email:- info@nihva.com
Website:- www.nihva.com

CLIENT -

PROJECT - DLAG1010

SITE LOCATION -

DWG. NO. : NIHVA/18-19/MFG/DLAG1010/001

SCALE: NTS | WT: | REV- 00