

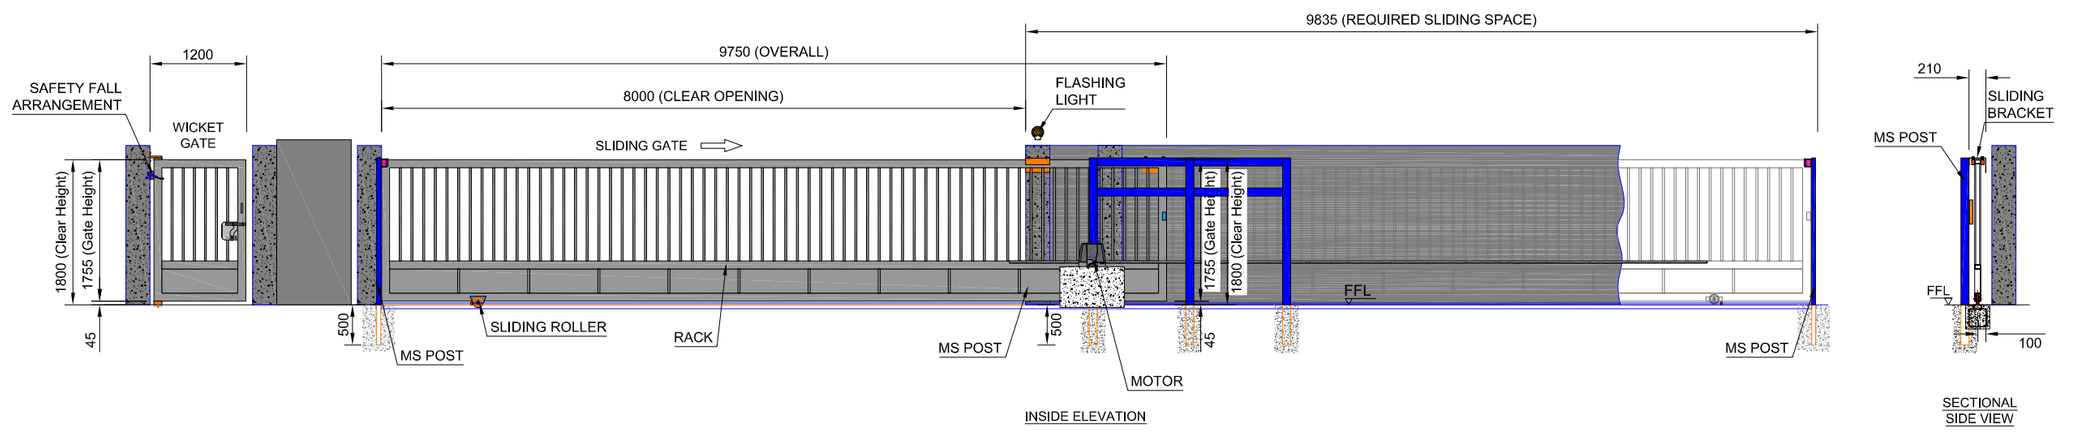


SINGLE LEAF SLIDING GATE
NORTH EAST CORNER GATE

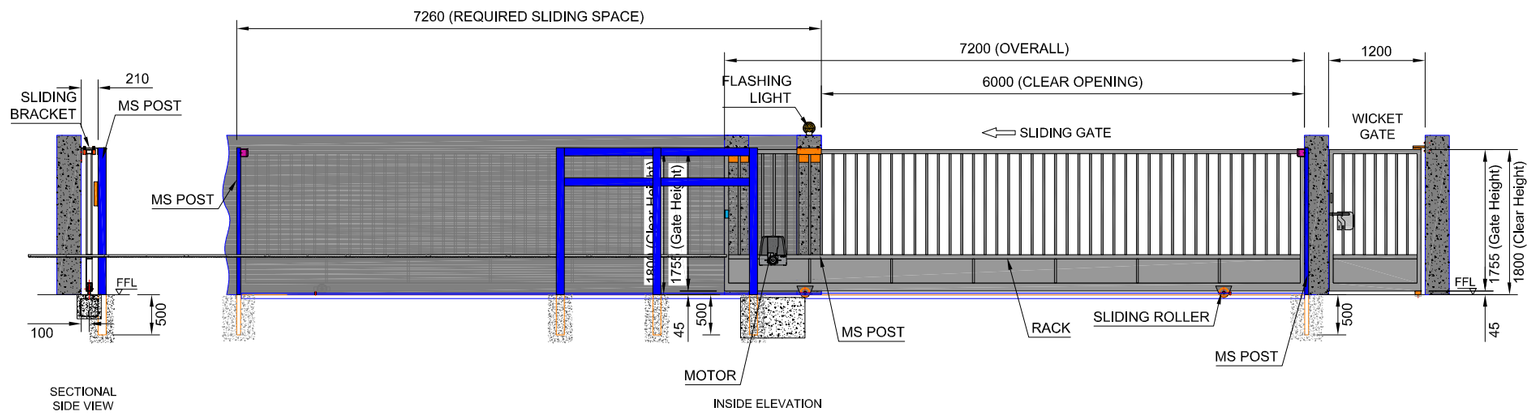


SINGLE LEAF SLIDING GATE
NORTH EAST CORNER GATE

R01

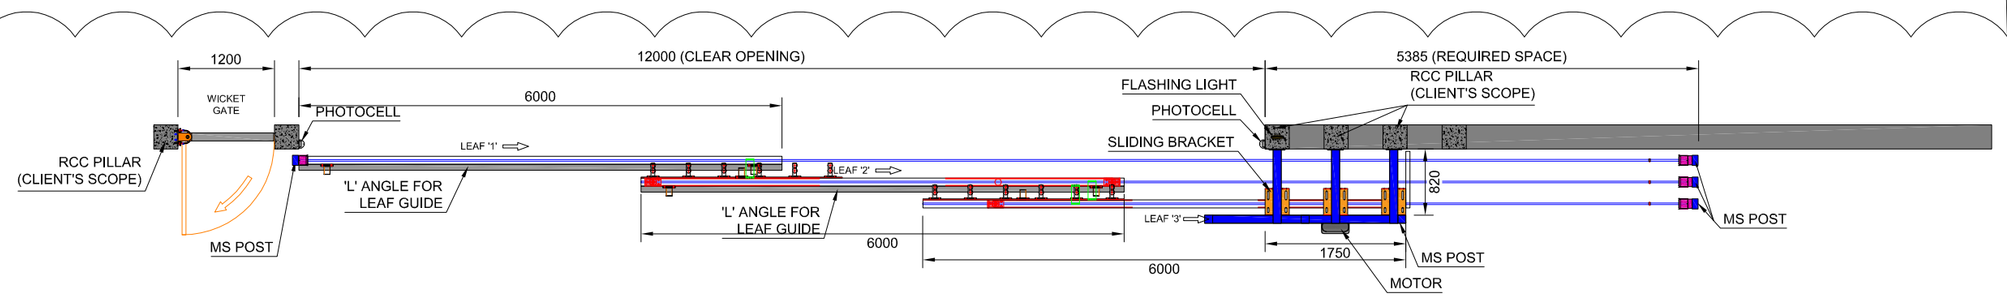

EAST SIDE GATE 2,3 & 4

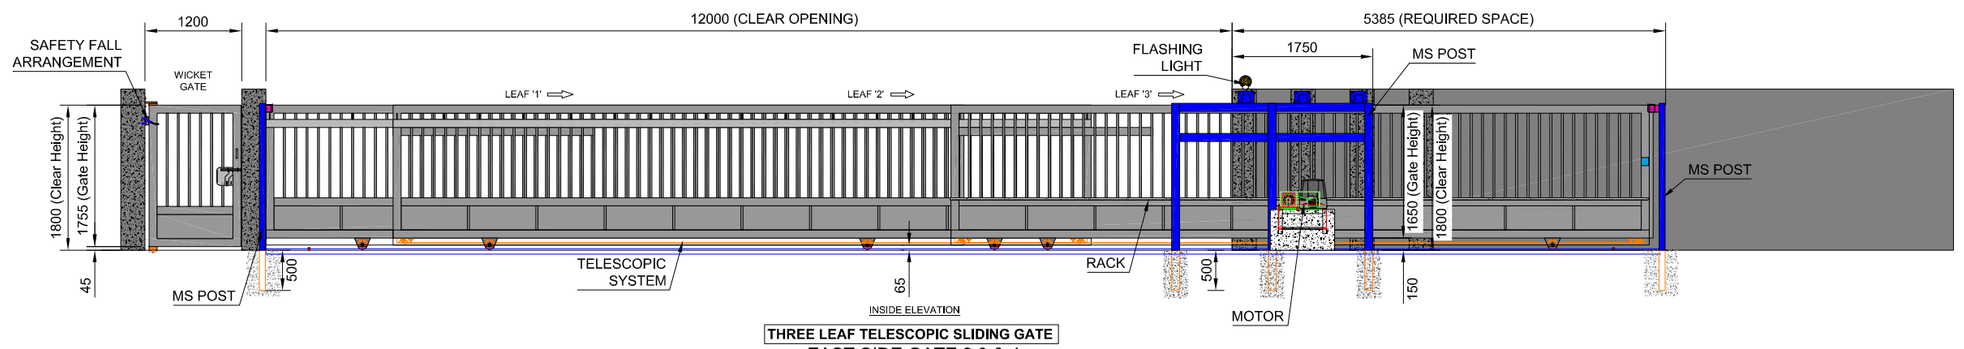

THREE LEAF TELESCOPIC SLIDING GATE
EAST SIDE GATE 2,3 & 4

GENERAL NOTES

1. ALL DIMENSIONS ARE IN mm AND LEVELS IN m UNLESS OTHERWISE SPECIFIED
2. THIS DRAWING IS TO BE READ IN CONJUCTION WITH REFERENCE DRAWINGS ALONG WITH RELEVANT LAYOUTS/SERV. & ARCH.DRAWINGS AND GENERAL NOTES. ANY DISCREPANCIES SHALL BE CLARIFIED FROM THE CONSULTANTS PRIOR TO THE COMMENCEMENT OF ANY RELATED WORKS
3. THIS SUPERCEDES PREVIOUS ISSUES.
4. "HOLD" INFORMATION IS NOT RELEASED FOR CONSTRUCTION.

NORTH POINT

S.No.	REFERENCE DRAWING TITLE	DRAWING NUMBER	DATE	PRE'D

DRAWING STATUS
- AS BUILT
- FOR CONSTRUCTION
- FOR TENDER
- SCHEME

ISSUED FOR CONSTRUCTION

REV.	DESCRIPTION	DRAWN	APPD.	DATE
R01	REVISION AS SHOWN R01	UMA	H.A.E	20.09.2021
R00	ISSUED FOR CONSTRUCTION	UMA	H.A.E	30.08.2021

TITLE

GATE DETAILS

DRAWING No.
0971-00-AR-0062

REVISION
R01

		BOX	DATE	SIGN	DOC. STATUS
JOB NO	: 0971				
SCALE	: 1:75	☐			APPROVED
DATE	: 27.8.21	☐			APPROVED WITH MINOR COMMENTS AS INDICATED
DRAWN	: UMA	☐			NOT APPROVED. COMMENTS AS INDICATED/ATTACHED
CHECKED	: S.S				
APPROVED	: H.A.E				

RALSON

SUB CONSULTANT	CLIENT
ASWATHANARAYANA & ESWARA CONSULTING ENGINEERS & ARCHITECTS MMPDA TOWERS,FIRST FLOOR, NO:184,(OLD NO: 214), ROYAPETTAH HIGH ROAD, ROYAPETTAH , CHENNAI-600014.	ASWATHANARAYANA & ESWARA CONSULTING ENGINEERS & ARCHITECTS MMPDA TOWERS,FIRST FLOOR, NO:184,(OLD NO: 214), ROYAPETTAH HIGH ROAD, ROYAPETTAH , CHENNAI-600014.
PROJECT MANAGEMENT	ARCHITECTS

This document is confidential and remains the property of A&E and must not be copied or used without prior written permission.

A2