


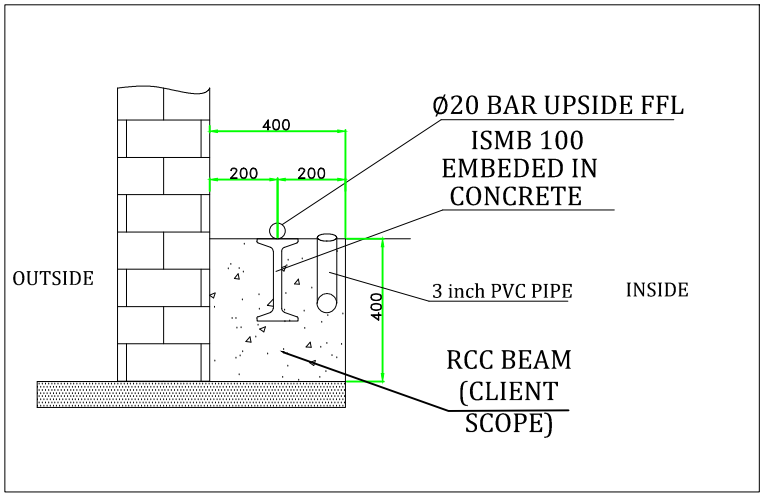

This drawing & designing is the property of NIHVA TECHNOLOGIES. Not be sold or copy to any other concern.

TITLE: SLIDING GATE 5.5 X 1.8 FOUNDATION DRAWING			
	NAME	SIGN	DATE
DRAWN	SMS		18.12.2020
CHECK			
APPROVAL			
If any queries contact : design@nihva.com			
ALL DIMENSION ARE IN mm			

NIHVA
NIHVA TECHNOLOGIES PVT. LTD.
Website:- www.nihva.com
NIHVA TECHNOLOGY PVT. LTD. PUNE
Tel : 020 66304033
Email:- info@nihva.com

CLIENT - INDAMER TECHNICS PVT. LTD.			
PROJECT -			
SITE - NAGPUR			
DWG. NO. : NIHVA/20-21/0114			REV. : 0
SCALE: NTS	WT:	SHEET:	